




Materialen/details:


- 001. Spiegel
- 002. Trap
- 003. Trapkast
- 004. Keukenwand
- 005. Kookeiland
- 006. Zitbank
- 007. Eettafel
- 008. Meterkast
- 009. Nissenkast
- 010. Haard/TV kast

Materialen/details:


Getinte spiegel met aan achterzijde rondom Led verlichting
Tafelblok: brons nobel

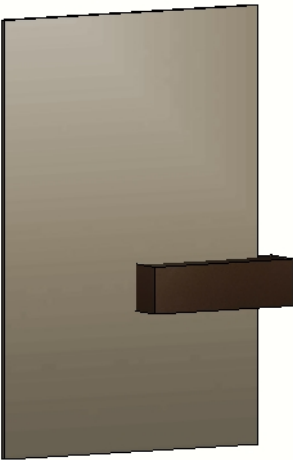


BOVENAANZICHT

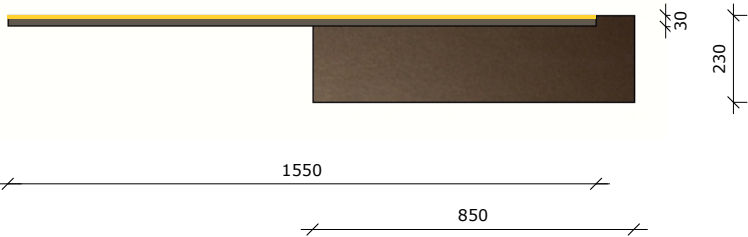

VOORAANZICHT

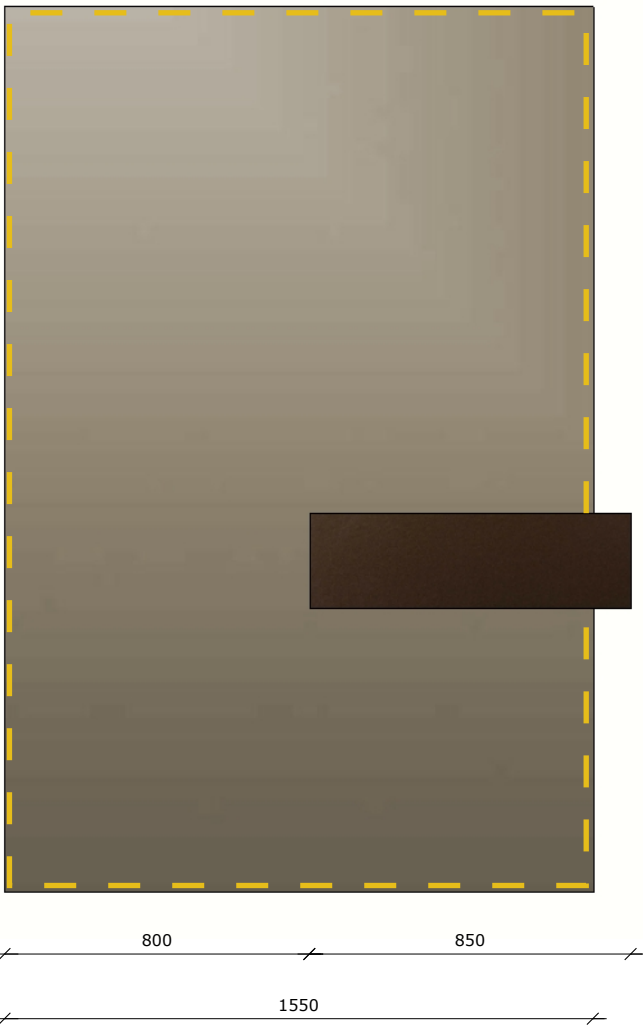


ZIJAAANZICHT

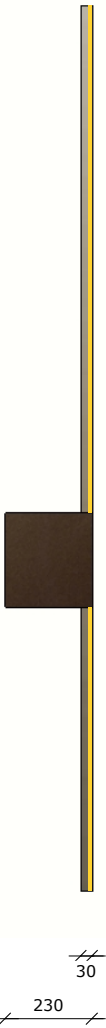



Materialen/details:

Traptreden bekleden met Aventura Carpets basic
Tione n.t.b. kleur
Leuning: Brons nobel met aan onderzijde Led verlichting
Trap boom + paal : Pure and Original Drift
Getint glas

BOVENAANZICHT

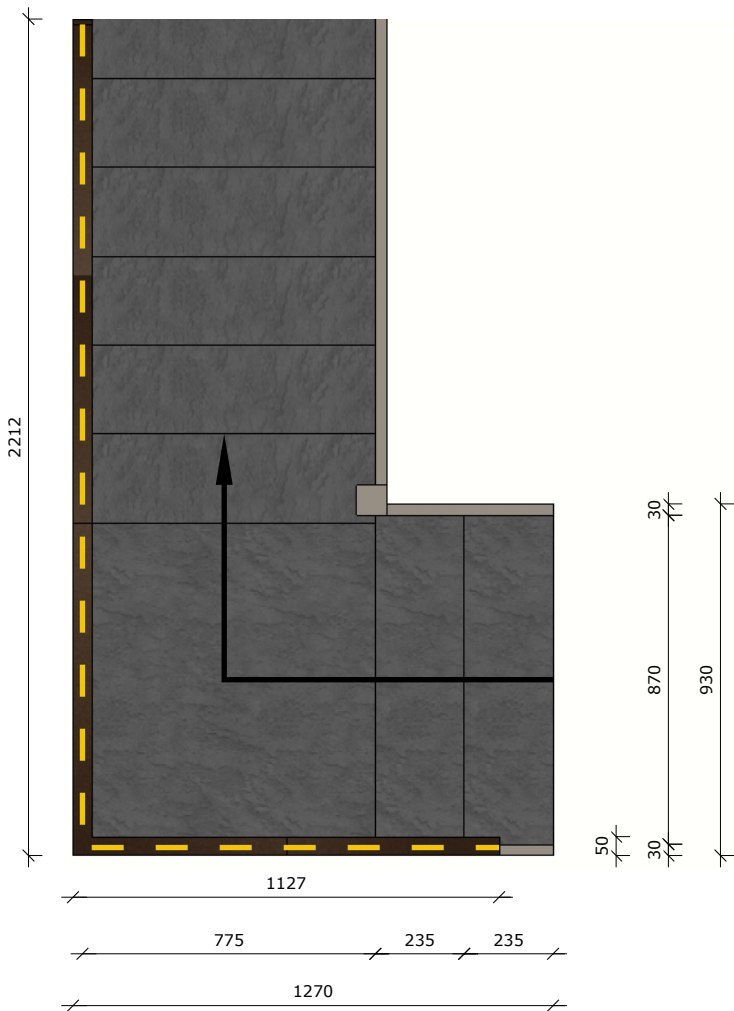

VOORAANZICHT

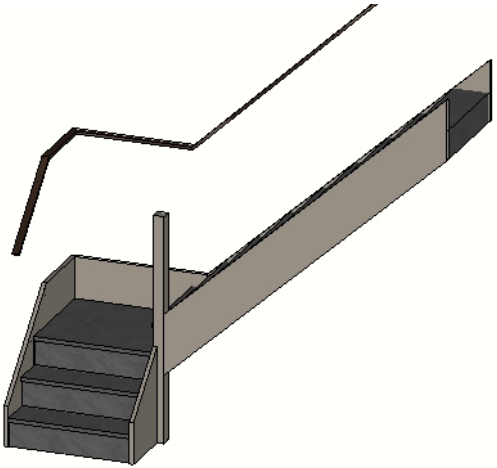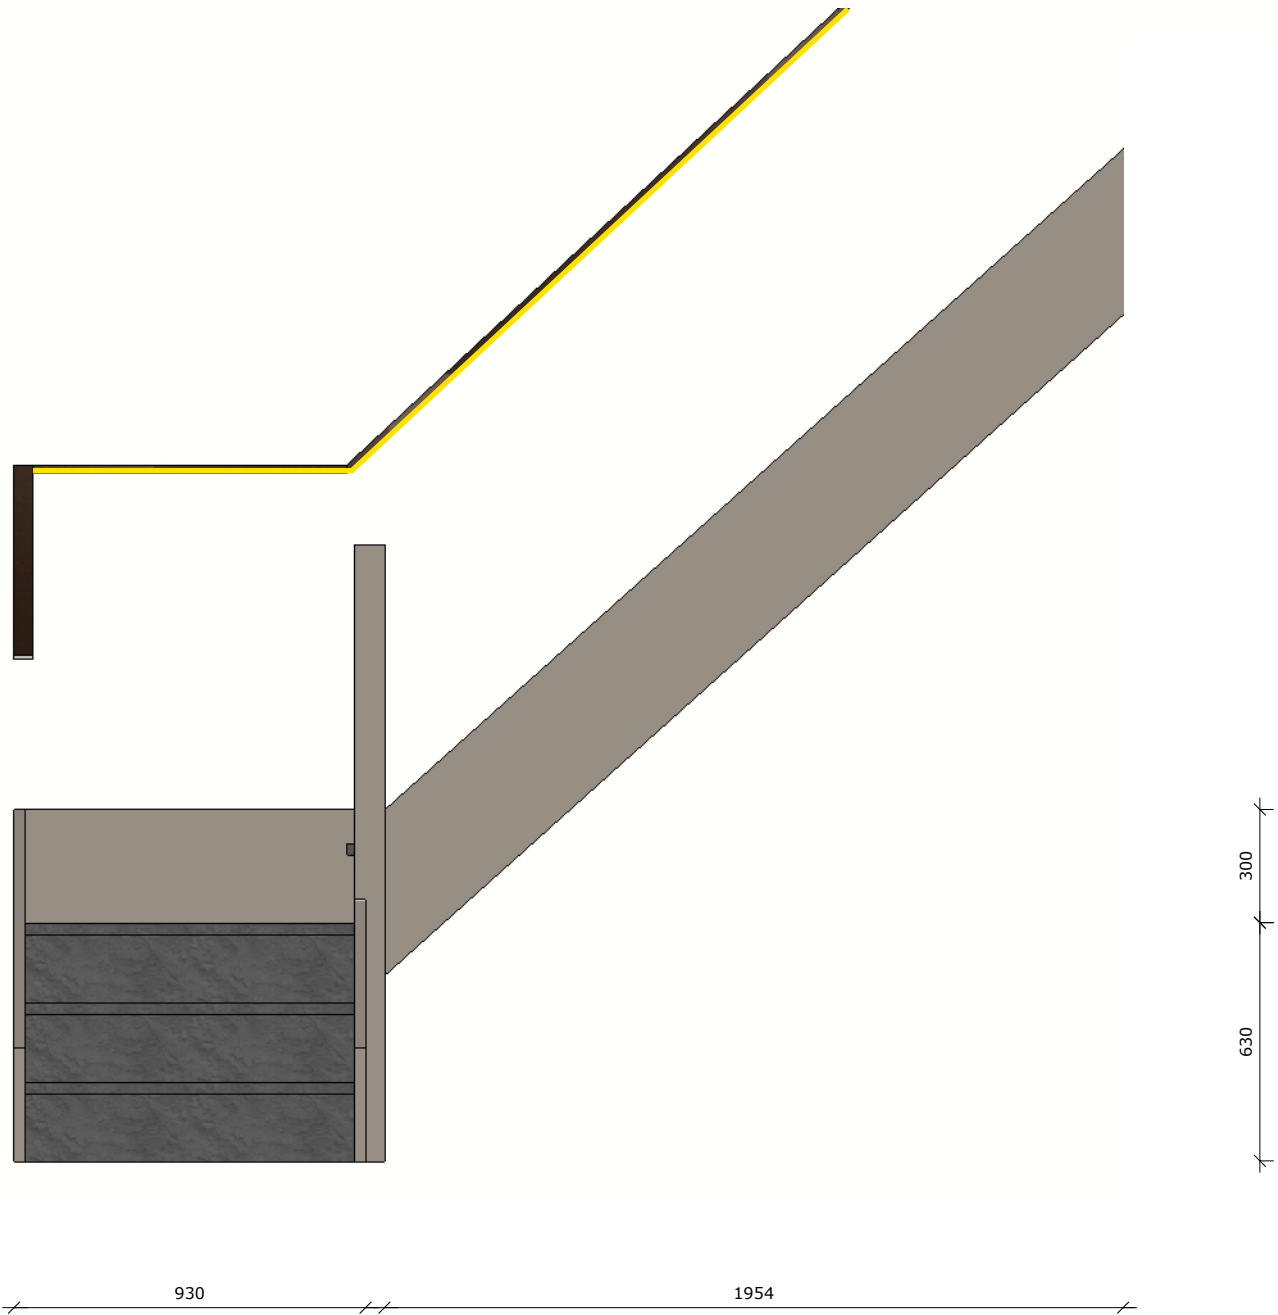


Materialen/details:


Deuren: Decolegno Primofiore FC33
Plint: Decolegno Primofiore FC33

Positie 01. Indeling n.t.b.
Positie 02. Indeling n.t.b.
Positie 03. Indeling n.t.b.

VOORAANZICHT

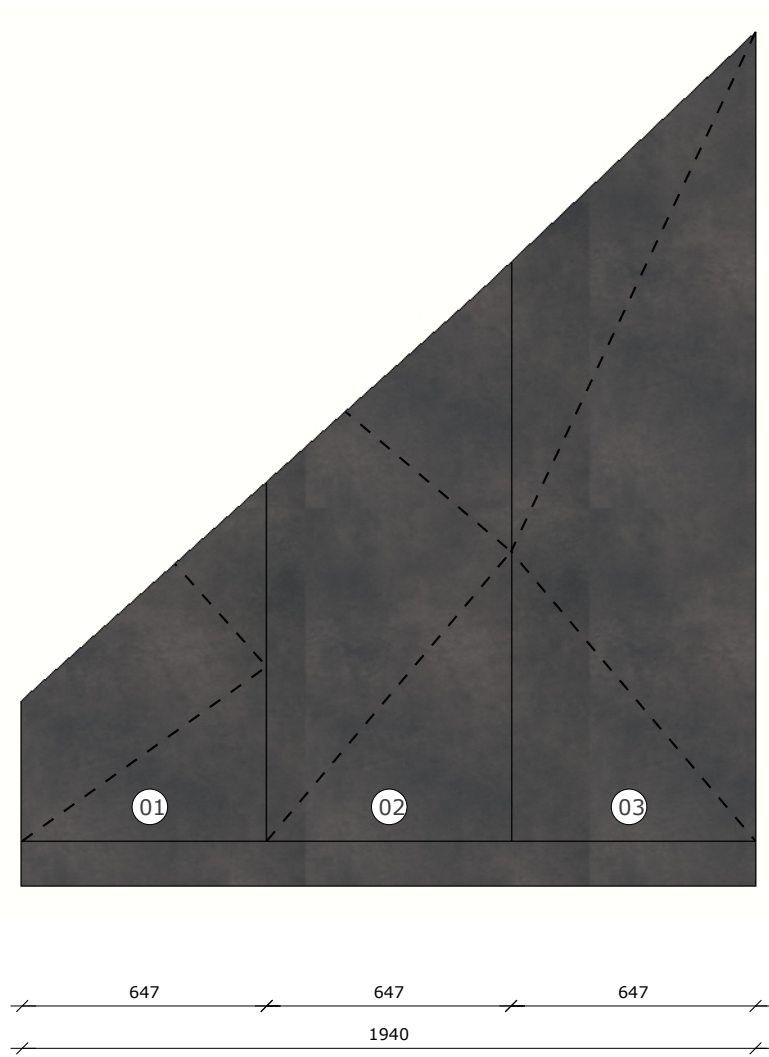

ZIJAANZICHT

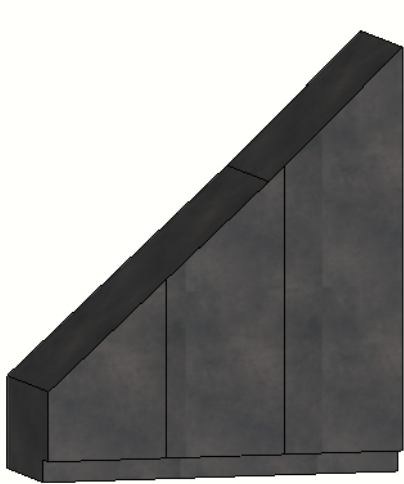


Materialen/details:


Fronten: Decolegno Primofiore FC33
Plint: Decolegno Primofiore FC33
Led onder planken Coffee Corner
Glazen deuren: Getint glas
Planken: Decolegno Primofiore FC33

Positie 01. Koelkast type: n.t.b.
Positie 02. Combi oven type: n.t.b.
Positie 03. Stoomoven type: n.t.b.

VOORAANZICHT

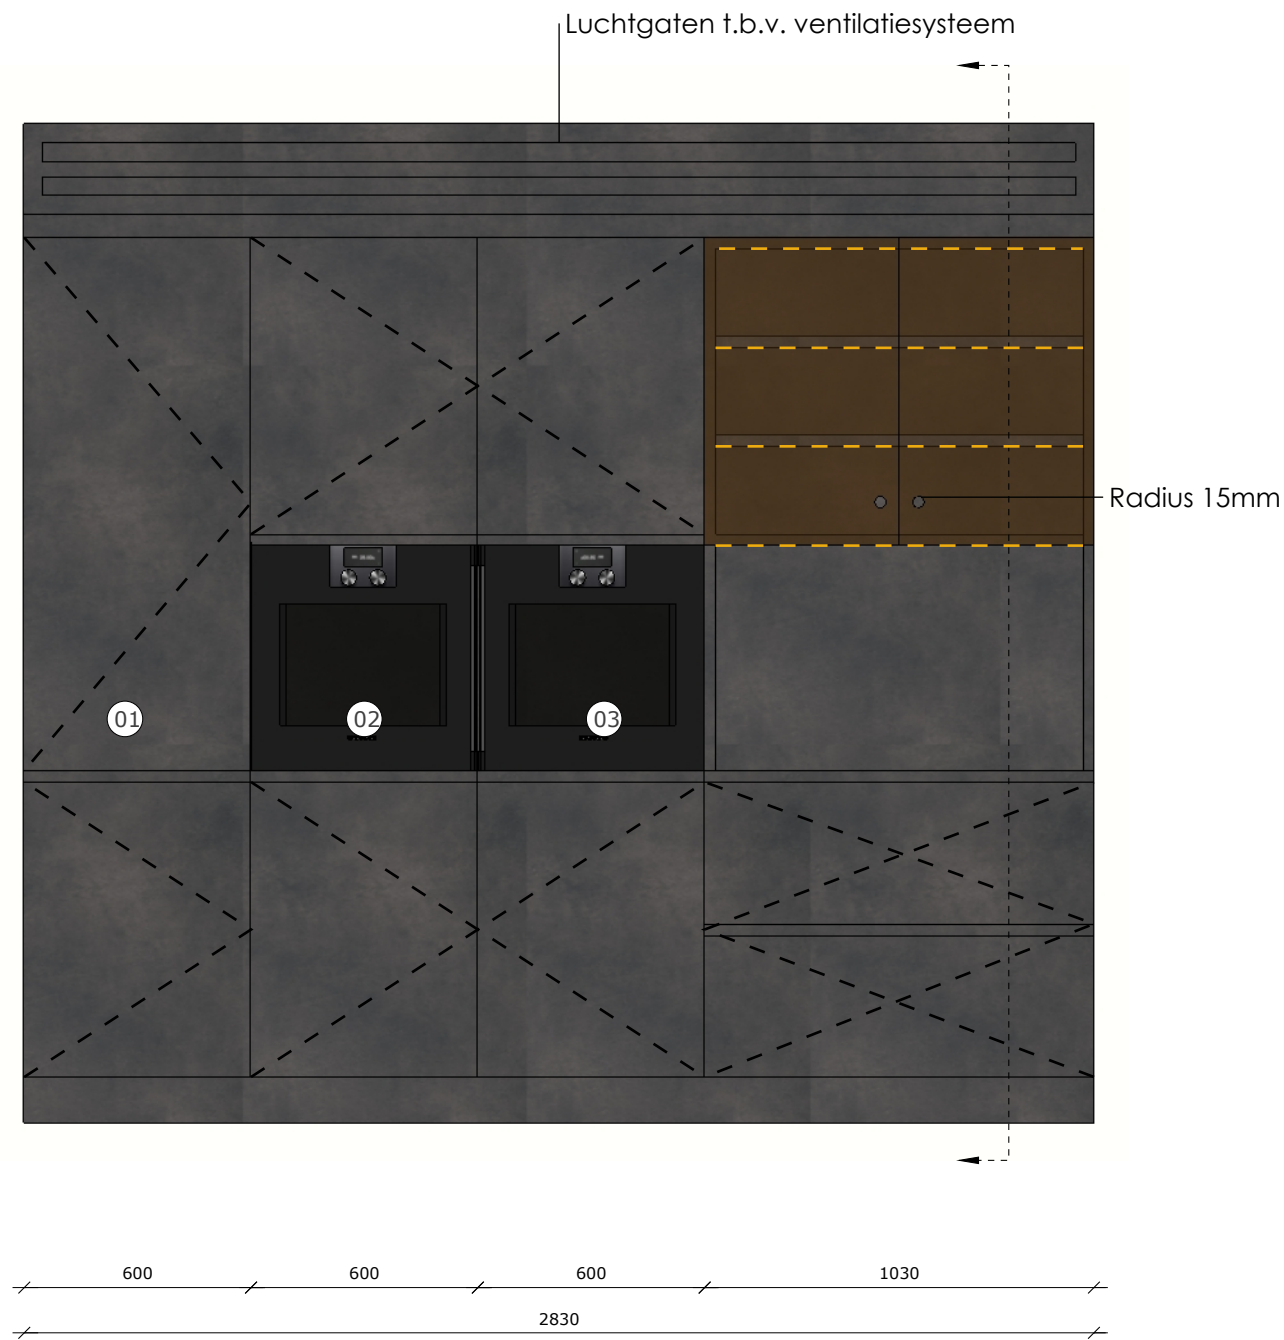

DOORSNEDE

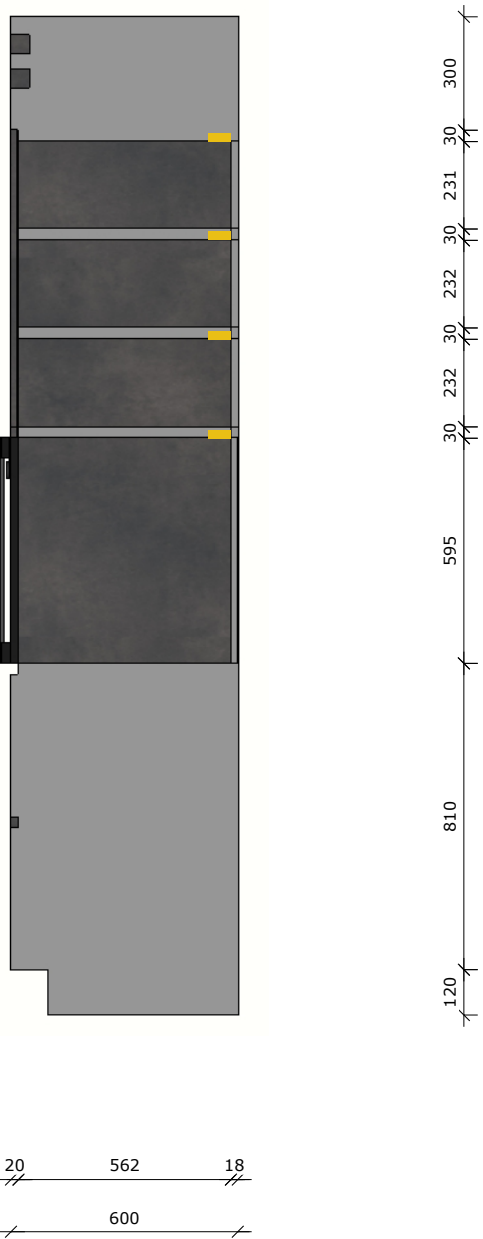

DEFINITIEF ONTWERP
PROJECT: ACHTERSTRAAT 1, LIENDEN

EXACTE MATEN IN HET WERK TE CONTROLEREN

THOMASDEGIER
WORLD OF INTERIOR DESIGN

Onderwerp: 004. Keukenwand
Datum: 19-12-2025

Versie: V1
Formaat: A3
Schaal: 1:20

Materialen/details:

Fronten: Brons Nobel
Plint: Brons Nobel
Greeplijst: Brons Nobel
Blad: Marazzi Frappuccino


Positie 01. Inductiekookplaat type: n.t.b.
Positie 02. Quooker in brons patina finish



BOVENAANZICHT




ACHTERAANZICHT

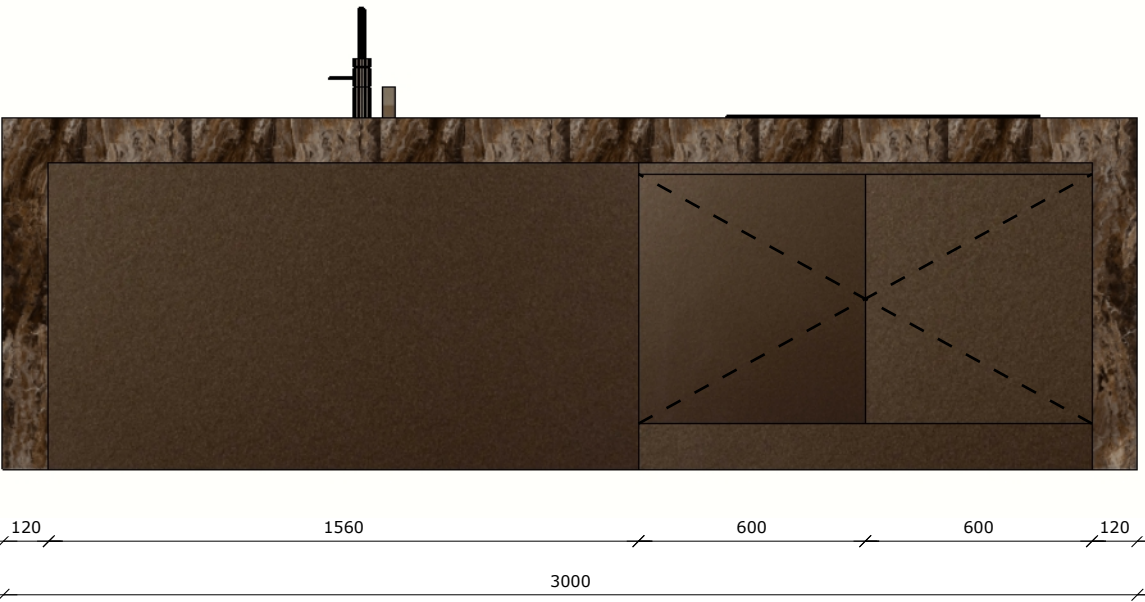


ZIJAAANZICHT



VOORAANZICHT

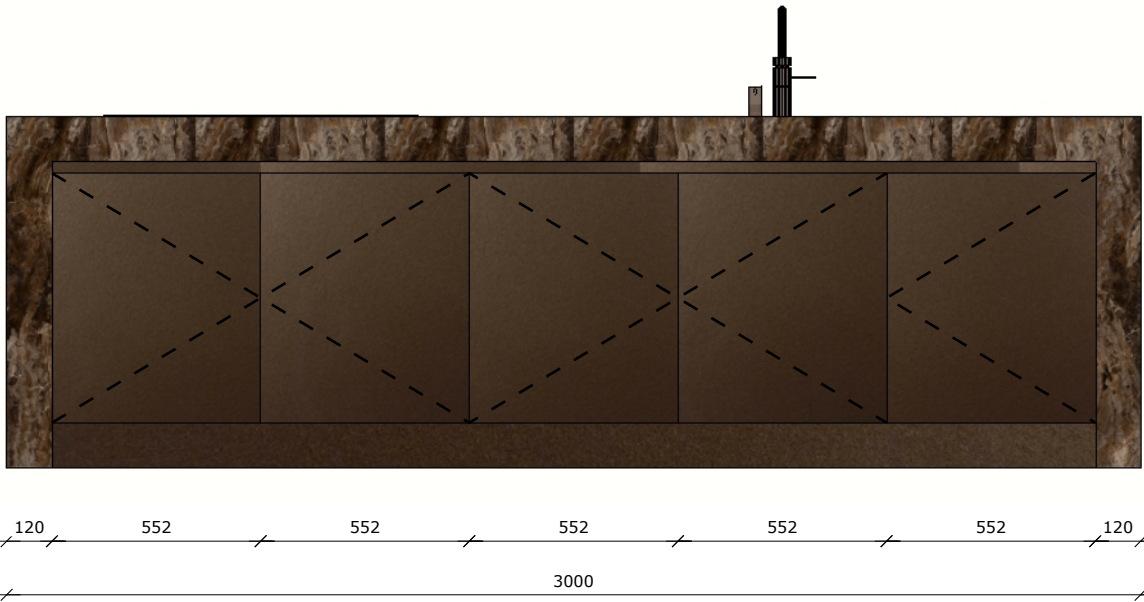

DOORSNEDE

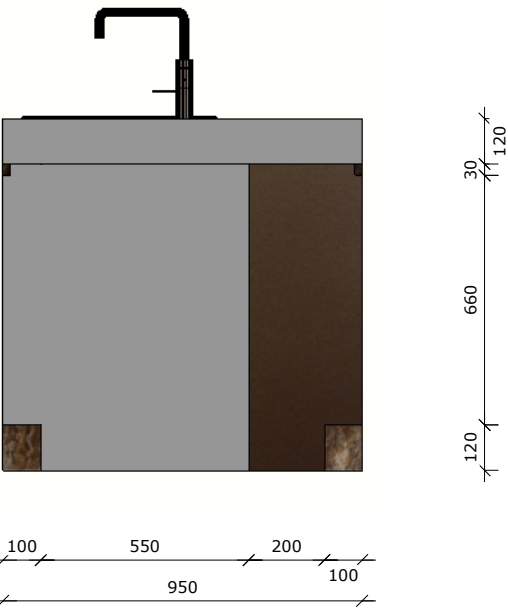

DEFINITIEF ONTWERP
PROJECT: ACHTERSTRAAT 1, LIENDEN

EXACTE MATEN IN HET WERK TE CONTROLEREN

THOMASDEGIER
WORLD OF INTERIOR DESIGN


Onderwerp: 005. Kookeiland
Datum: 23-12-2025

Versie: V2
Formaat: A3
Schaal: 1:20

Materialen/details:

Panelen: Koudschuim gestoffeerd met Aristide Markle Taupe 250
Zitting: Aristide Markle Taupe 250
Onderzijde: Donker gebeitst hout

BOVENAANZICHT

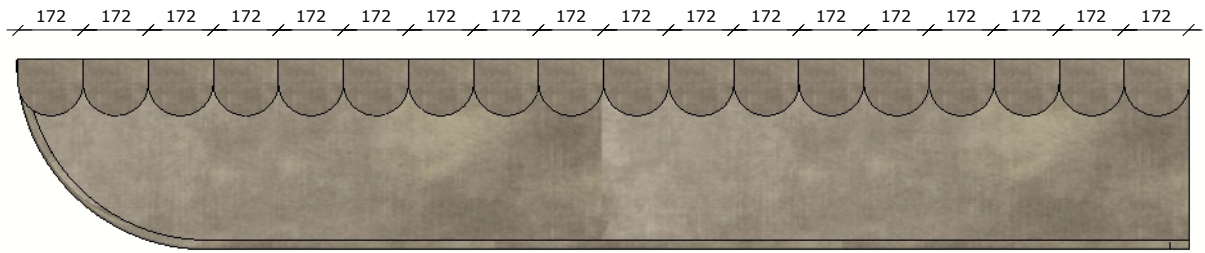

VOORAANZICHT



500


2140

2640


100

400

ZIJAANZICHT

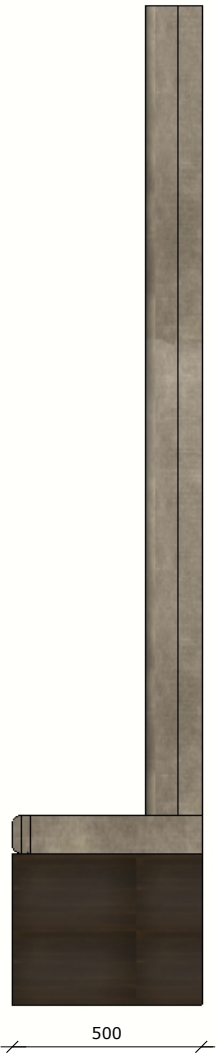


500

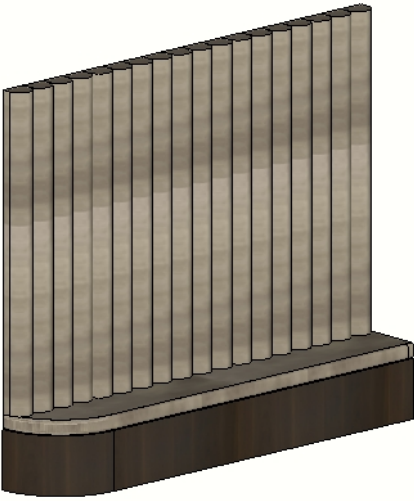

Materialen/details:

Blad: Donker gebeitst hout met brons nobel rand
Poten: Bovenzijde brons nobel onderzijde donker gebeitst hout


DETAIL RAND
SCHAAL 1:1

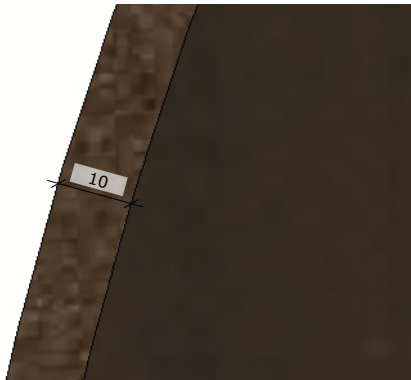


BOVENAANZICHT



VOORAANZICHT

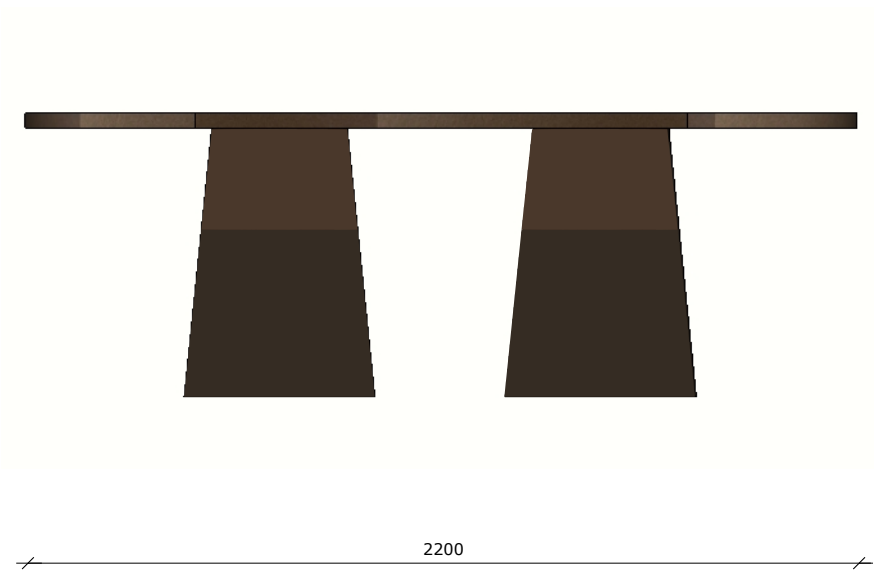


ZIJAAANZICHT

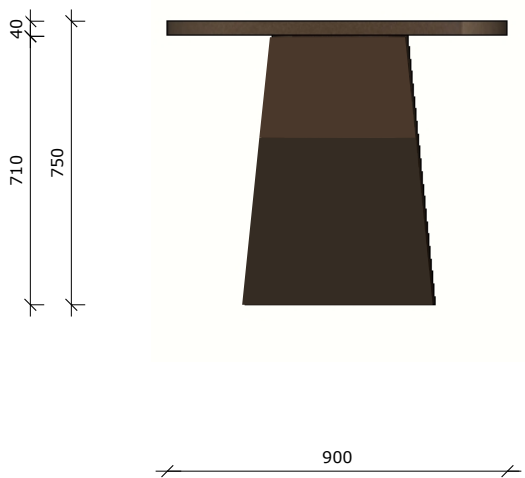


Materialen/details:
Fronten: Decolegno Primofiore FC33
Plint: Decolegno Primofiore FC33
Meterkast in kast




BOVENAANZICHT

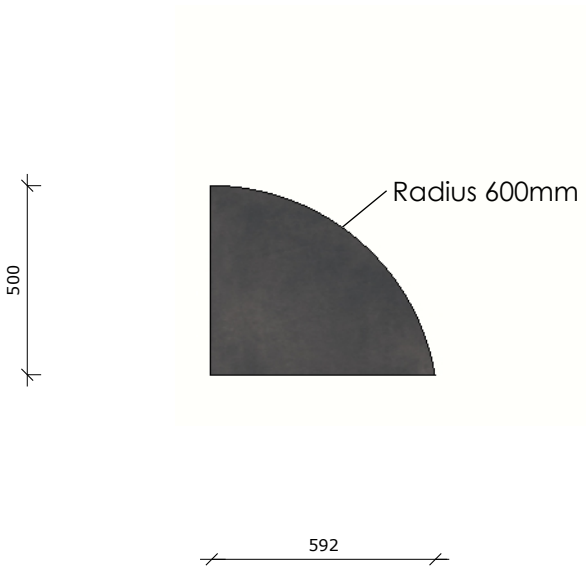

VOORAANZICHT

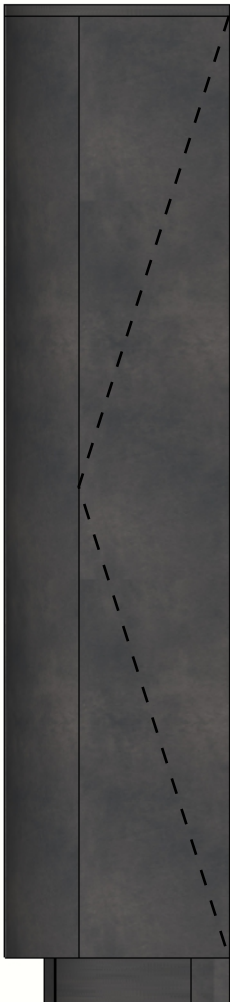

397

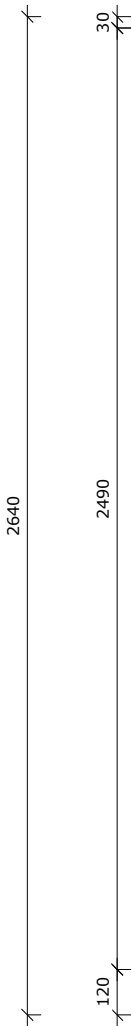


30

2490

120

ZIJAAANZICHT

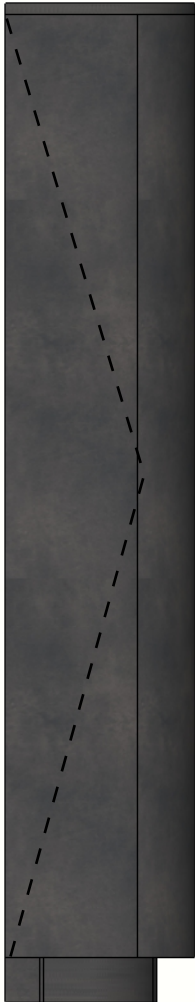

351

Materialen/details:


Achterwand: Rebel Walls Water color flow
Led onder planken
Planken: Decolegno Primofiore FC33
Fronten: Decolegno Primofiore FC33
Plint: Decolegno Primofiore FC33

BOVENAANZICHT



4632

VOORAANZICHT

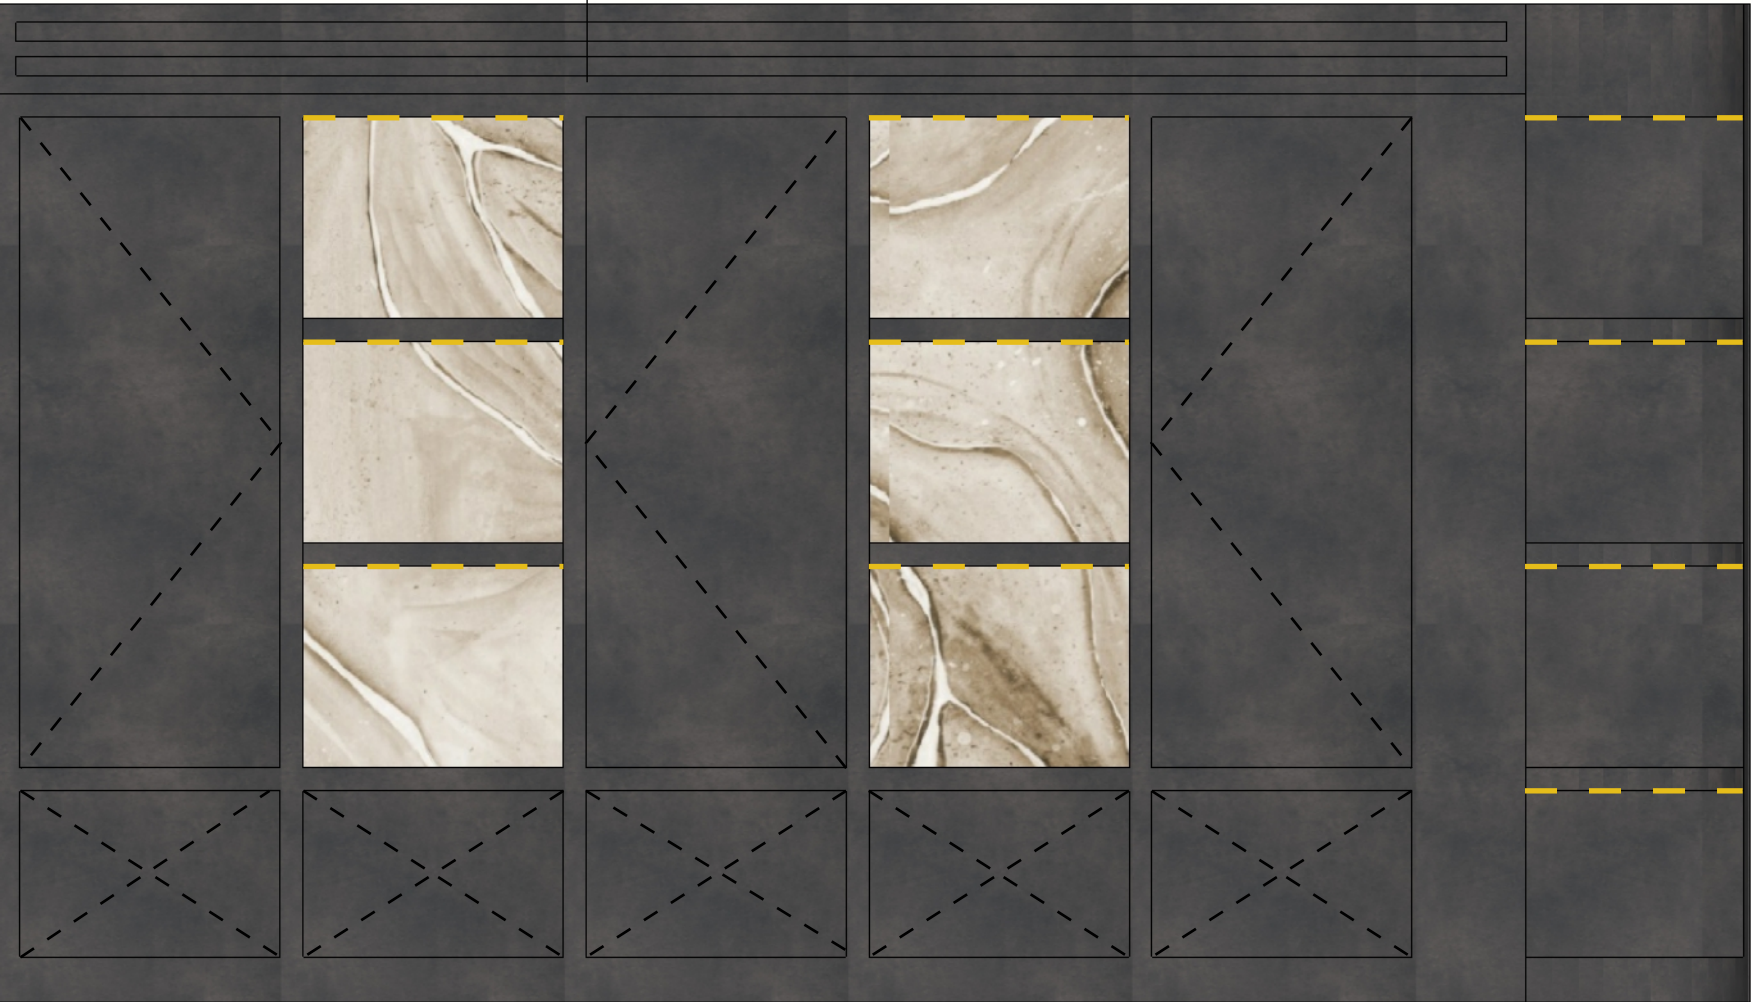

Luchtgaten t.b.v. ventilatiesysteem


60 688 60 688 60 688 60 688 60 688 300 592
4632

500



ZIJAANZICHT

60 240 60 240 533 60 533 60 533 60 533 60 440 120
1720 2640 620

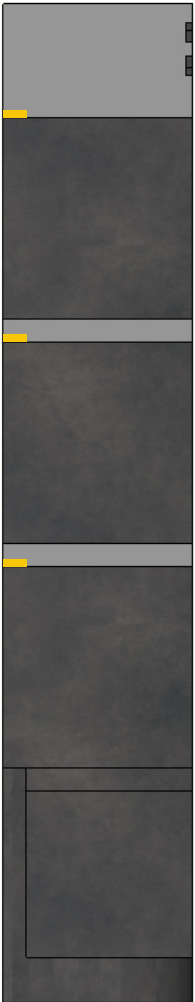

500

DEFINITIEF ONTWERP
PROJECT: ACHTERSTRAAT 1, LIENDEN

EXACTE MATEN IN HET WERK TE CONTROLEREN





Onderwerp: 009. Nissenkast
Datum: 19-12-2025

Versie: V1
Formaat: A3
Schaal: 1:20


Materialen/details:

Achterwand: Rebel Walls Water color flow
Led boven kasten
Bovenzijde: Pure & Original Old Flax
Onderzijde: Marazzi frappucino
3- zijdige haard type: n.f.b.



BOVENAANZICHT

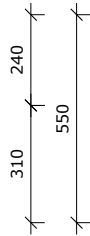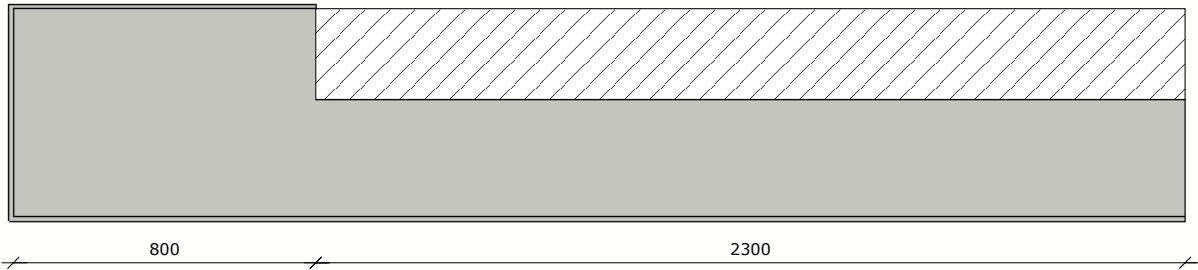

VOORAANZICHT

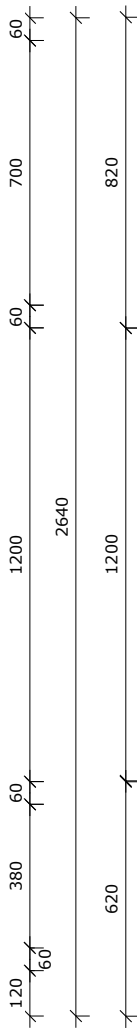

ZIJAAANZICHT

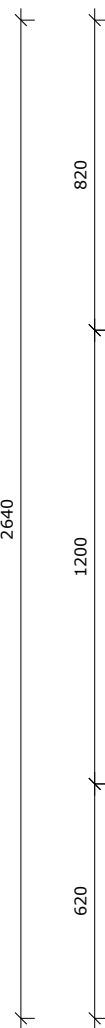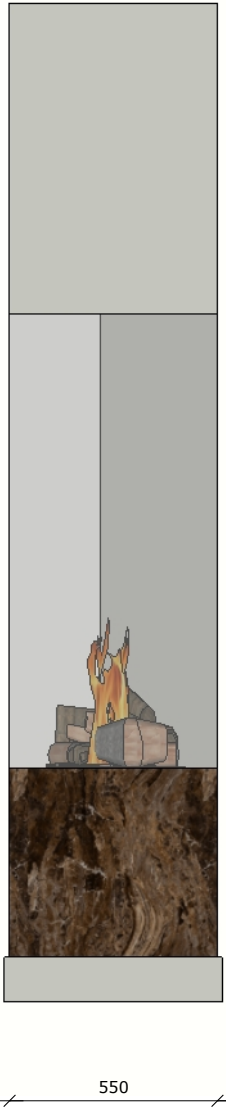

DOORSNEDE

