

DEFINITIEF ONTWERP
PROJECT: ACHTERSTRAAT 1, LIENDEN

EXACTE MATEN IN HET WERK TE CONTROLEREN



Onderwerp: Plattegrond
Datum: 19-12-2025

Versie: V1
Formaat: A3
Schaal: 1:50




LED strip in stuc
Directe LED verlichting
Dimbaar warm wit 2700K



LED strip
Indirecte LED verlichting
t.b.v. interieurmeubilair
Dimbaar warm wit 2700K



Frame lamp
Brons
Dimbaar warm wit 2700K

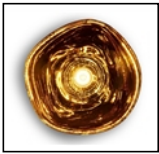

Wandlamp
Tom Dixon Melt mini
surface
Dimbaar warm wit 2700K
Aantal: 5
Exacte posities n.t.b.



Hangarmatuur
Tom Dixon
Excl. plafondplaat
Dimbaar warm wit 2700K
Aantal: 6
Exacte posities n.t.b.

DEFINITIEF ONTWERP
PROJECT: ACHTERSTRAAT 1, LIENDEN


EXACTE MATEN IN HET WERK TE CONTROLEREN


THOMASDEGIER
WORLD OF INTERIOR DESIGN



Onderwerp: Lichtplan
Datum: 19-12-2025



Versie: V1
Formaat: A3
Schaal: 1:50

VERLAAGD PLAFOND MET
LED

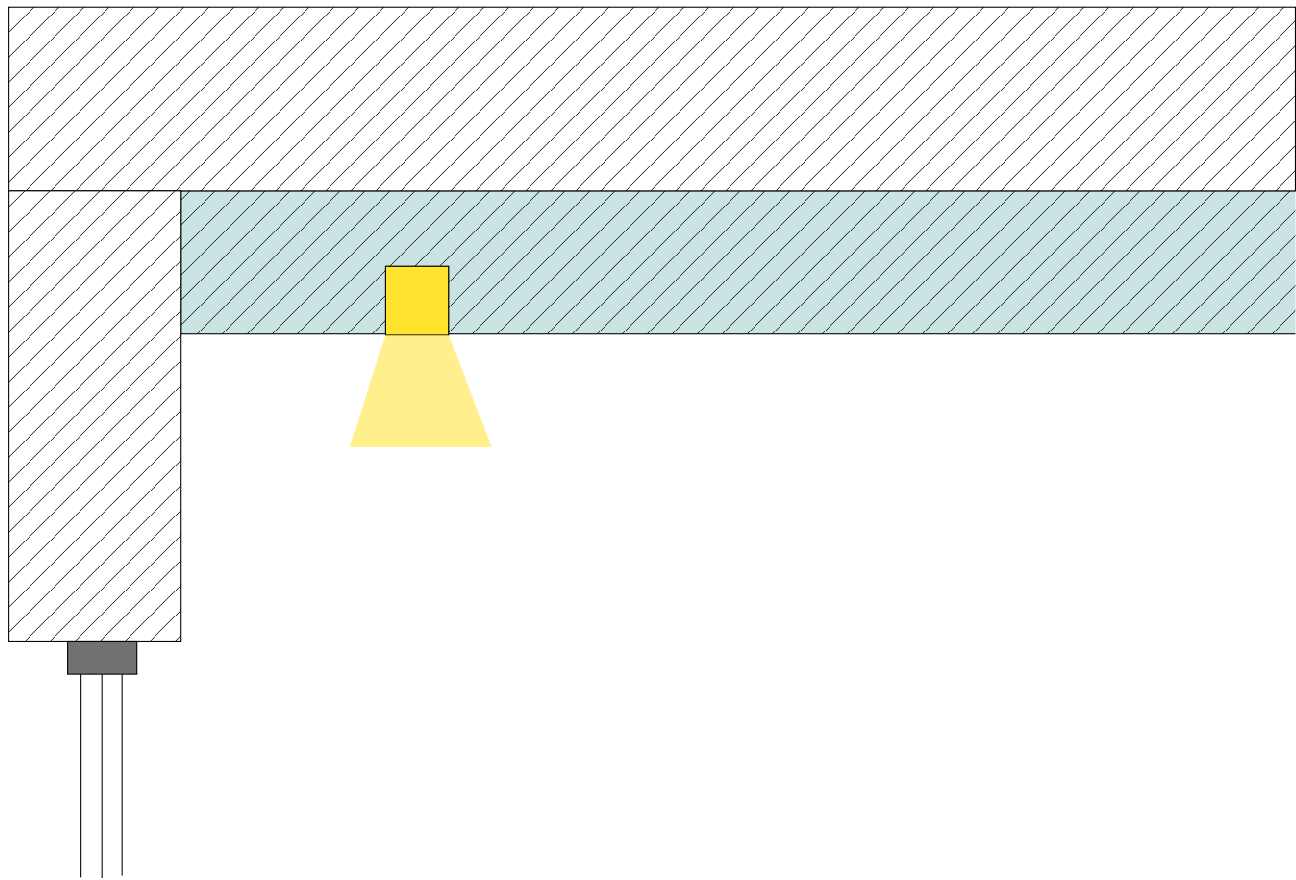

VOORBEELD AFBEELDING

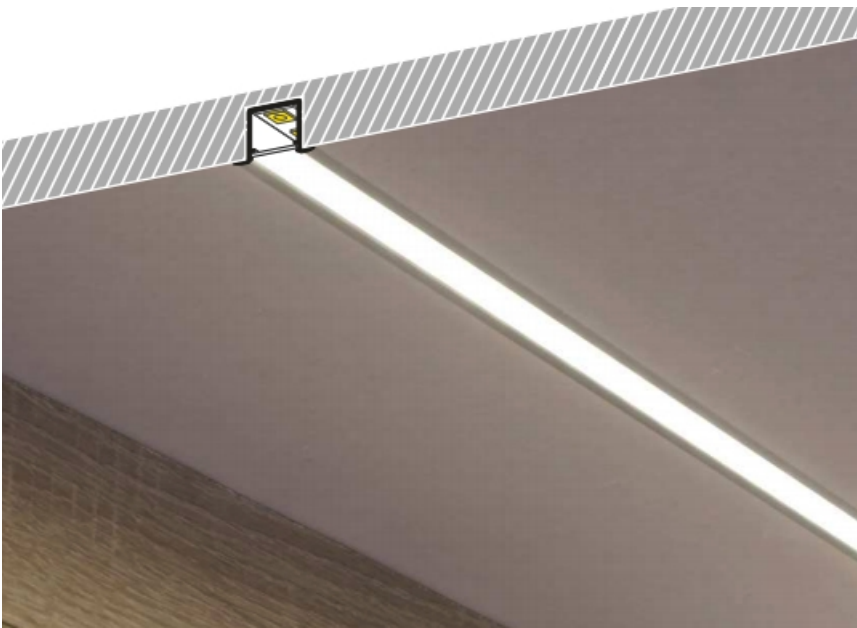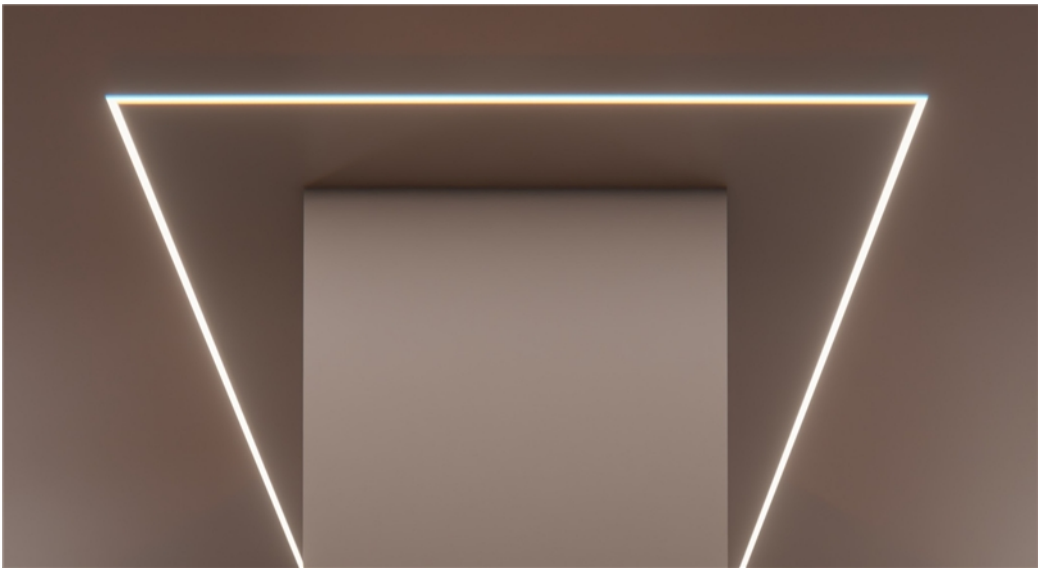

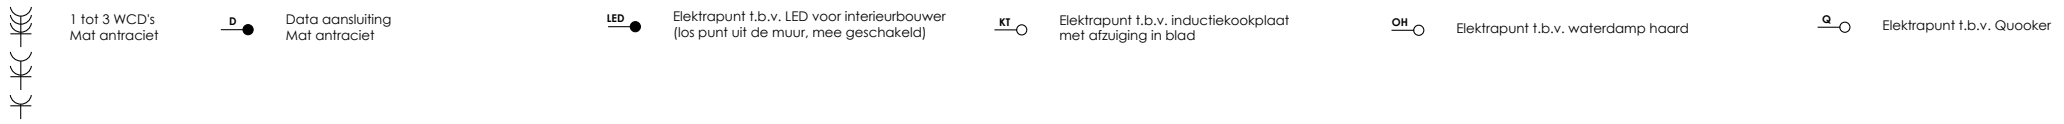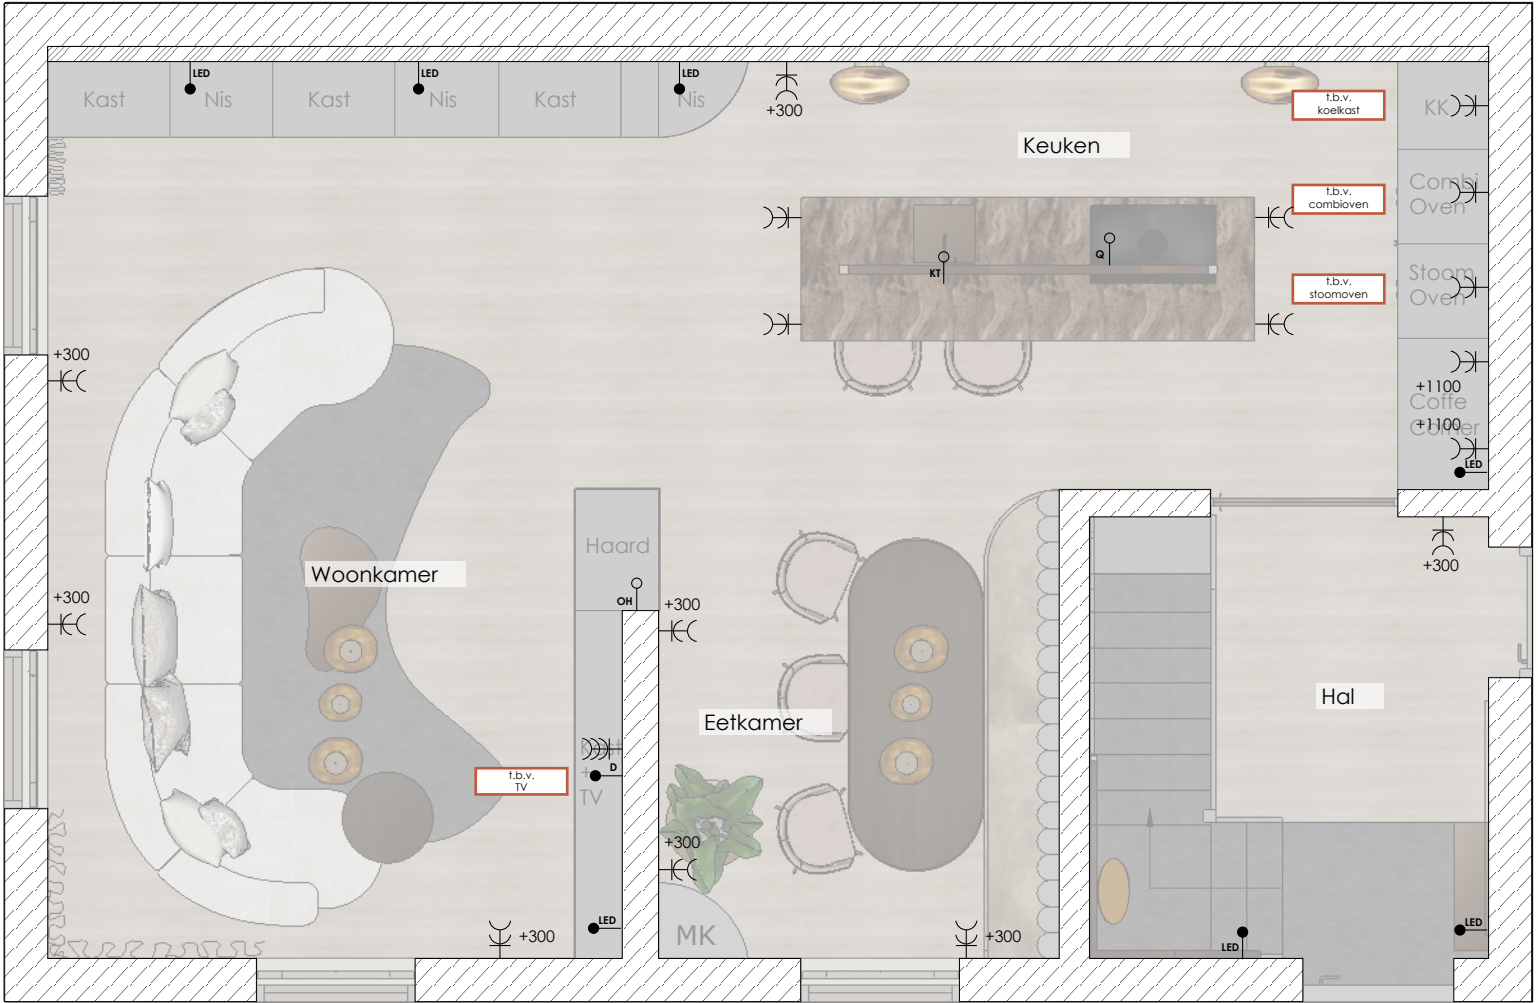


DEFINITIEF ONTWERP
PROJECT: ACHTERSTRAAT 1, LIENDEN

EXACTE MATEN IN HET WERK TE CONTROLEREN



Onderwerp: Elektraplan
Datum: 23-12-2025


Versie: V2
Formaat: A3
Schaal: 1:50

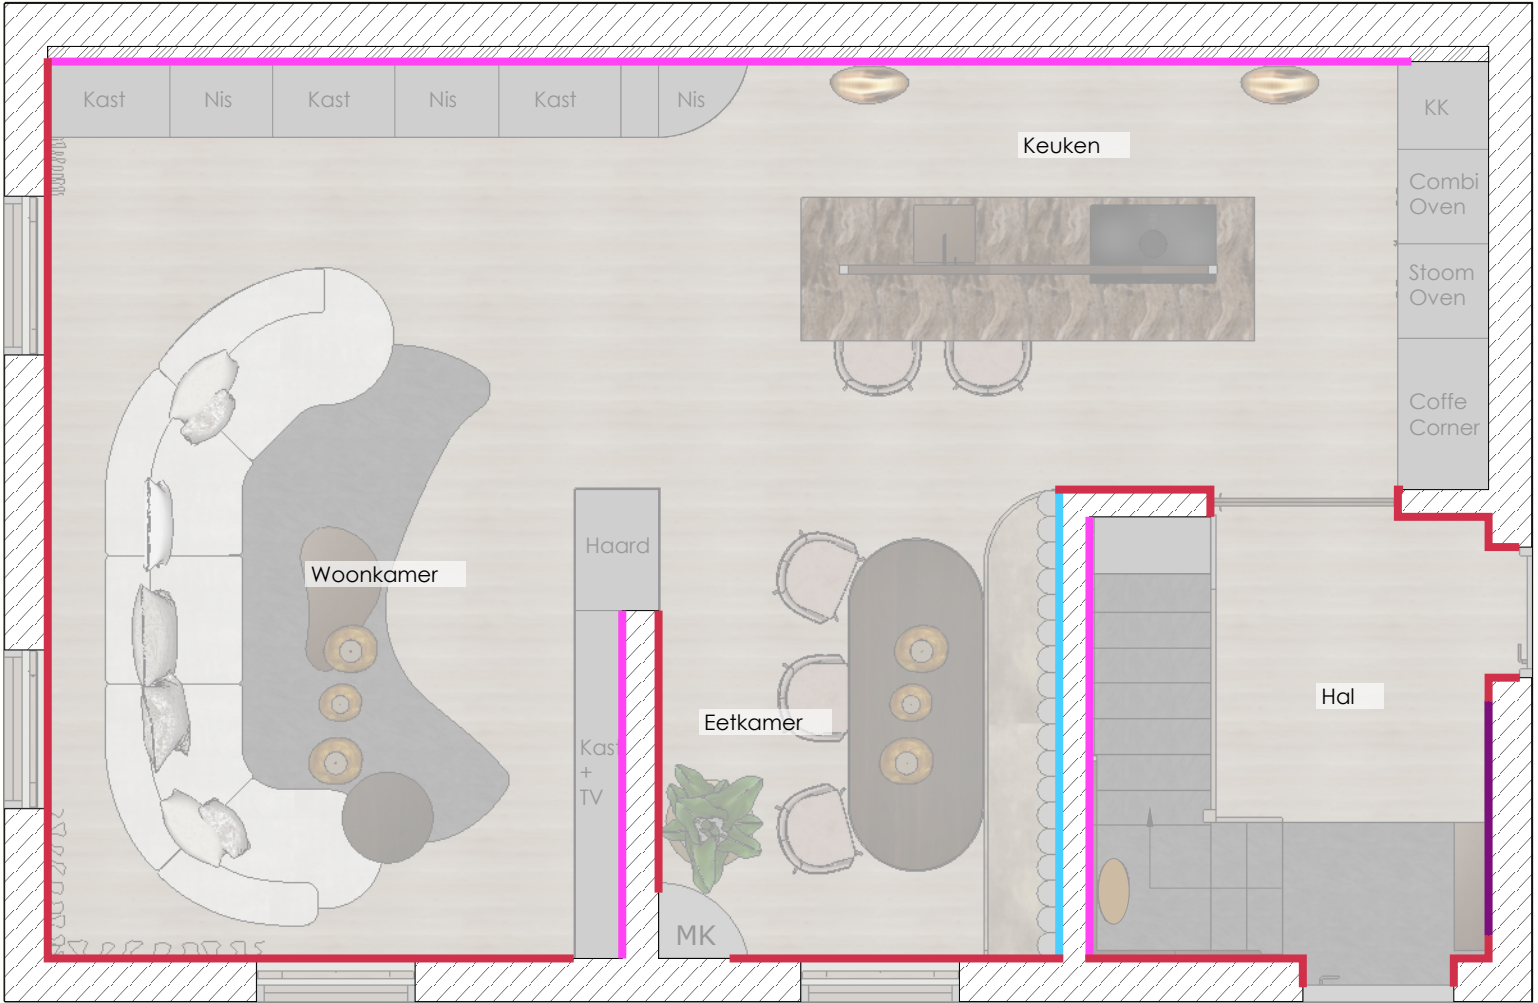

Plafond in Pure & Original Old Flax
Gordijnrail in stuc



Sausklaar stucwerk
Pure & Original Old Flax

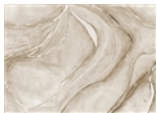



Behang
Rebel Walls
Type: Water Color Flow




Koudschuim gestoffeerd
Aristide Markle Taupe 250




Getint spiegelglas

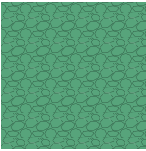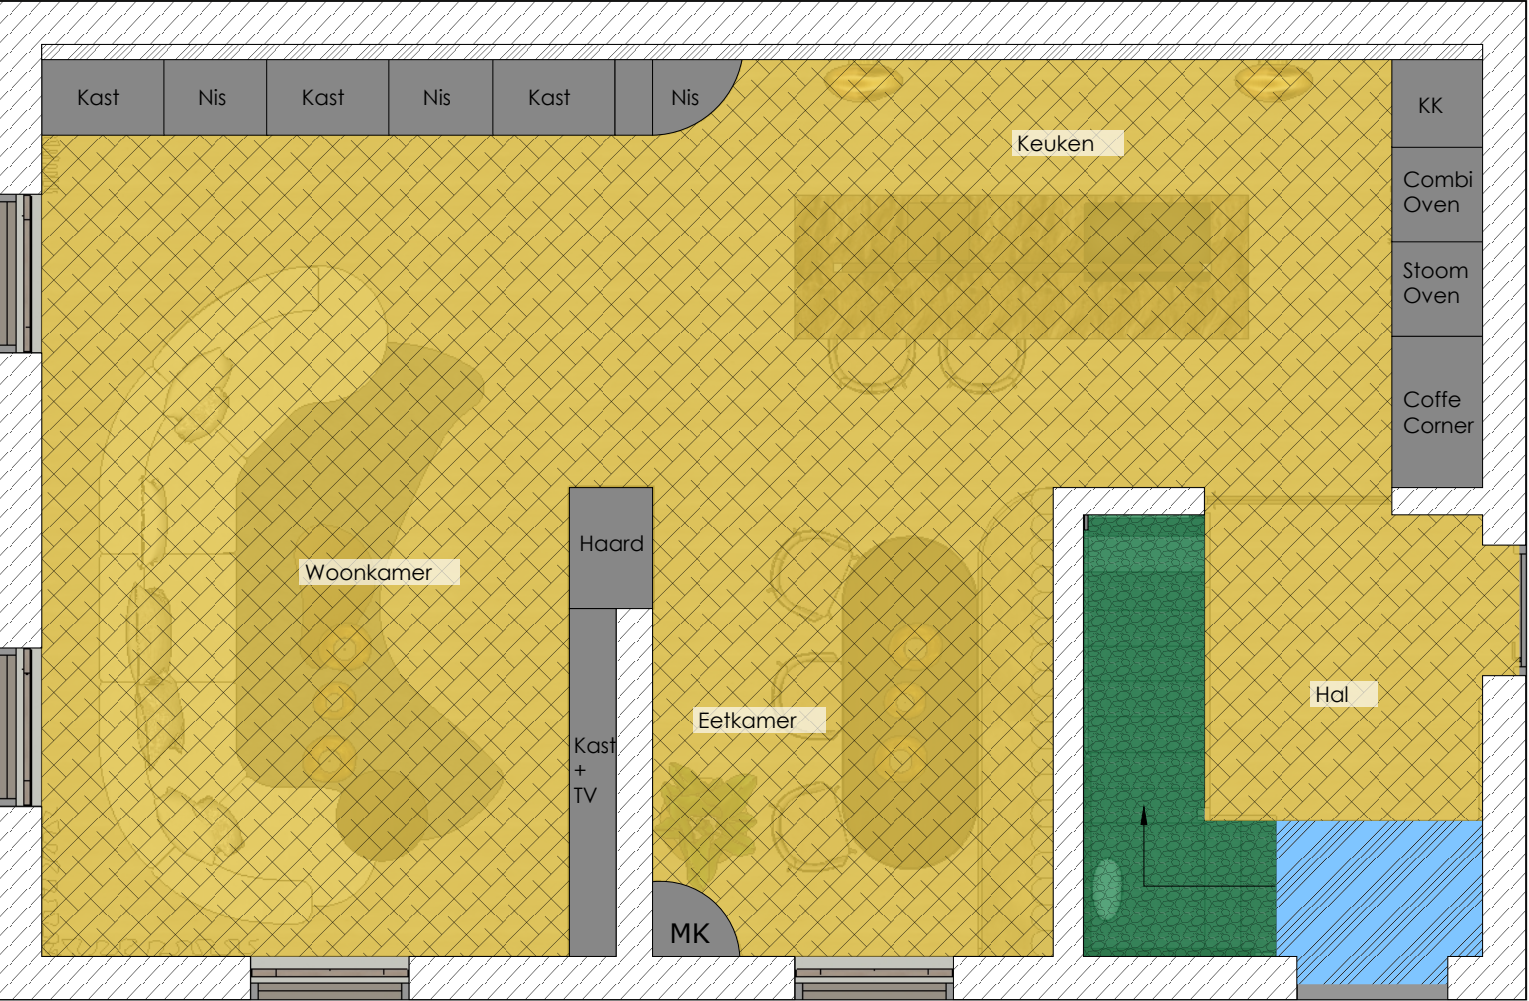


Traptredes: Bekleed met
stoffering af te stemmen op
samples Aventura carpets
Basic tione
Exacte merk en type n.t.b.

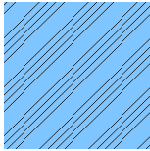

Aventura carpets Basic
Tione 10mm kleur n.t.b.
Af te stemmen op samples
Totaal m2: 1,5 m2

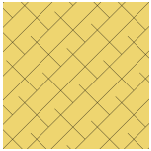

Houten vloer
rechte plank
geolied, gebeitst in n.t.b.
kleur in showroom
Totaal m2: 54,4 m2

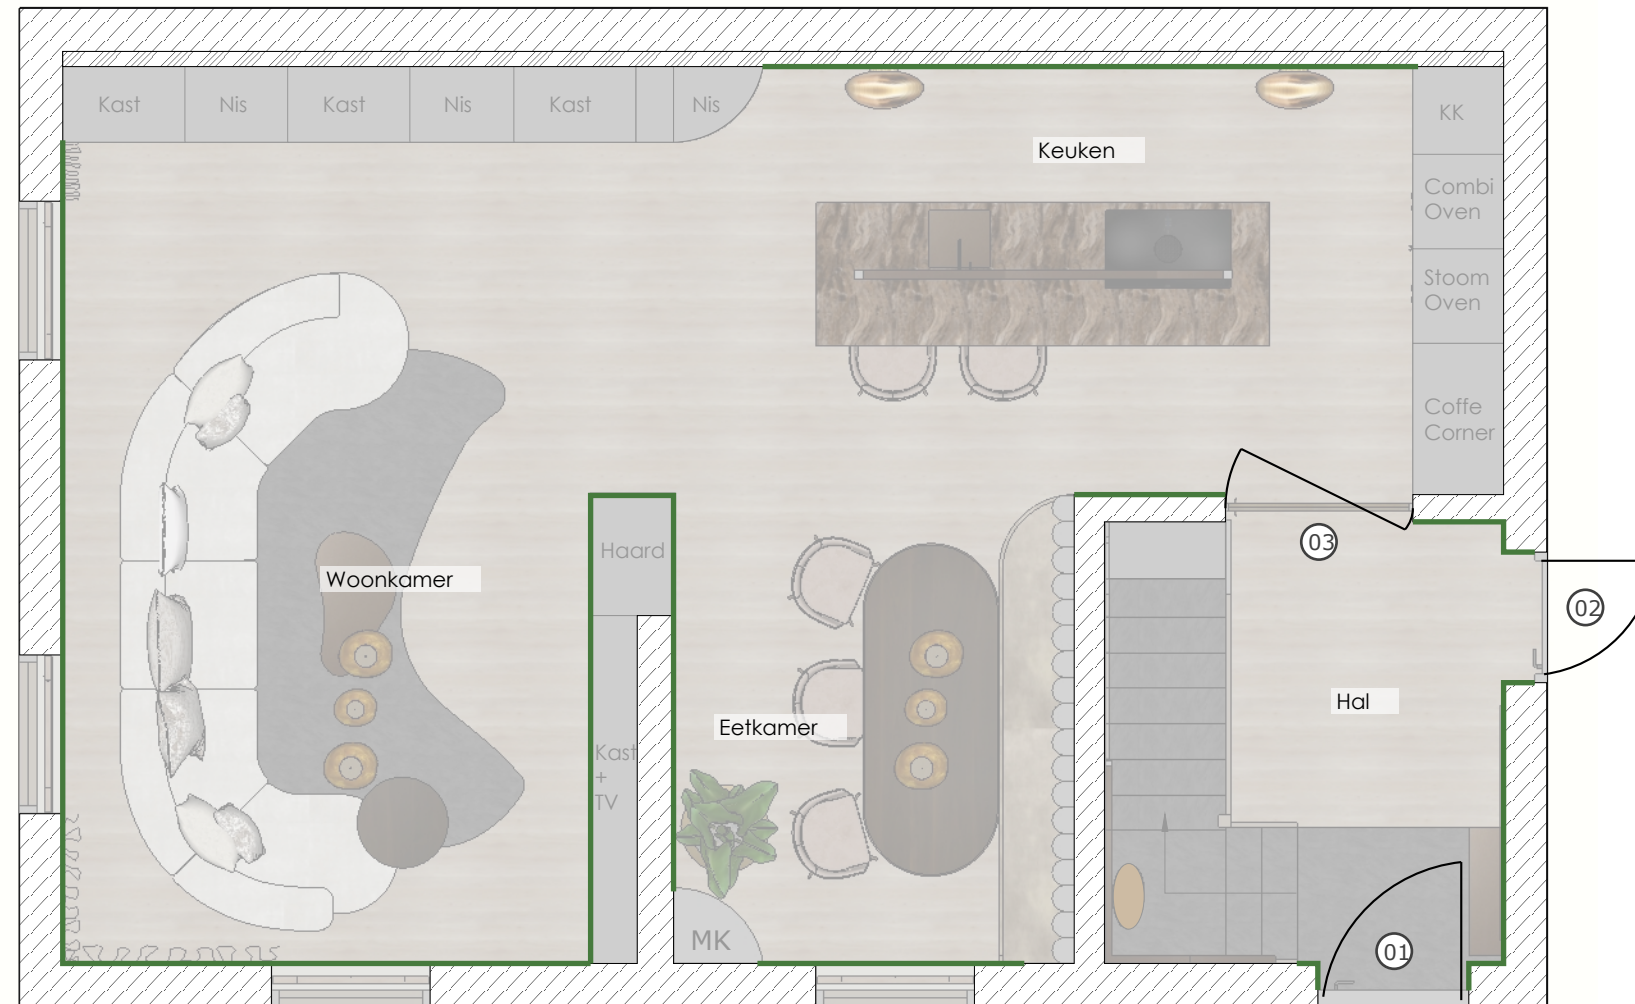

MDF Plint 120mm hoog, 12mm dik
MDF schilderen in kleur Pure and
Original Old Flax

01 Bestaande voordeur
Binnenzijde: Pure and Original Old Flax
Kozijn: Pure and Original Old Flax
Klink: merk: n.t.b.

02 Bestaande binnendeur
Kleur: Pure and Original Old Flax
Kozijn: Pure and Original Old Flax
Klink: merk: n.t.b.

03 Taatsdeur 2460x1240
Kleur: Licht gefint glas en rank stalen frame
in Nobel brons finish
Greep: maatwerk
Zie maatwerk tekening




DEFINITIEF ONTWERP
PROJECT: ACHTERSTRAAT 1, LIENDEN

EXACTE MATEN IN HET WERK TE CONTROLEREN

THOMASDEGIER
WORLD OF INTERIOR DESIGN

Onderwerp: Deurenplan
Datum: 19-12-2025

Versie: V1
Formaat: A3
Schaal: 1:50

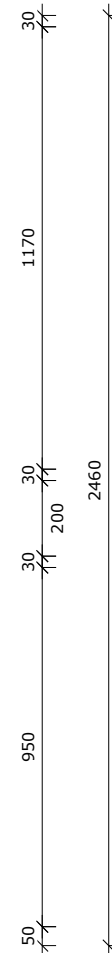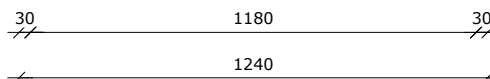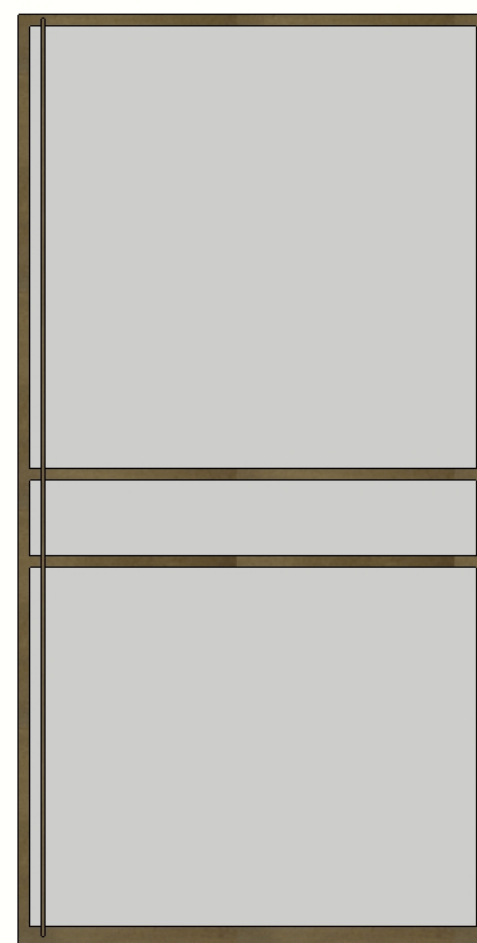

03

Taatsdeur 2460x1240
Kleur: Licht gefint glas en rank stalen frame
in Nobel brons finish
Greep: maatwerk
Zie maatwerk tekening