


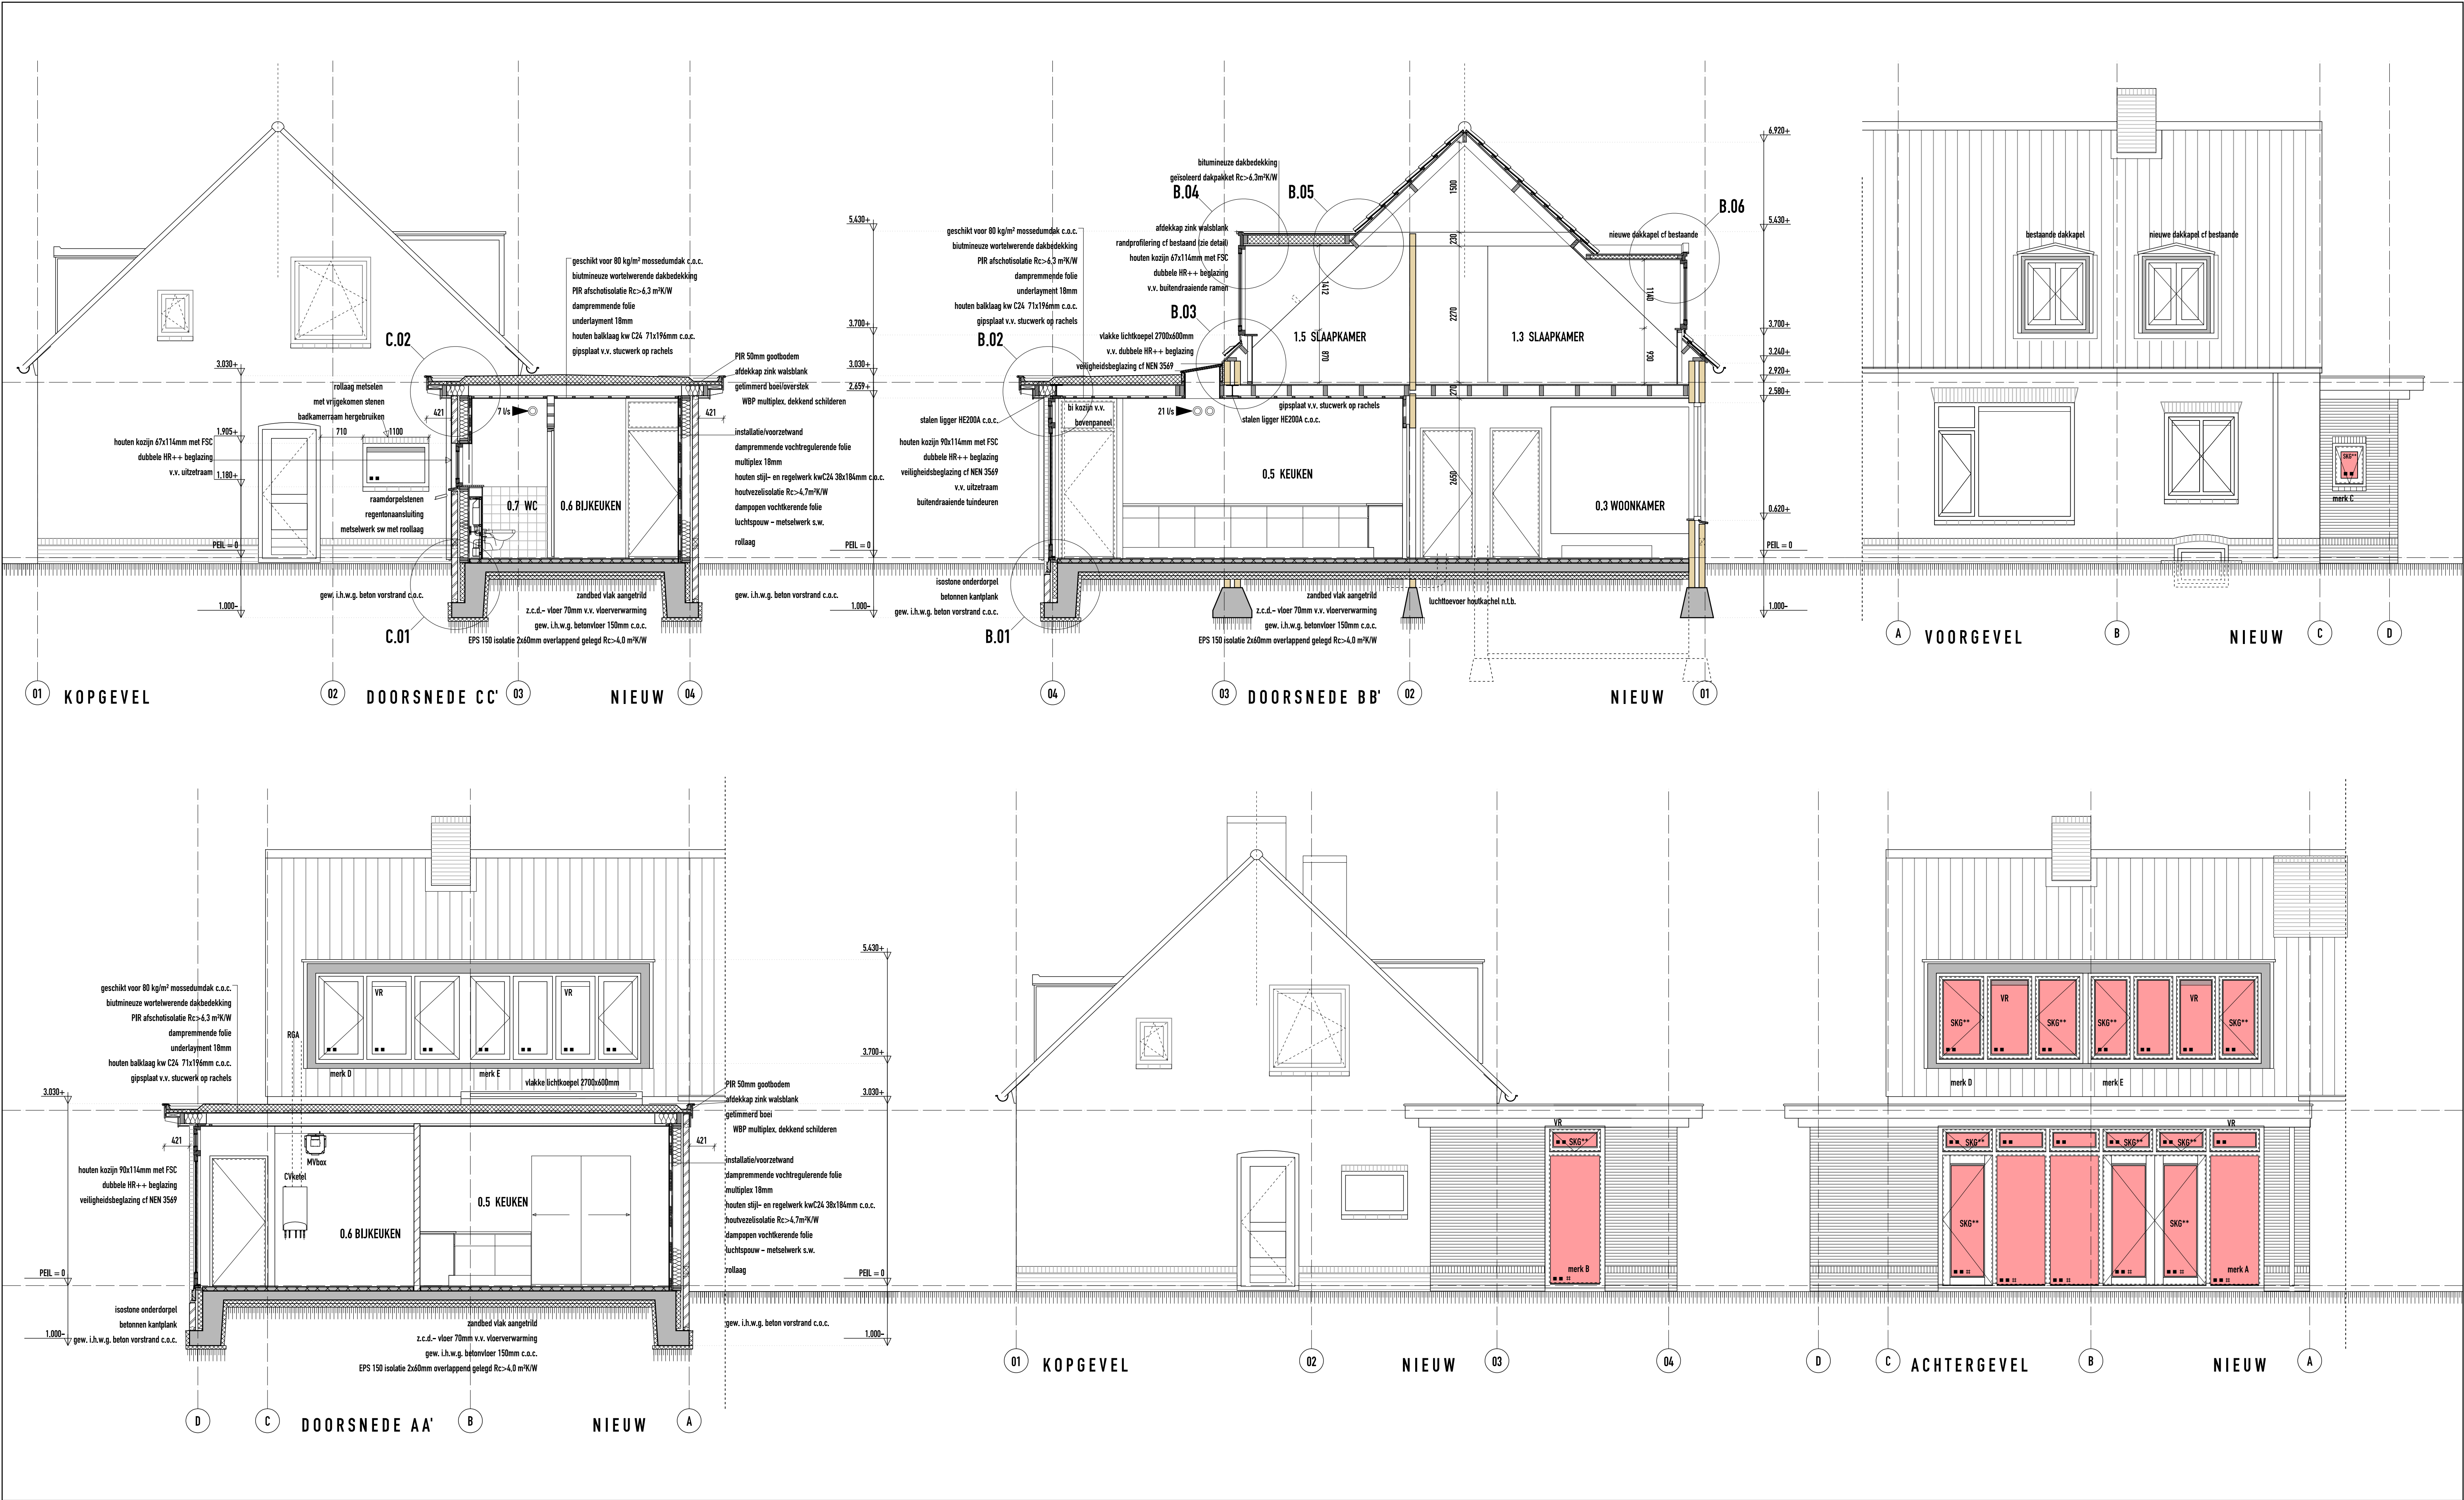

RENOVOI

MATERIAALAANDUIDINGEN

bestaande steenachtige constructie

te verwijderen bestaande constructie, steenachtig

gew. l.h.w.g. beton vuilwerk

prefab beton onderdelen

cellenbeton

metselwerk met baksteen, sw

metselwerk met betonsteen, sw

porisietsteen, kalkzandsteen, baksteen, klinkers, wv

lichte scheidingwand binnen

zand-cement dekvloer

glasbouwstenen

staalprofielen c.o.c.

thermisch isolatiemateriaal EPS - XPS - PUR

thermisch isolatiemateriaal glas- v. las of minerale wol

KOZIJNEN EN TIMMERWERKEN

kozijnhout - raamhout - beglazing

geïsoleerd paneel + buitenbekleding

prefab houtskelbouwwand

houtkwaliteit C24 tenzij anders vermeld

kruisings gelamineerd hout

hang- en sluitwerk

inbraakwerende klasse 2 cf. NEN 5096

isolerende beglazing - veiligheidsbeglazing

cf. NEN 3569

hoofdentree

AFKORTINGEN EN SYMBOLEN

M.K.

Mv

Mg

Mw

CV-WP

MV

KK

KT

GS

UG

WM

DR

c.o.c.

c.o.b.

meterkast

meters resp. elektra, gas, water

opstelplaats opwekkingsapparaat centrale verwarming

opstelplaats mechanische ventilatie-box

opstelplaats koelkast - kooktoestel

opstelplaats gootsteen - uitstortgootsteen

opstelplaats wasmachine - droger

conform opgave constructeur - bouw fysicus

TECHNISCH BLAD

overspanningsrichting

laten / liggen

houten balk met verankering of opp. constr.

houtkwaliteit C24 tenzij anders vermeld

vloerdikte - peilmaat constructievloer

radiator

W-INSTALLATIES

7.0 l/s

14.0 l/s

13.6 l/s

50mm

GS

UG

rioolpomp

N.O.

ventilatie afvoer - invoer - capaciteit

cf. NEN 1078, NPR 1088 en ventilatiebalans

ventilatiebevoering via roosters, capaciteit

cf. ventilatiebalans

overstromvoorziening, capaciteit

cf. doorstroomdeuropening

riolering - liggende leiding met diameter VWA

HWA

capaciteit en uitmonding rioolaansluitpunten cf. NEN 3215

GS: gootsteen, FT: fontein, WM: wasmachine WC: toilet

SL: standleiding, VT: wastafel, DP: doucheput, LB: ligbad

afvoerput - hemelwaterafvoer noodoverloop

lucht- en waterdichtheid cf. NEN 3215, BBI 4.205

wateraansluiting, bijvo

drinkwatervoorziening cf. NEN 1006

E-INSTALLATIES

schakelaars

verlichtingspunten

centraaldoos

wandcontactdozen

datacommunicatie

NEN 1010

E-installaties cf. NEN 1010

BRANDVEILIGHEID

wdbdo > 30 resp 60 min

zelfsluitende deur

blusmiddelen

netgekoppelde optische rookmelder cf. NEN 2555

dagmaten openingen

ALLE MATEN IN HET WERK CONTROLLEREN

UITBREIDING WOONHUIS

BURGEMEESTER GERADTSLAAN 45 6641 ZS BEUNINGEN

IN OPDRACHT VAN MARLOUS VAN DER HOOGE EN GERARD VAN ROEKEL

ONTWERPTEKENING GEVELS EN DOORSNEDEN NIEUW

werksnummer 225

tekeningsnummer BA-12

formaat - schaal A1 1:50

afdruk op A3 1:100

getekend JK

datum 20-02-2026

wjz. A --

wjz. B --

wjz. C --

wjz. D --

johnkusters

bouw kundig ontwerp en advies

E info@john-kusters.nl A Tweede Oude Hestelaan 247 6542 VH Nijmegen M 06 26442226 KvK 09186431 I www.john-kusters.nl