


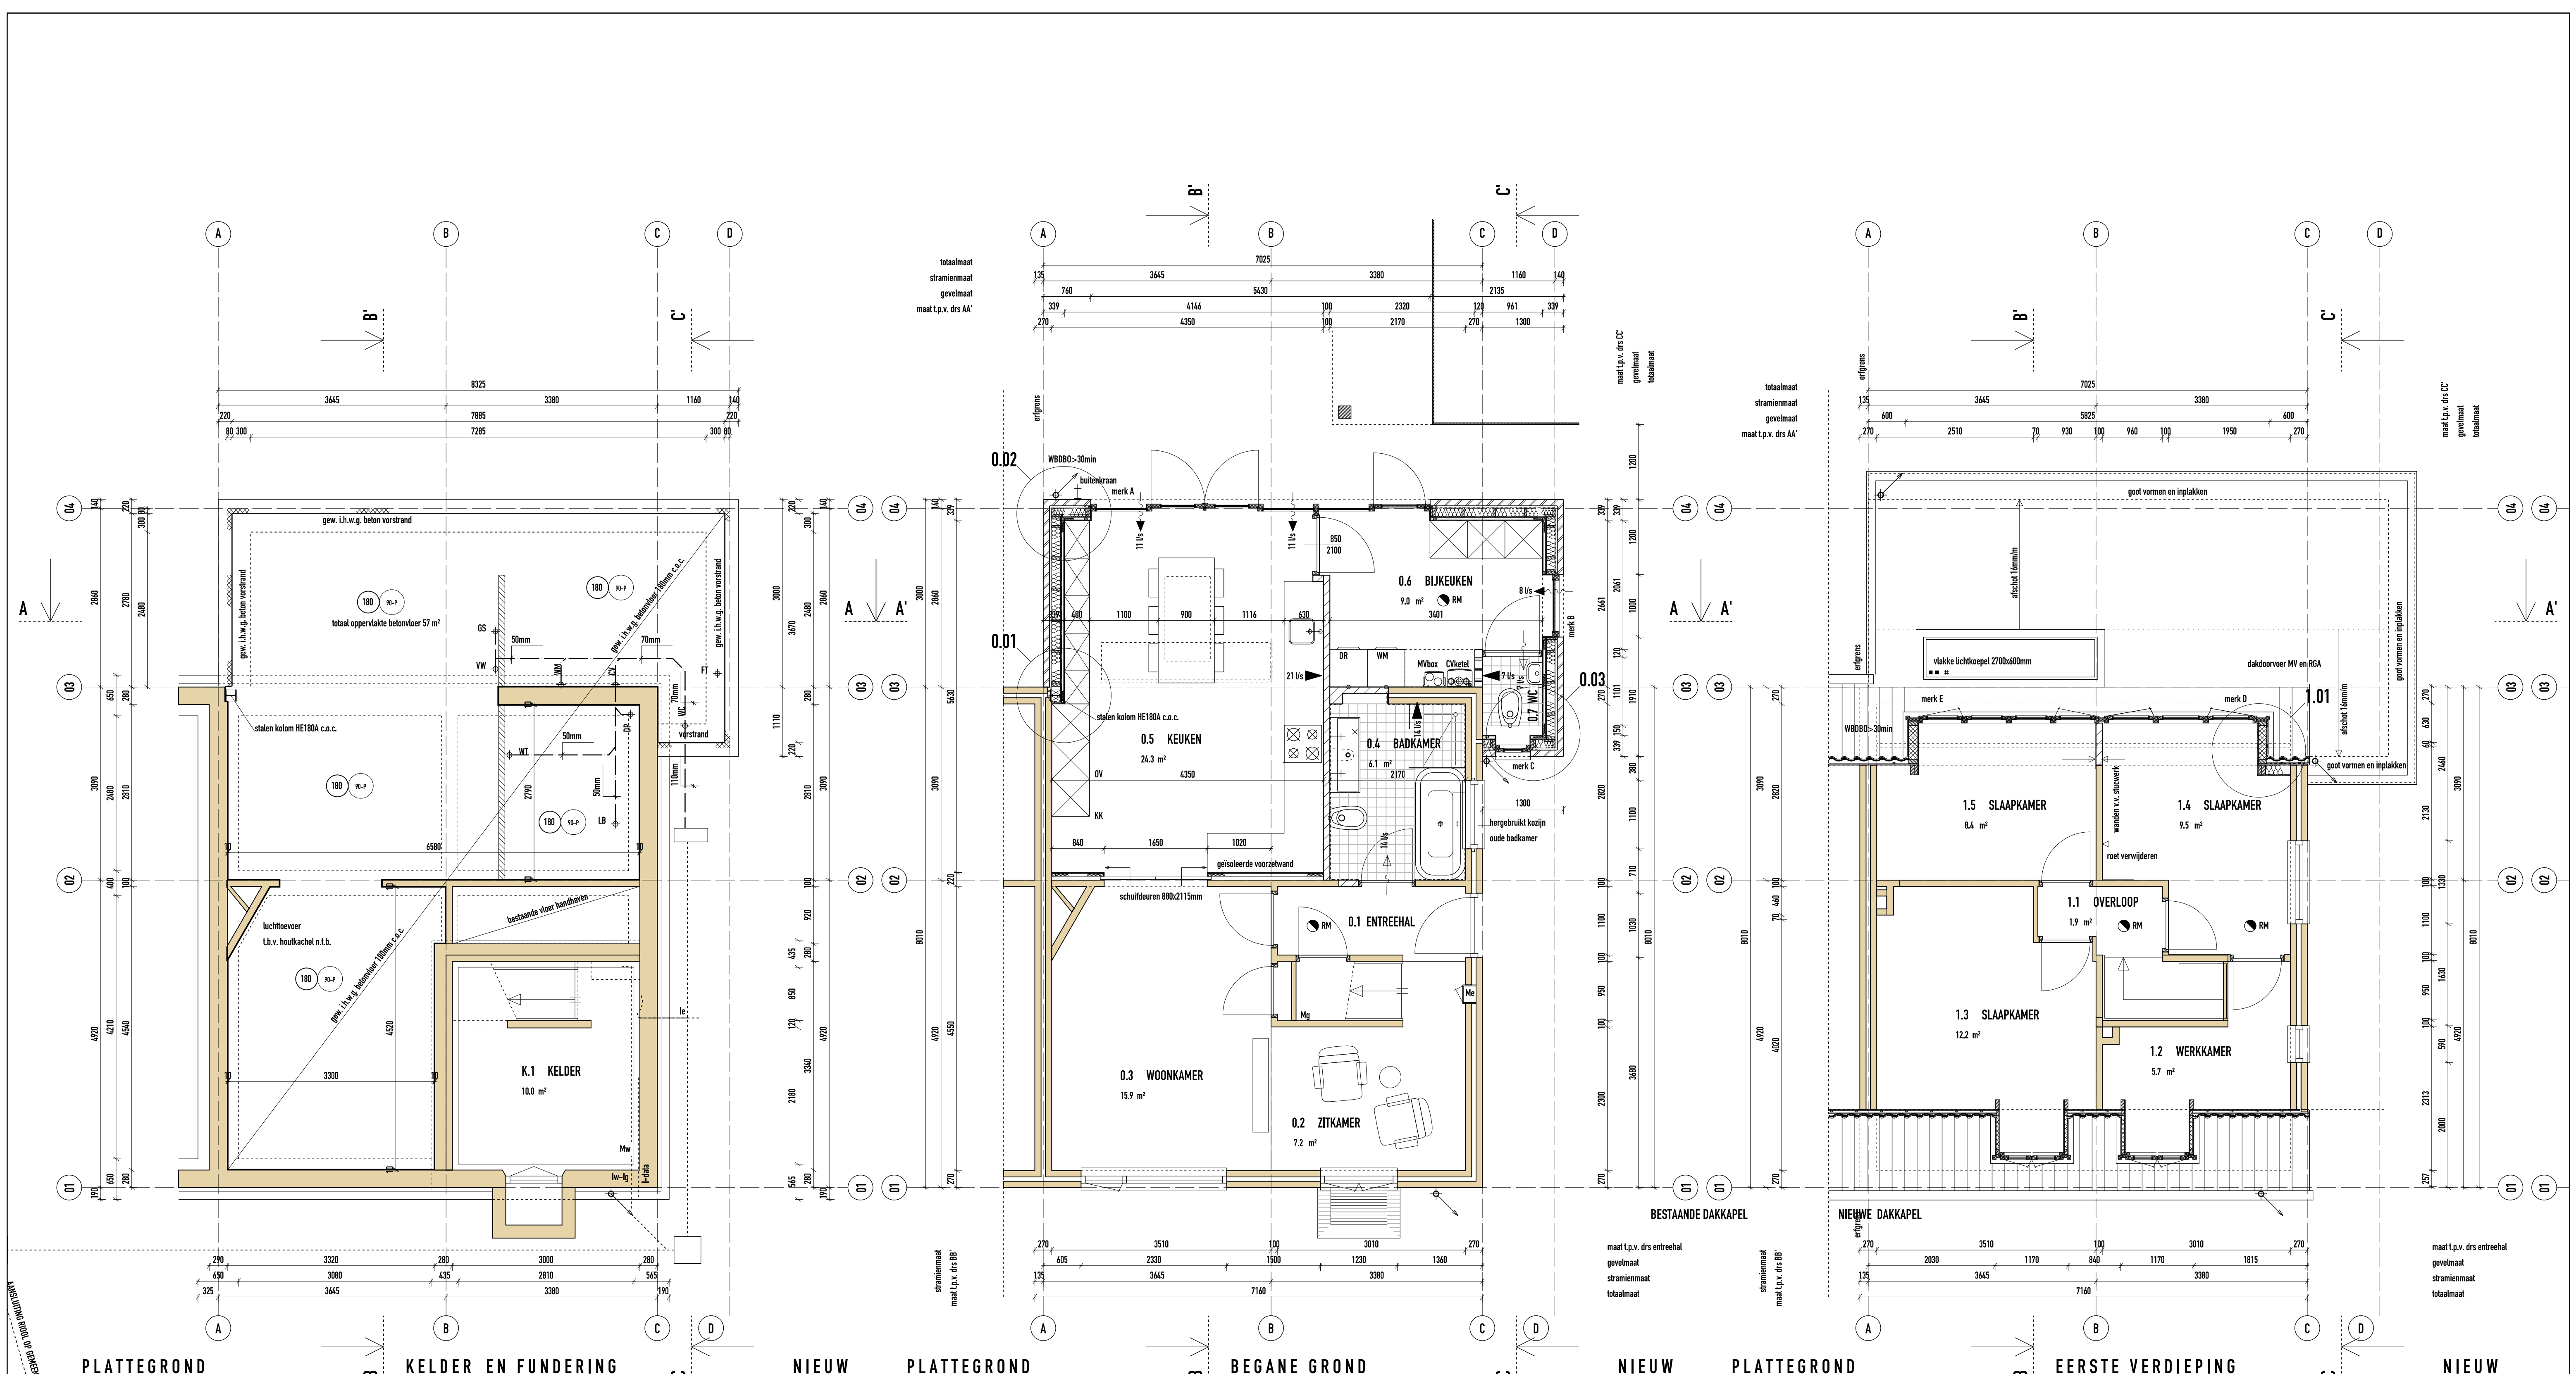

RENV001

MATERIAALAANDUIDINGEN

bestaande steenachtige constructie

te verwijderen bestaande constructie, steenachtig

gew. l.h.w.g. beton vuilwerk

prefab beton onderdelen

cellenbeton

metseelwerk met baksteen, sw

metseelwerk met betonsteen, sw

porisosteent, kalkzandsteen, baksteen, klinkers, vw

lichte scheidingwand binnen

zand-cement dekplaat

glasbouwstenen

staalprofielen c.o.c.

thermisch isolatiemateriaal EPS - XPS - PUR

thermisch isolatiemateriaal glas-, vlas of minerale wol

KOZIJNEN EN TIMMERWERKEN

kozijnhout - raamhout - beglazing

geïsoleerd paneel + buitenbekleding

prefab houtskelbouwplaat

houtkwaliteit C24 tenzij anders vermeld

kruisings gelamineerd hout

hang- en sluitwerk

inbraakwerendheidsklasse 2 cf. NEN 5096

isolerende beglazing - veiligheidsbeglazing

cf. NEN 3569

hoofdentree

AFKORTINGEN EN SYMBOLEN

M.K.

M.K.

M.K.

meterkast

meters resp. elektra, gas, water

CY-WP

opstelplaat opwekkingsapparaat centrale verwarming

opstelplaats mechanische ventilatie-box

KK

KT

opstelplaats koelkast - kooktoestel

opstelplaats gootsteen - uitstortgootsteen

GS

UG

opstelplaats gootsteen - uitstortgootsteen

opstelplaats wasmachine - droger

WM

DR

opstelplaats wasmachine - droger

conform opgave constructeur - bouwtechnicus

TECHNISCH BLAD

overspanningsrichting

laten / ligger

houden balk met verankering cf. opg. constr.

houtkwaliteit C24 tenzij anders vermeld

vloerdikte - peilmaat constructievloer

radiator

W-INSTALLATIES

7.0 l/s

ventilatie afvoer - invoer - capaciteit

cf. NEN 1078, NPR 1088 en ventilatiebalans

14.0 l/s

ventilatiebevoering via roosters, capaciteit

cf. ventilatiebalans

13.6 l/s

overstromvoorziening, capaciteit

cf. doorsnoodonderzoeken

50mm

riolering - liggende leiding met diameter VWA HWA

capaciteit en uitrustingsrioolaanstulpunten cf. NEN 3215

GS

GS: gootsteen, FT: fontein, WM: wasmachine WC: toilet

SL: standleiding, WT: wastafel, DP: doucheput, LB: ligbad

N.O.

afvoerput - hemelwaterafvoer noodoverloop

lucht- en waterdichtheid cf. NEN 3215, Bbl 4.205

wateraansluiting, bijvo

drinkwatervoorziening cf. NEN 1006

E-INSTALLATIES

schakelaars

verlichtingspunten

centraaldoos

wandcontactdozen

datacommunicatie

NEN 1010

E-installaties cf. NEN 1010

BRANDVEILIGHEID

wdbto > 30 resp 60 min

zelfsluitende deur

blusmiddelen

netgekoppelde optische rookmelder cf. NEN 2555

dagmaten openingen

ALLE MATEN IN HET WERK CONTROLLEREN

UITBREIDING WOONHUIS

BURGEMEESTER GERADTSLAAN 45 6641 ZS BEUNINGEN

IN OPDRACHT VAN MARLOUS VAN DER HOOGTE EN GERARD VAN ROEKEL

BESTEK TEKENING PLATTEGRONDEN NIEUW

werksnummer 225

tekeningsnummer BA-11

formaat - schaal A1 1:50

afdruk op A3 1:100

getekend JK

datum 20-02-2026

wjz. A --

wjz. B --

wjz. C --

wjz. D --

johnkusters

bouw kundig ontwerp en advies

E info@johnkusters.nl A Tweede Oude Heselaaan 247 6542 VH Nijmegen M 06 26442226 KvK 09186431 I www.johnkusters.nl