


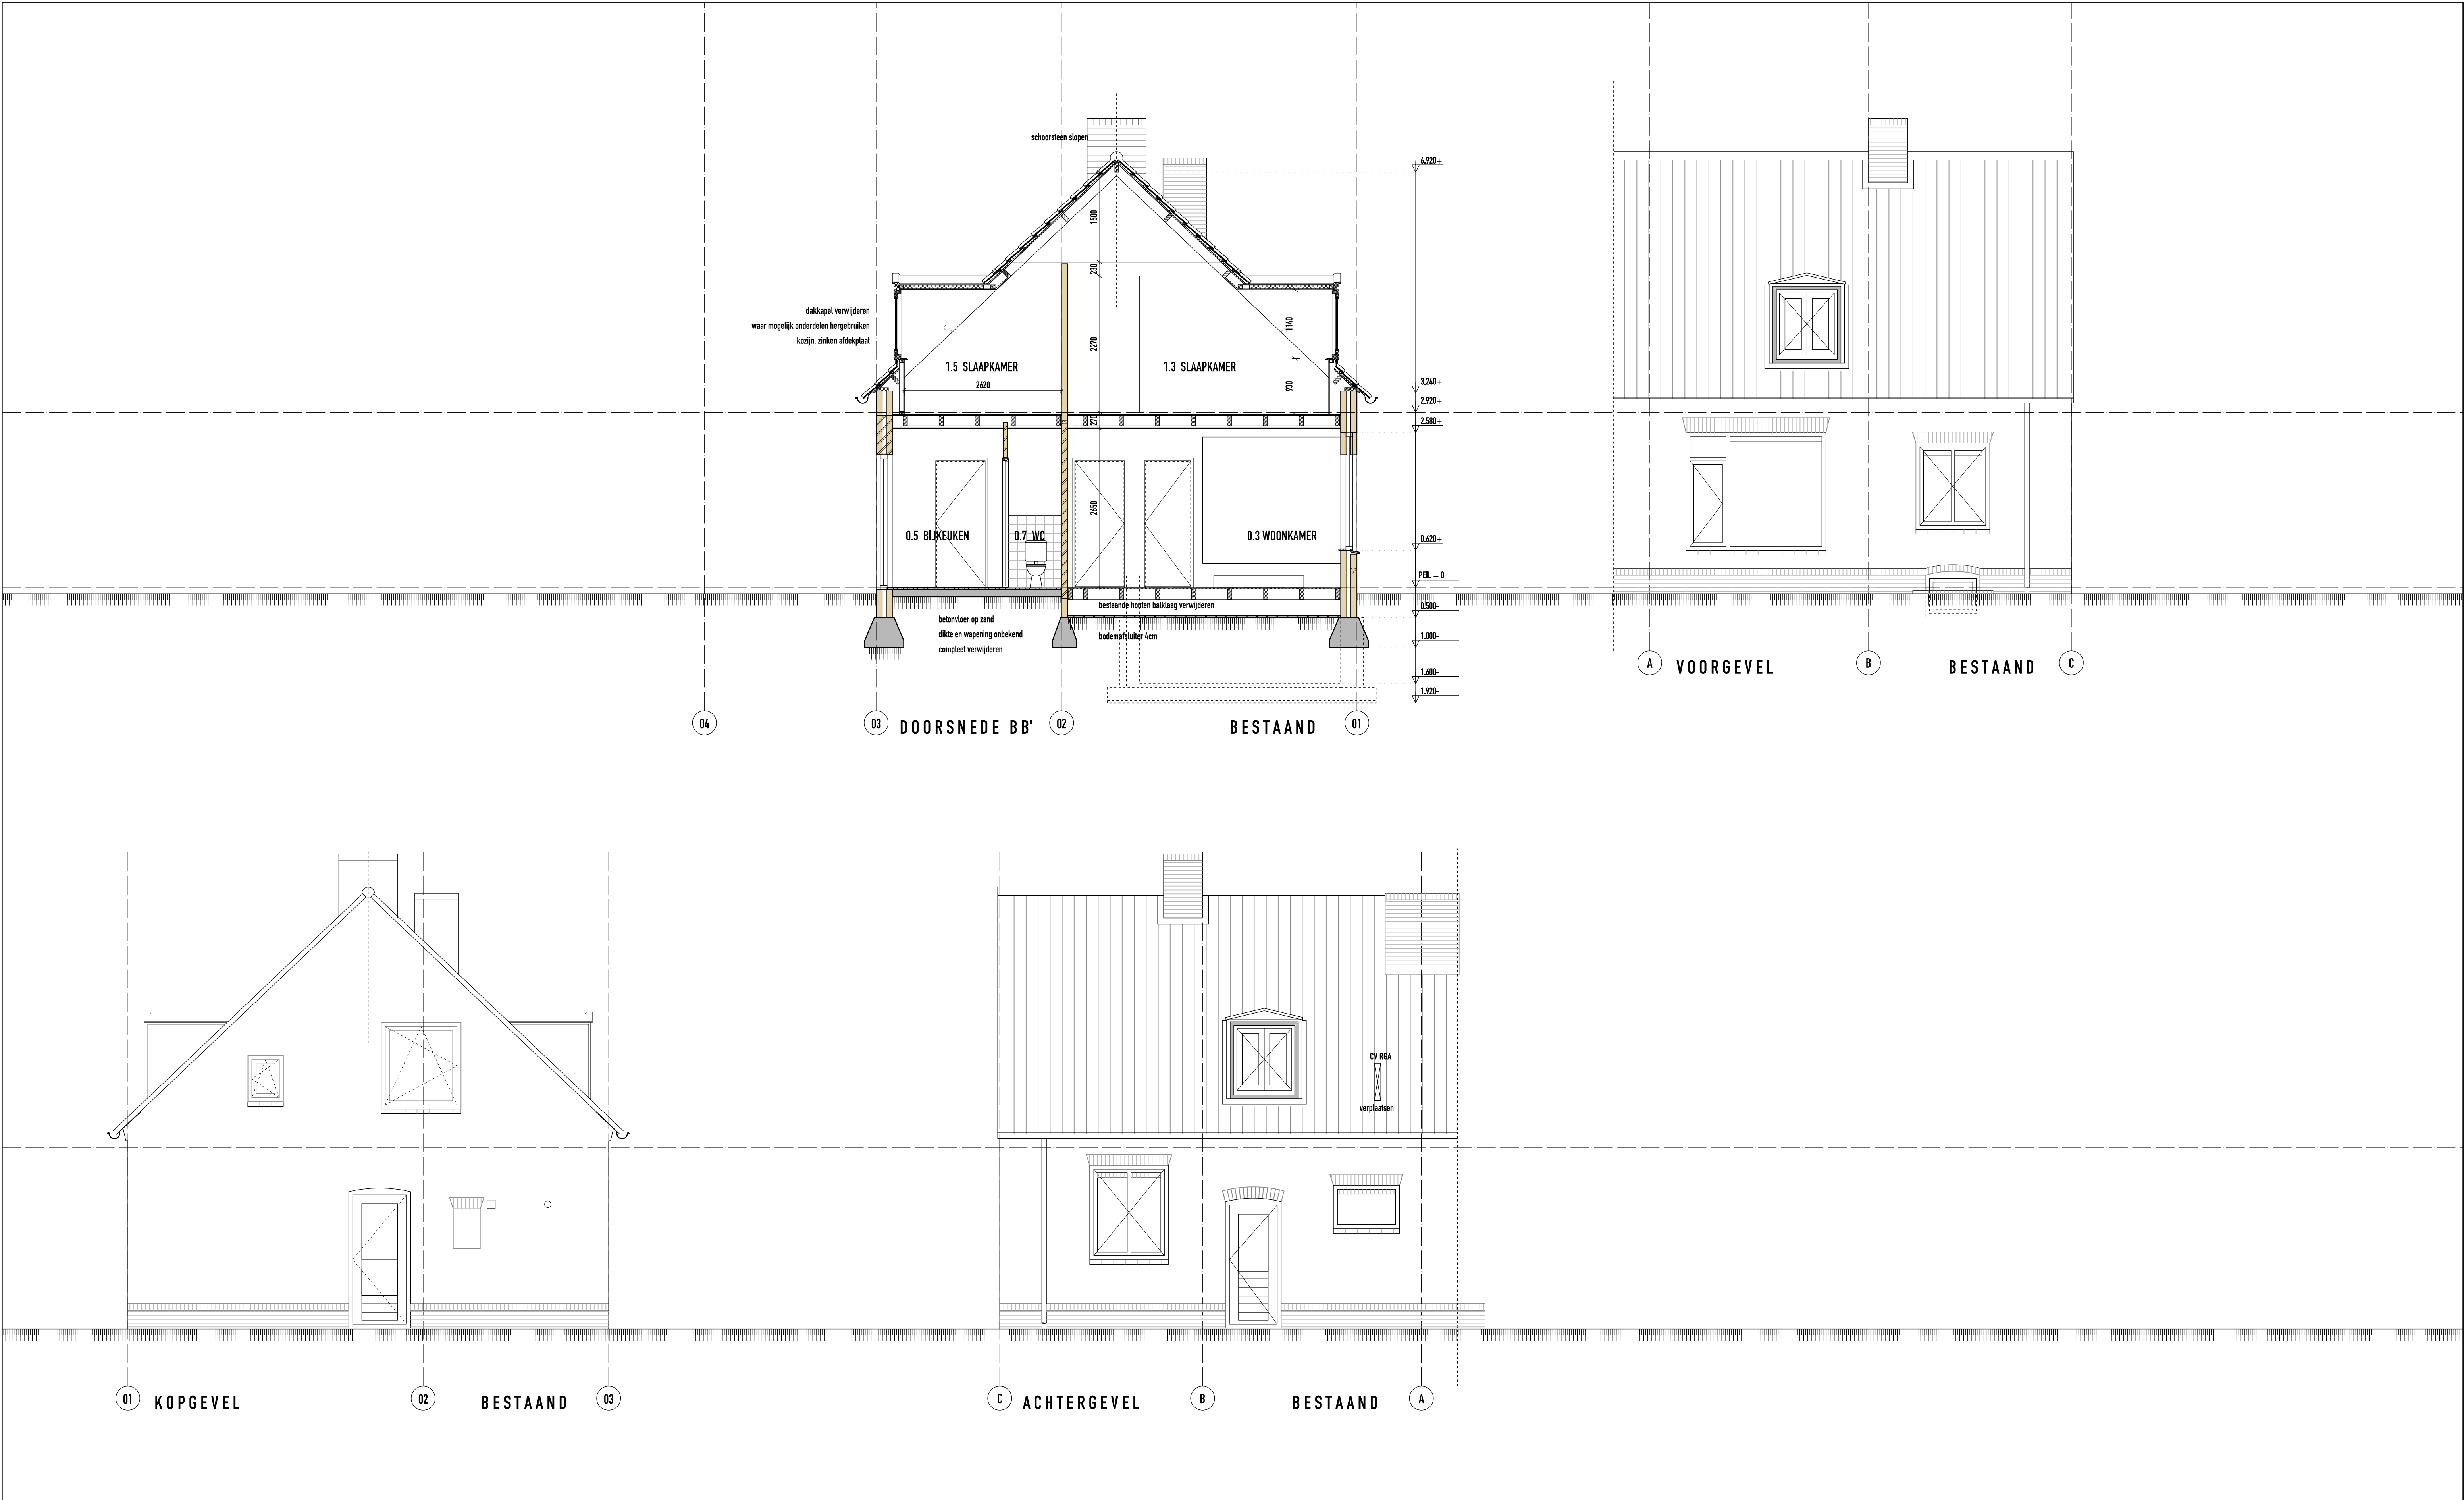

RENV001

MATERIAALAANDUIDINGEN

bestaande steenachtige constructie

te verwijderen bestaande constructie, steenachtig

gew. i.h.w.g. beton vuilwerk

prefab beton onderdelen

cellenbeton

metselwerk met baksteen, sw

metselwerk met betonsteen, sw

porisosteent, kalkzandsteen, baksteen, klinkers, vv

lichte scheidingwand binnen

zand-cement dekplaat

glasbouwstenen

staalprofielen c.o.c.

thermisch isolatiemateriaal EPS - XPS - PUR

thermisch isolatiemateriaal glas-, vlas of minerale wol

kozijnhout - raamhout - beglazing

geïsoleerd paneel + buitenbekleding

prefab houtskelbouwwand

houtkwaliteit C24 tenzij anders vermeld

kruisings gelamineerd hout

hang- en sluitwerk

inbraakwerendheidsklasse 2 cf. NEN 5076

isolerende beglazing - veiligheidsbeglazing

cf. NEN 3569

SGK **

hoofdentree

M.K.

Mu

Mg

Mw

meterkast

meters resp. elektra, gas, water

CV-WP

opstelplaats opwekkingsapparaat centrale verwarming

MV

opstelplaats mechanische ventilatie-box

KK

KT

opstelplaats koelkast - kooktoestel

GS

UG

opstelplaats gootsteen - uitstortgootsteen

WM

DR

opstelplaats wasmachine - droger

c.o.c.

c.o.b.

conform opgave constructeur - bouwfysicus

TECHNISCH BLAD

overspanningsrichting

laten / ligger

houden balk met verankering cf. opg. constr.

houtkwaliteit C24 tenzij anders vermeld

150

200+

vloerdikte - peilmaat constructievloer

radiator

W-INSTALLATIES

7.0 l/s

ventilatie afvoer - invoer - capaciteit

cf. NEN 1078, NPR 1088 en ventilatiebalans

14.0 l/s

cf. ventilatiebalans

13.6 l/s

overstromvoorziening, capaciteit

50mm

rioolpomp

N.O.

afvoerput - hemelwaterafvoer

noodoverloop

lucht- en waterdichtheid cf. NEN 3215, Bbl 4.205

watersluiting, bijvo

drinkwatervoorziening cf. NEN 1006

E-INSTALLATIES

schakelaars

verlichtingspunten

centraaldoos

wandcontactdozen

datacommunicatie

NEN 1010

E-installaties cf. NEN 1010

BRANDVEILIGHEID

wdbto > 30 resp 60 min

zelfsluitende deur

blusmiddelen

netgekoppelde optische rookmelder cf. NEN 2555

900

2200

dagmaten openingen

ALLE MATEN IN HET WERK CONTROLEREN

UITBREIDING WOONHUIS

BURGEMEESTER GERADTSLAAN 45 6641 ZS BEUNINGEN

IN OPDRACHT VAN MARLOUS VAN DER HOOGE EN GERARD VAN ROEKEL

BESTEK TEKENING GEVELS EN DOORSNEDEN BESTAAND

werknnummer 225

tekeningsnummer BA-02

formaat - schaal A1 1:50

afdruk op A3 1:100

getekend JK

datum 20-02-2026

wijz. A --

wijz. B --

wijz. C --

wijz. D --

johnkusters

bouw, kundig ontwerp en advies

E info@john-kusters.nl

A Tweede Oude Hesielaan 247 6542 VH Nijmegen

M 06 26442226

KvK 09186431

I www.john-kusters.nl