


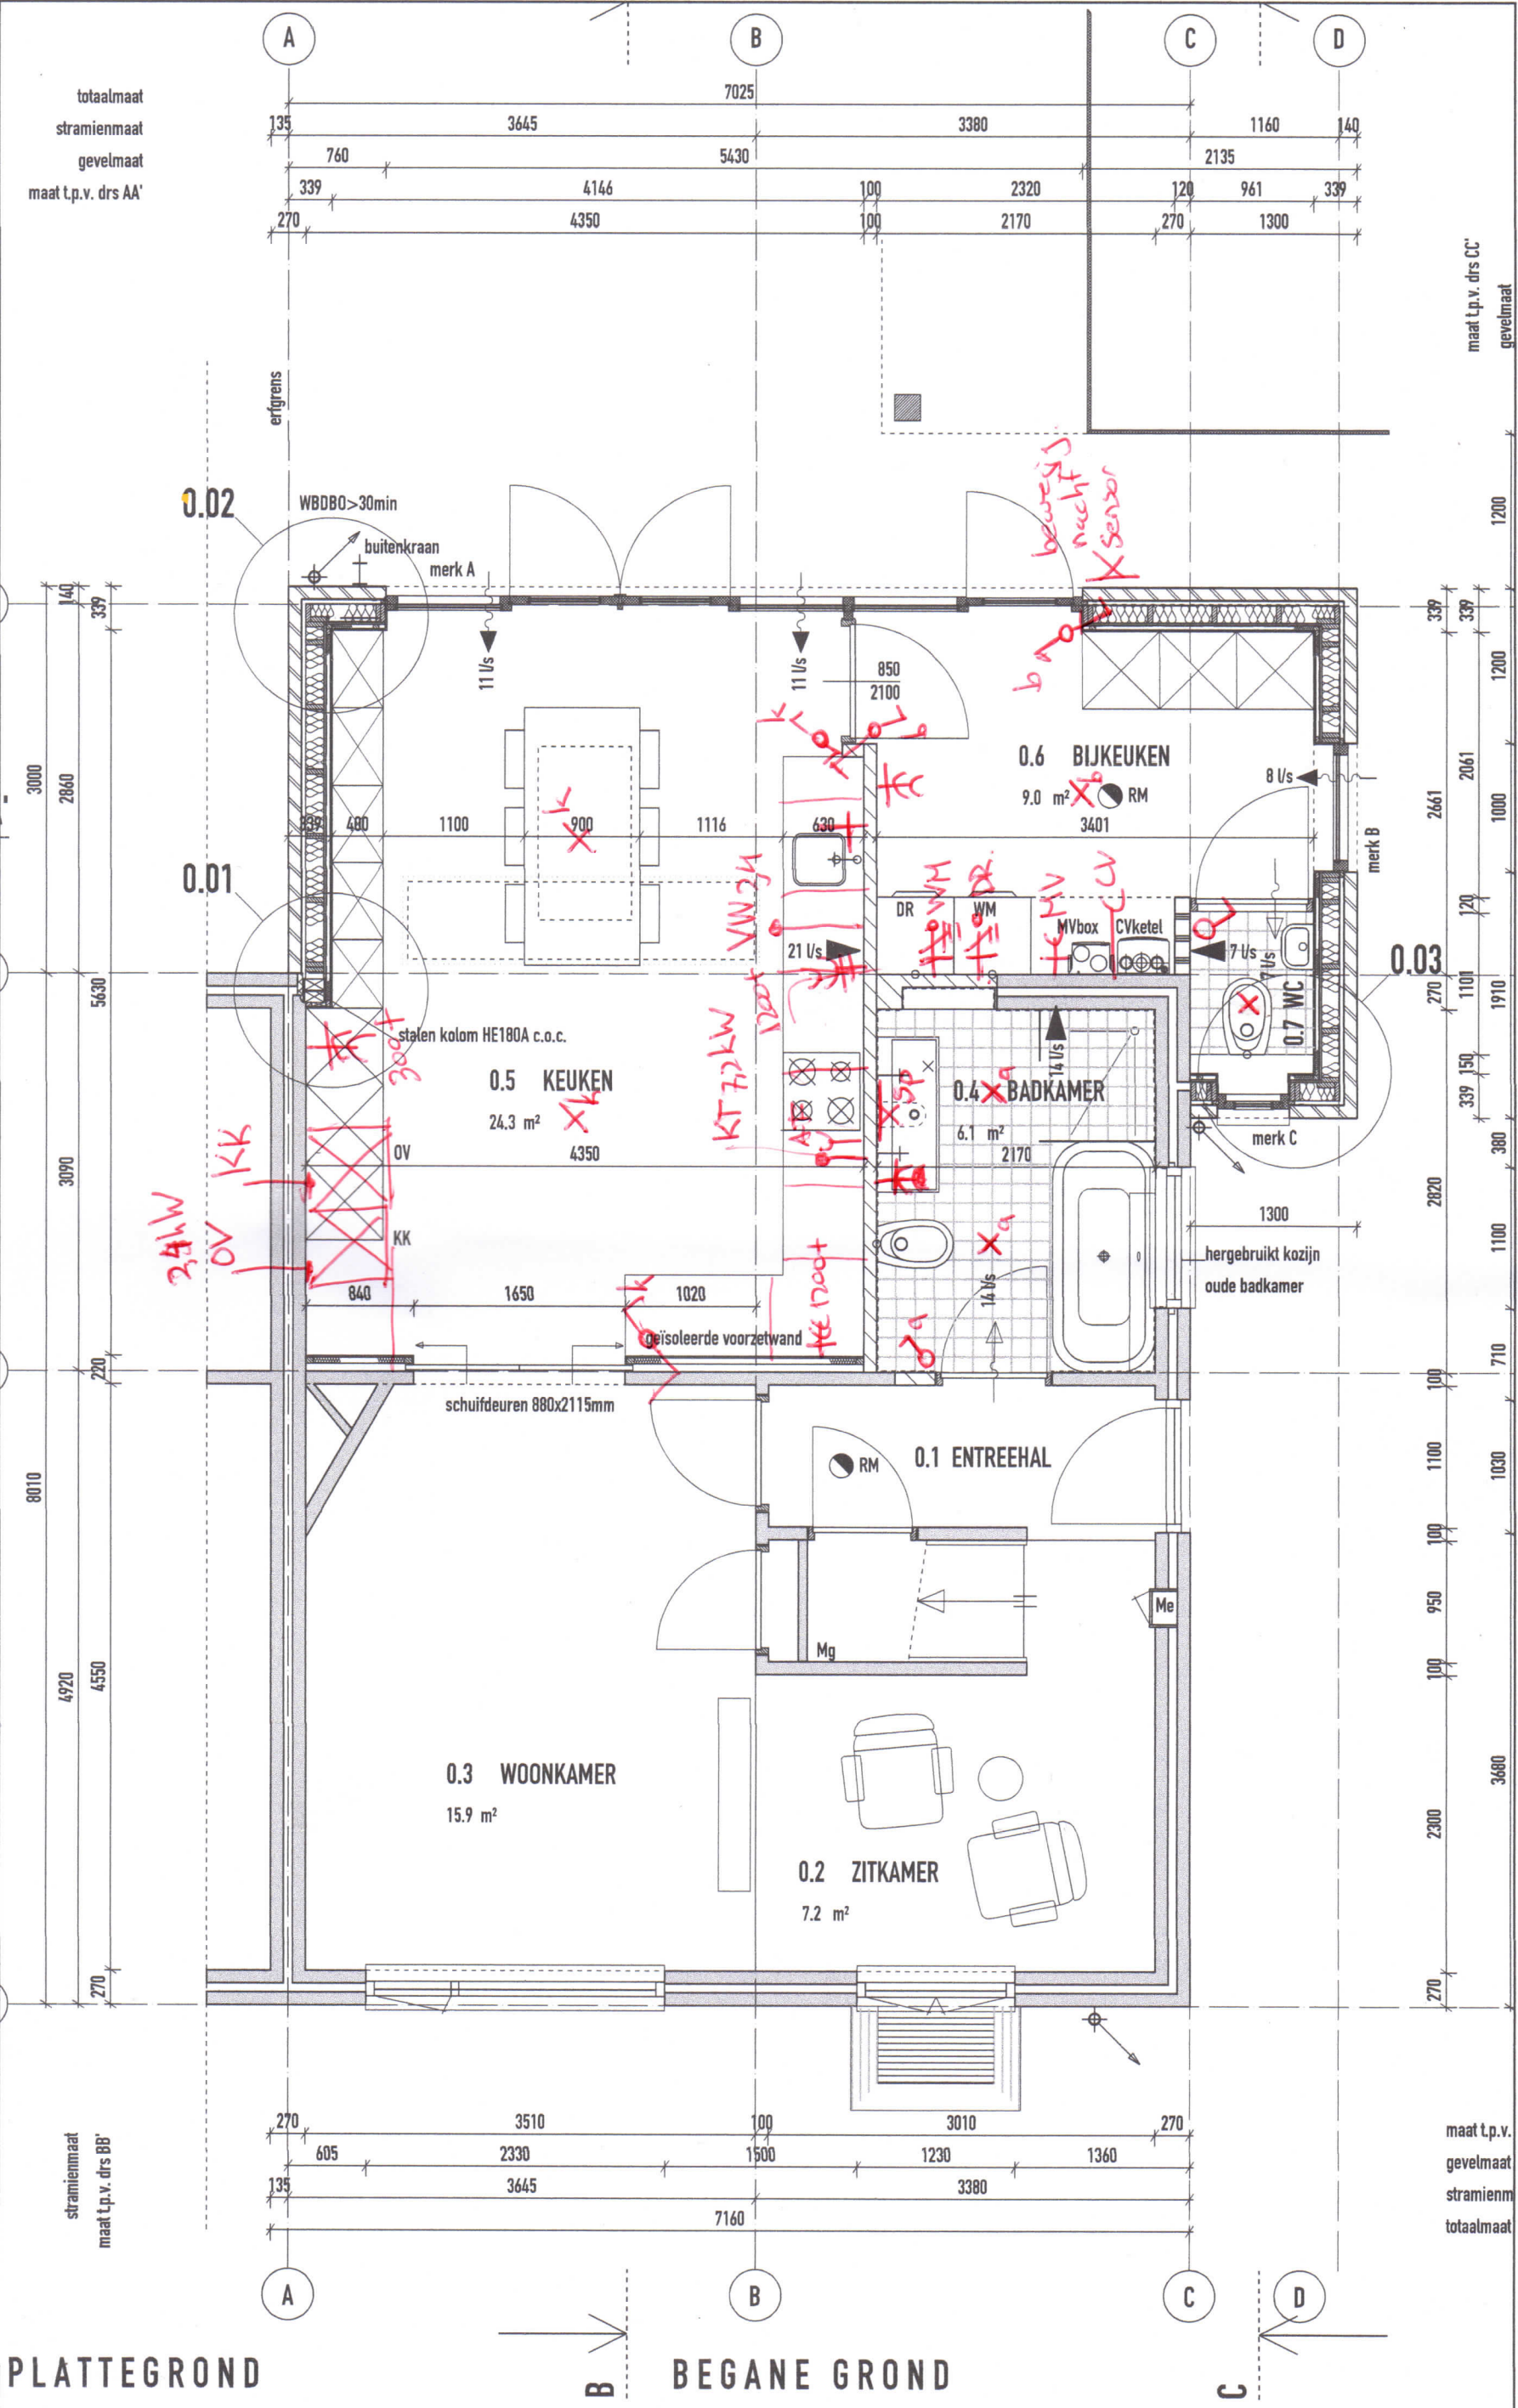

PLATTEGROND

BEGANE GROND

UITBREIDING WOONHUIS

BURGEMEESTER GERADTSLAAN 45 6641 ZS BEUNINGEN

IN OPDRACHT VAN MARLOUS VAN DER HOOOTE EN GERARD VAN ROEKEL

BESTEKTEKENING

PRINCIPEDETAILLERING

johnkusters

bouw kundig ontwerp en advies

verklaring

225

BA-15

formaat - schaal

A3 - 1:10

datum

wijz. A

E info@john-kusters.nl

A Tweede Oude Heselaan 247 6542 VH Nijmegen M 06 26442226

KvK 09186431 I www.john-kusters.nl