


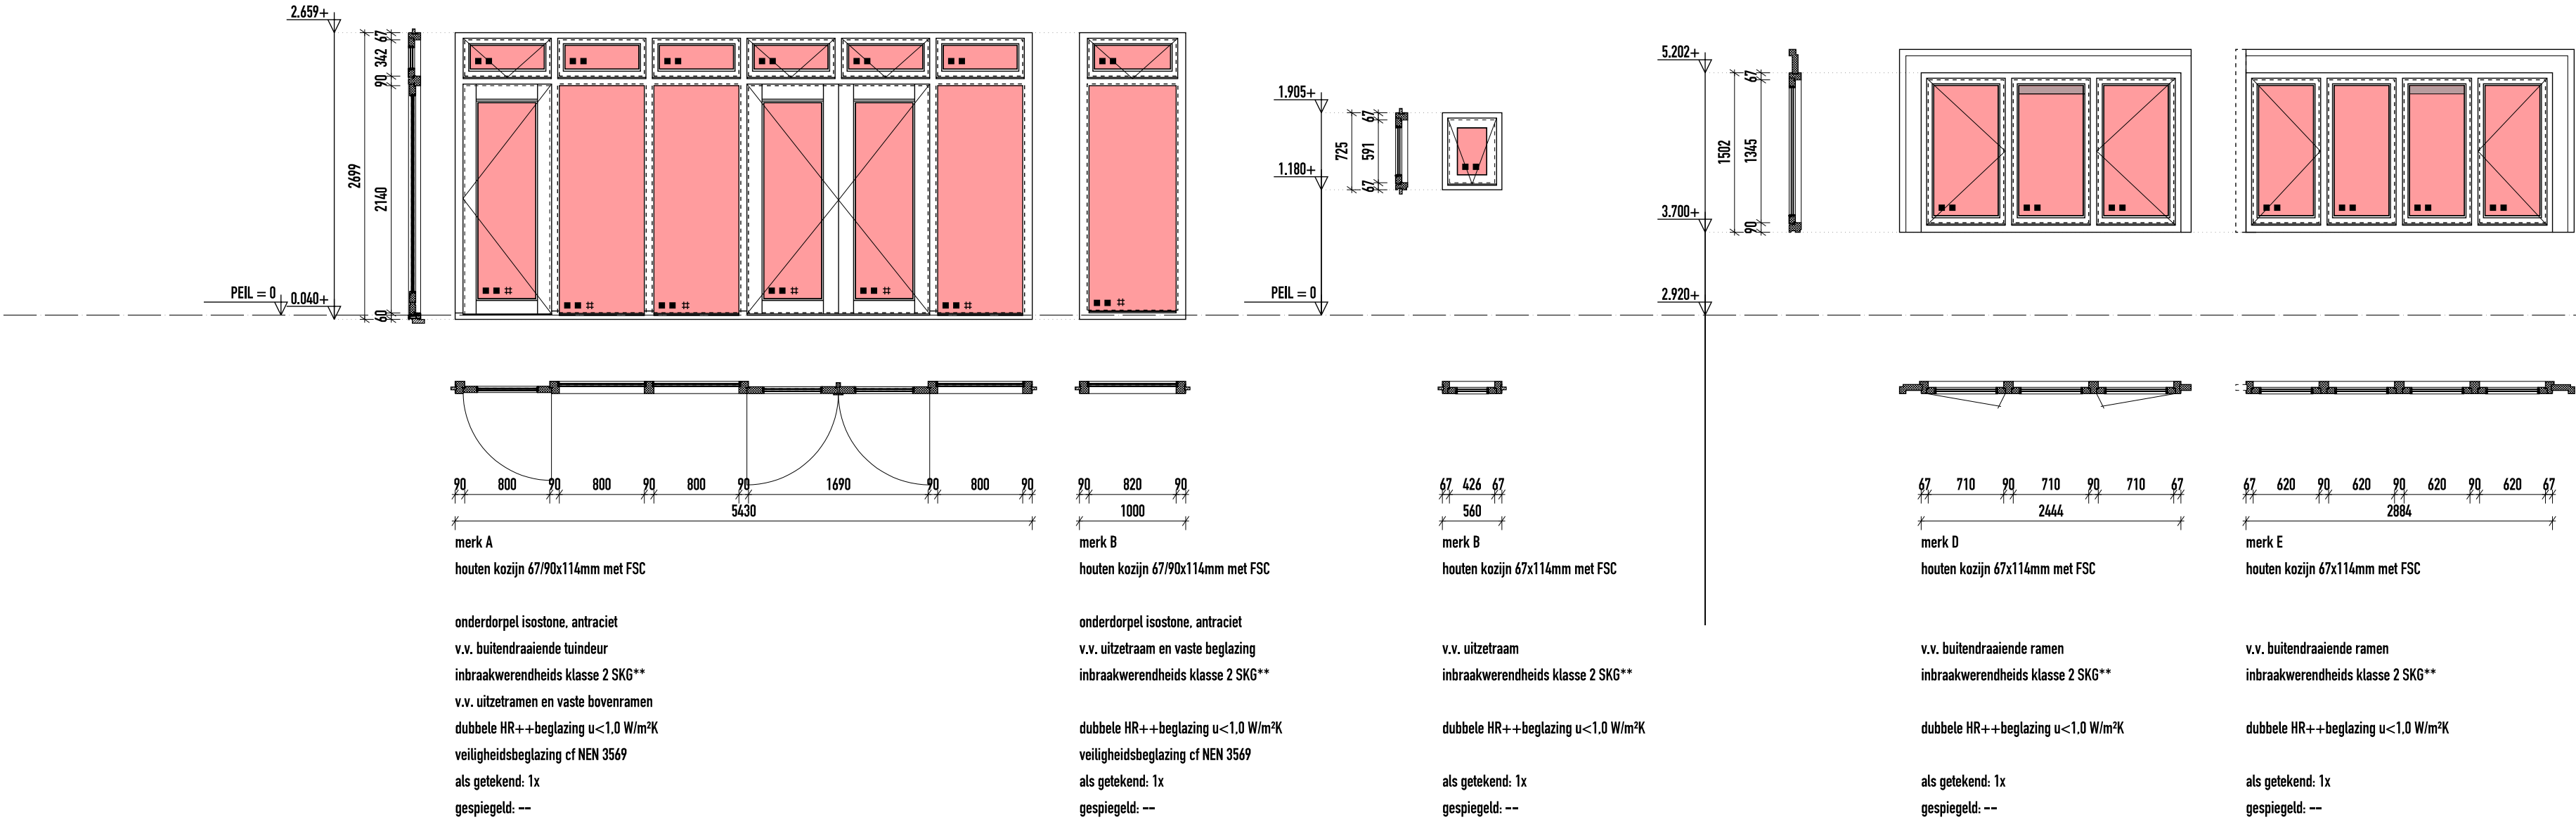

UITBREIDING WOONHUIS	werknnummer	225	datum	20-02-2026
BURGEMEESTER GERADTSLAAN 45 6641 ZS BEUNINGEN	tekeningnummer	BA-30	wijz. A	--
IN OPDRACHT VAN MARLOUS VAN DER HOOGTE EN GERARD VAN ROEKEL	formaat - schaal	A2 1:50	wijz. B	--
ONTWERPTEKENING KOZIJNBLAD	afdruk op A3 1:100		wijz. C	--
	getekend	JK	wijz. D	--