




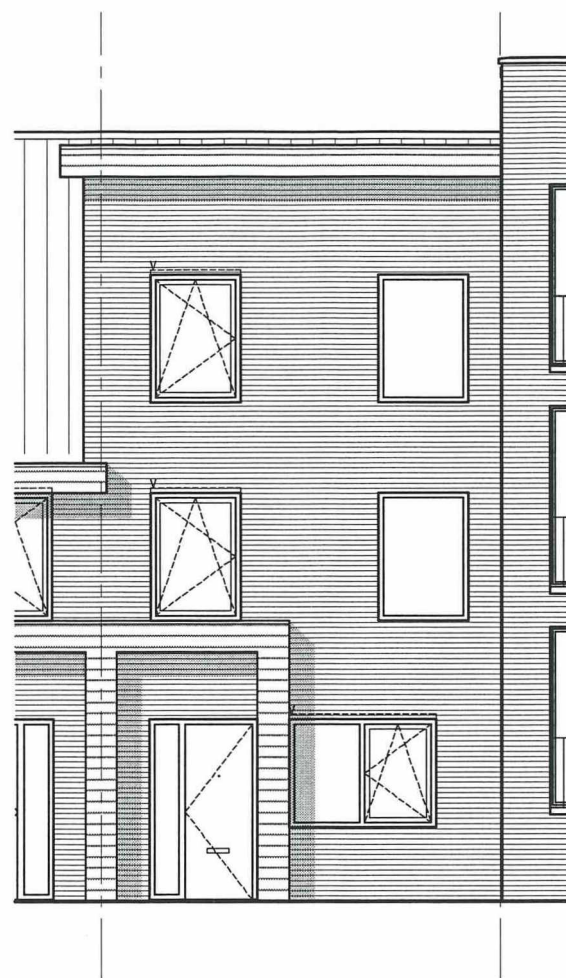


voorgevel

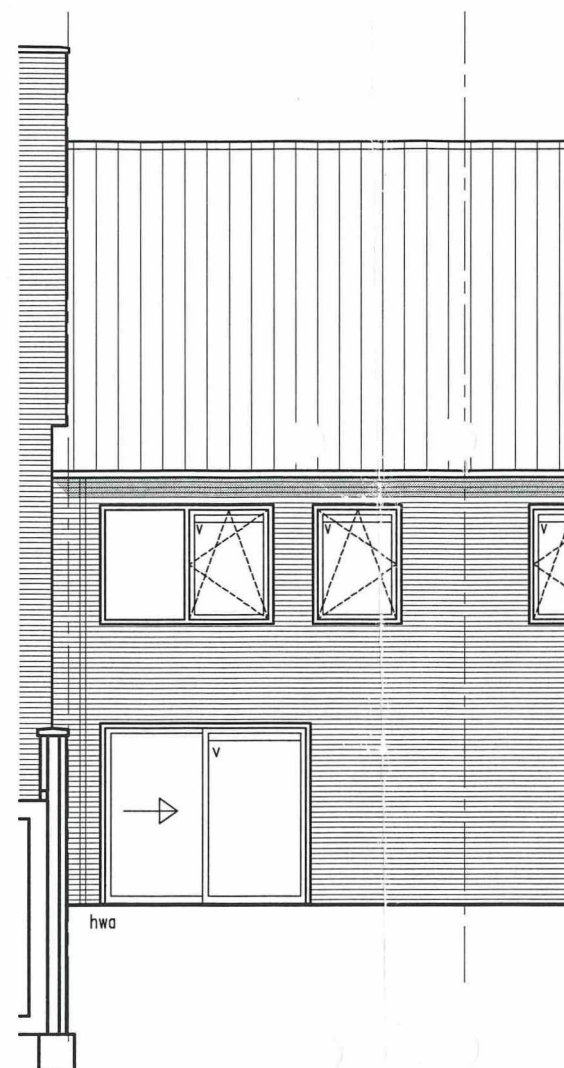

achtergevel

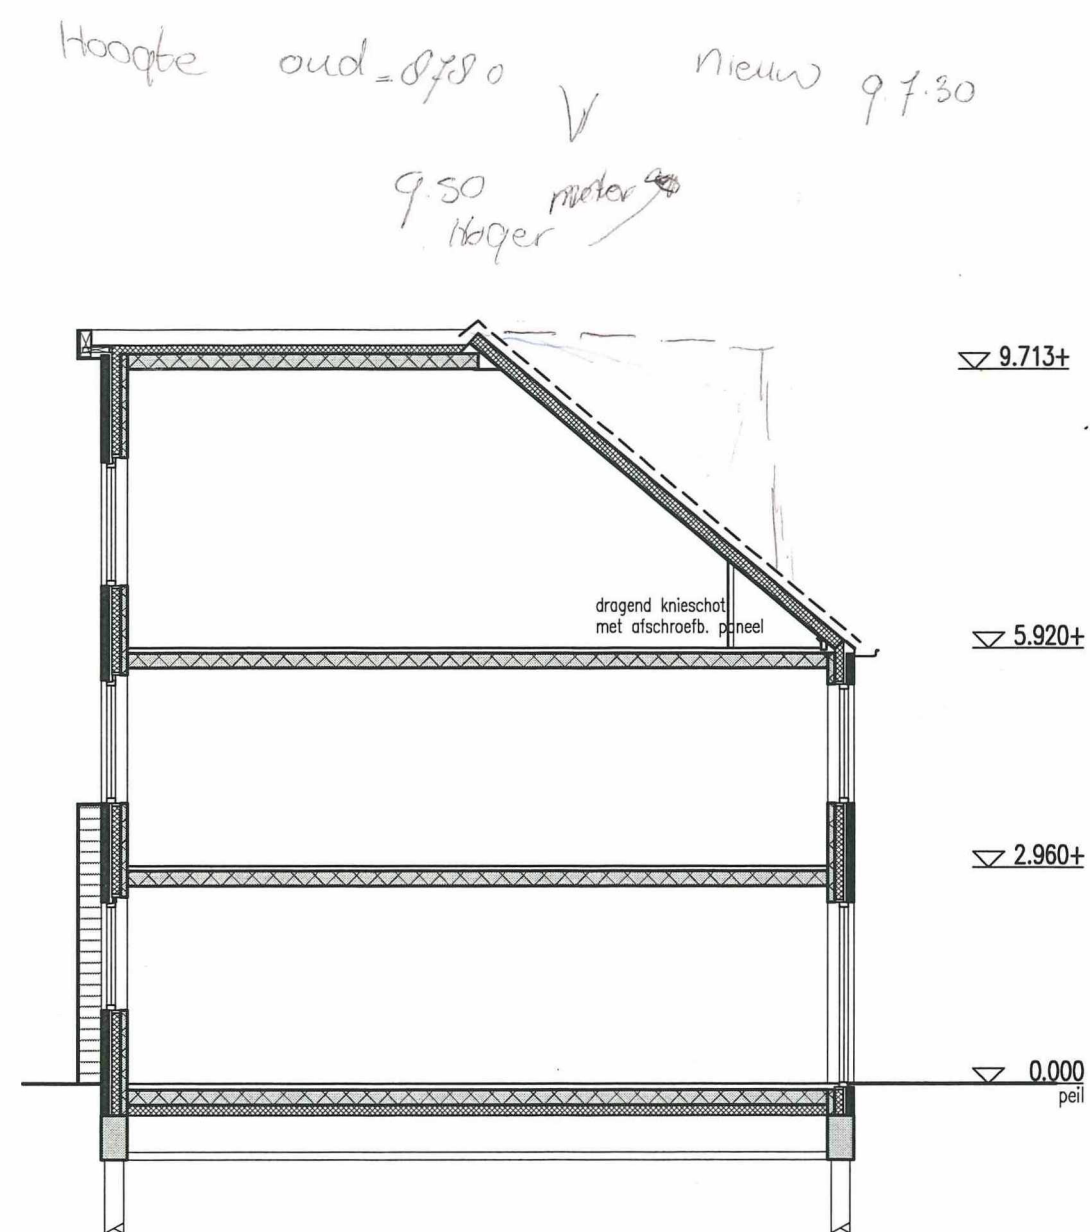

doorsnede

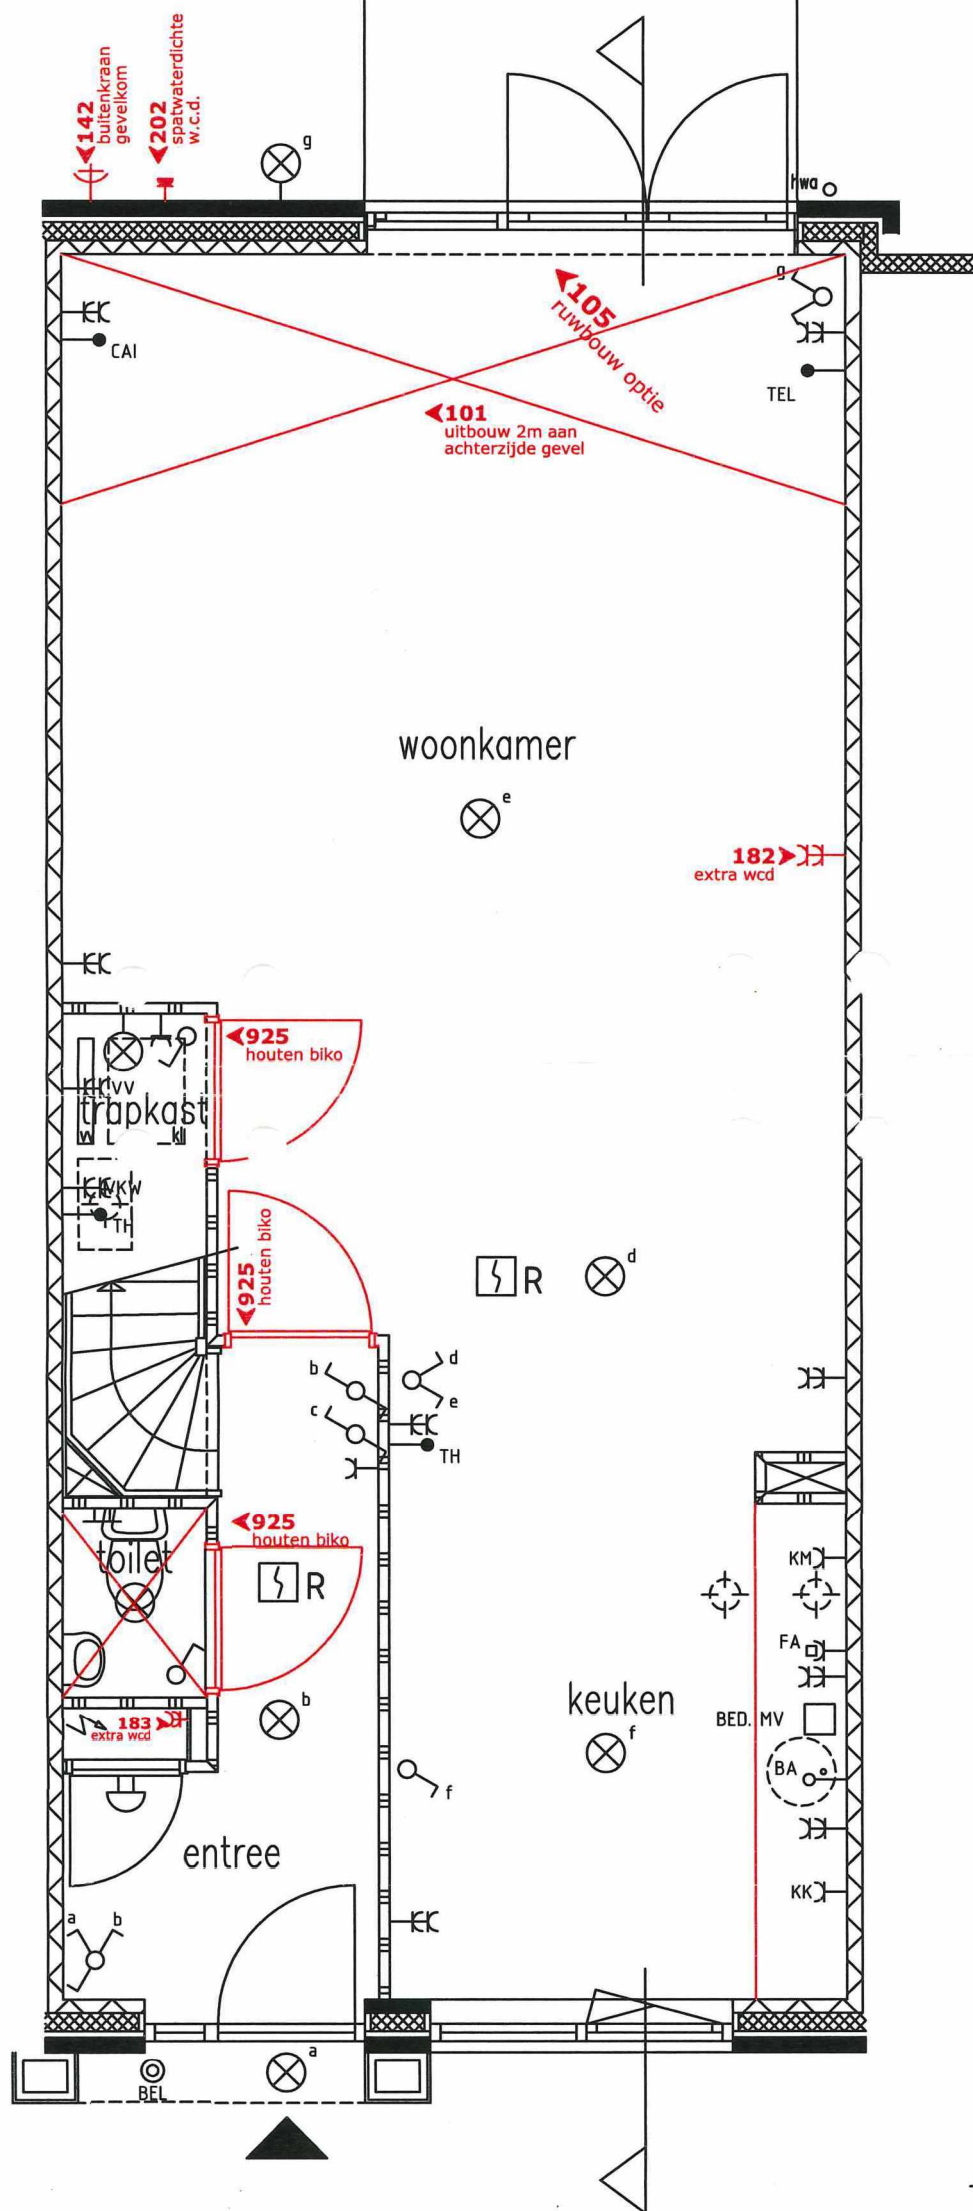


ALGEMEEN
BEGANE GROND
TOILET BADKAMER
603
 Sanitair volgens offerte en spec.
 showroom / installateur nr. 59553
 d.d. 09-09-08 tek. 17-09-08
705
 Tegels volgens offerte showroom
 offerte nr. 5700
KEUKEN
802
 Leidingwerk vlg. opgave en spec.
 KeukenHome offerte nr.
 d.d. 11-09-08
ZOLDER

Datum ondertekening: _____
 Handtekening: _____

Legenda	
	Basis
	Meerwerk
	Wijziging

Tekening onder voorbehoud van technische wijzigingen

AANNEMER		MeesterWerk Amersfoort									
	Naam:	M. Tamaela			Datum	19-09-2008					 Sprey Bouw Support Bouwkundige advisering en coaching
	Schaal:	1:50			Wijz. 1		Wijz. 5				
	051	Kopersbegeleiding: Sprey Bouw Support Meeneweg 14 7021 HN Zelhem 0314 - 62 08 05 (Maandag tussen 9.00 en 12.00 uur) 0314 - 62 08 95			Wijz. 2		Wijz. 6		BG		
					Wijz. 3		Wijz. 7				
					Wijz. 4		Wijz. 8				

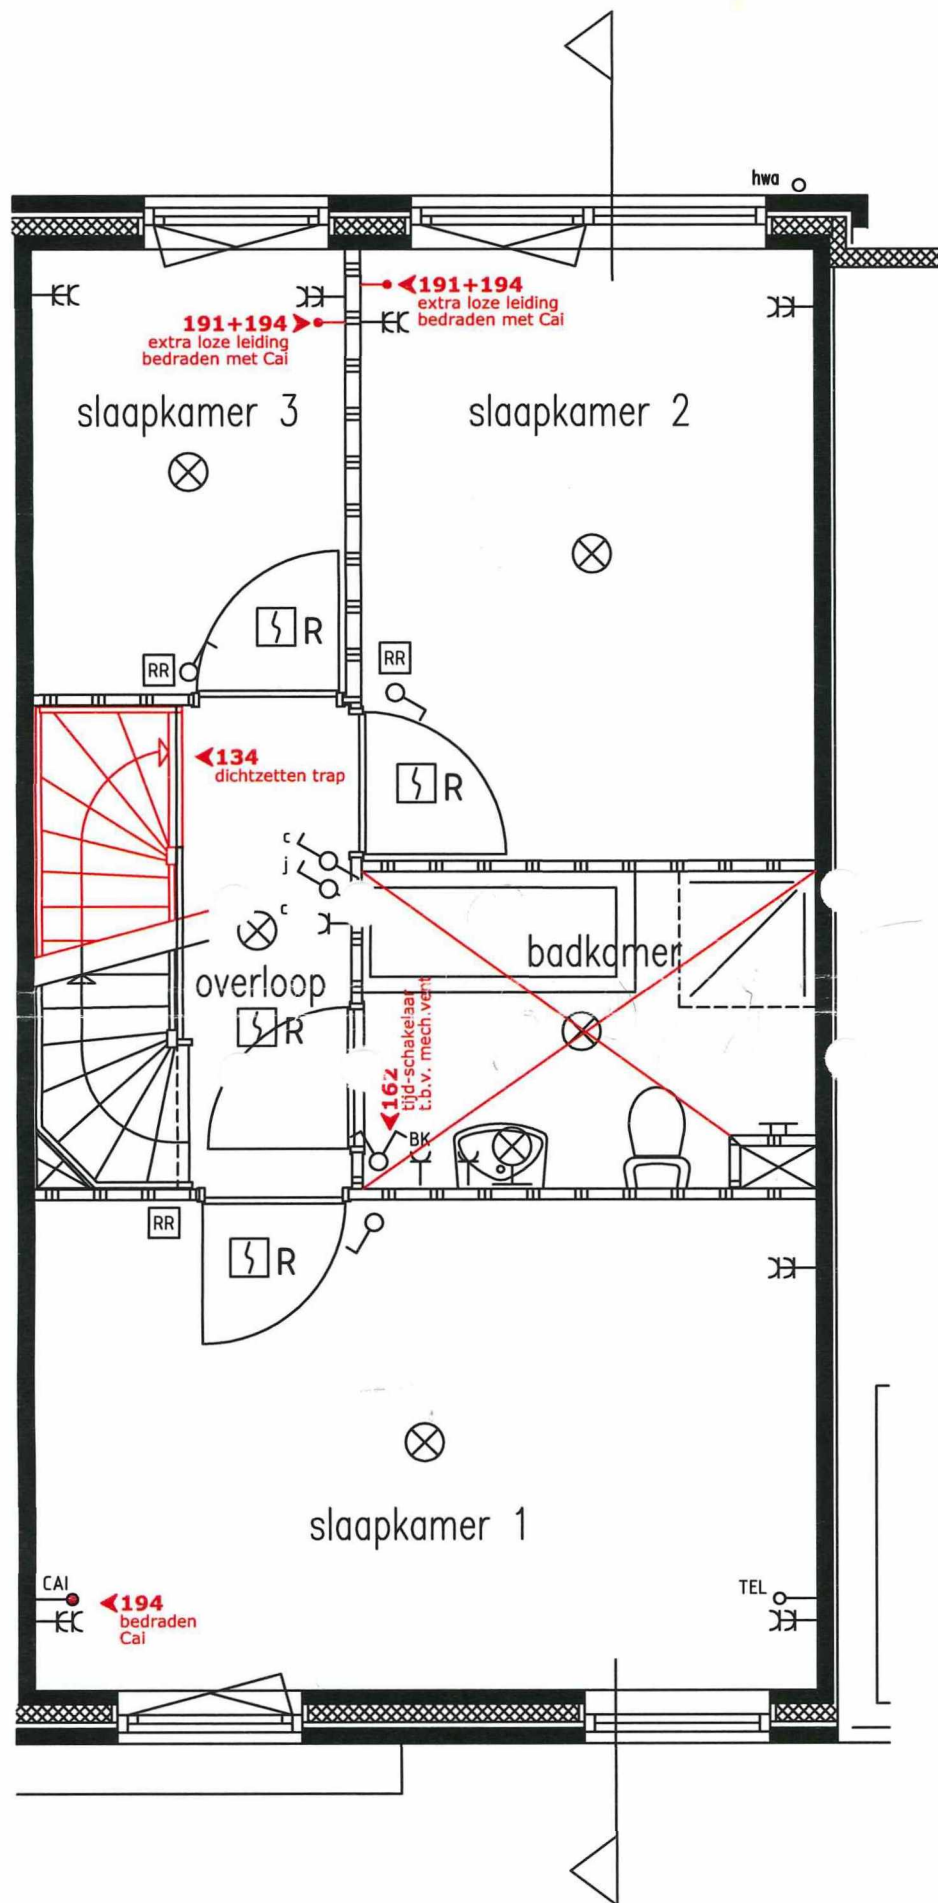

ALGEMEEN
 BEGANE GROND
 TOILET BADKAMER

603
 Sanitair volgens offerte en spec.
 showroom / installateur nr. 59553
 d.d. 09-09-08 tek. 17-09-08

705
 Tegels volgens offerte showroom
 offerte nr. 5700

KEUKEN
802
 Leidingwerk vlg. opgave en spec.
 KeukenHome offerte nr.
 d.d. 11-09-08


ZOLDER

Datum ondertekening: _____
 Handtekening: _____

Legenda	
	Basis
	Meerwerk
	Wijziging

Tekening onder voorbehoud van technische wijzigingen

AANNEMER		MeesterWerk Amersfoort									
	Naam:	M. Tamaela			Datum	19-09-2008					
	Schaal:	1:50			Wijz. 1		Wijz. 5				
	051	Kopersbegeleiding: Sprey Bouw Support Meeneweg 14 7021 HN Zelhem 0314 - 62 08 05 (Maandag tussen 9.00 en 12.00 uur) 0314 - 62 08 95			Wijz. 2		Wijz. 6		1e		
					Wijz. 3		Wijz. 7				
					Wijz. 4		Wijz. 8				
			 Sprey Bouw Support Bouwkundige advisering en coaching								

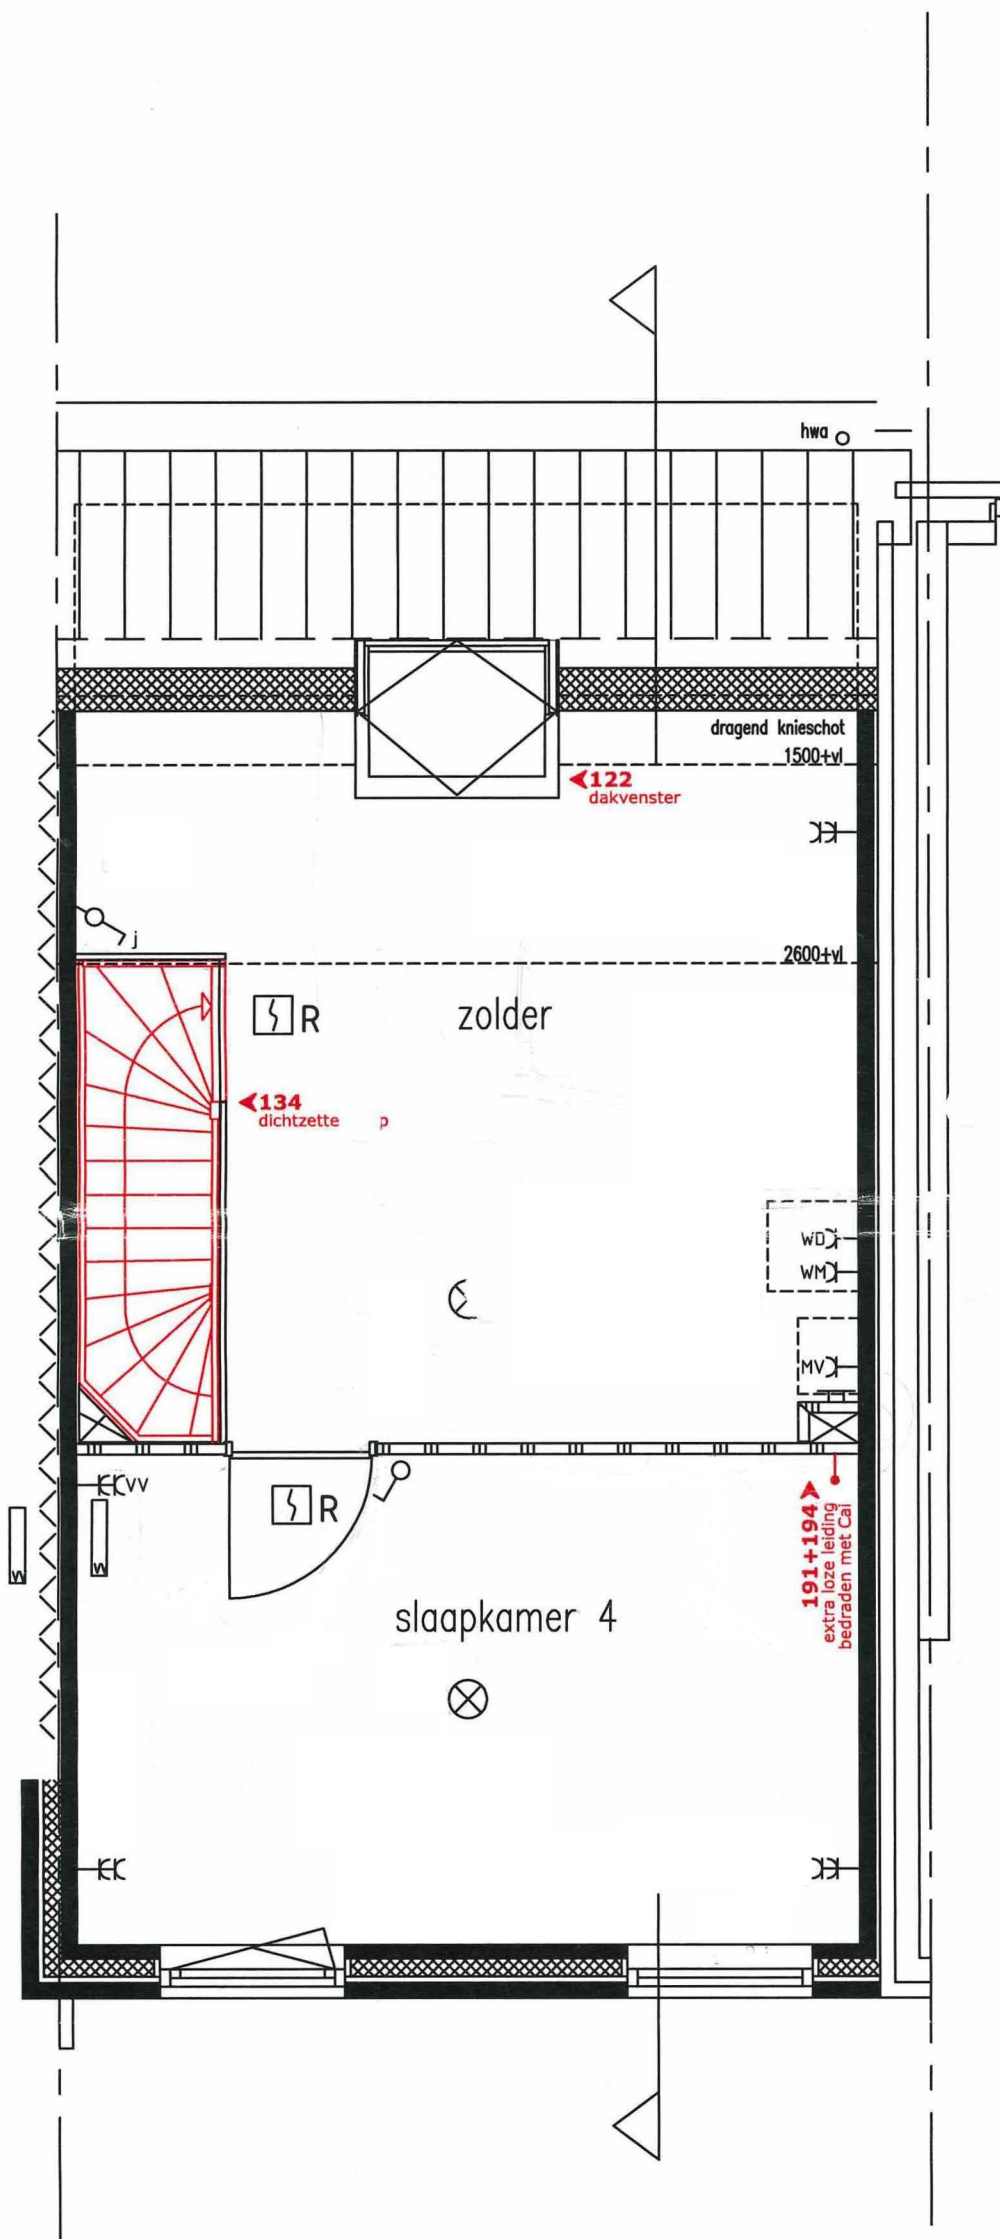

ALGEMEEN
BEGANE GROND
TOILET BADKAMER

603
Sanitair volgens offerte en spec.
showroom / installateur nr. 59553
d.d. 09-09-08 tek. 17-09-08

705
Tegels volgens offerte showroom
offerte nr. 5700

KEUKEN
802
Leidingwerk vlg. opgave en spec.
KeukenHome offerte nr.
d.d. 11-09-08

ZOLDER

Datum ondertekening:




Handtekening:

Legenda


■	Basis
■	Meerwerk
■	Wijziging

Tekening onder voorbehoud van technische wijzigingen


AANNEMER		MeesterWerk Amersfoort									
	Naam:	M. Tamaela			Datum	19-09-2008					
	Schaal:	1:50			Wijz. 1		Wijz. 5				
	051	Kopersbegeleiding: Sprey Bouw Support Meeneweg 14 7021 HN Zelhem 0314 - 62 08 05 (Maandag tussen 9.00 en 12.00 uur) 0314 - 62 08 05			Wijz. 2		Wijz. 6		Zol		
					Wijz. 3		Wijz. 7				
					Wijz. 4		Wijz. 8				
 Sprey Bouw Support Bouwkundige advisering en coaching											

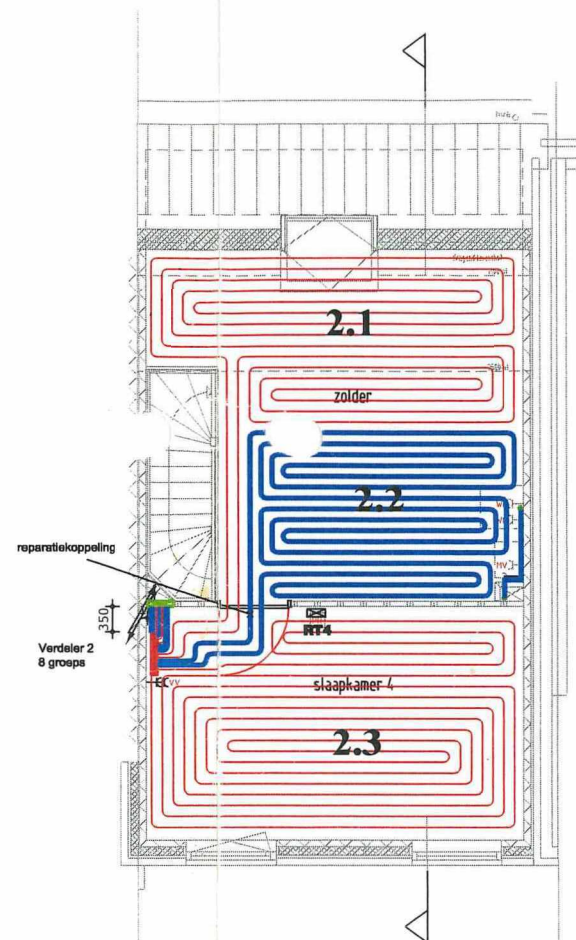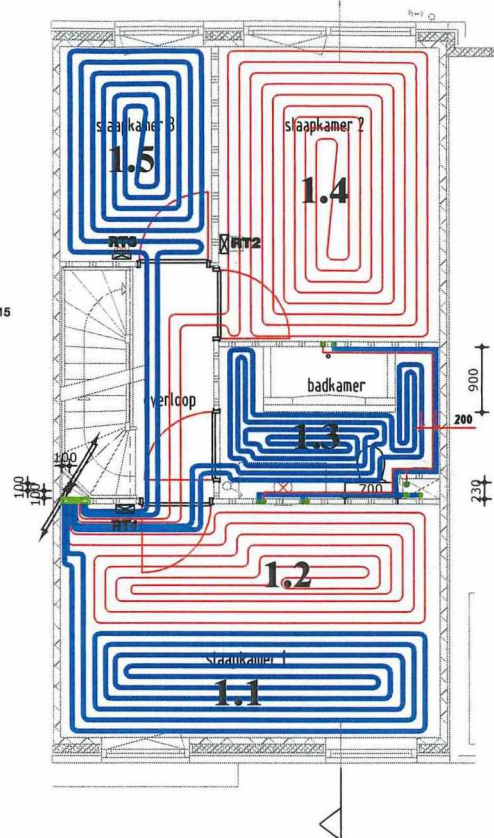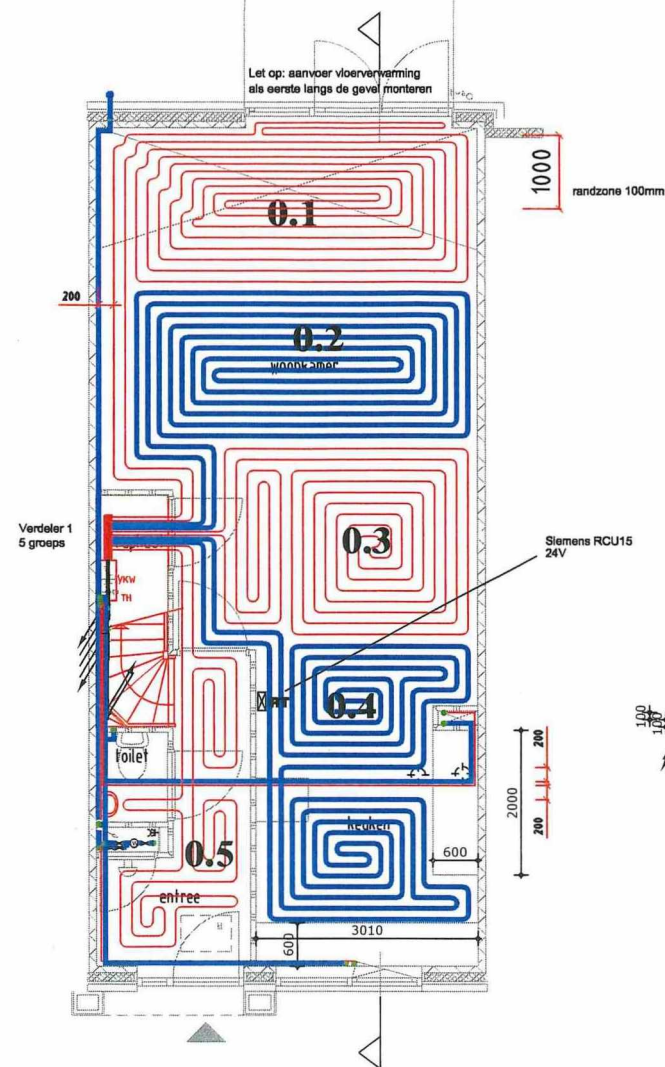

Verdeler 2

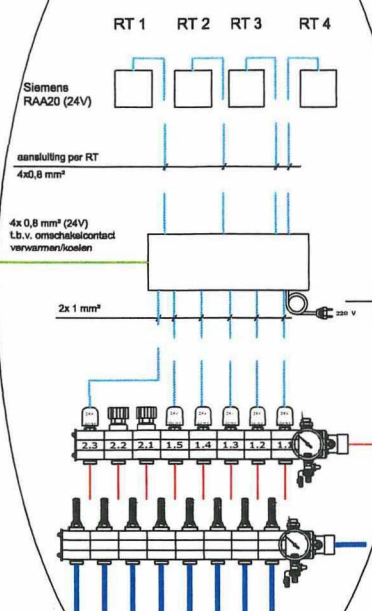

Verdeler 2

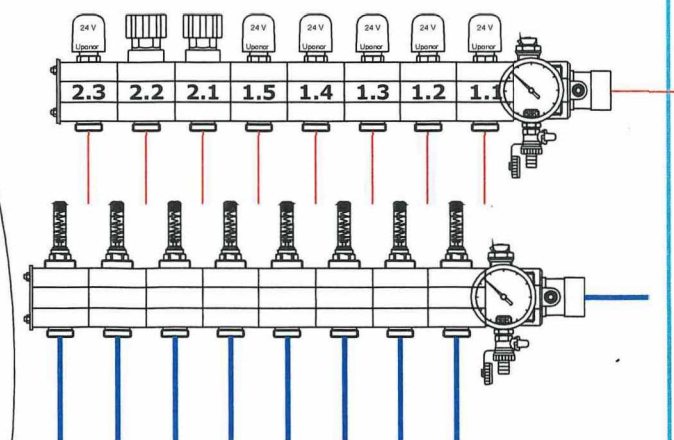

REVISIE

Uponor vloerverwarming/vloerkoeling met Uponor PE-MDX leiding 17x2mm

Groep	Ruimte	Lengte per groep (m)	Buis afstand (mm)	Volumestroom per groep (l/min)
Verdeler 1:				
0.1	woonk./keuken	95	100-150	1,3
0.2	woonk./keuken	75	150	1,0
0.3	woonk./keuken	65	150	0,9
0.4	woonk./keuken	70	150	0,9
0.5	entree/toilet	35	150	0,3

Verdeler 2:				
1.1	slaapkamer 1	60	150	0,8
1.2	slaapkamer 1	60	150	0,8
1.3	badkamer	45	100	0,3
1.4	slaapkamer 2	95	150	1,1
1.5	slaapkamer 3	50	150	0,8
Verdeler 2:				
2.1	zolder	85	150	1,0
2.2	zolder	65	150	0,8
2.3	slaapkamer 4	95	150	1,8

Let op: aanvoer vloerverwarming als eerste langs de gevel monteren

Afstand vloerverwarming/waterleiding 200 mm aanhouden

Vloerverwarming op een door derden geleverde en gemonteerde bouwstaalnet

vloerverwarming/koeling bnr: 51/blok 5

Firma: **Stewitech Duurzaam B.V.**
Project: **137 woningen Puntenburg Amersfoort**

stewitech
Duurzaam B.V.

Postbus 1069 - 3350 CB Papendrecht
Prisma 83-85 - 3364 DJ Sliedrecht
Tel : 0184 - 430 030 / Fax : 0184 - 423 391
E-mail : info@stewitech.nl
Internet : www.stewitech.nl

Maatvoering vloerverwarmingsverdeler

Aantal circuits	2	3	4	5	6	7	8	9	10	11	12	13	14	15
Hoogte (mm)	355	355	355	355	355	355	355	355	355	355	355	355	355	355
Breedte (mm)	225	280	335	390	445	500	555	610	665	720	775	830	885	940
Diepte (mm)	120	120	120	120	120	120	120	120	120	120	120	120	120	120



tel. (026) 4459845 - fax. (026) 4459373

impact 73 - 6921 RZ Duiven

postbus 1008 - 6920 BA Duiven

internet: www.nathan.nl - e-mail: tekening@nathan.nl

tekenaar: M. Diephuis
e-mail: m.diephuis@nathan.nl
formaat: A3
school: 1:100

datum: 06-10-2009

laatste wijz.: 11-05-2010

versie: B

file: 8915-51-5R.dwg

tek.no:

51

werk no.:

8915