



Renvooi

- wandcontactdoos enkel
- wandcontactdoos dubbel
- w wandcontactdoos waterdicht
- vp wandcontactdoos in vloerpot
- aansluitpunt verlichting plafond
- spot in plafond
- bs spot in plafond geschakeld op bewegingssensor
- ss spot in plafond geschakeld op schemersensor
- ks spot in plafond geschakeld op kastschakelaar
- aansluitpunt verlichting wand
- enkele schakelaar
- enkele schakelaar met dimfunctie
- hotelschakelaar
- hotelschakelaar met dimfunctie
- utp aansluitpunt utp rechtstreeks naar meterkast
- in invoerpunt data
- wifi aansluitpunt wifi
- aansluitpunt telefoon
- bel
- beldrukker
- rookmelder

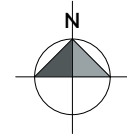

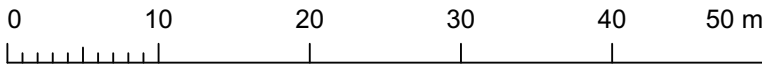



1320 **DO 1.6 situatie** versie 251121
schaal 1:500
Birkstraat 100 Soest
www.valkarchitecten.nl







The logo for VALK ARCHITECTEN features the word "VALK" in a large, bold, black, hand-drawn style font. Below it, the word "ARCHITECTEN" is written in a smaller, black, sans-serif, all-caps font. The text is centered within a yellow square background.

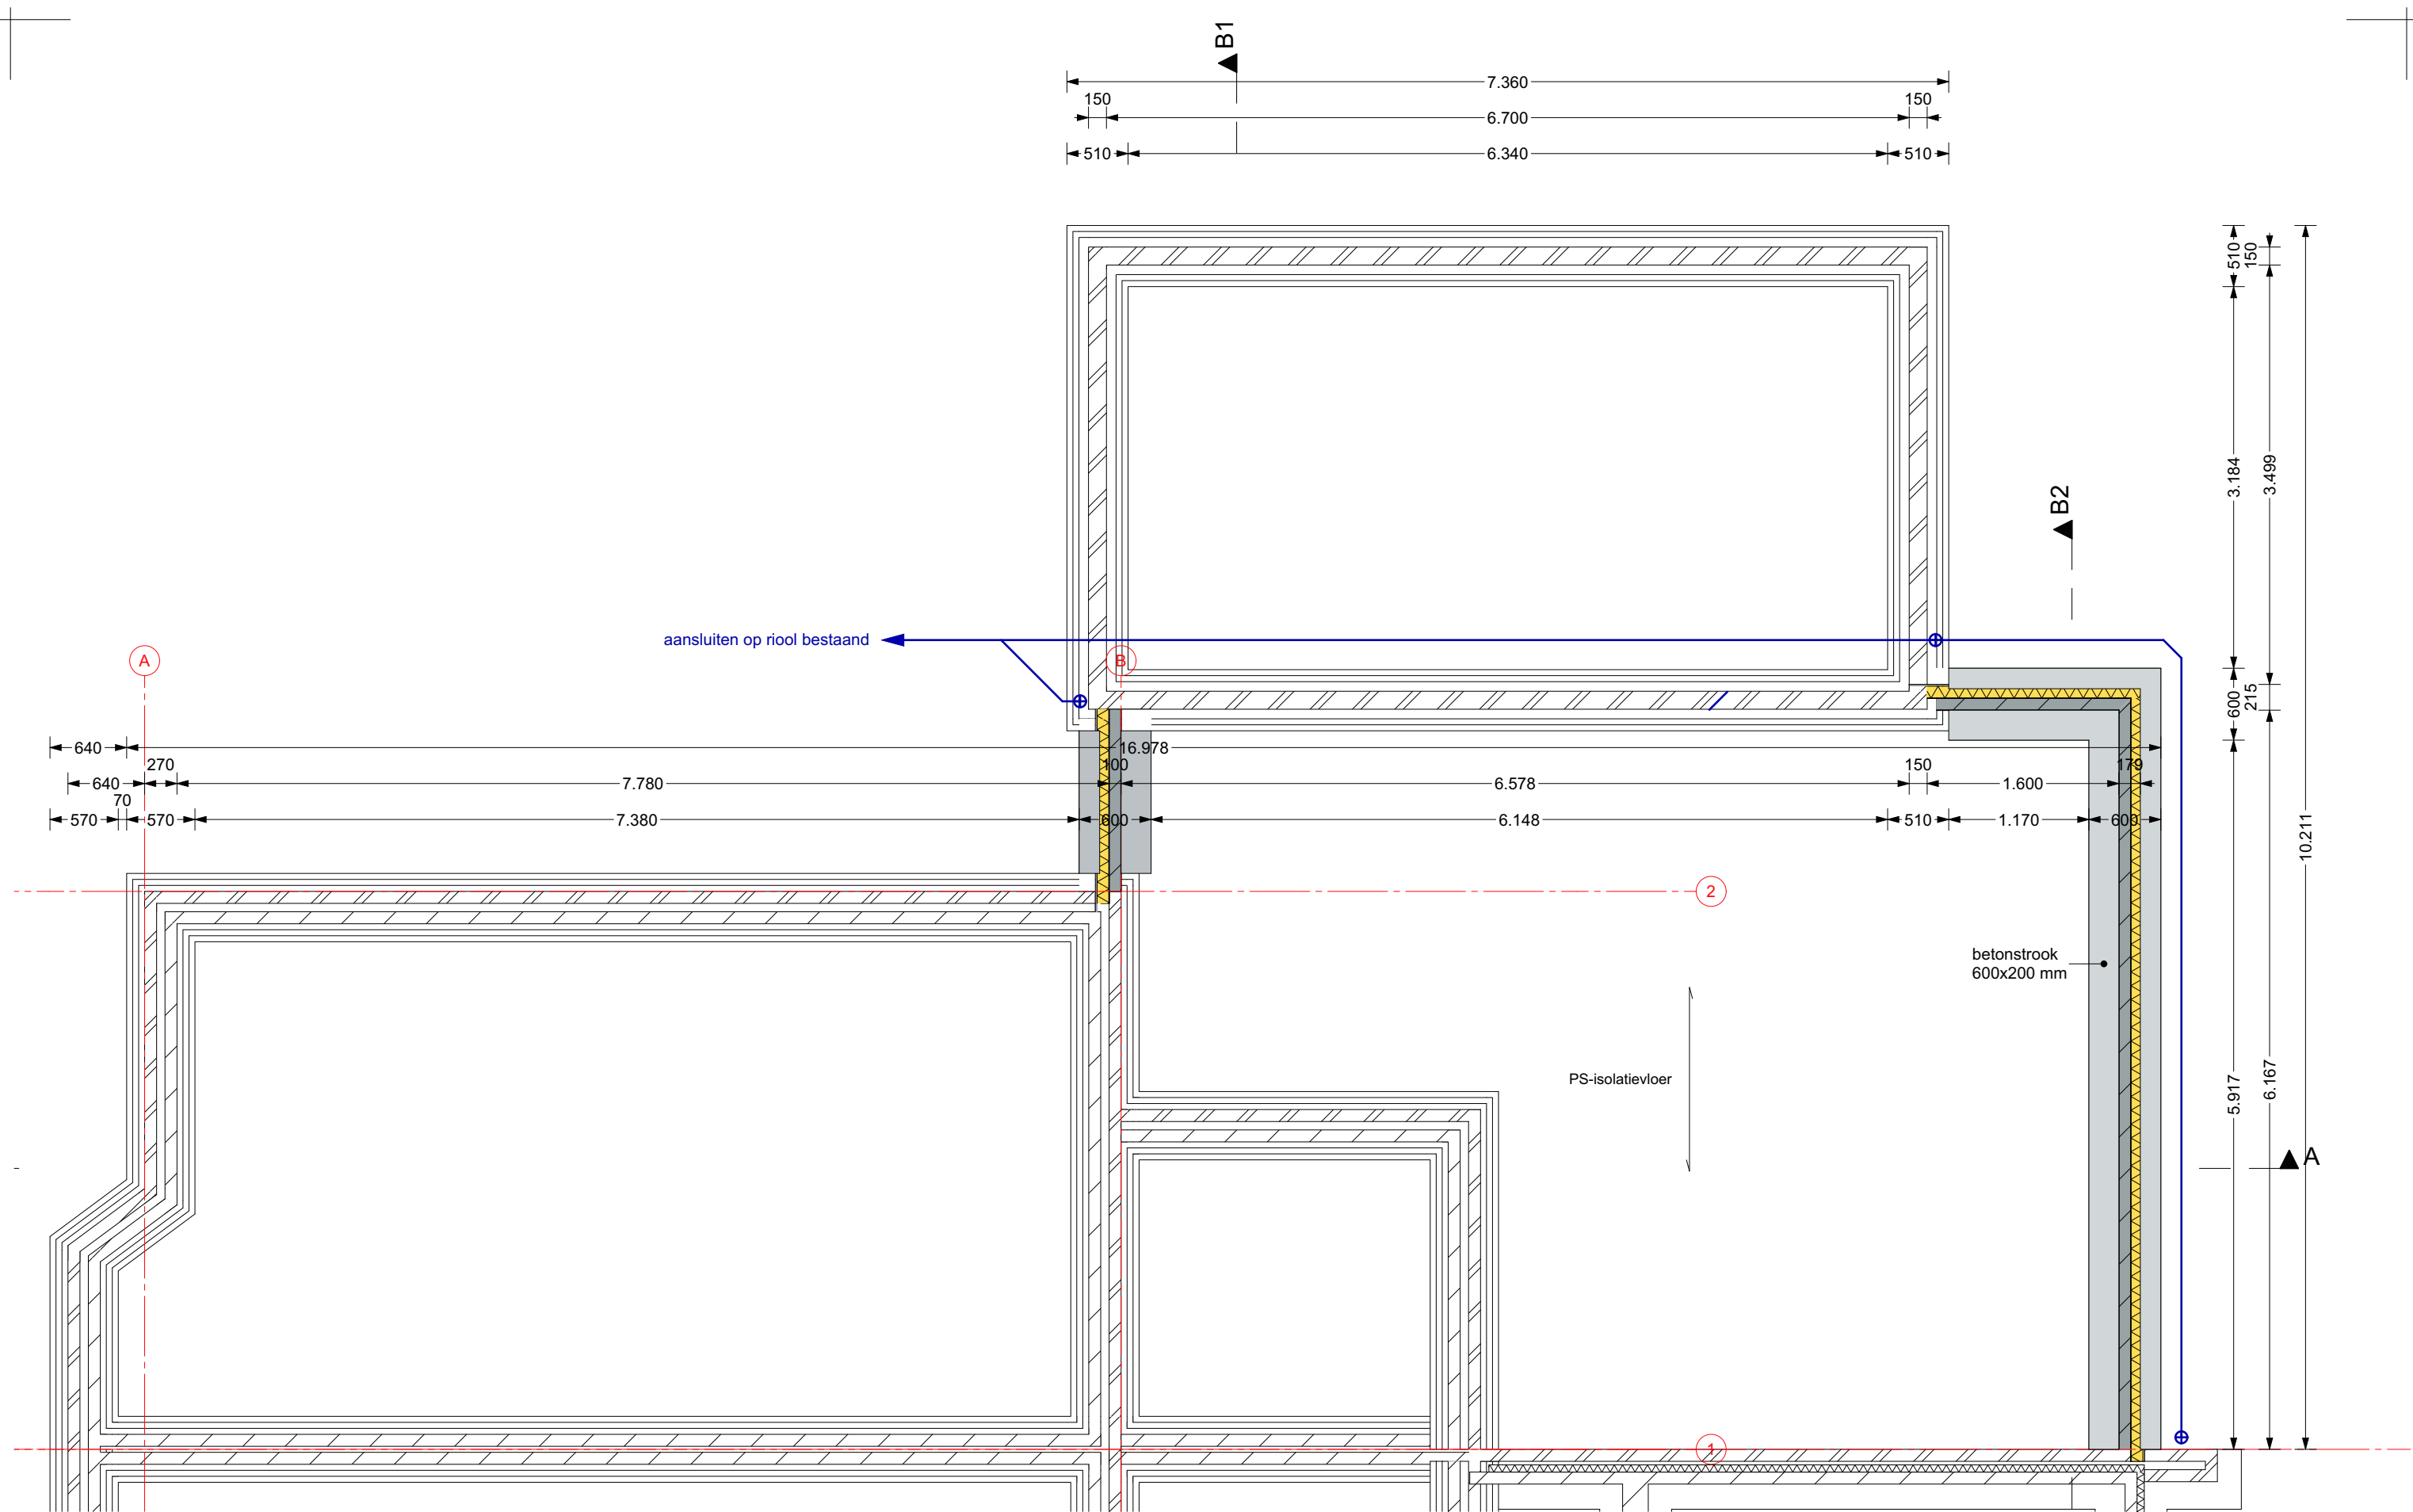

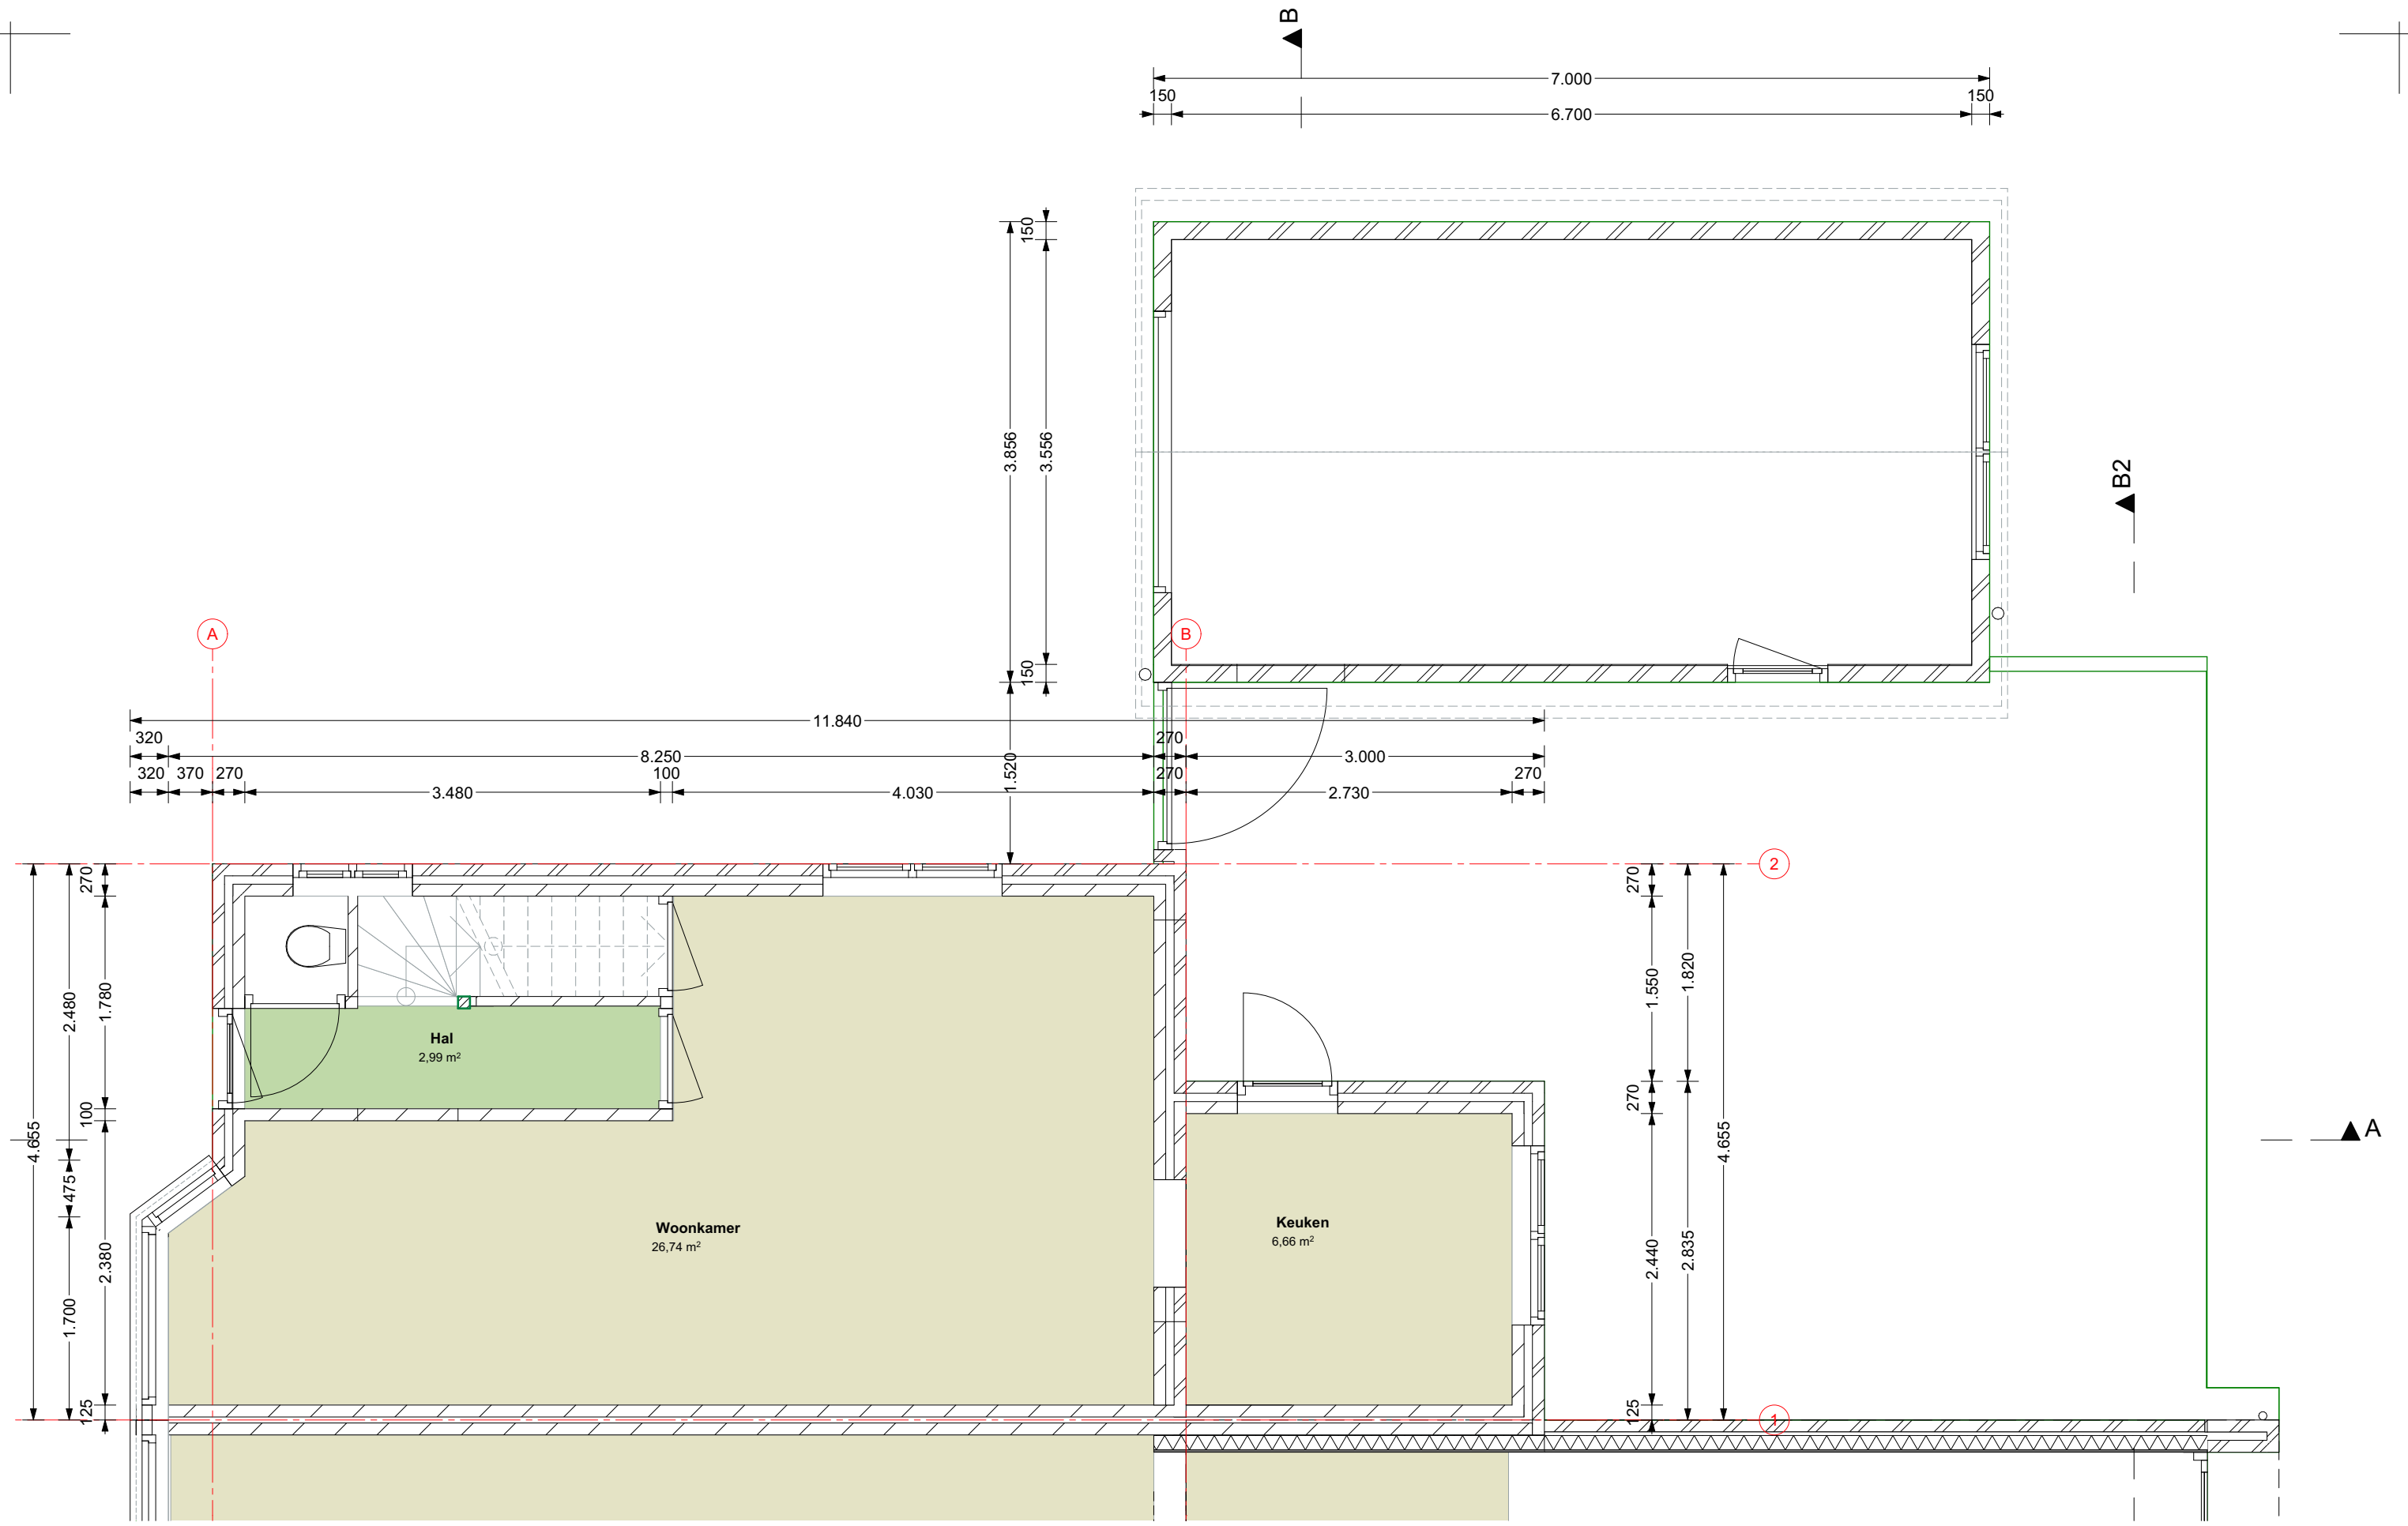

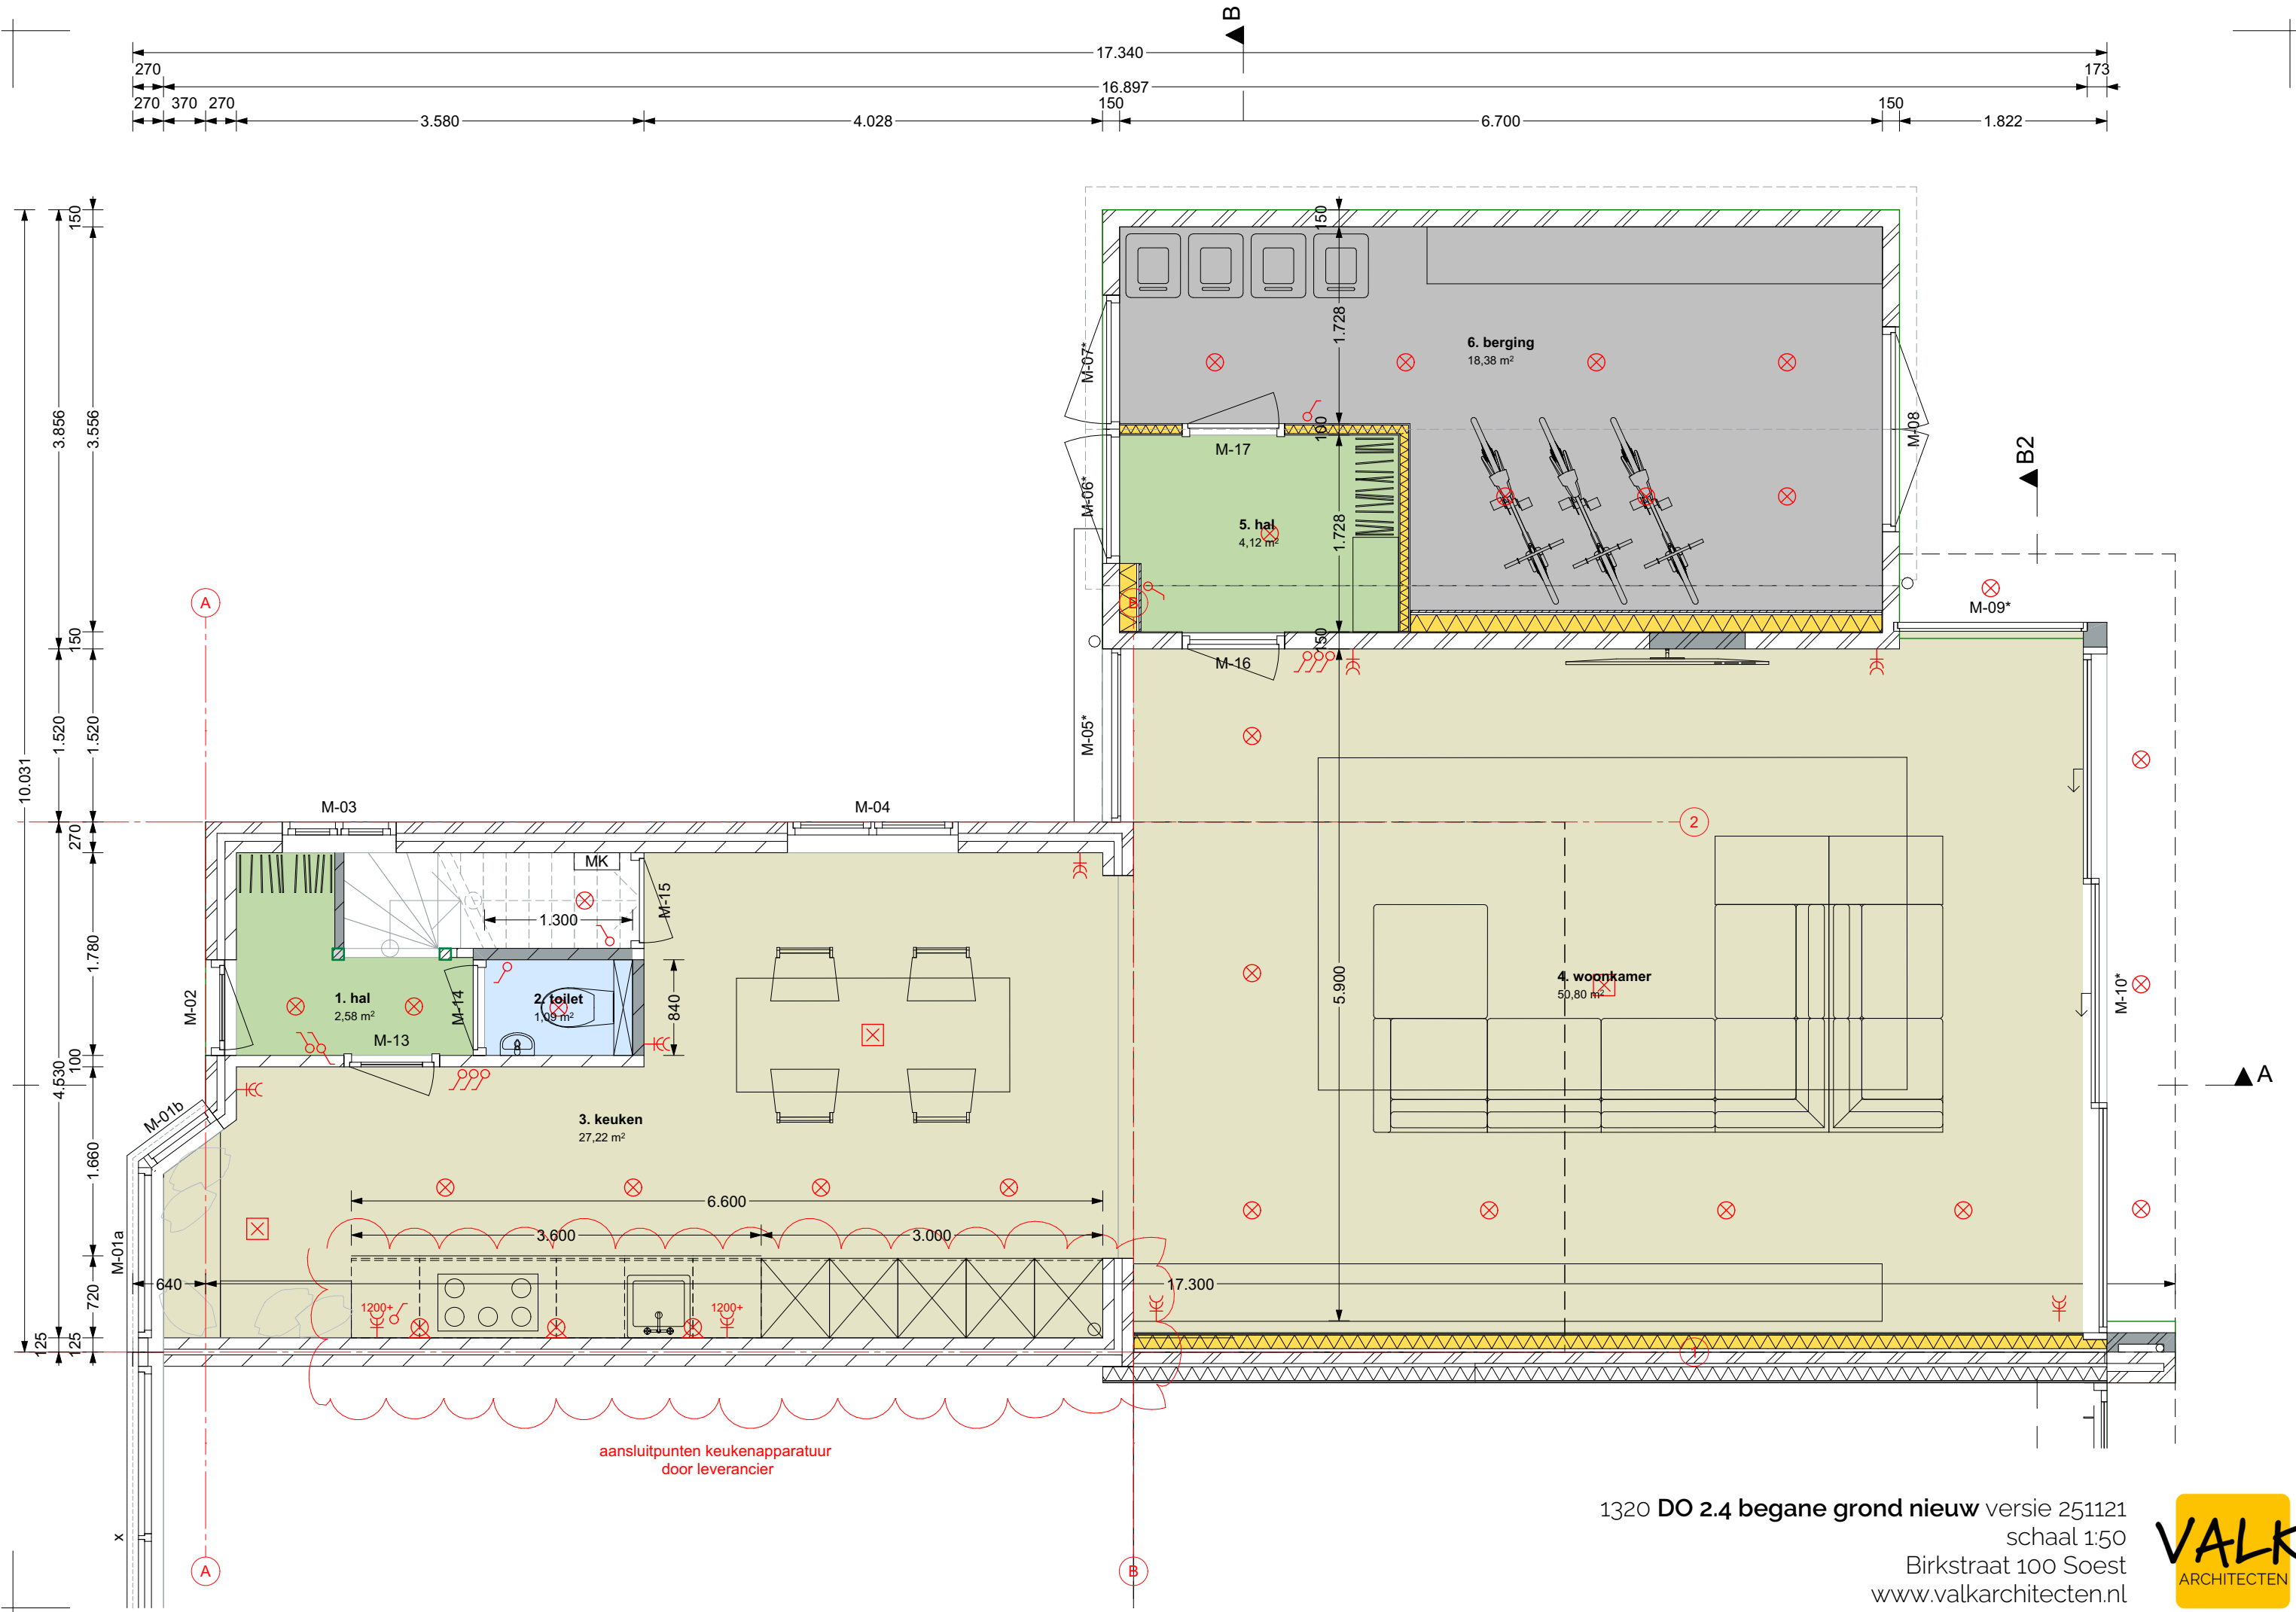


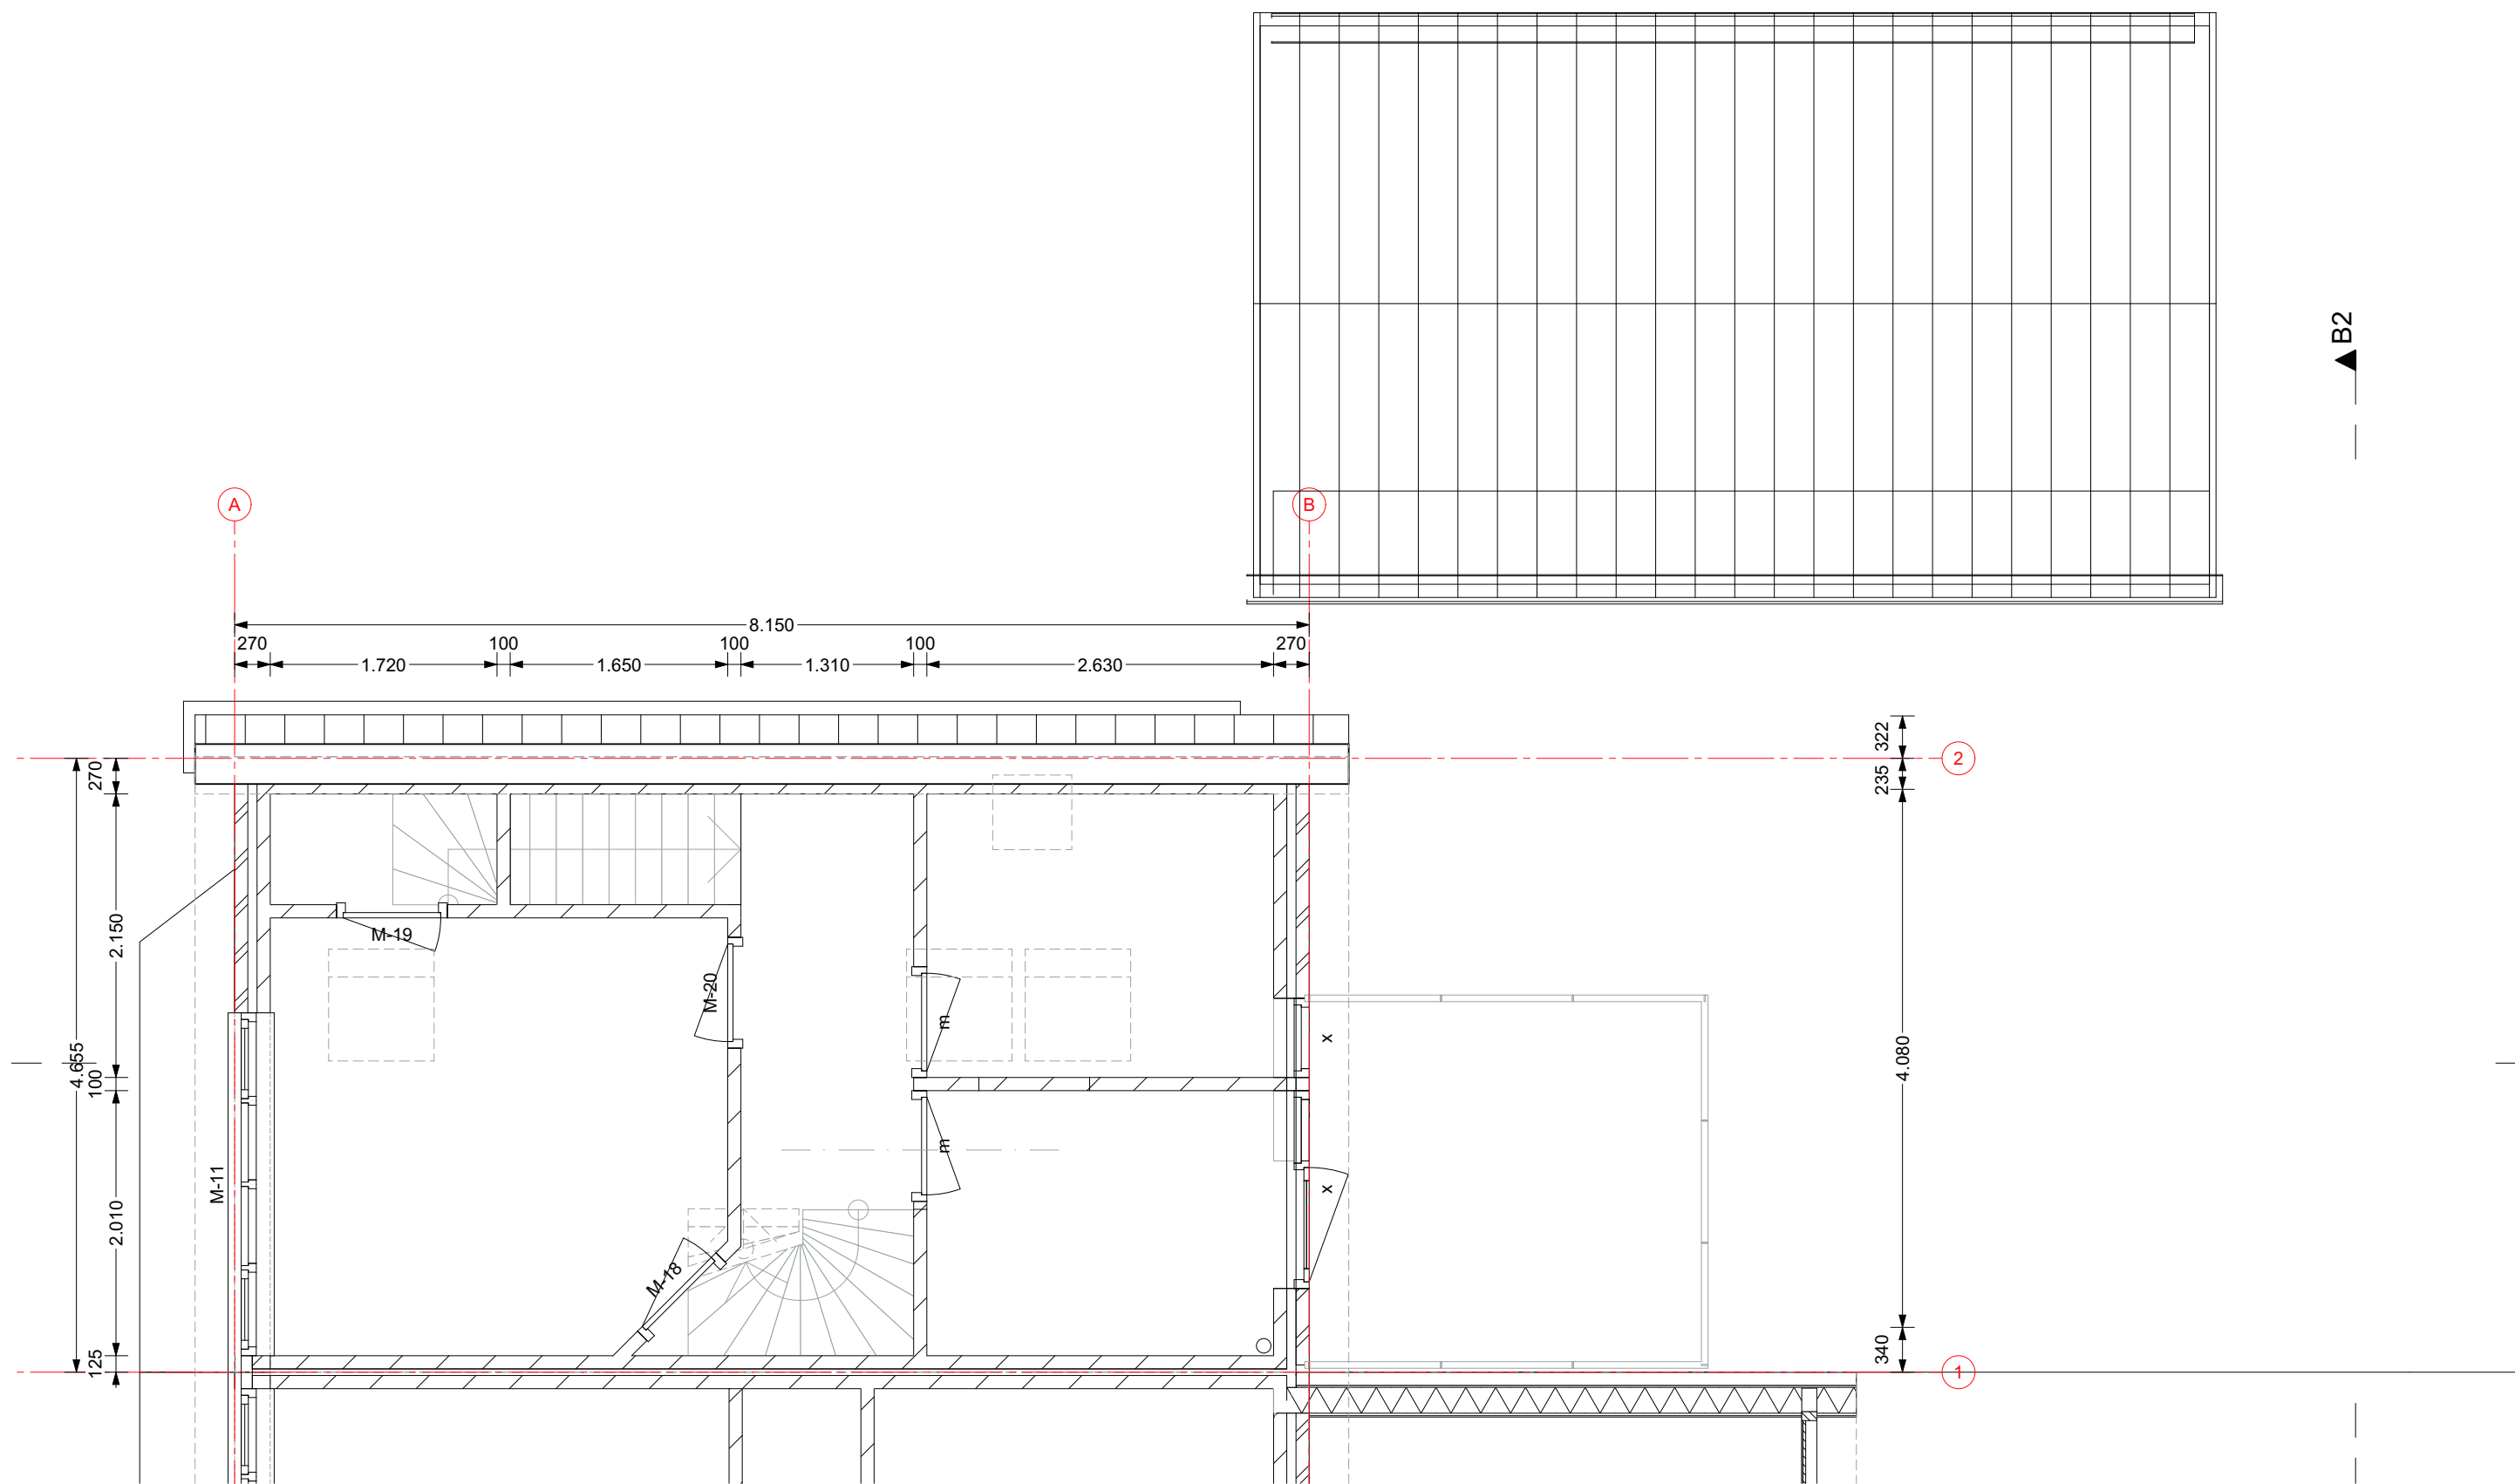

▲ B2


▲ A




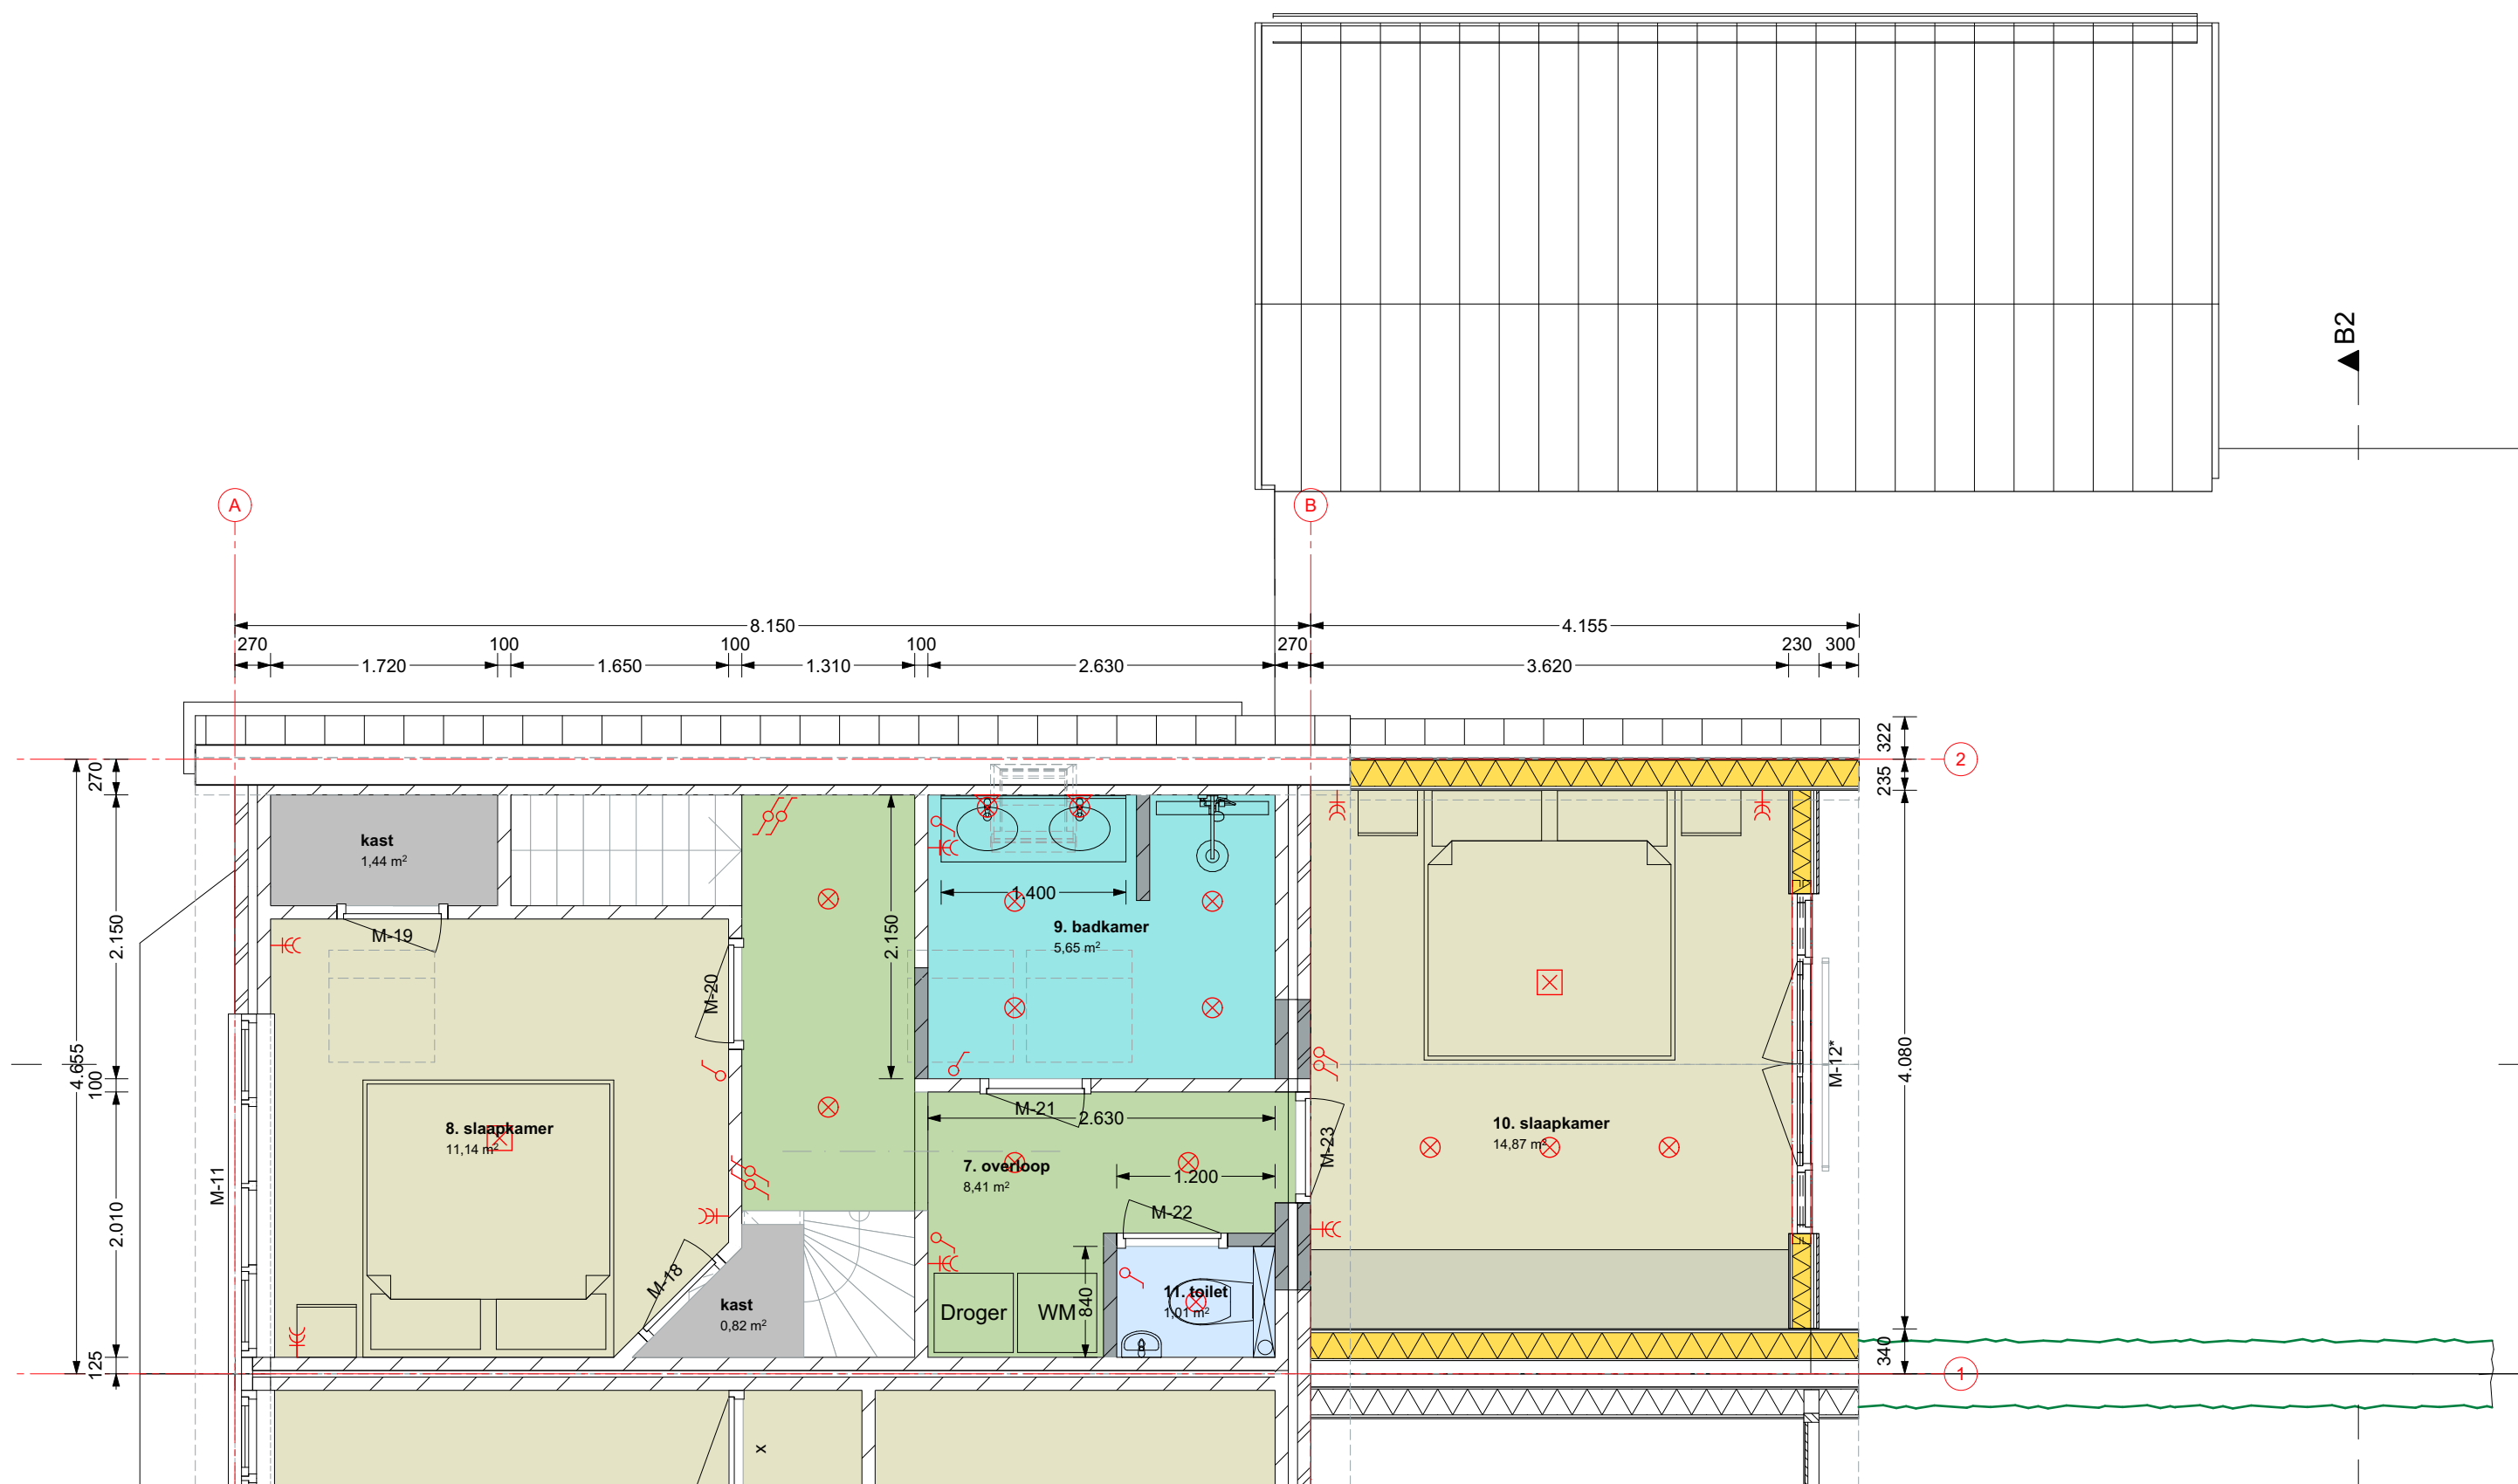


▲ B2

▲ A

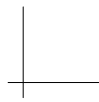


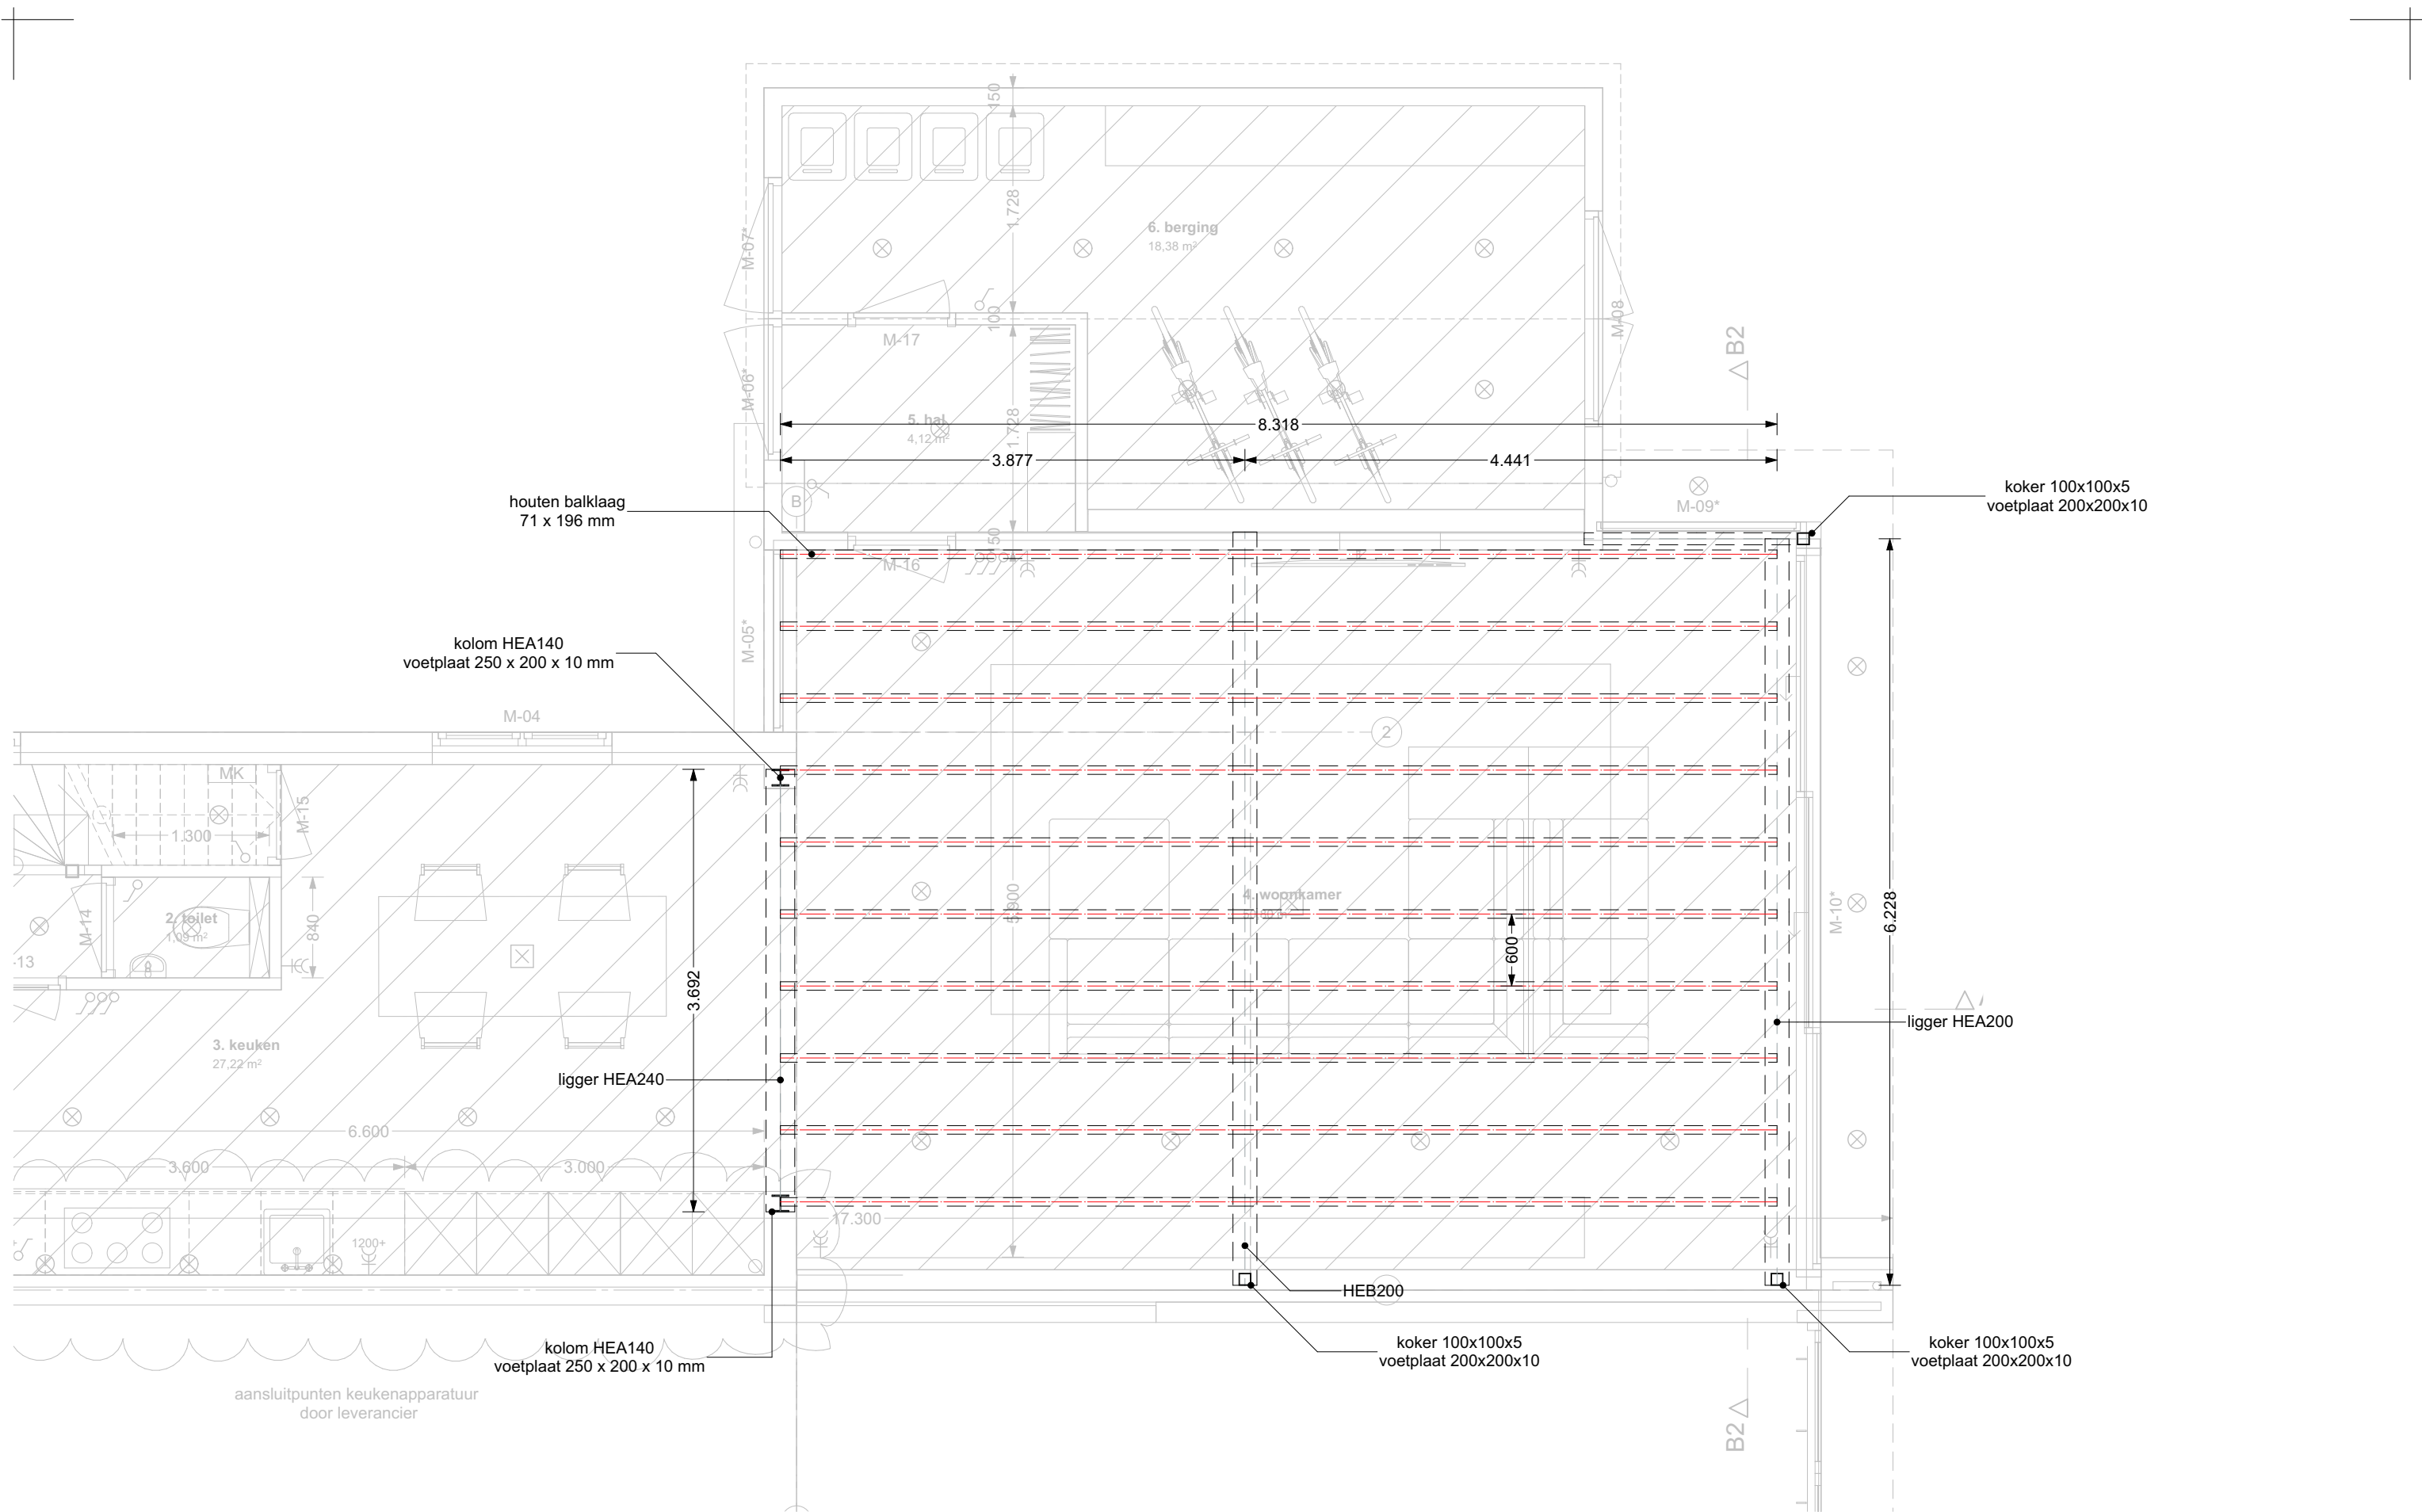

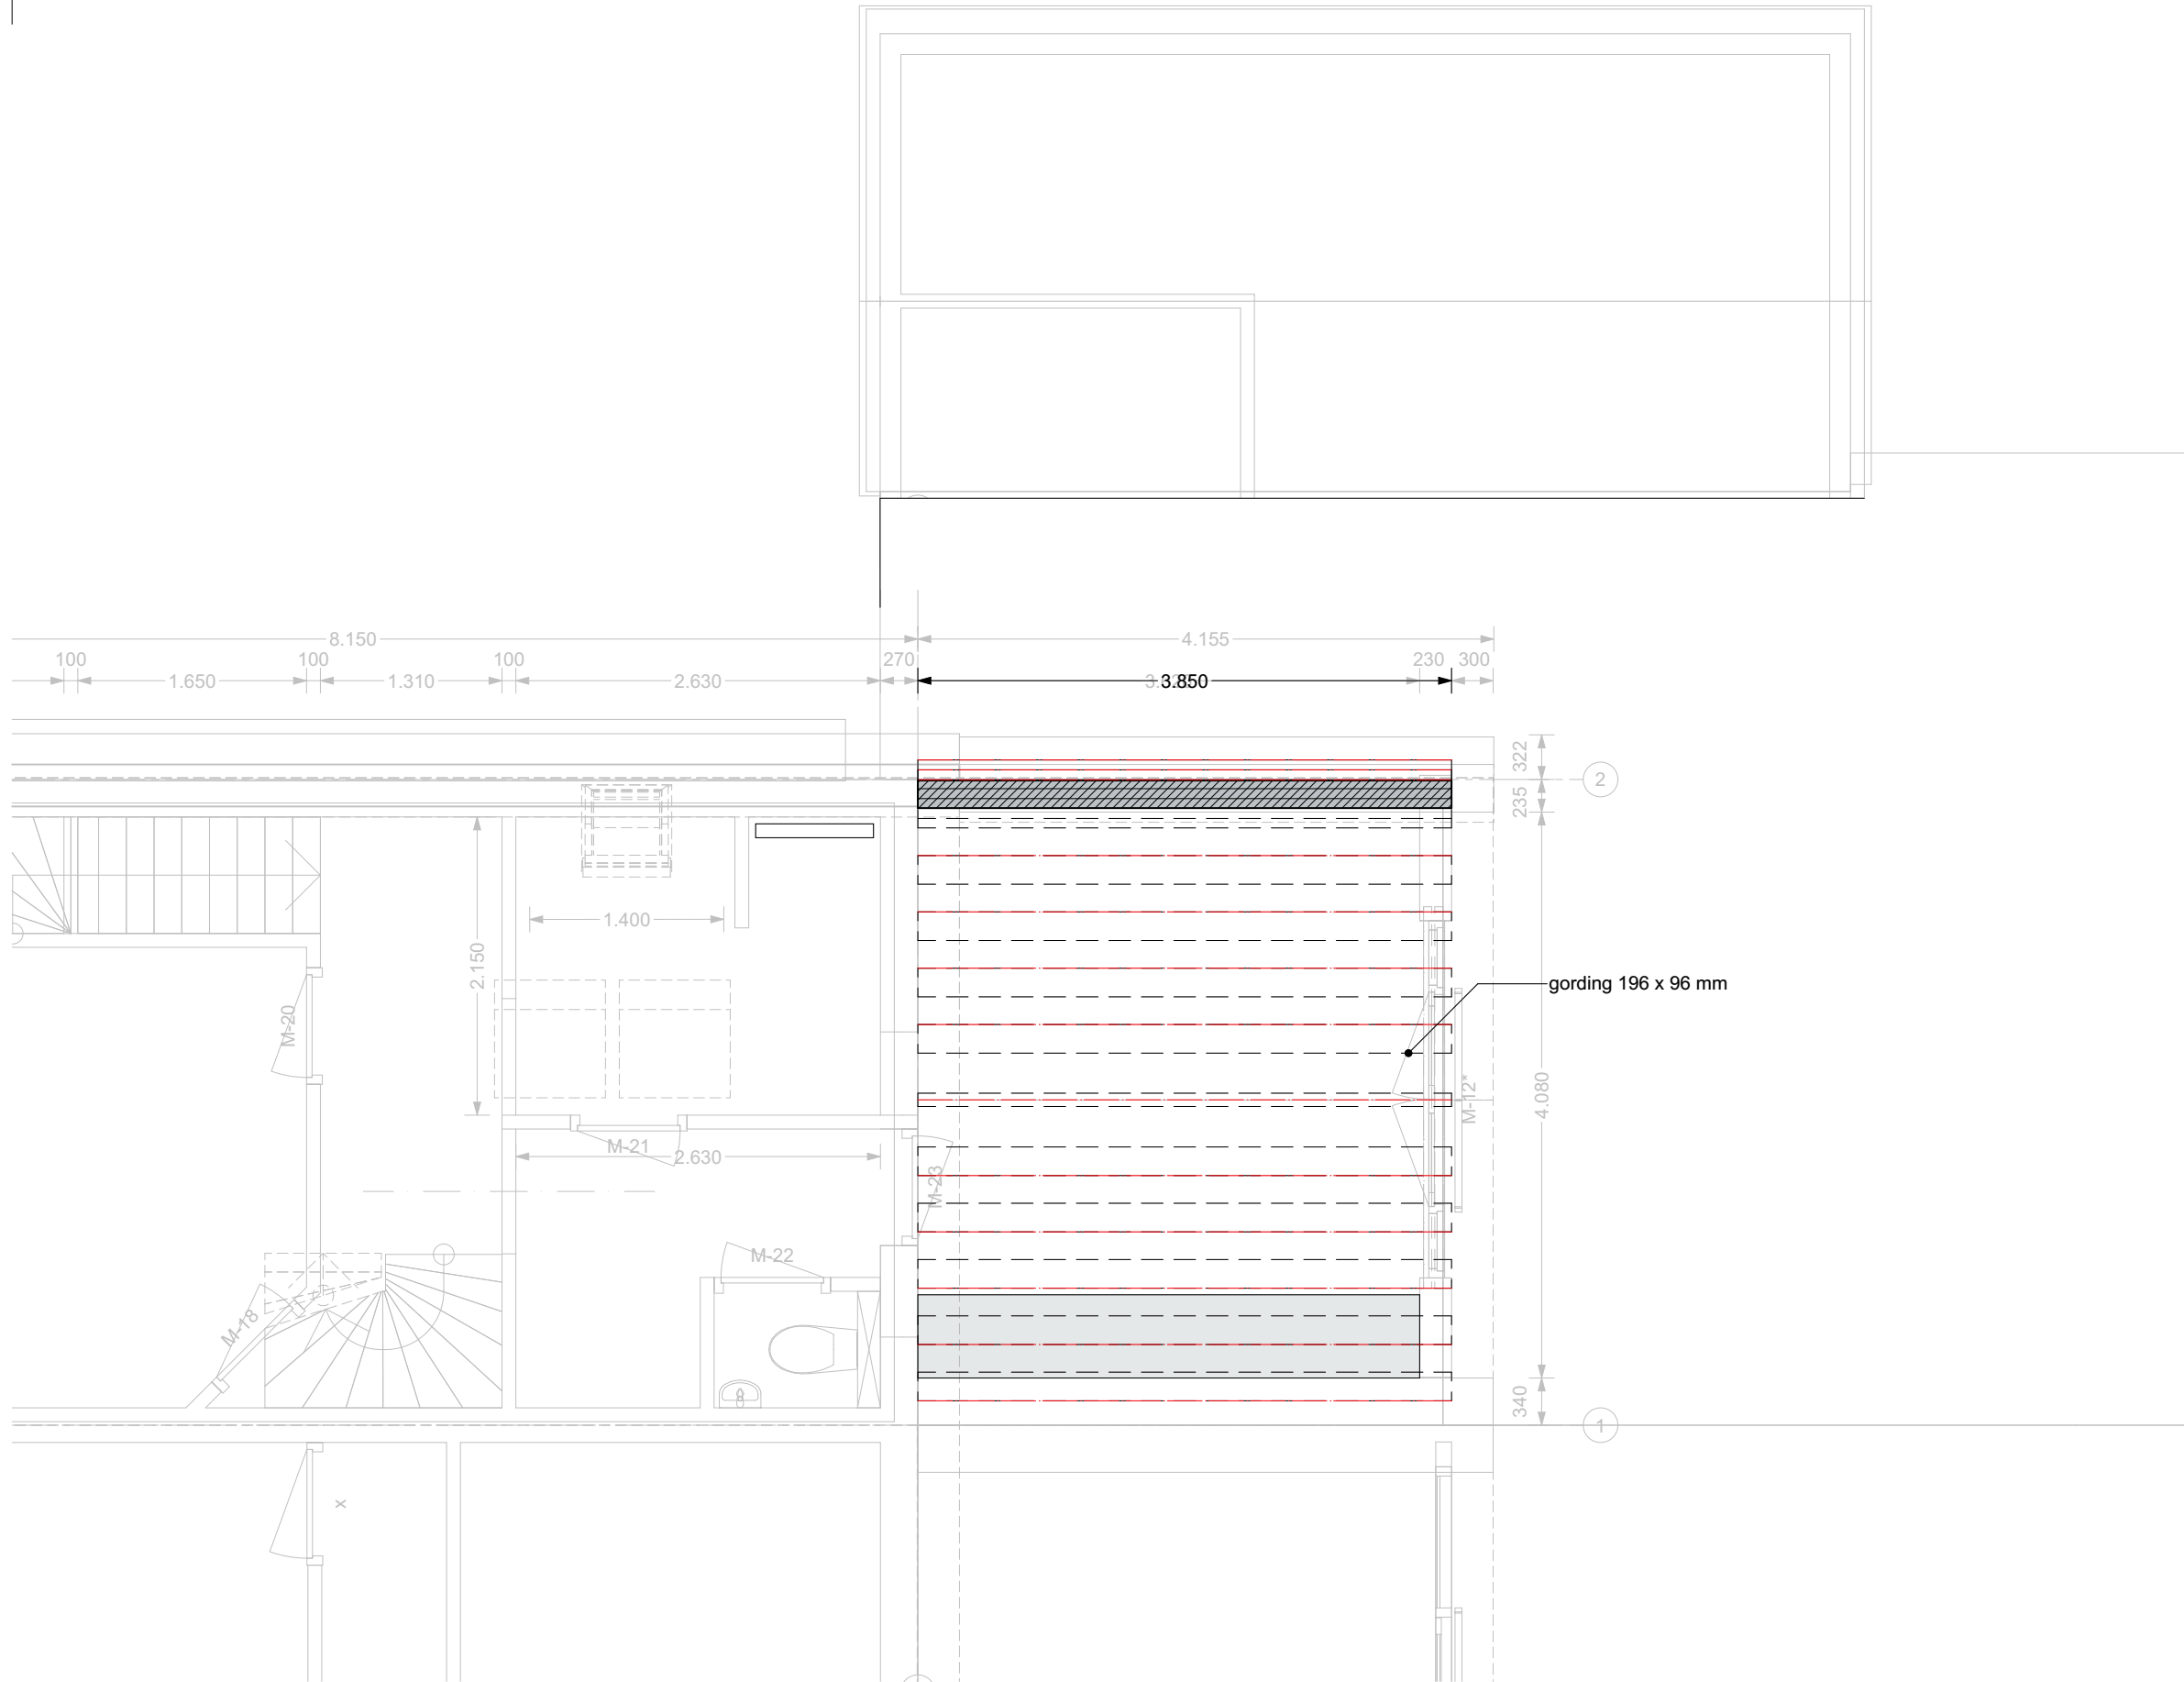





bestaand

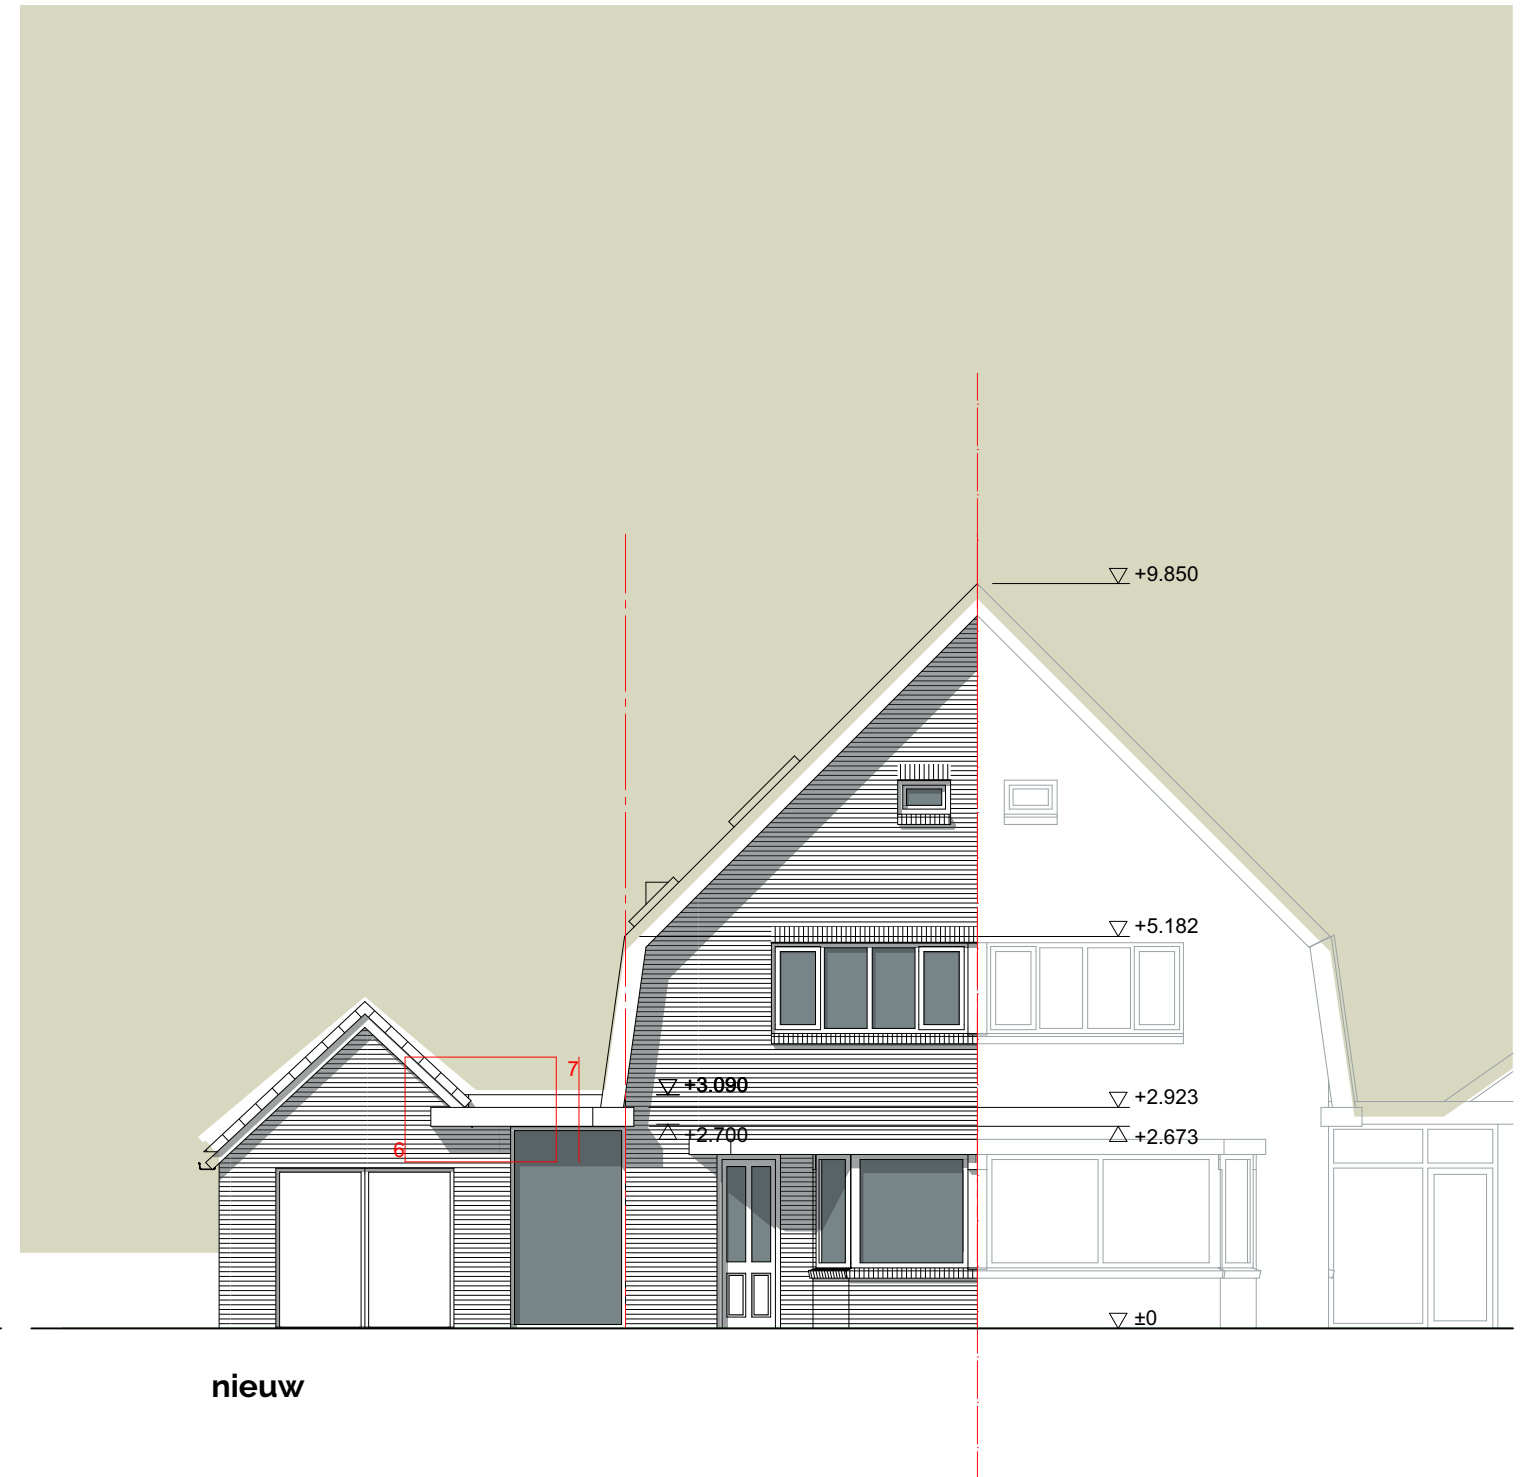

nieuw

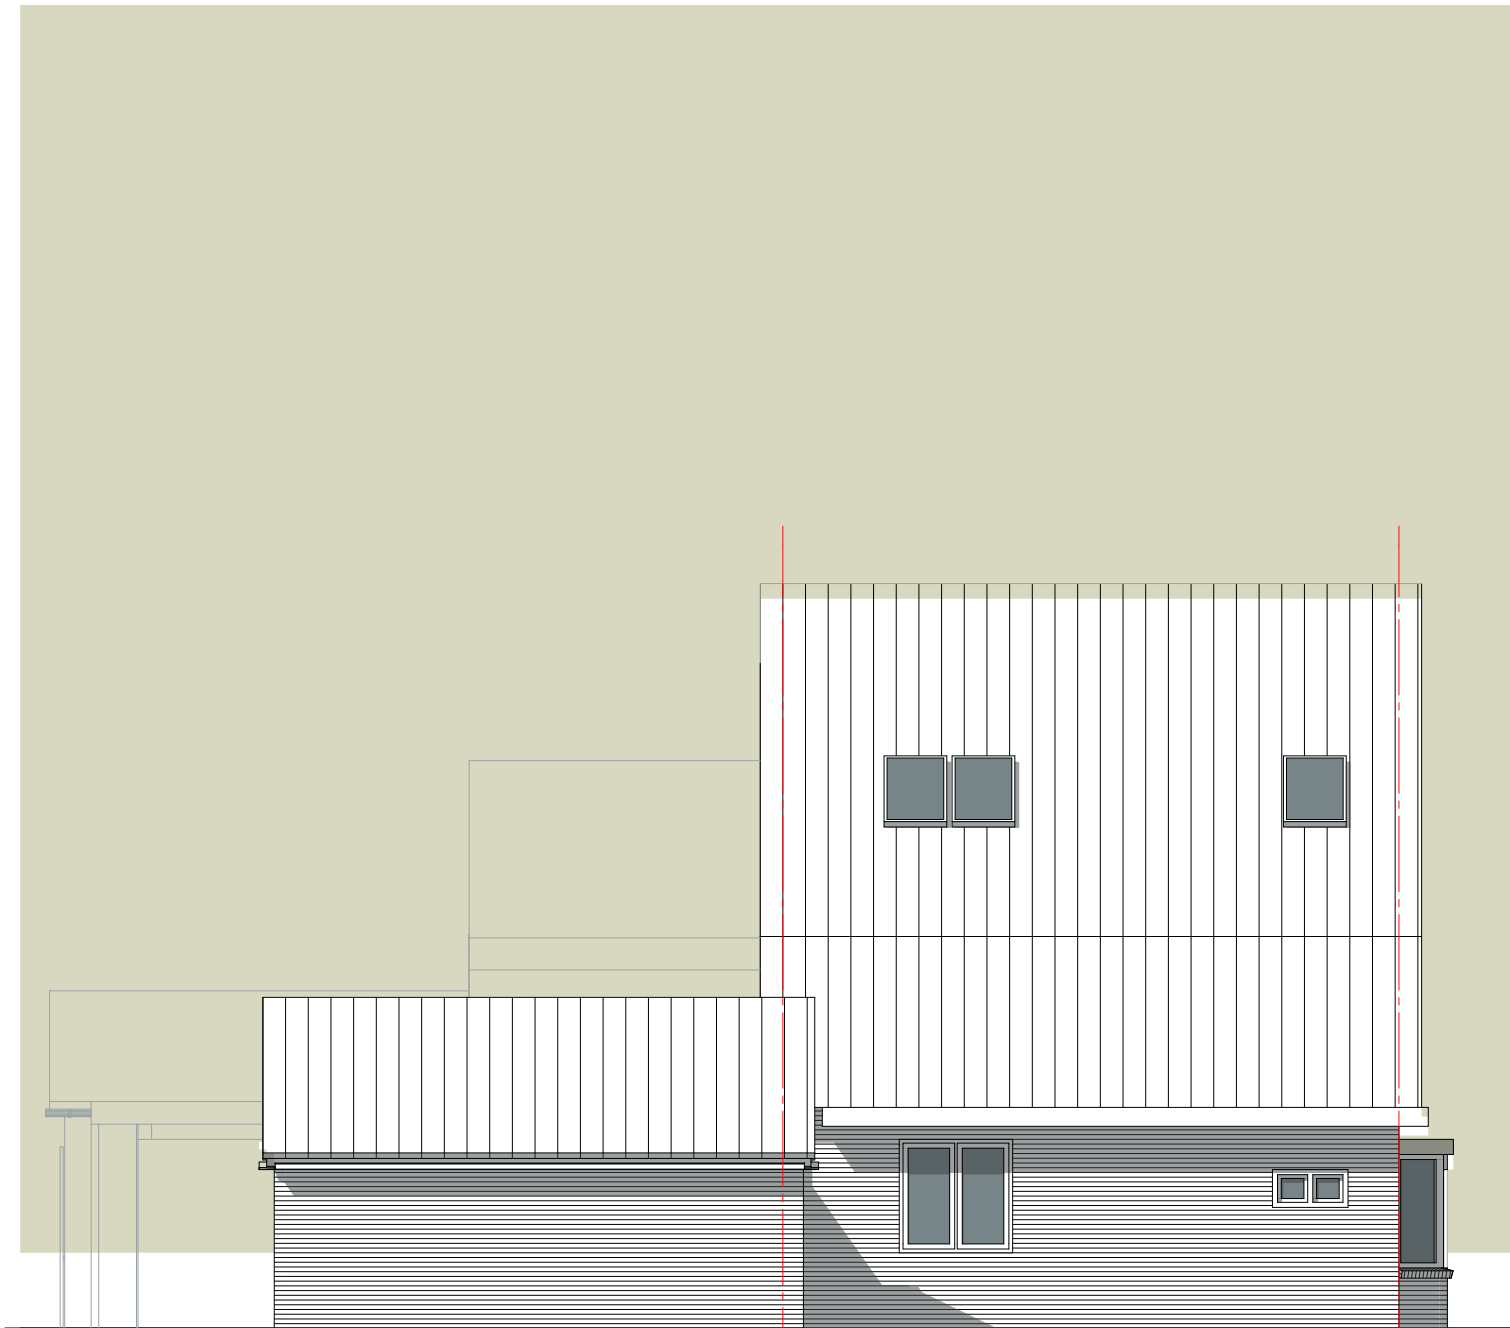


bestaand

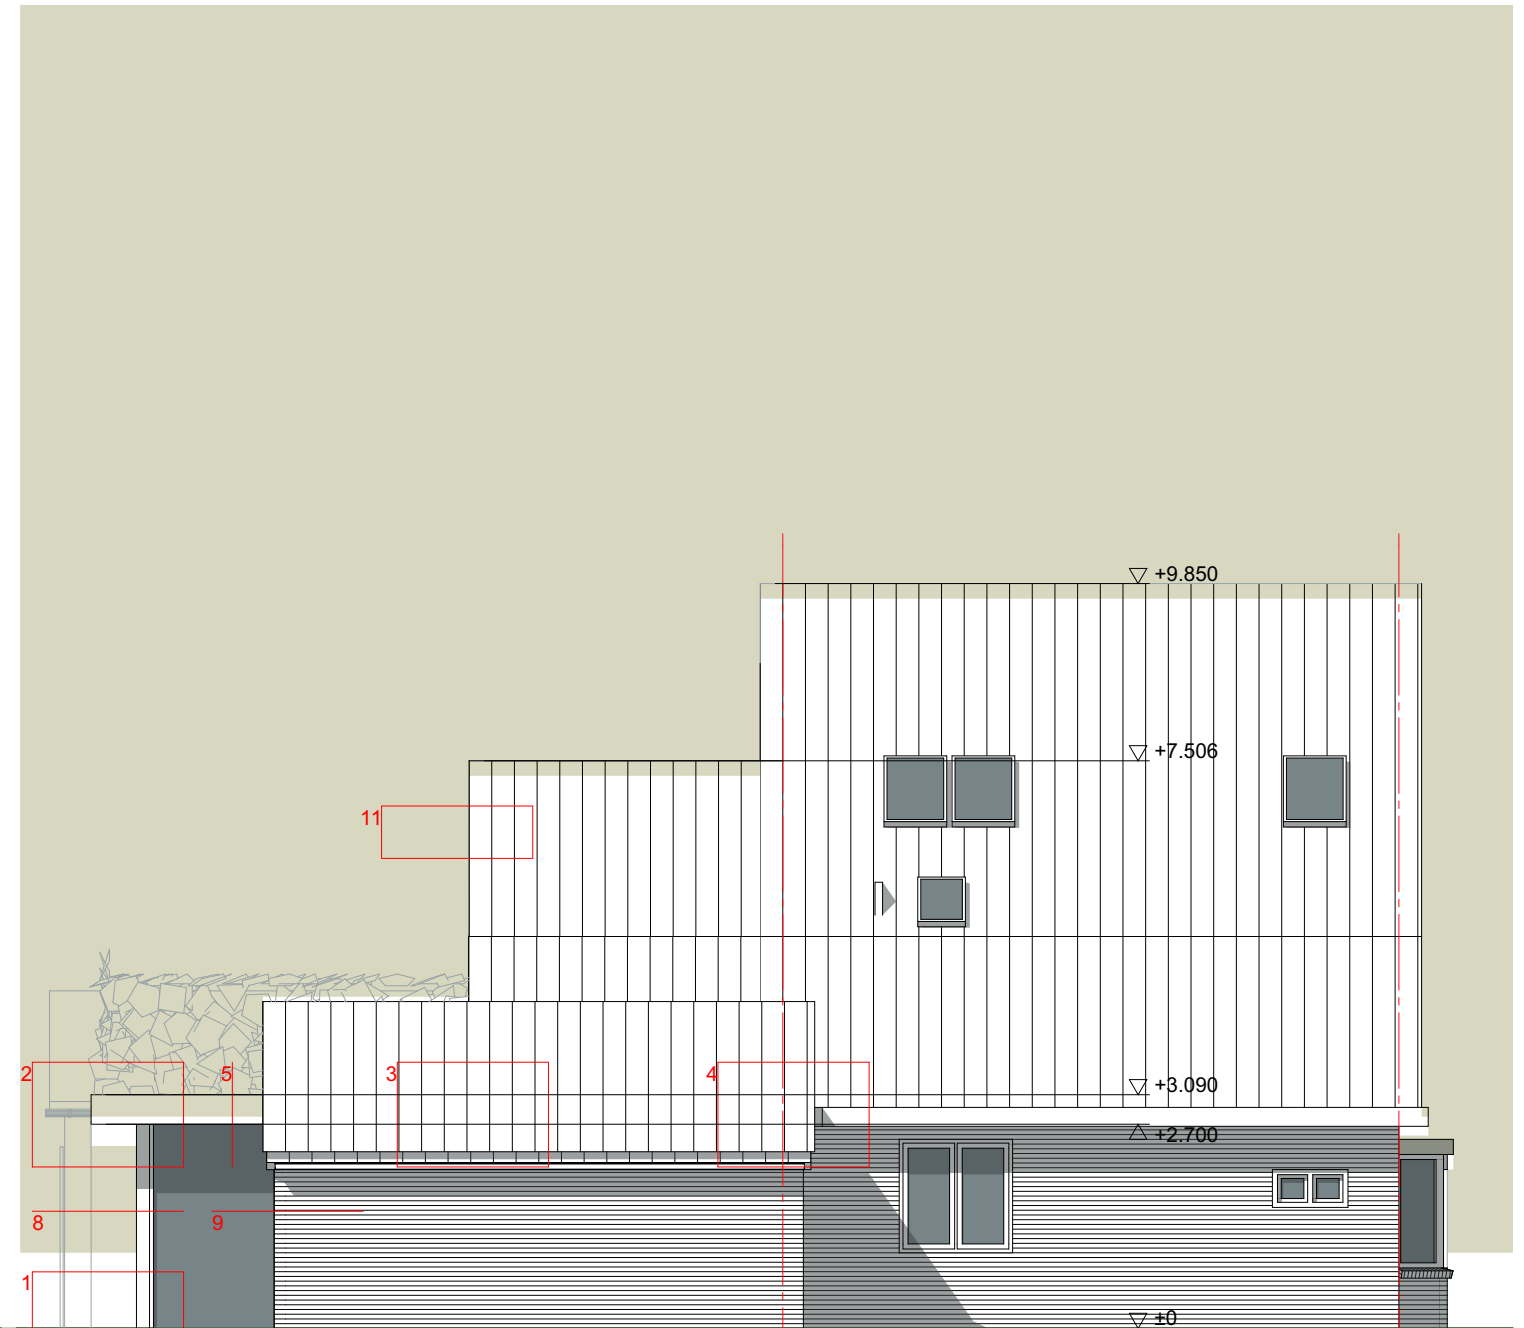


nieuw










bestaand

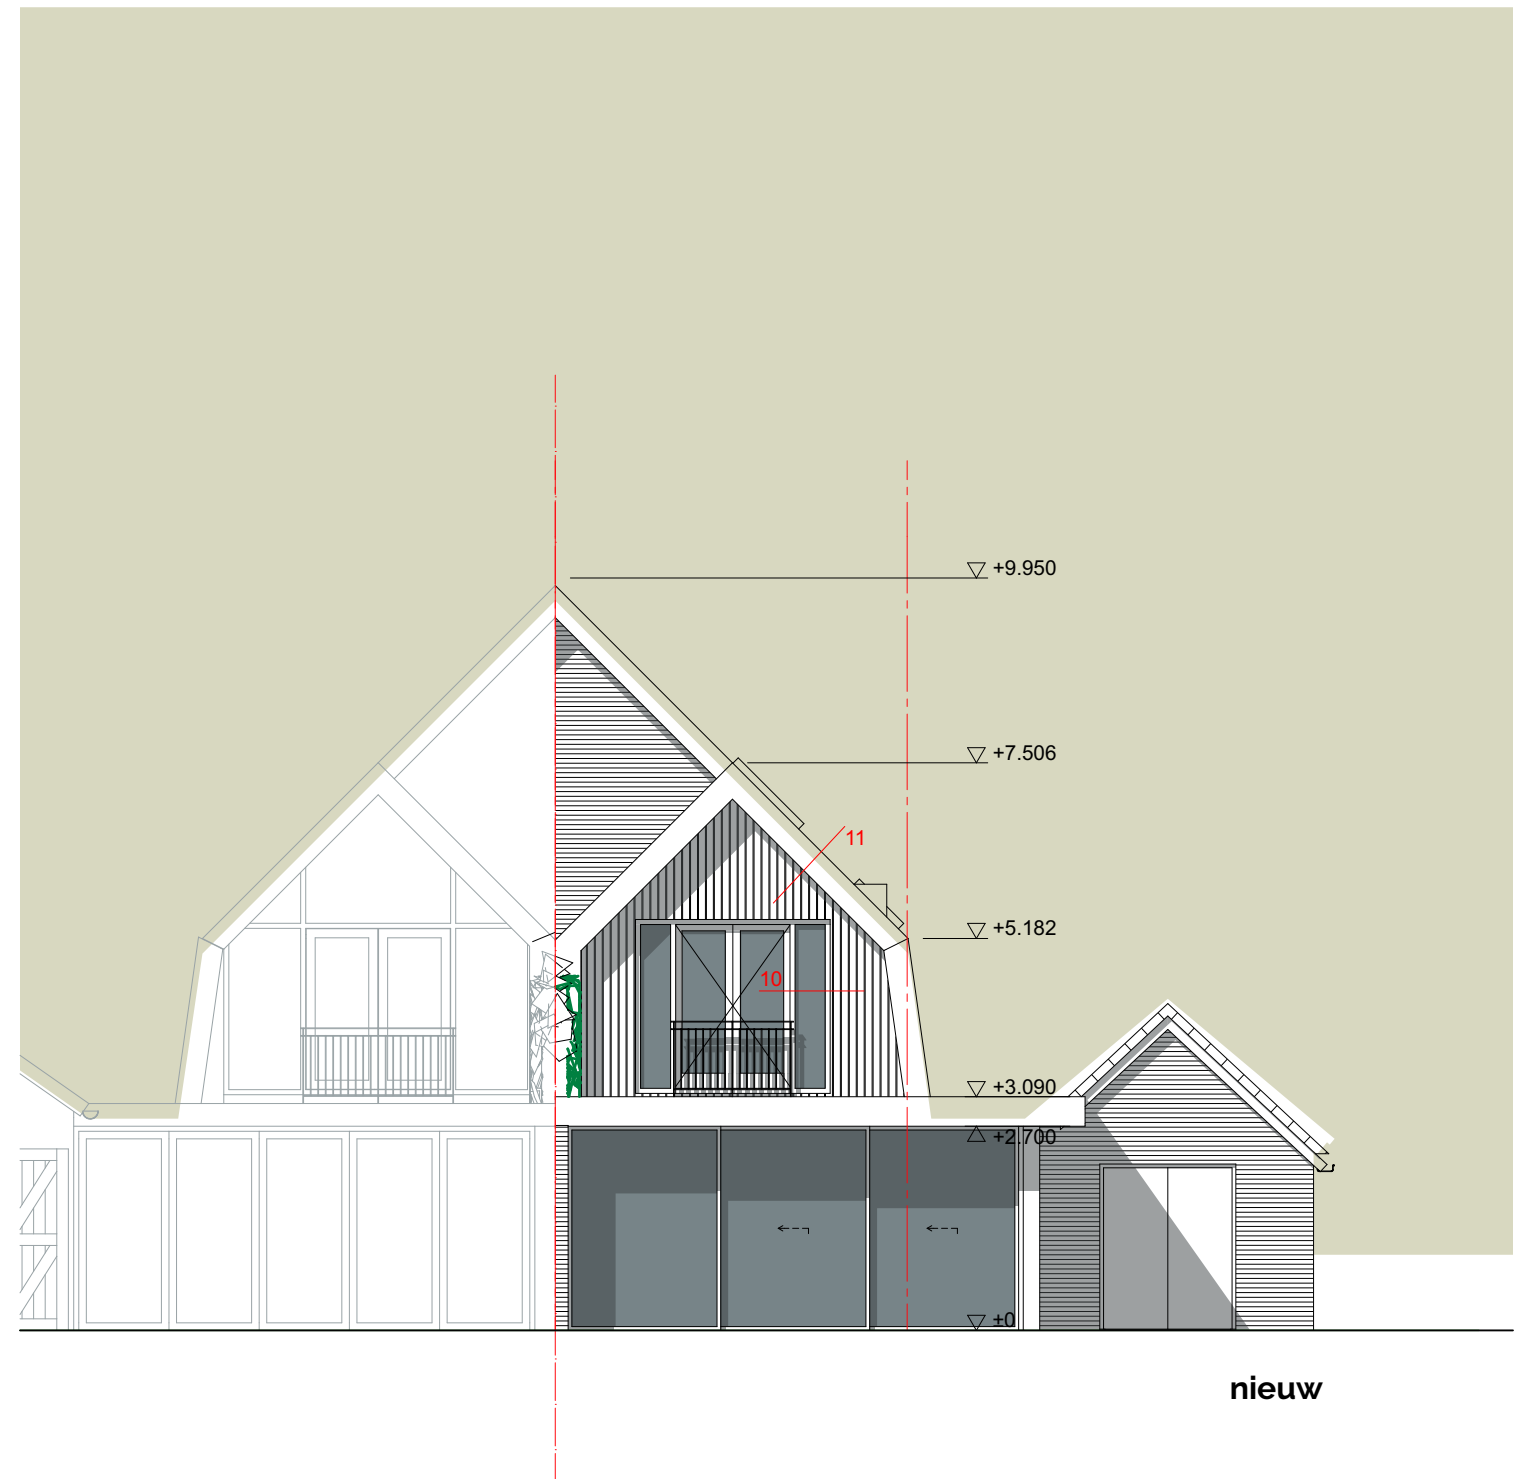



nieuw

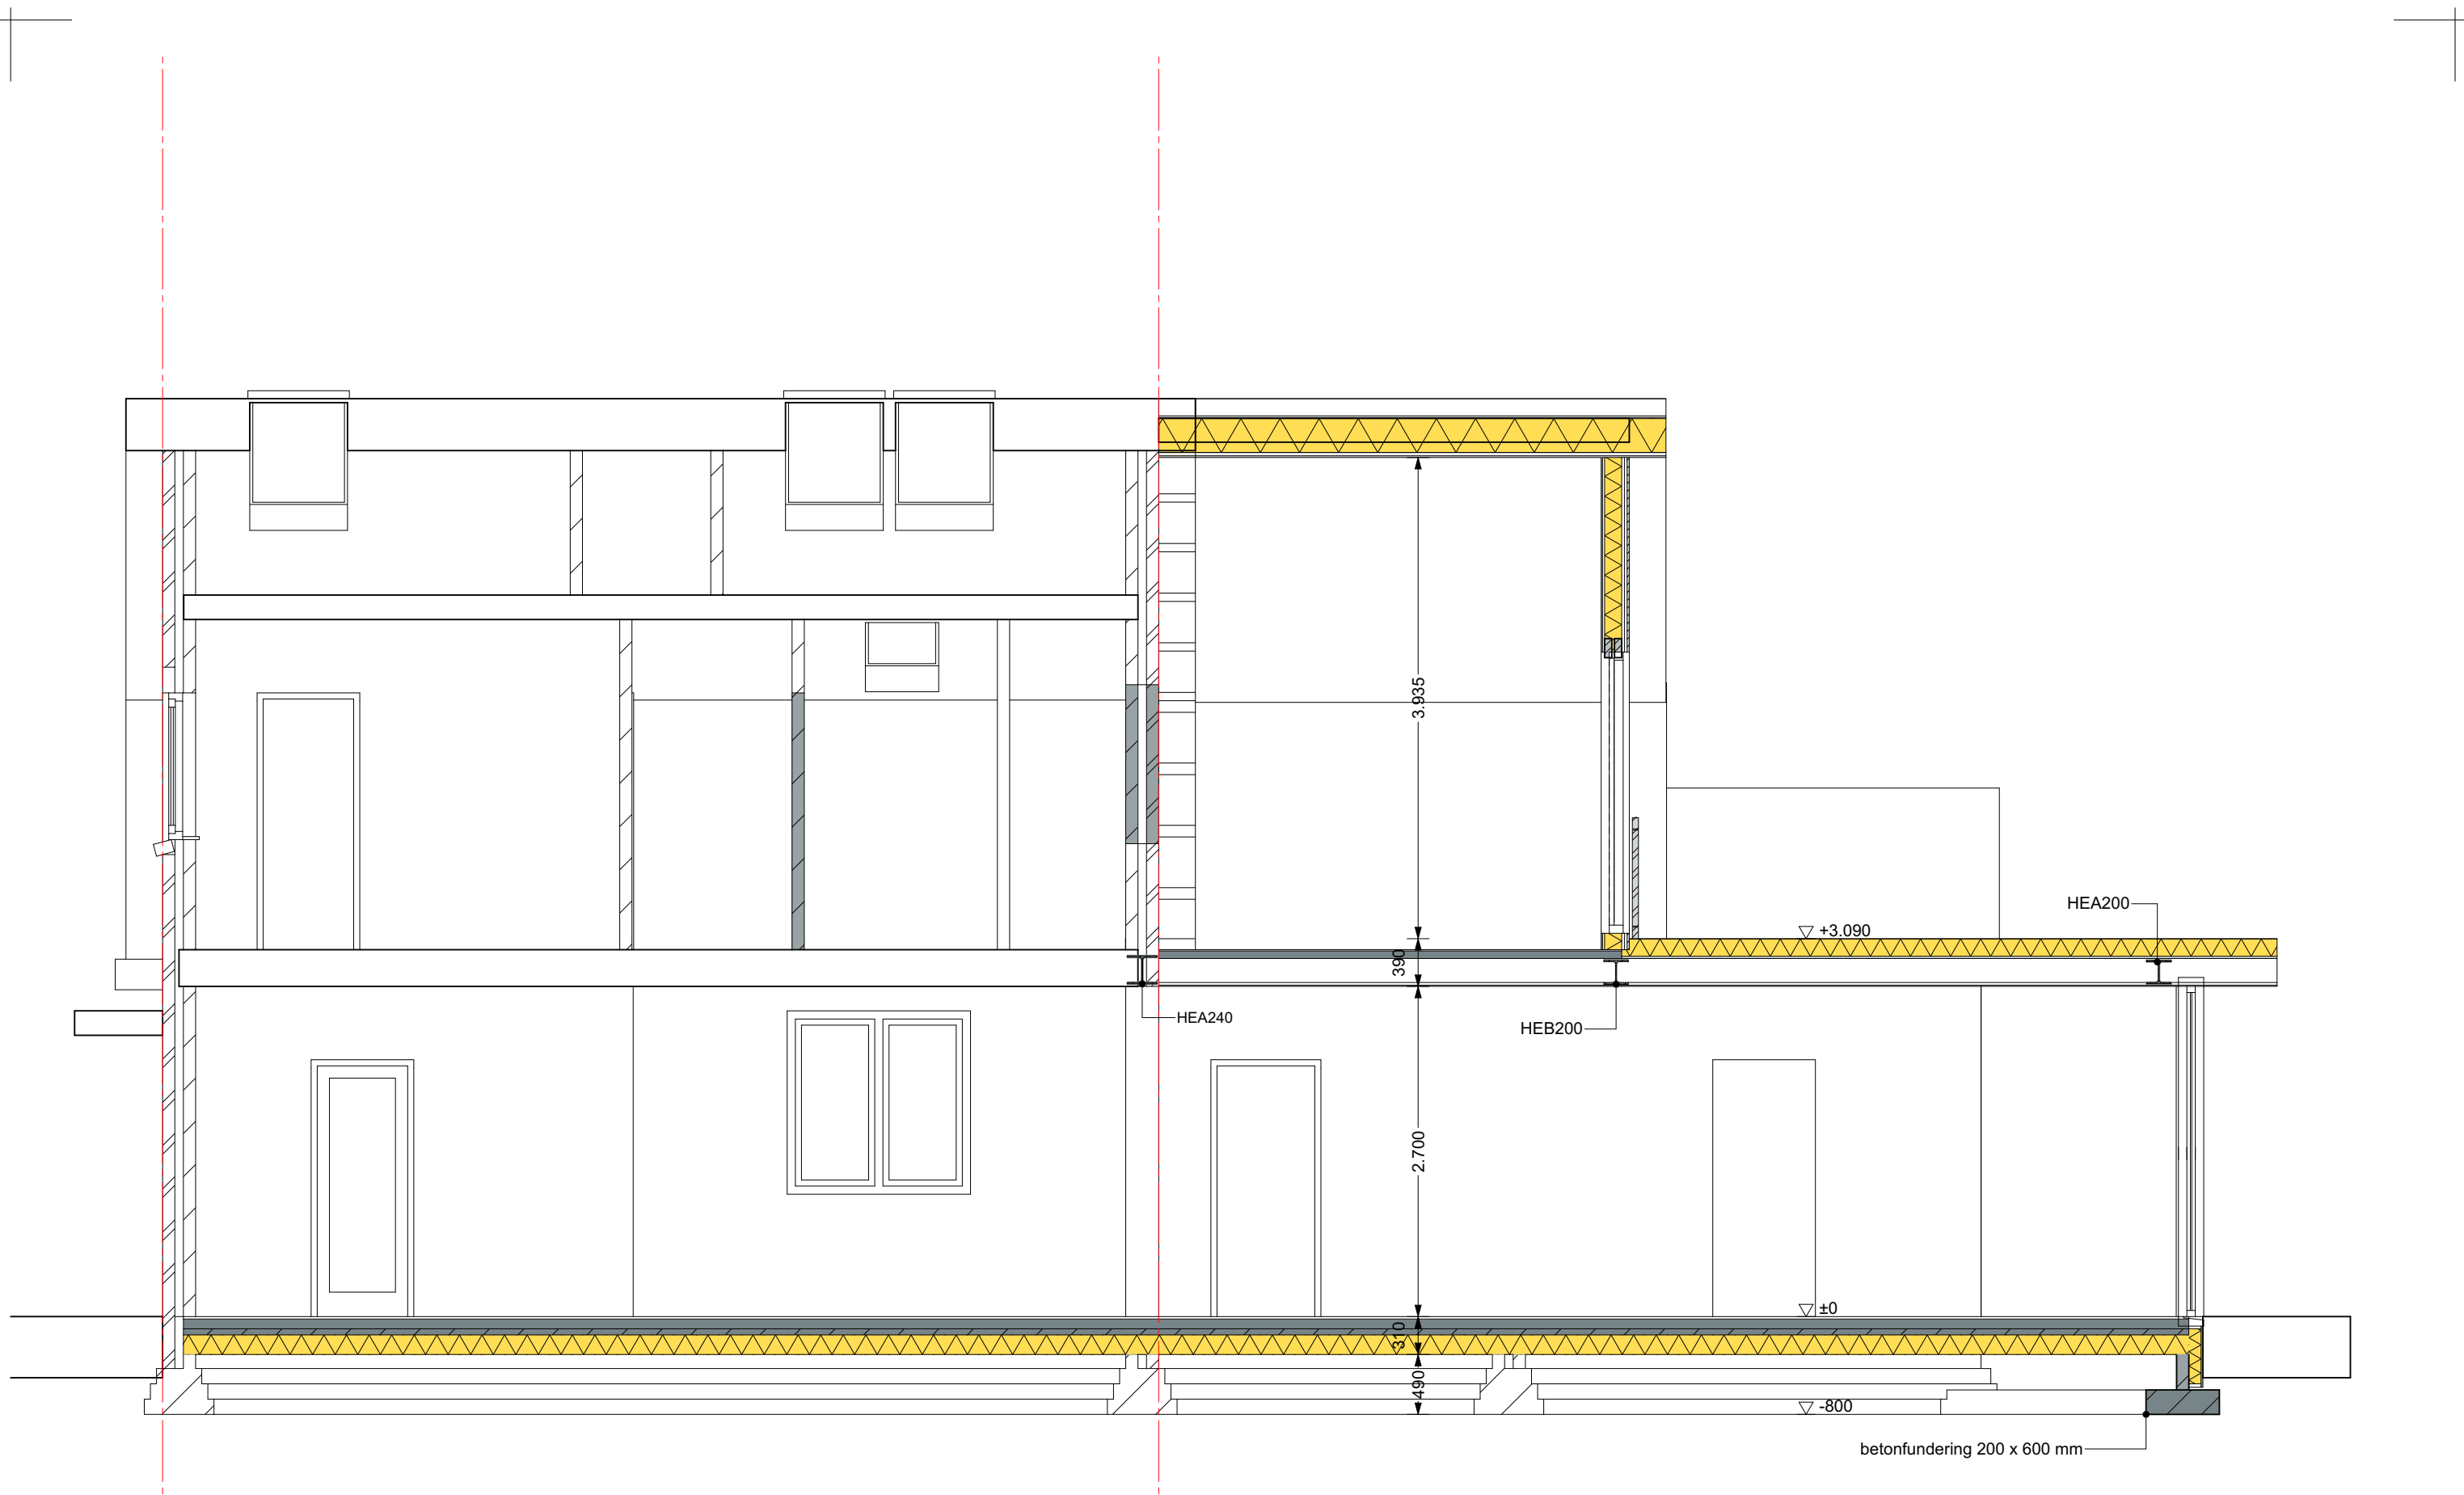


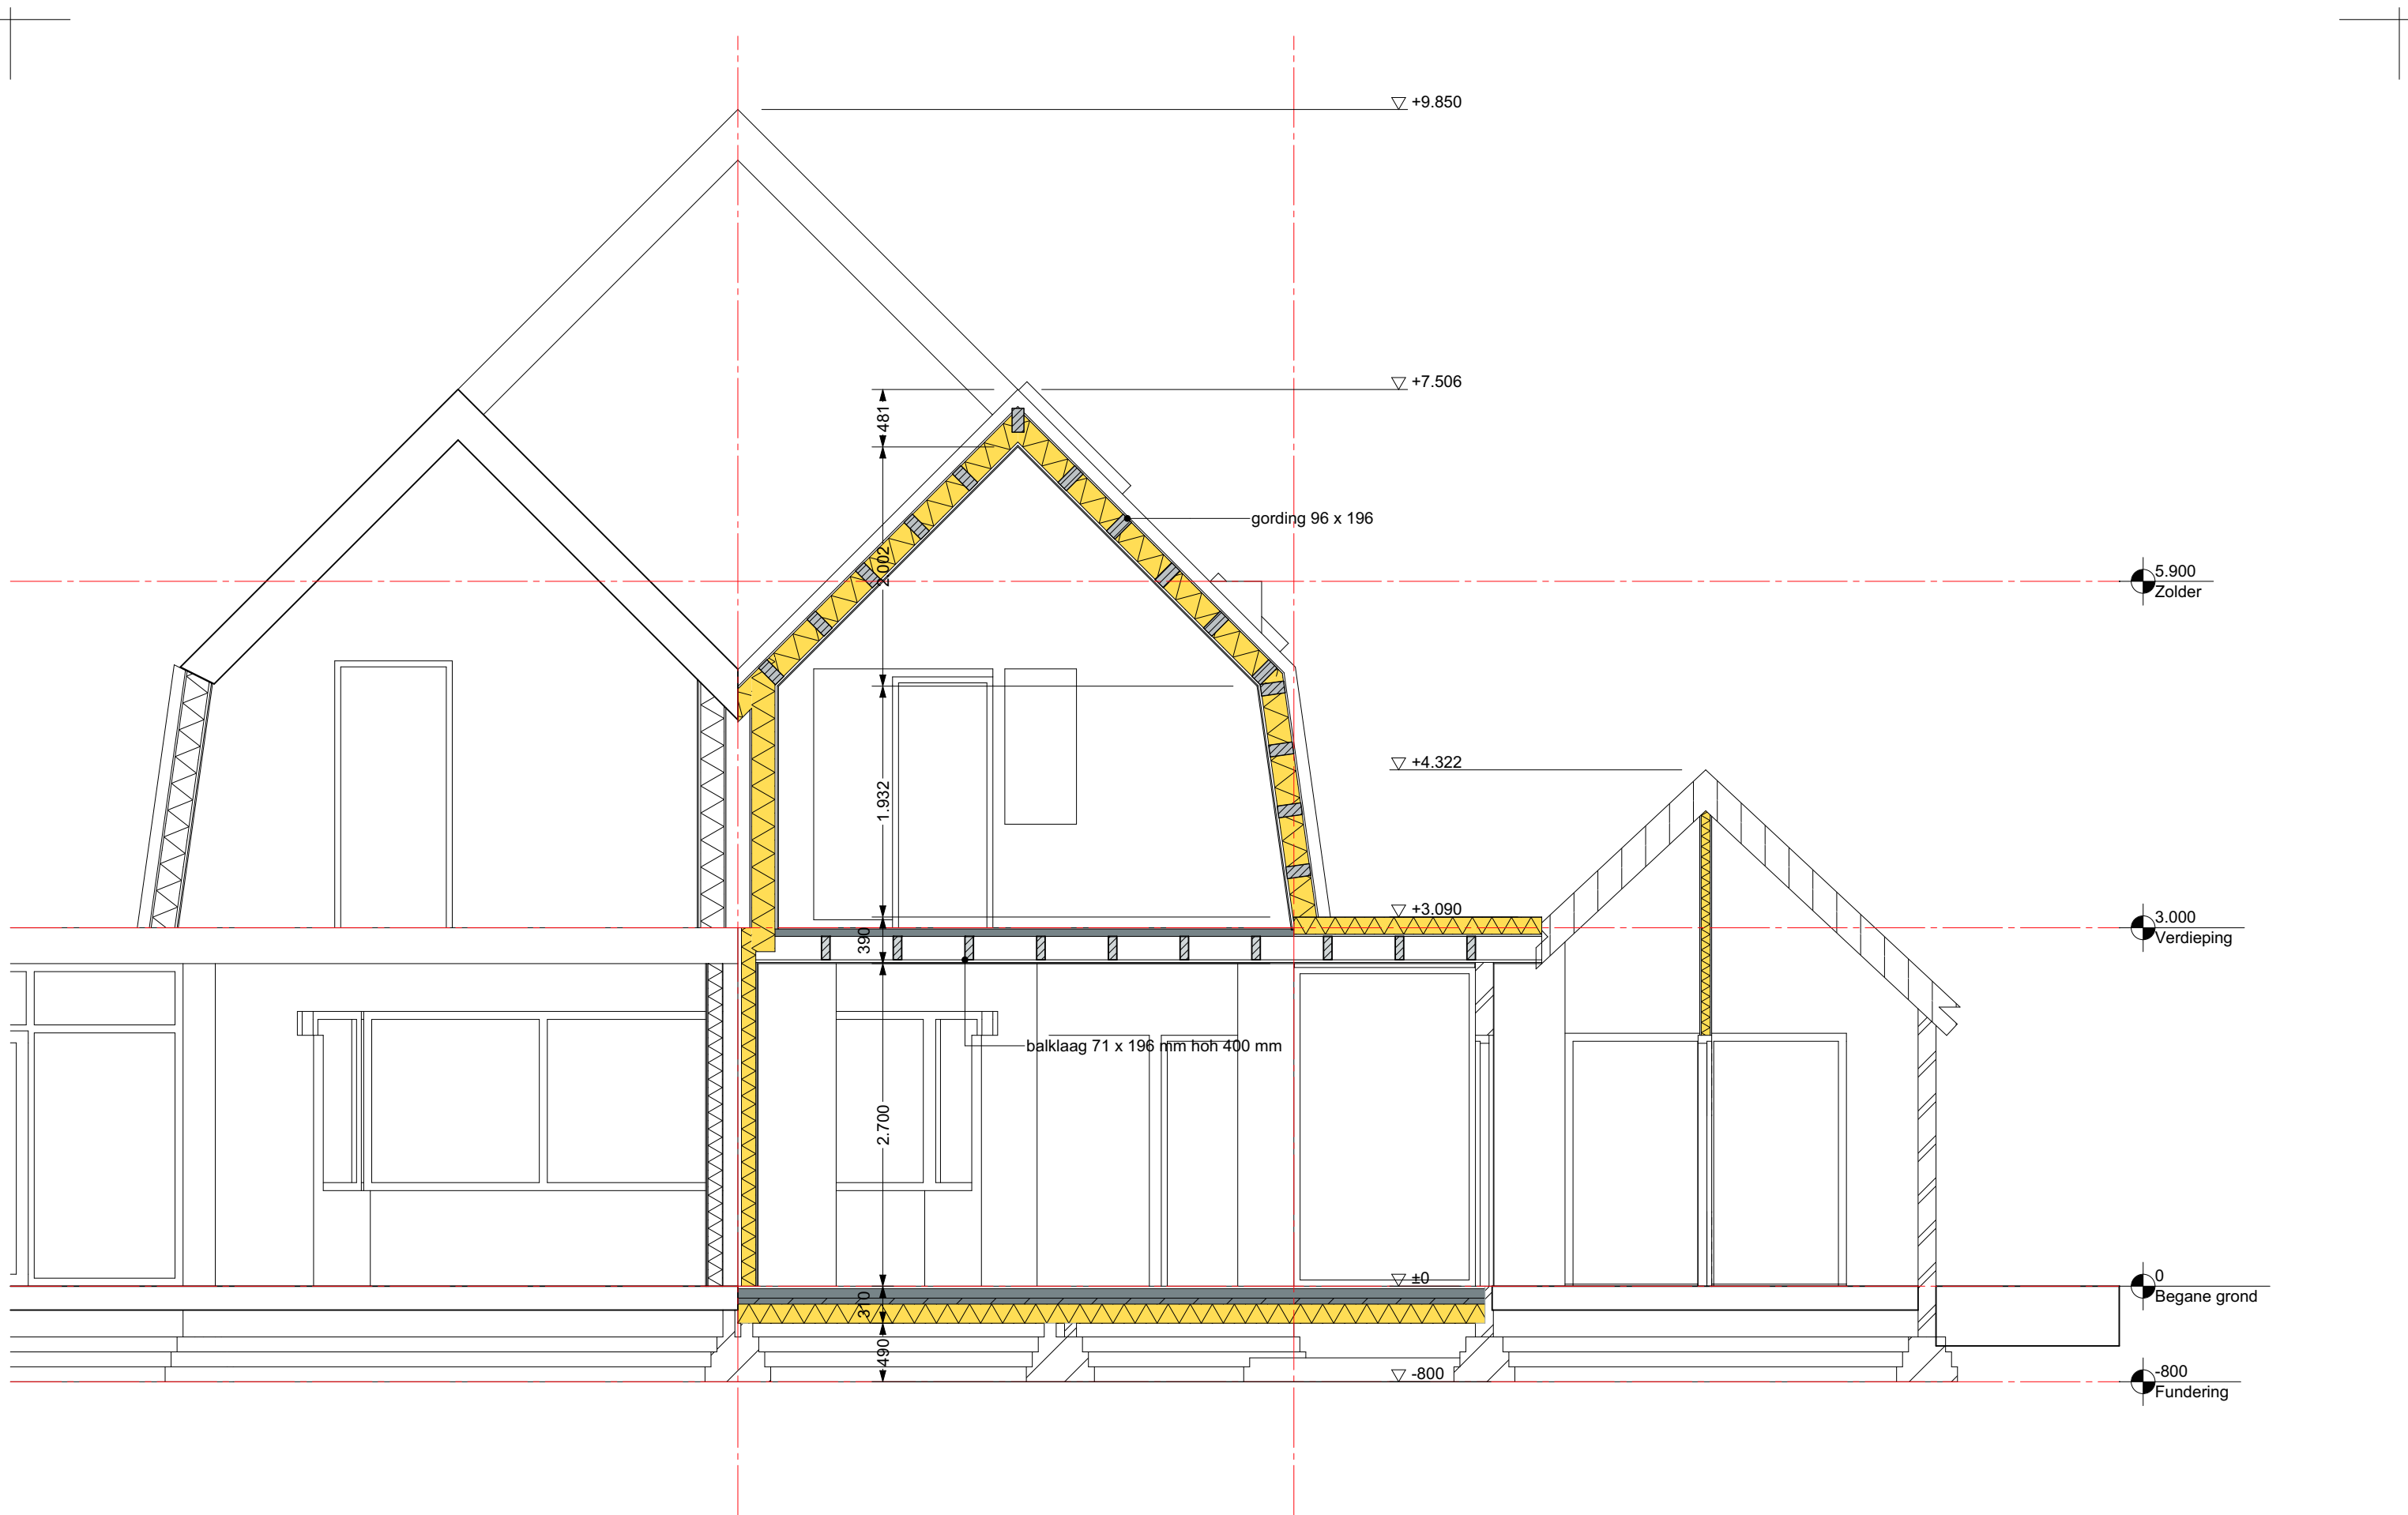

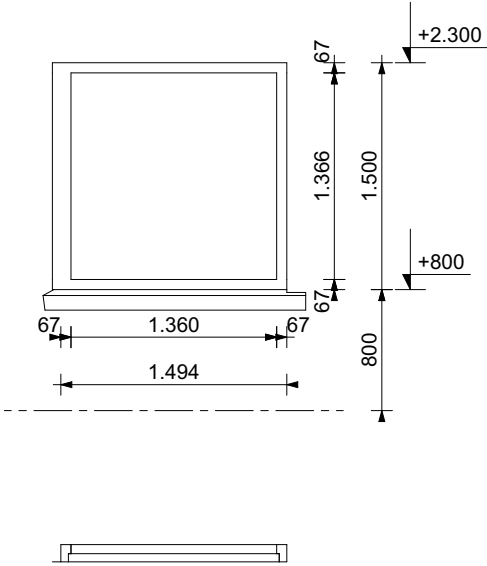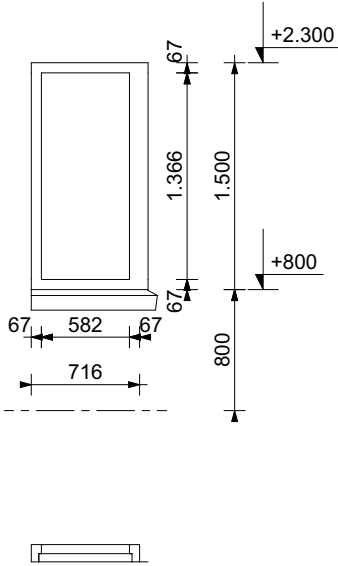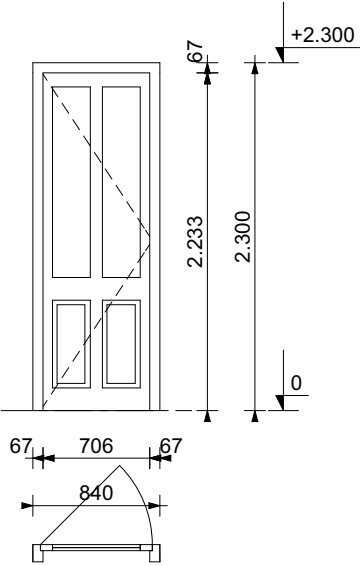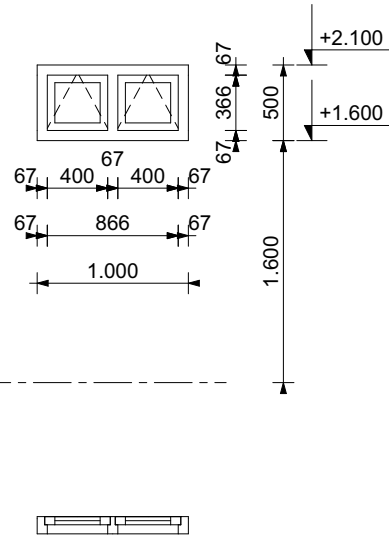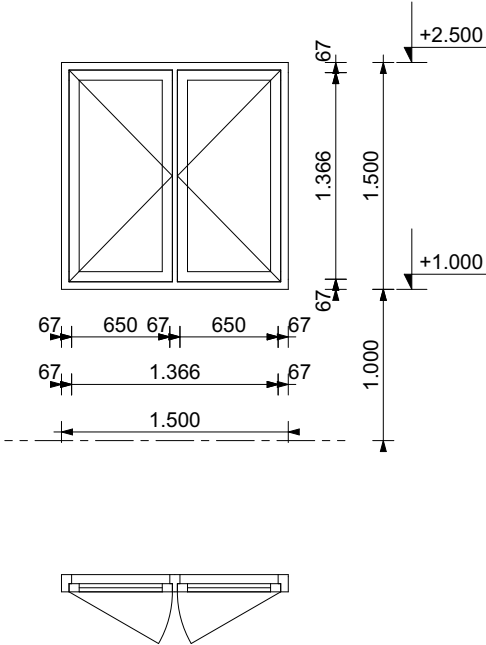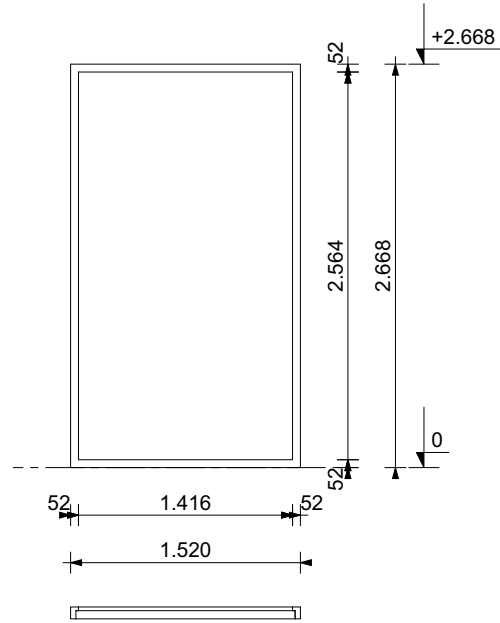M-01a	M-01b	M-02	M-03	M-04	M-05*
					

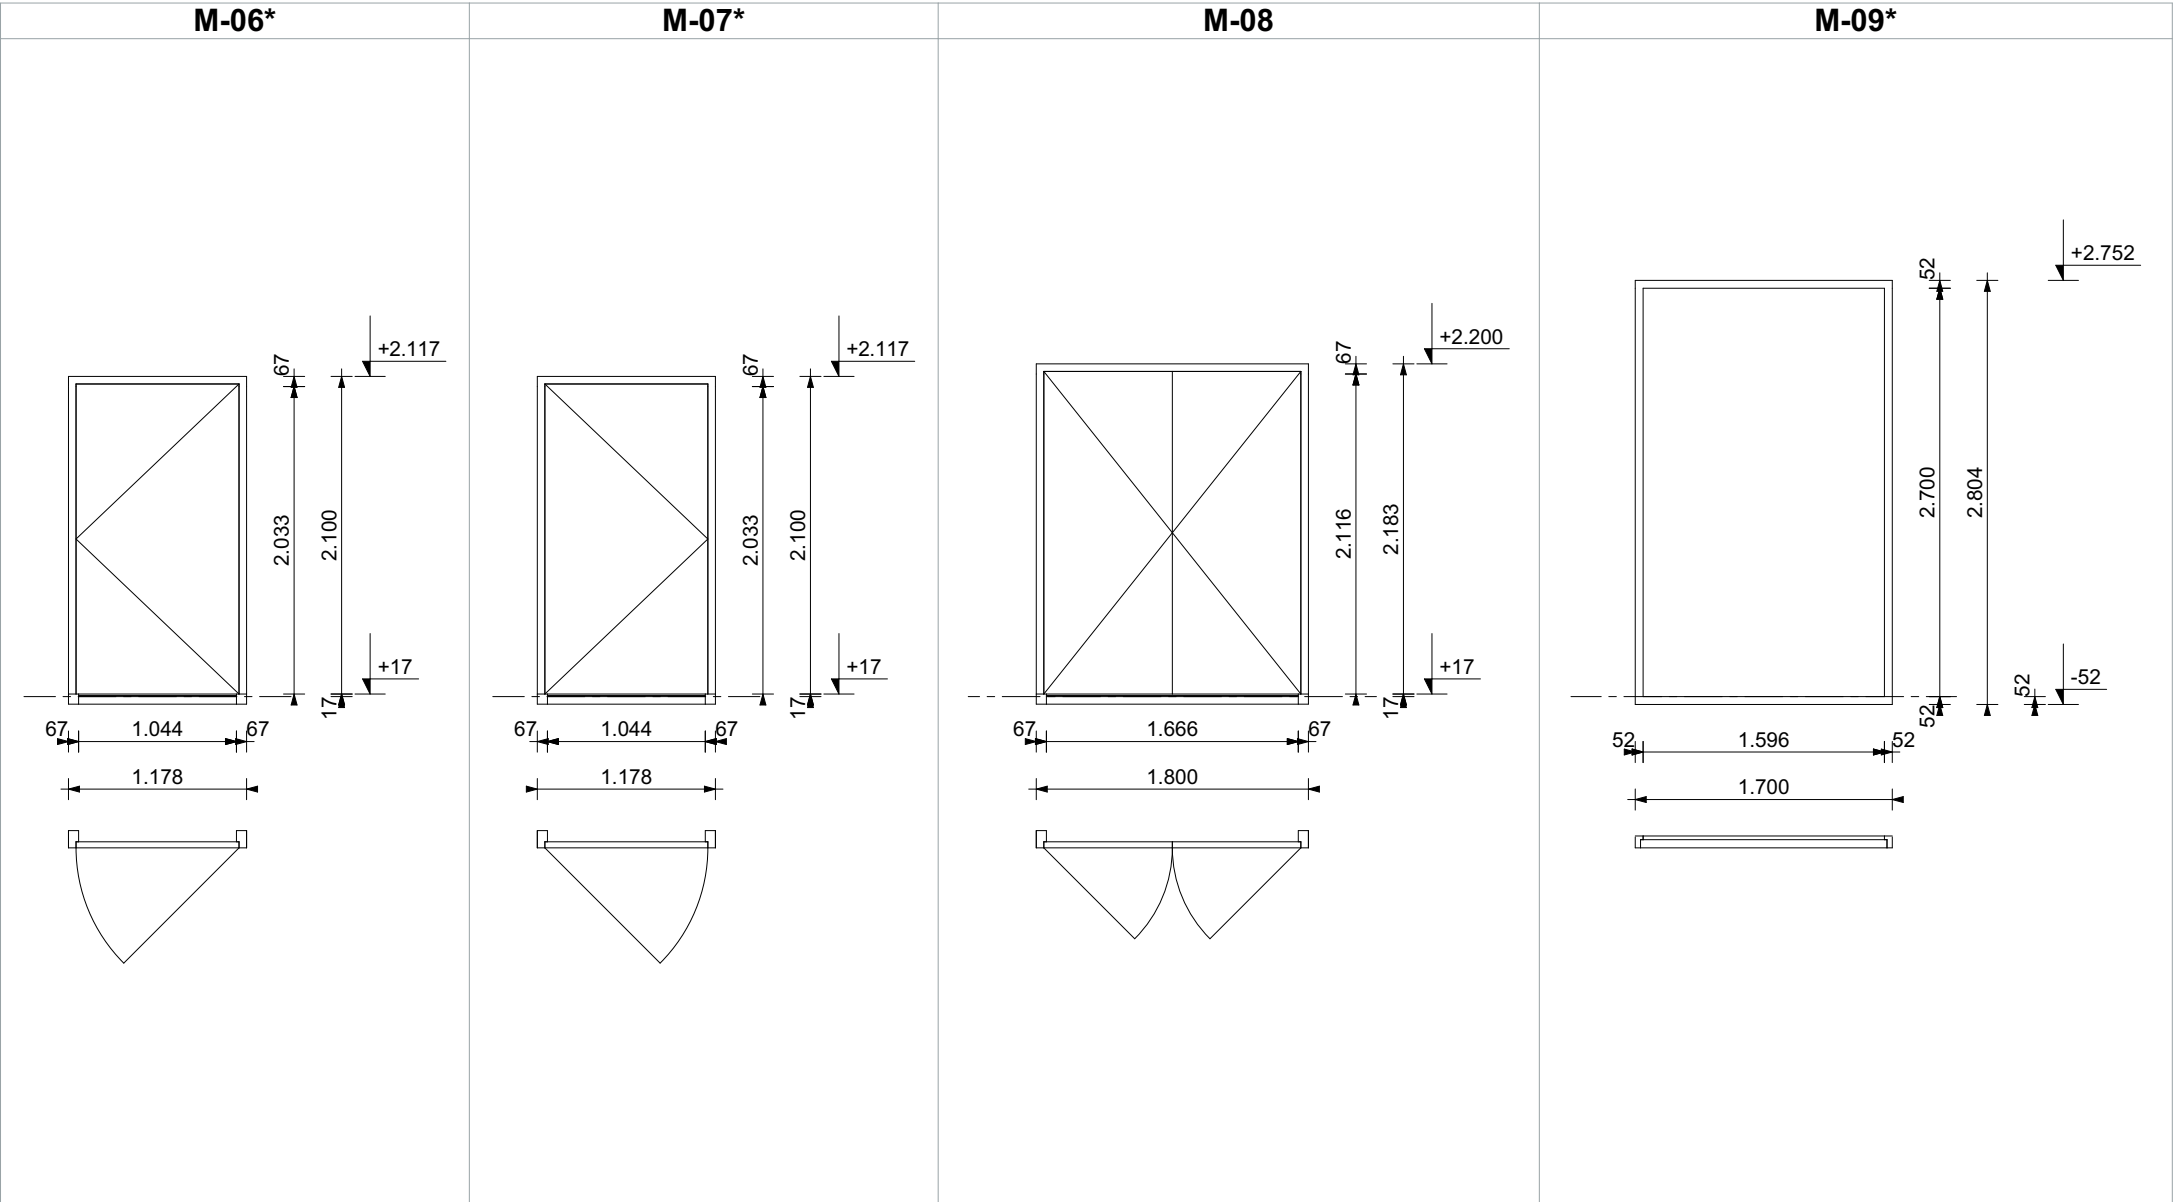

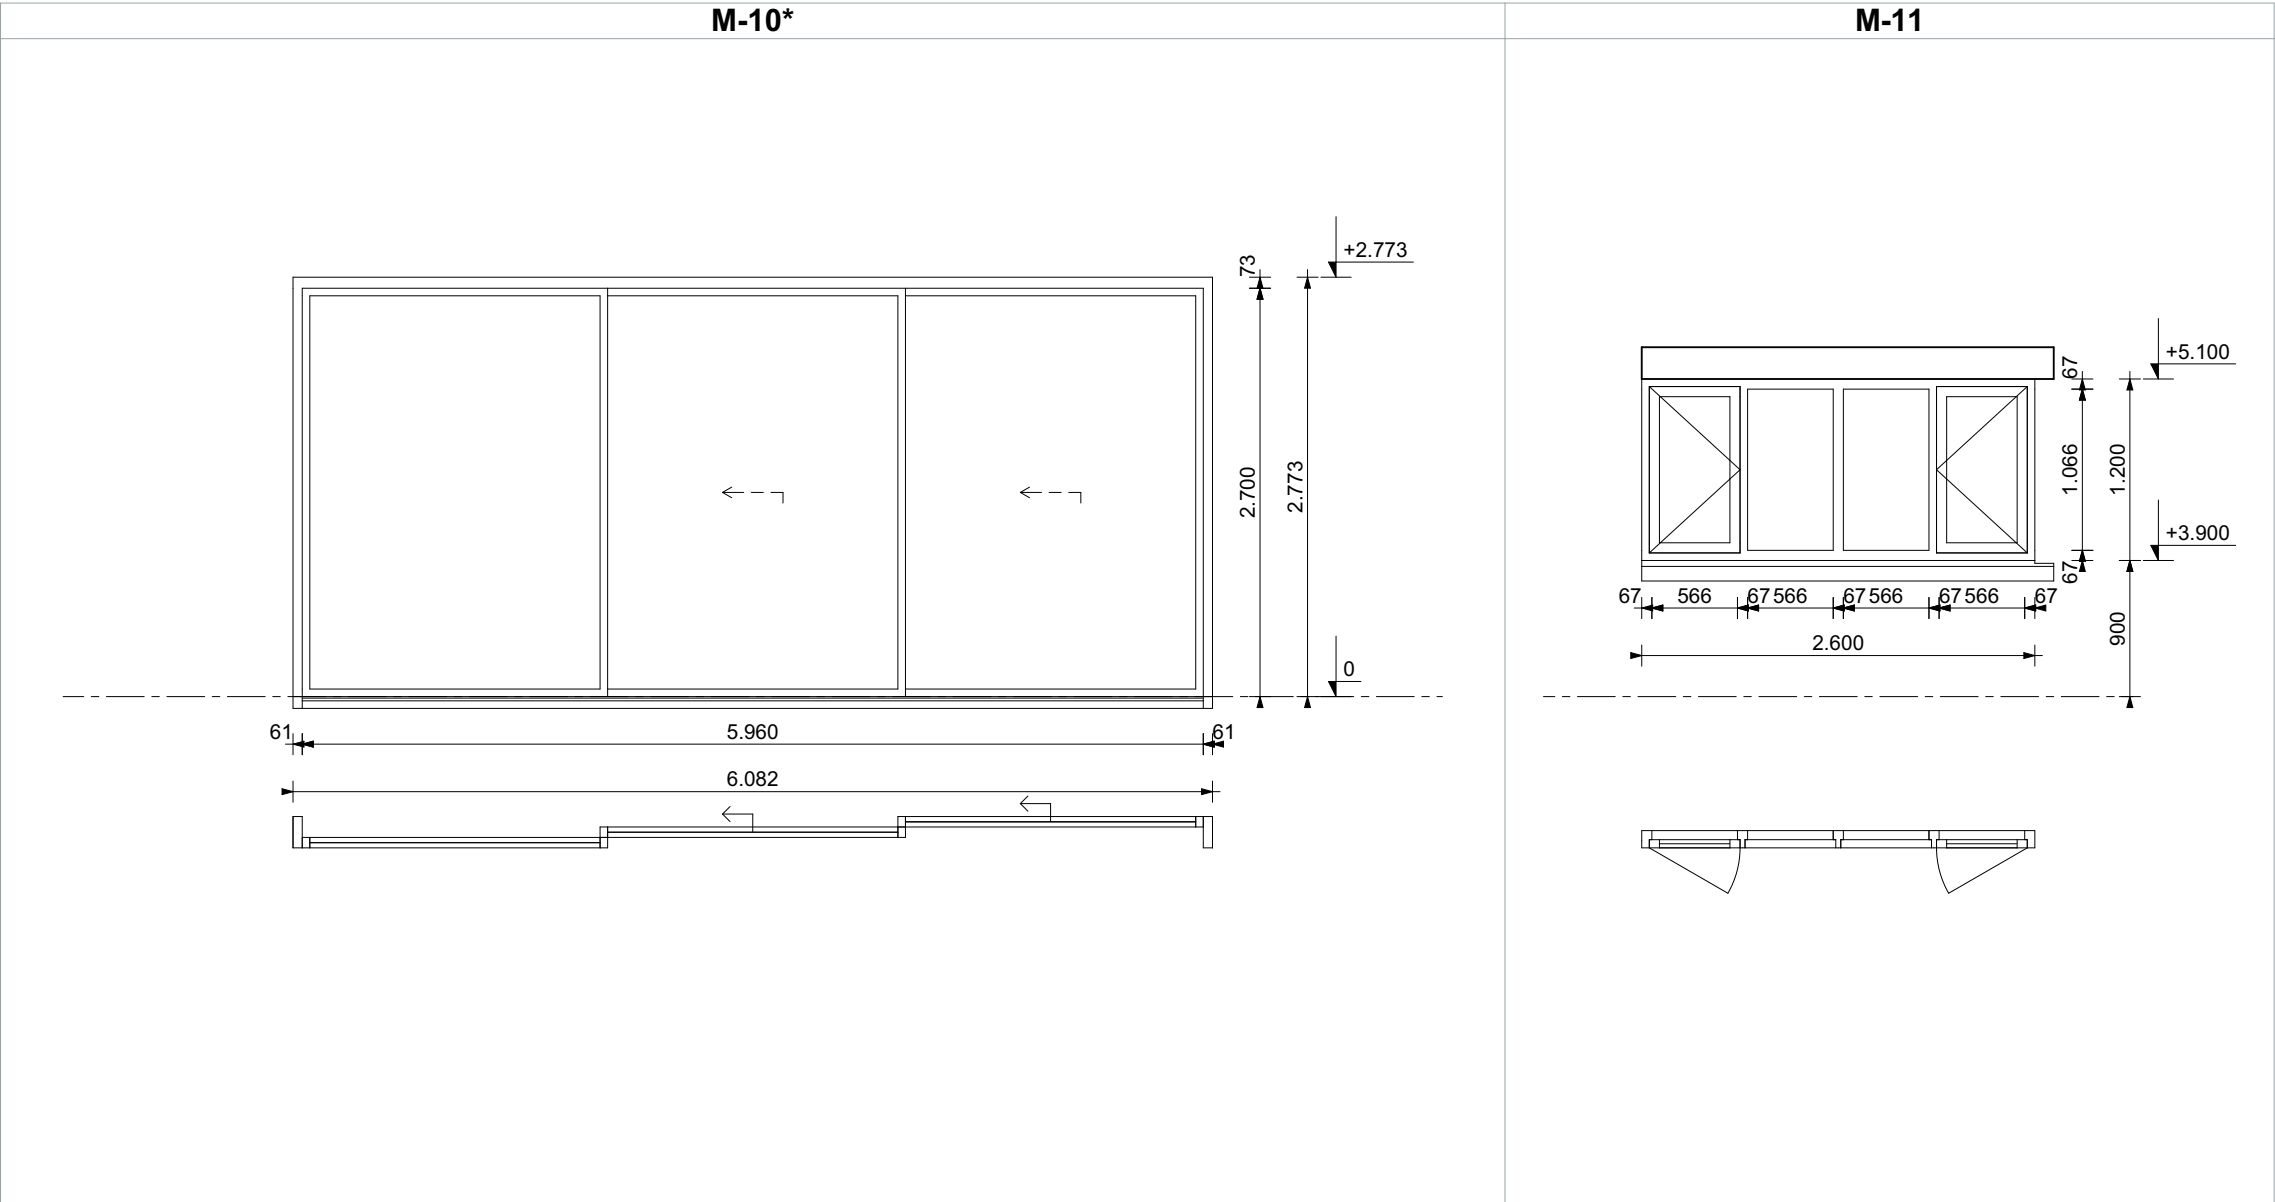

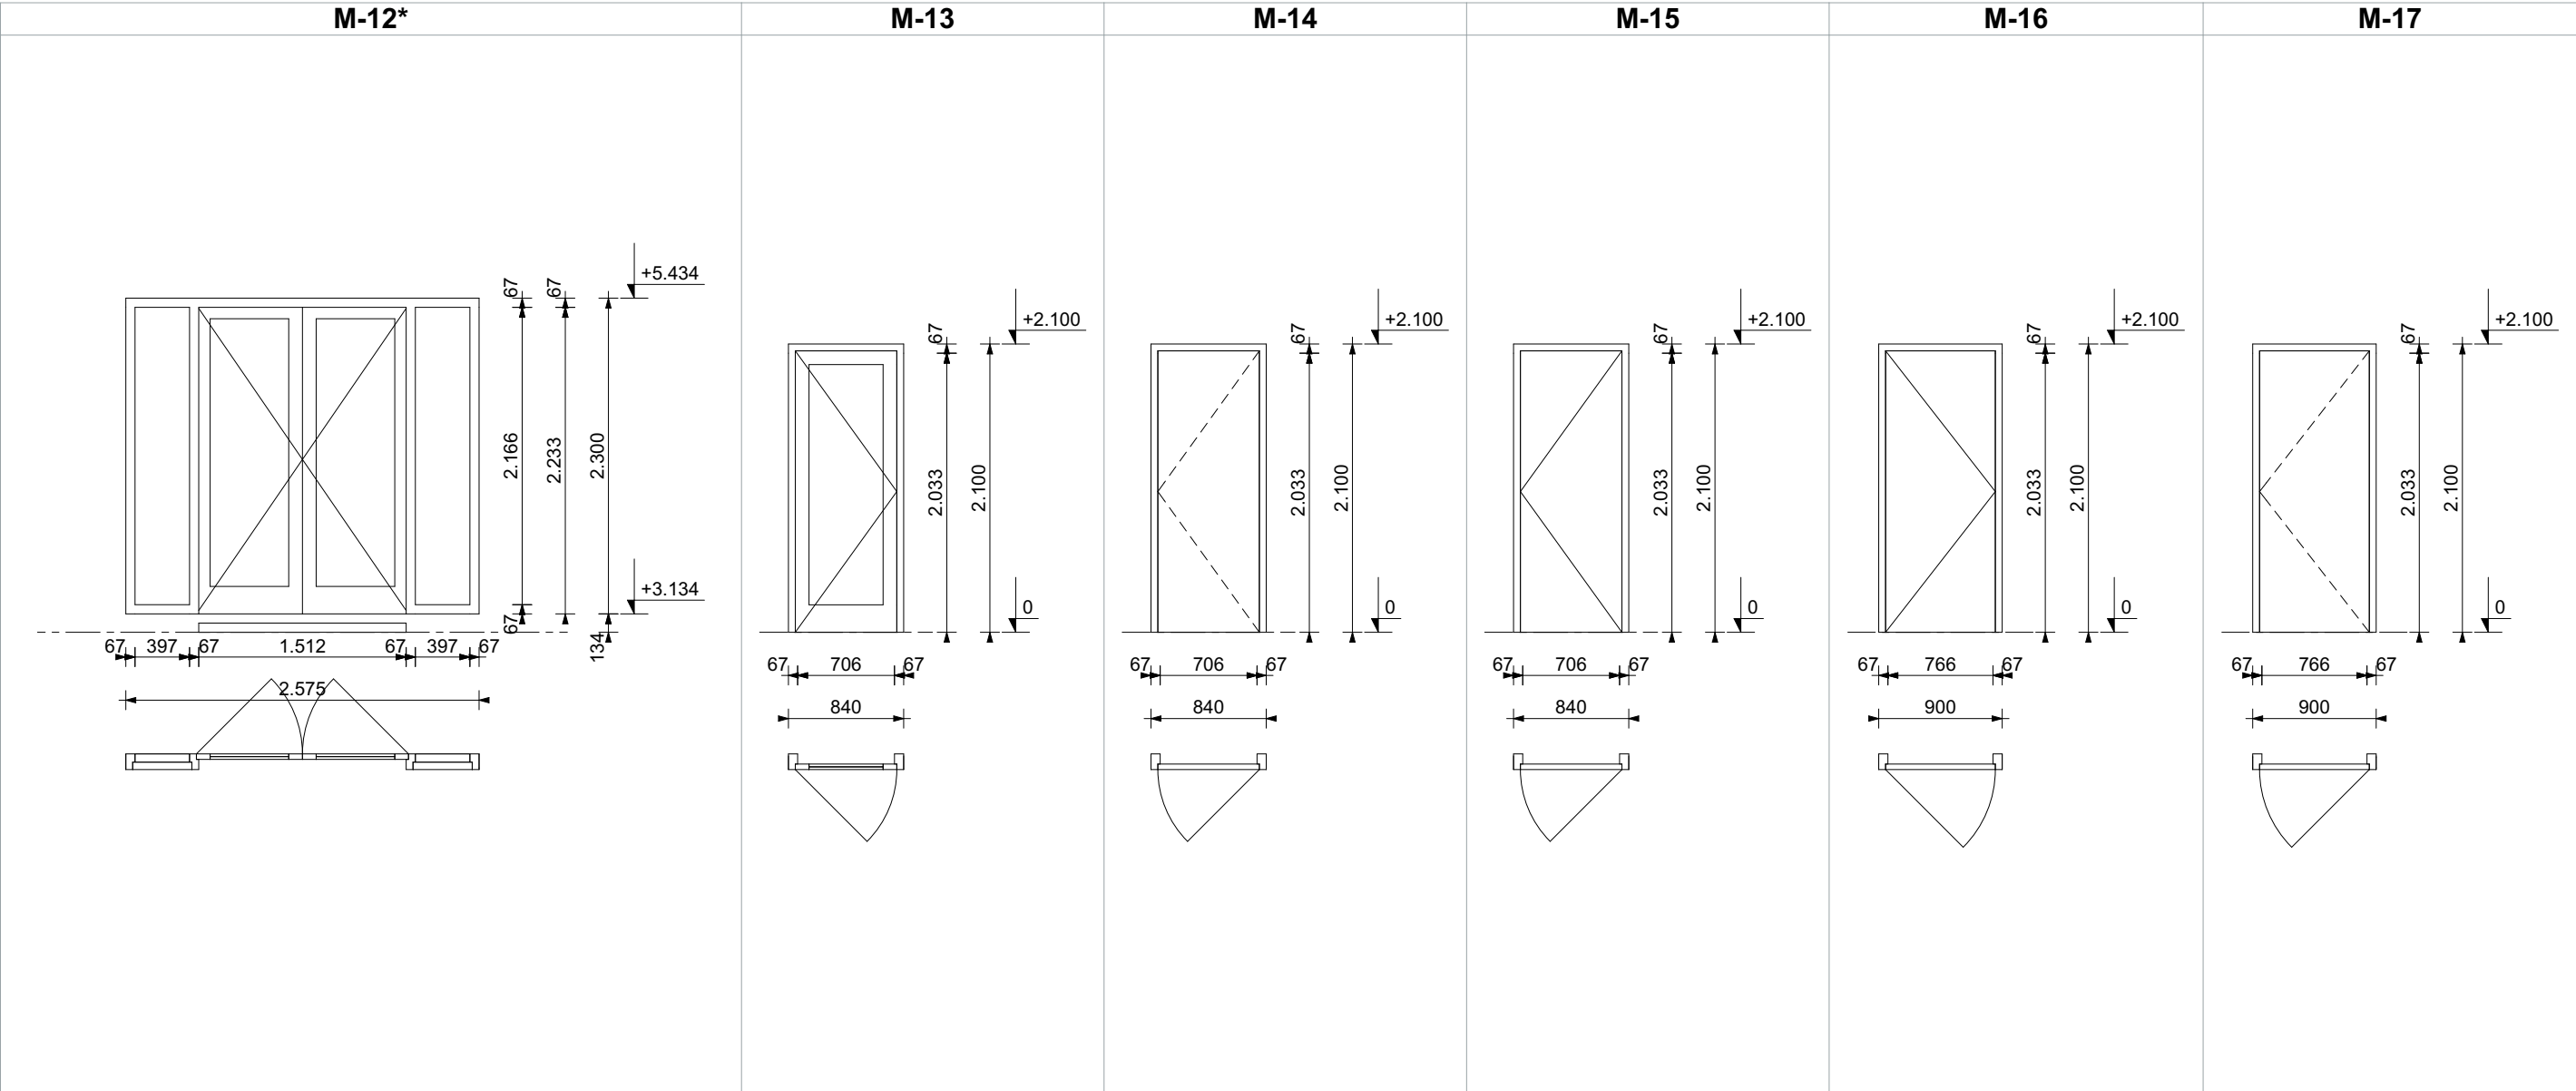

M-18	M-19	M-20	M-21	M-22	M-23	M-24
