


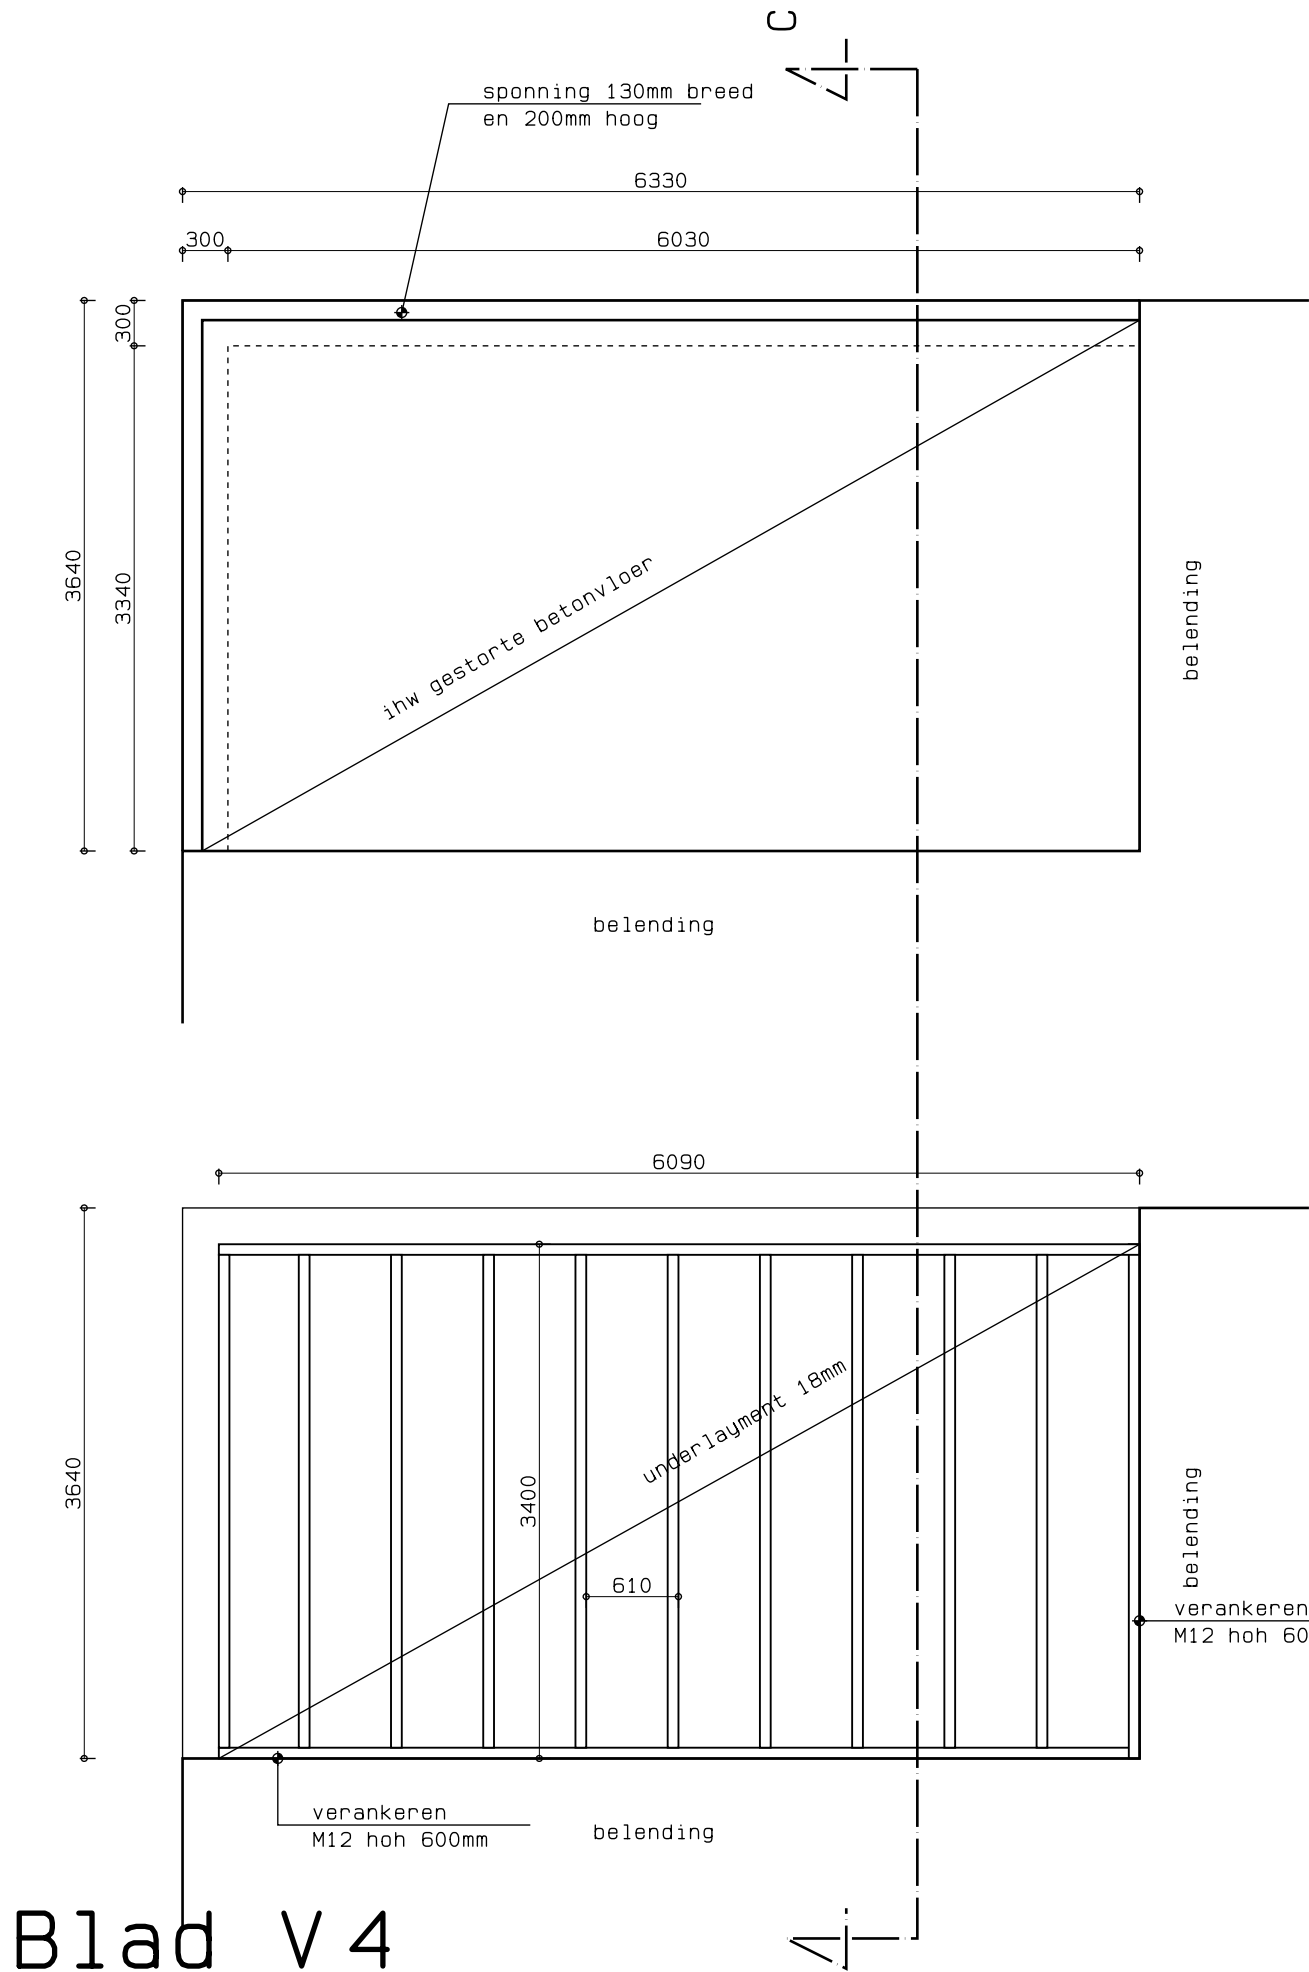


fundering

vloer met vorstrand
-vloer 150mm dik.
-vorstrand 200-300mm
wapening mat rond 8-150mm
vloerafwerking vinderen

dakconstructie

balklaag 71x171mm hoh 610mm C24
underlaymant 18mm

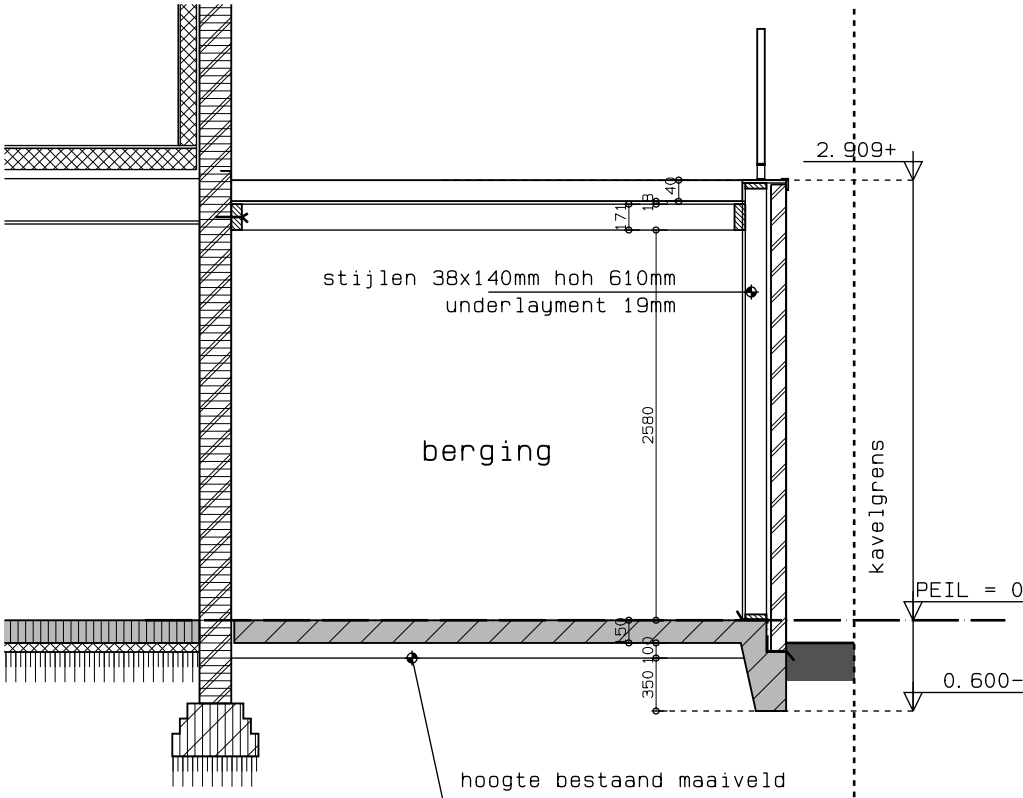

doorsnede C-C

berging