bestaande situatie

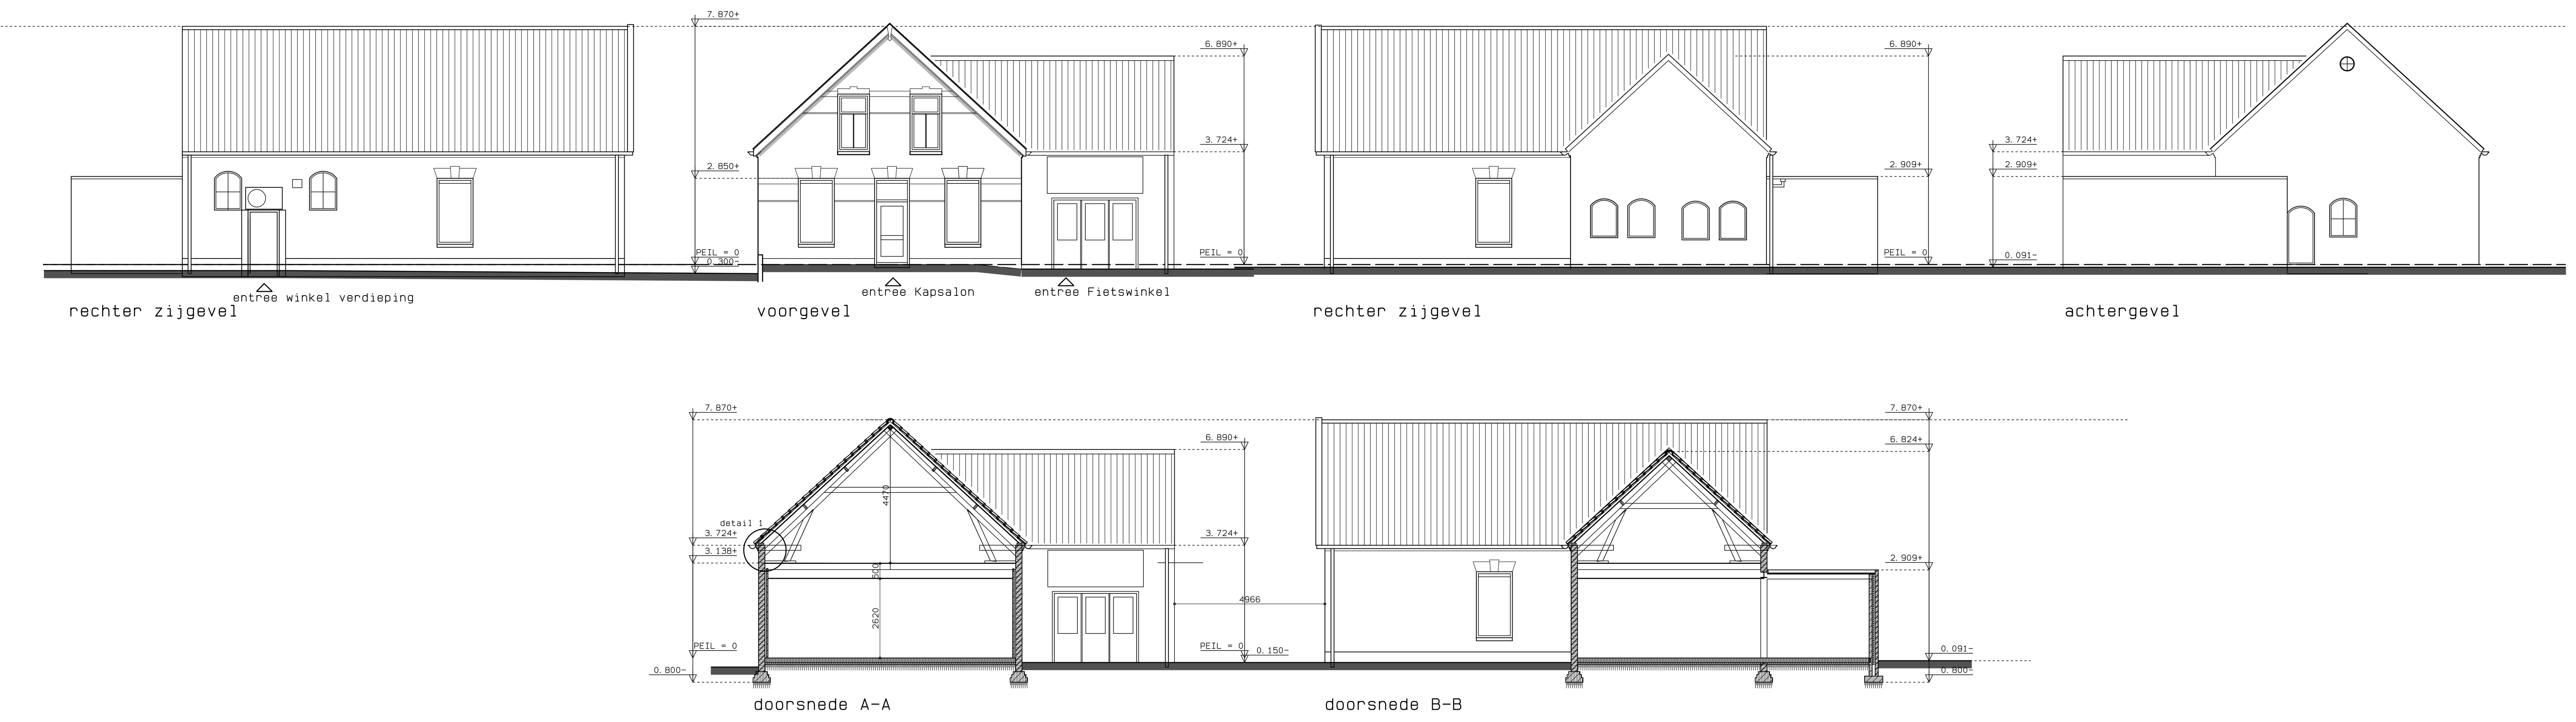

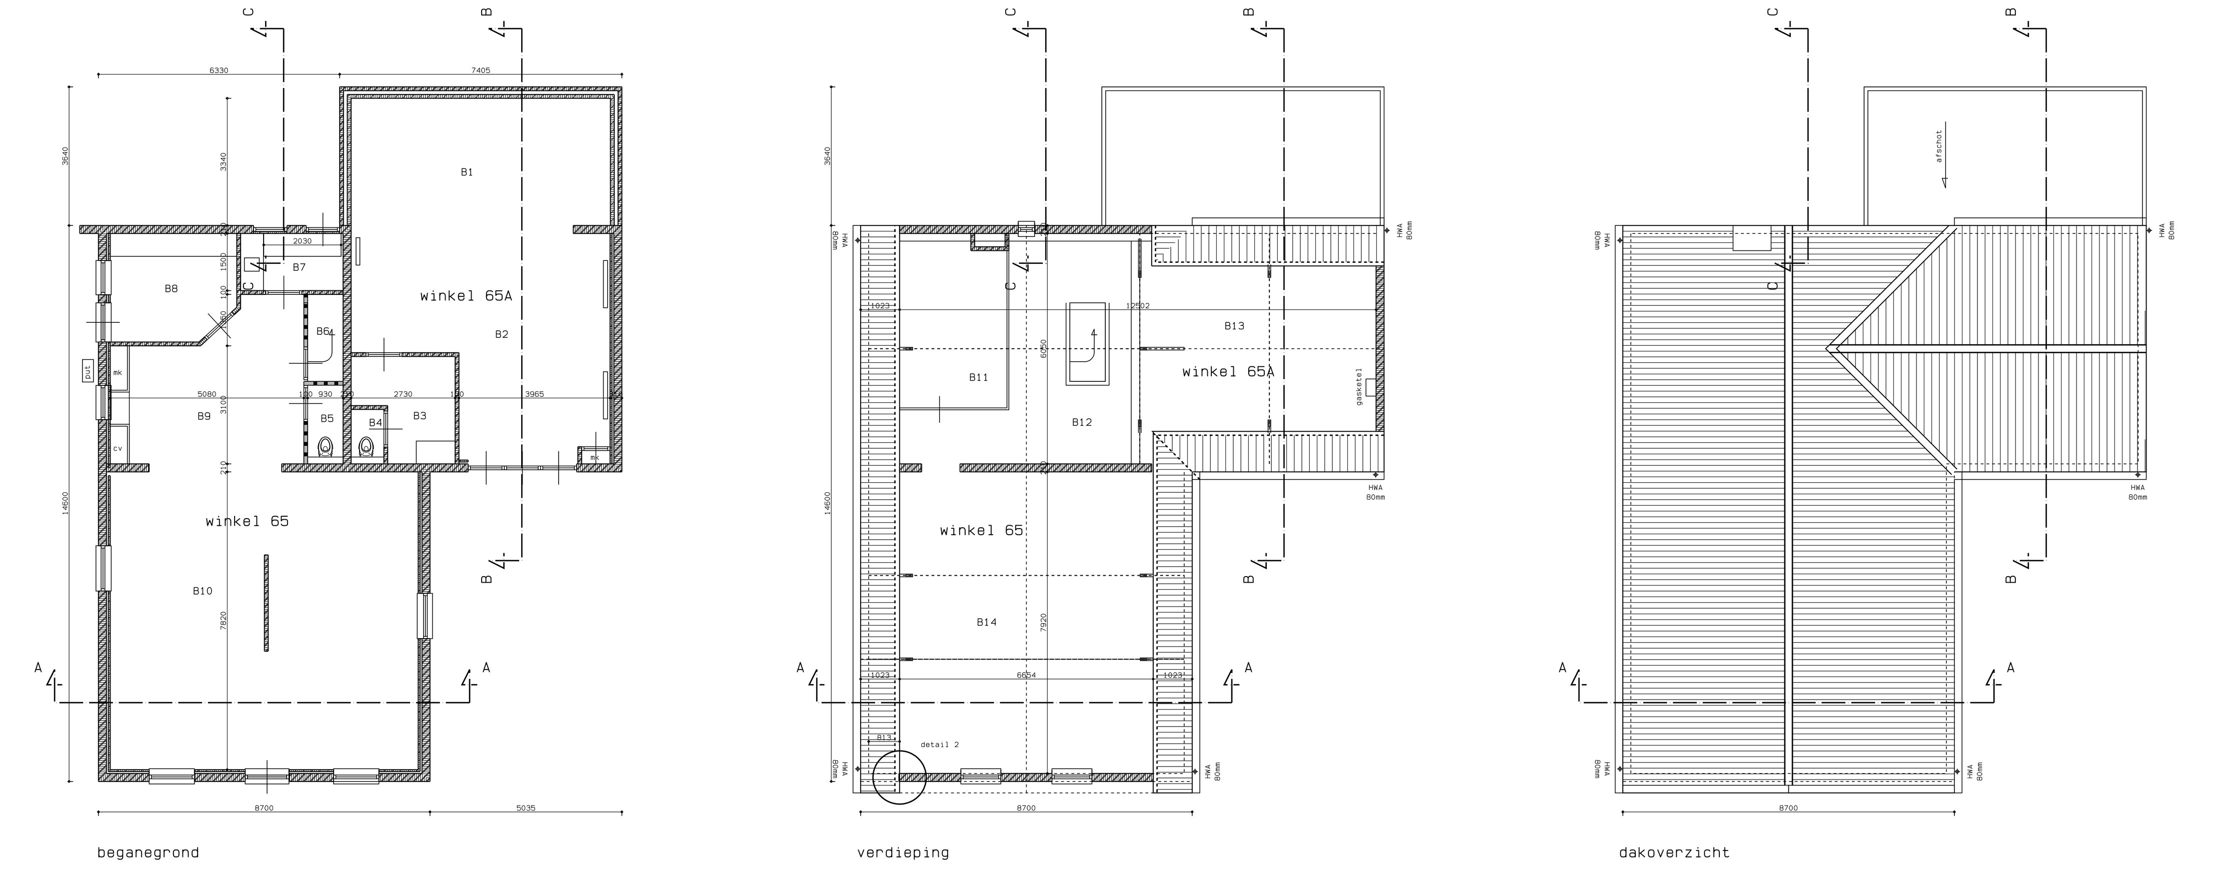

nieuwe situatie

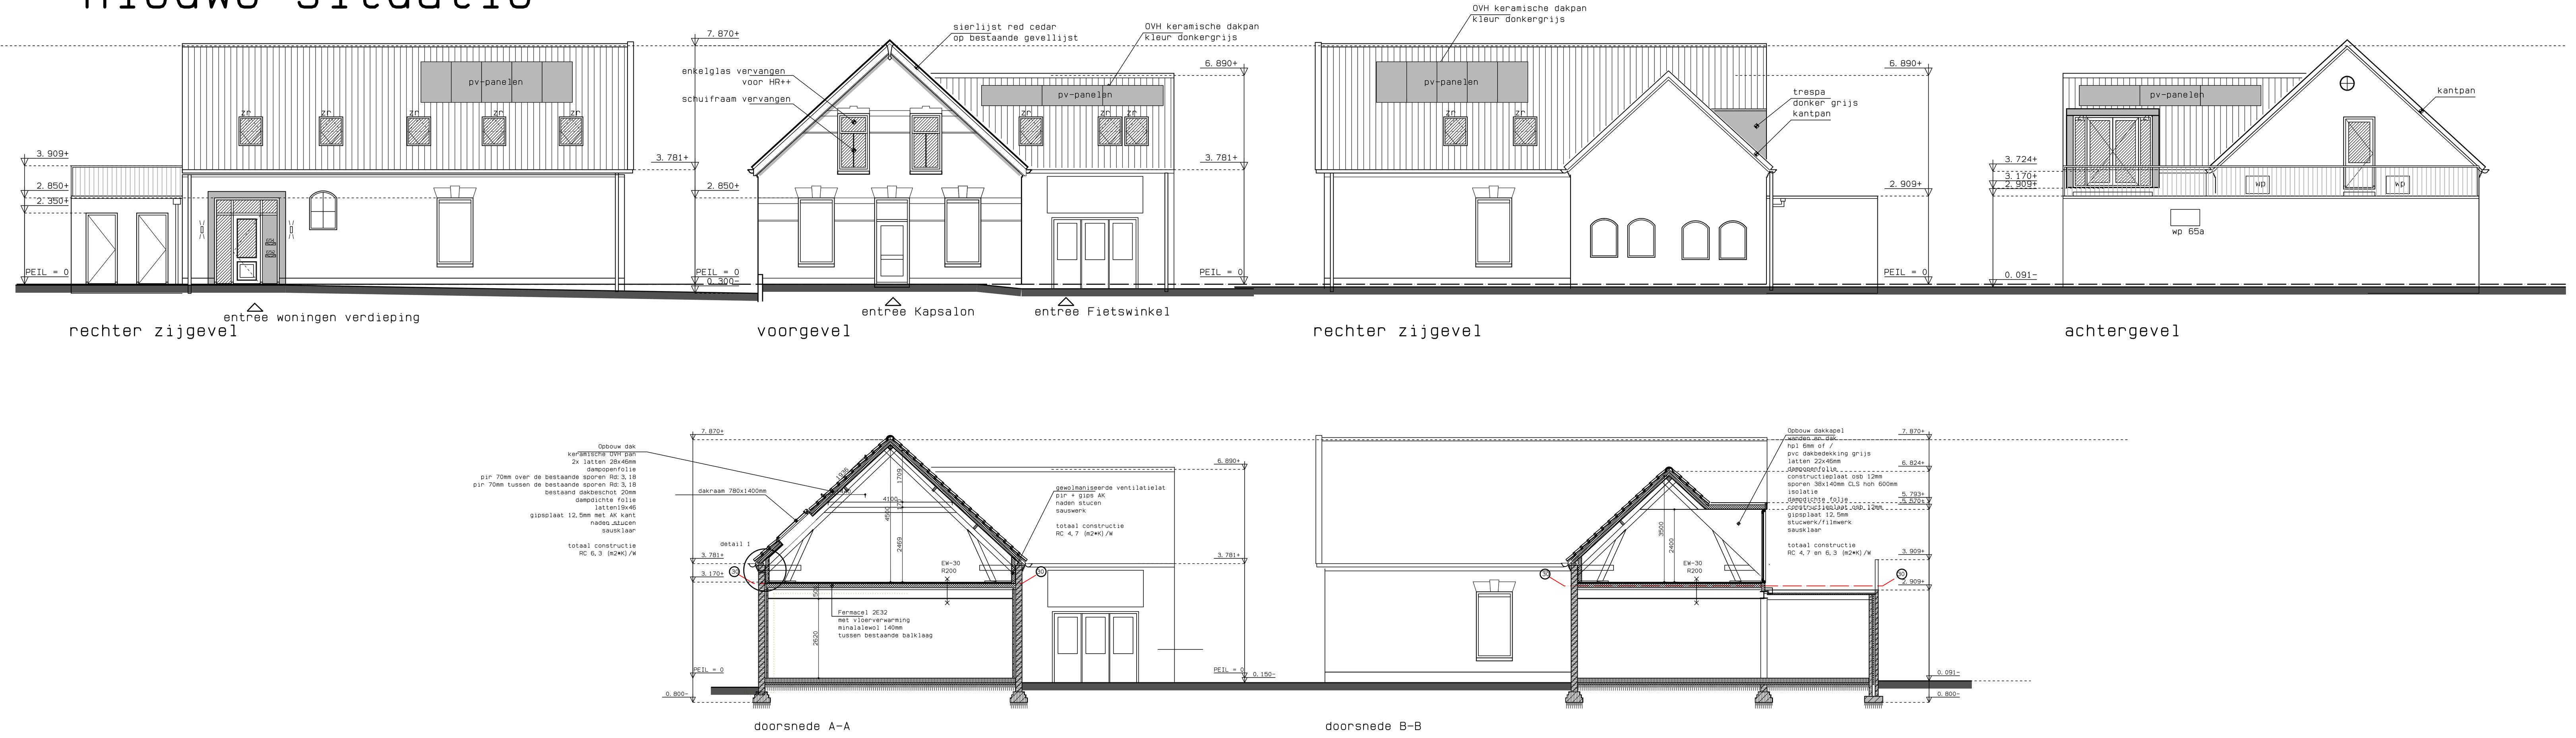

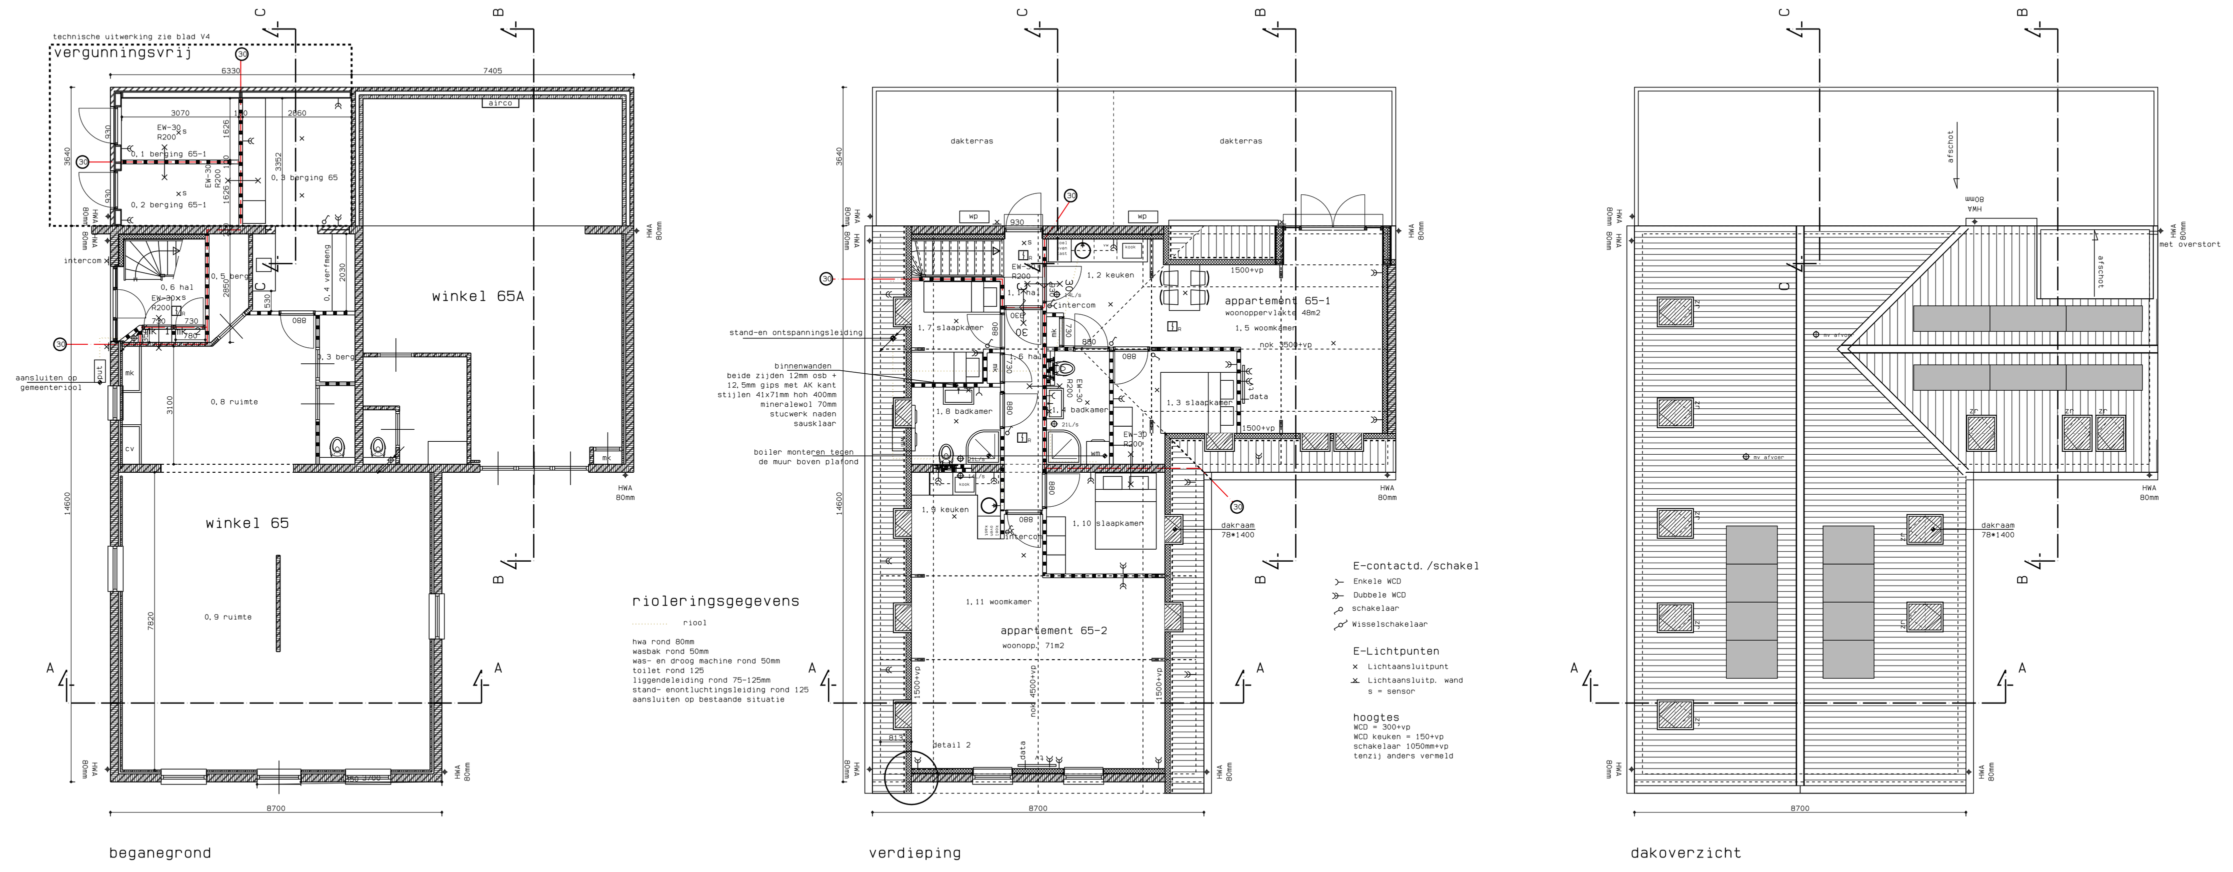

Renvooi eisen en bepalingen algemeen

-Brandwerendheid
Alle doorvoeringen in een brandscheiding moeten worden voorzien van een brandwerende voorziening en/of applicatie
Brandwerend afzuigventiel/brandklep = R-vent SC60+V. zie bijlage
Brandwerend wand 30 = GF_100_HT_1_75_1_A-Scheidingswanden. zie bijlage
Elke woning en vluchtweg is een brandcompartiment van 30min wbdbo

-Het binnen- en buitenoppervlak moeten voldoen aan de gestelde eisen voor de brandklasse D en rookklasse S2

-NUTS
aansluiting conform netwerkbeheerder

-Uitwendige scheidingsconstructies van verblijfsruimte, toiletruimte en badruimte moeten, volgens NEN 2778, waterdicht worden uitgevoerd

-30 minuten weerstand tegen branddoorslag en brandoverslag (WBDBO), conform de NEN 6068 of NEN-EN 13501-2.

-De brandwerendheid van doorvoeringen door brandwerende wanden of vloeren moeten gelijk zijn aan die van de desbetreffende wand of vloer e.e.a. conform de NEN 6069 of de NEN-EN 1366 - 3 + 4.
De brandwerendheid van de doorvoeringen moeten worden aangebracht door een daartoe gecertificeerd bedrijf.

-Deur, die in combinatie met het kozijn een brandwerendheid bezit van tenminste 30 minuten.

-Deur, die zelfsluitend is uitgevoerd in combinatie met het kozijn een brandwerendheid bezit van tenminste 30 minuten.

-Schachten, kokers of kanalen moeten aan de binnenzijde onbrandbaar zijn over een dikte van 0,01 m conform de NEN 6064.

-Het rookkanaal moet worden uitgevoerd conform de NEN 6062.

mv mechanische ventilatie. Voor capaciteit zie dakoverzicht
CV verwarmingstoestel
HWA hemelwaterafvoer

R optische rookmelder, aan elkaar gekoppeld, op lichtnet aangesloten, moet voldoen aan NEN 2555

Renvooi eisen en bepalingen algemeen

- Maatvoering in het werk controleren en bepalen
- Aannames moeten in het werk overeenkomen met tekening en/of constructieberekening. Bij een afwijkende situatie moet er contact opgenomen worden met betreffende adviseur.
- Definitieve constructieve gegevens uitvoeren volgens berekening en tekening constructeur
- Toegepast besluit particuliere opdrachtgeverschap
- Uitwerking constructie conform BBL met verzoek berekeningen op te nemen in de nadere eisen en voorwaarden van de omgevingsvergunning
- Buitenwanden Rc=4.7 m2K/W
- Schuindak Rc=6.3 m2K/W
- Platdak Rc=6.3 m2K/W
- Beglazing: HR++, U=1.2 W/m□.K, ZTA 0,60.
- Kozijn incl. glas U=variabel min. 1,65 W/m2
- Ventilatie, luchtverversing, rookgasafvoer en luchttoevoer conform NEN 1087 en het Bouwbesluit
- Ventilatietoevoer badruimte, toiletruimte, meterkast, bergruimte, wasruimte, verkeersruimte middels kier van 20mm onder deur
- Ventilatievoorzieningen; natuurlijke toevoer en mechanische afzuiging. Uitvoering conform installateur
- De vuilwater- en schoonwaterriolering worden op het gemeente riool aangesloten.
- verwarming: vloerverwarming met warmtepomp
- Warmwater / boiler met warmtepomp
- Luchtverversing installaties
- volgens tekeningen installateur, moet voldoen aan NEN 1087
  afzuiging toilet 7 l/s
  afzuiging keuken 21 l/s
  badkamer 14 l/s
- Luchtverversing als bestaand, nieuwe opp conform BB afd.3.10
- Constructie 30min wbdbo
- Uitgaand van het 'rechtens verkregen niveau' zowel voor:
  - Wering van buitengeluid, lucht- en contactgeluid als installatiegeluid.
  - Daglicht
  - Luchtverversing, ventilatie en doorspuibaarheid

Renvooi eisen en bepalingen algemeen

- Bereikbare kozijnen/gevelelementen/hang-en sluitwerk conform Politiekeurmerk klasse 3.
- Equivalente daglichtopppervlakte conform NEN 2057= min. 10% van het V.G.
  Alle verblijfsruimtes voldoen aan minimaal 0,5 m2 E.D.
- Elektra installatie conform NEN 1010 en het Bouwbesluit
- Binnenriolering conform NEN 3215 en NPR 3216 en het Bouwbesluit
- Riolering in het hele plan uitvoeren volgens gescheiden stelsel
- Gasinstallatie conform NEN 1078 en het Bouwbesluit
- Waterinstallatie conform NEN 1006 en het Bouwbesluit
- Invoerhoogte en diameter t.b.v. invoer elektra, gas, water, volgens opgave nutsbedrijven.
- Hoofddraagconstructie 30 min. brandwerend.
- Elke woning is een brandcompartiment 30 min. brandwerend.
- Houten trap conform Bouwbesluit:
  Voor optrede en aantrede wordt uitgegaan van het rechtens verkregen niveau. Niet beweegbare afscheiding trap conform bouwbesluit
- Bovenkant hekwerken minimaal 1000 mm boven loopvlak
- Dagmaat loopdeuren, minimaal 850 mm en 2300 mm hoog
- Karakteristiek geluidniveau max. 30 dB van toilet, kraan, mv en installatie voor warmte- of koudeopwekking conform NEN 5077 en het Bouwbesluit
- Karakteristiek geluidniveau max. 40 dB van installatie voor warmte- of koudeopwekking conform NEN 5077 en Bouwbesluit
- Tegelhoogte badruimte tot plafond. Toilet tot min. 1200+ vl.
- Badruimten en toiletruimten worden voorzien van tegelvloer.
- Een uitwendige scheidingsconstructie heeft geen openingen groter dan 0,01 m (ter voorkoming van binnendringen van ratten en muizen)

materiaalspecificatie

materialen en kleuren:

gevels:	metselwerk	rood/bruin (als bestaand)
	voegwerk	grijs (als bestaand)
gevellijst	red cedar	creme (als bestaand)
deklijst	hout met zink	grijs
pannen:	keramisch	donkergrijs
kozijn:	hardhout	creme (als bestaand)
HWA/goot:	zink	grijs

Renvooi

- baksteen, bestaand
- kalkzandsteen
- verdicht zandpakket, bestaand
- gewapend beton, bestaand
- HSB-wand
- lichte scheidingswand metalstud
  Gyproc GF 100 HT/1.75.1.A
  beidezijden 12,5mm gips
  mineralewol 60mm
  totaal 100mm

Brand- en rookklasse

Constructie-onderdeel	Brandklasse vlgs NEN-EN-13501-1	Rookklasse in m-1 vlgs NEN-EN-13501-1
Beloopbaar vlak		
Andere ruimten	Dfl	S1fl
(Extra) beschermde vluchtroute	Cfl	S1fl
Overige constructie-onderdelen binnen		
(Extra) beschermde vluchtroute	B	S2
Andere ruimten	D	S2
Overige constructie-onderdelen buiten		
(Extra) beschermde vluchtroute	C	
Andere ruimten	D	

Renvooi

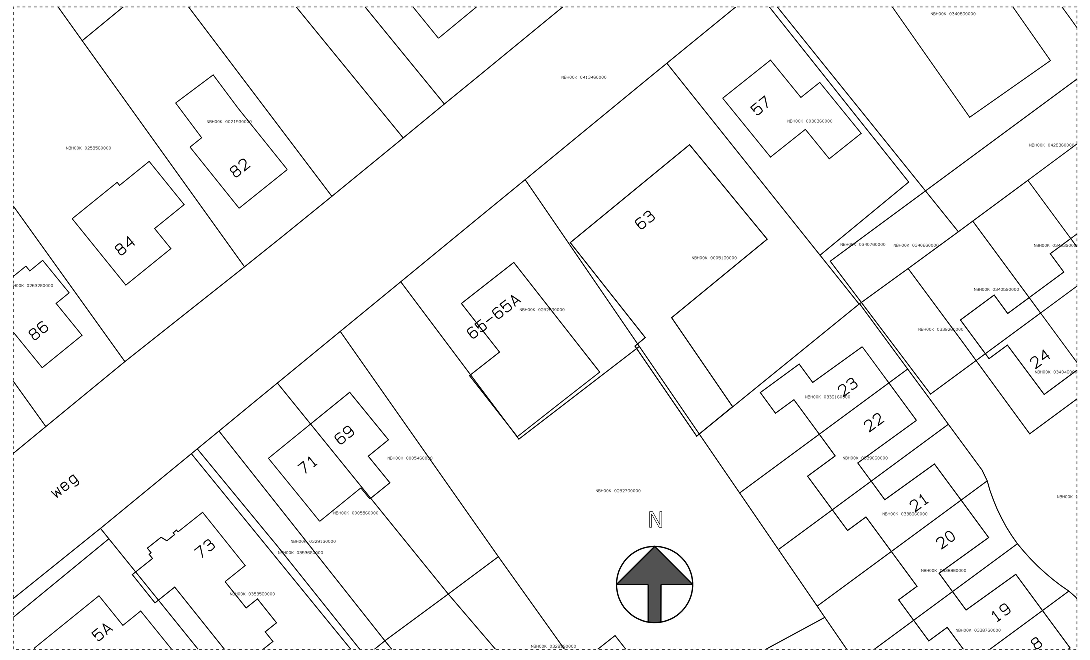

Kadastrale gegevens:
Gemeente Nijmegen
Sectie K
Perceel 2528
Schaal 1:500

Veranderen aanbouw

Bestaande aanbouw buiten het bouwvlak wordt veranderd.
Uitbreiding past binnen de 50% regel en is totaal niet meer dan 50m2.
De bestaande hoogte blijft gehandhaafd op 3 meter.
De berging is geheel vergunningsvrij.

parkeren

Gebruik wordt gemaakt van beleidsregel 2 van beleidsregels parkeren 2025 oftewel salderen.
Winkelfunctie op de 1e verdieping wordt veranderd in 2 appartementen, daarom zijn er verder geen parkeerplaatsen ingetekend op de situatie tekening.

HZBOUWADVIES

Twee appartementen St.Agnetenweg 65 Nijmegen
Dhr. H.J. Zaaijer
Batouwse Singel 11
4033KP Lienden

ING H.J. Zaaijer
Batouwse Singel 11
4033 KP Lienden
info@hzbouwadvies.nl
www.hzbouwadvies.nl

omgevingsvergunning
gevel plattegronden
doorsenden detaillering

Blad V1

get.	gew. HZ	a.	
schaal	1:100	b.	
form.	A0	c.	
dat.	22-01-'26	d.	
		e.	
		f.	

NI-328

Op al onze particuliere opdrachten is de 'Rechtsverhouding consument - architect' de CR 2013 van toepassing.
Voor de niet particulier is de 'Rechtsverhouding opdrachtgever-architect, ingenieur en adviseur DNR 2011' van toepassing

copyright HZbouwadvies