


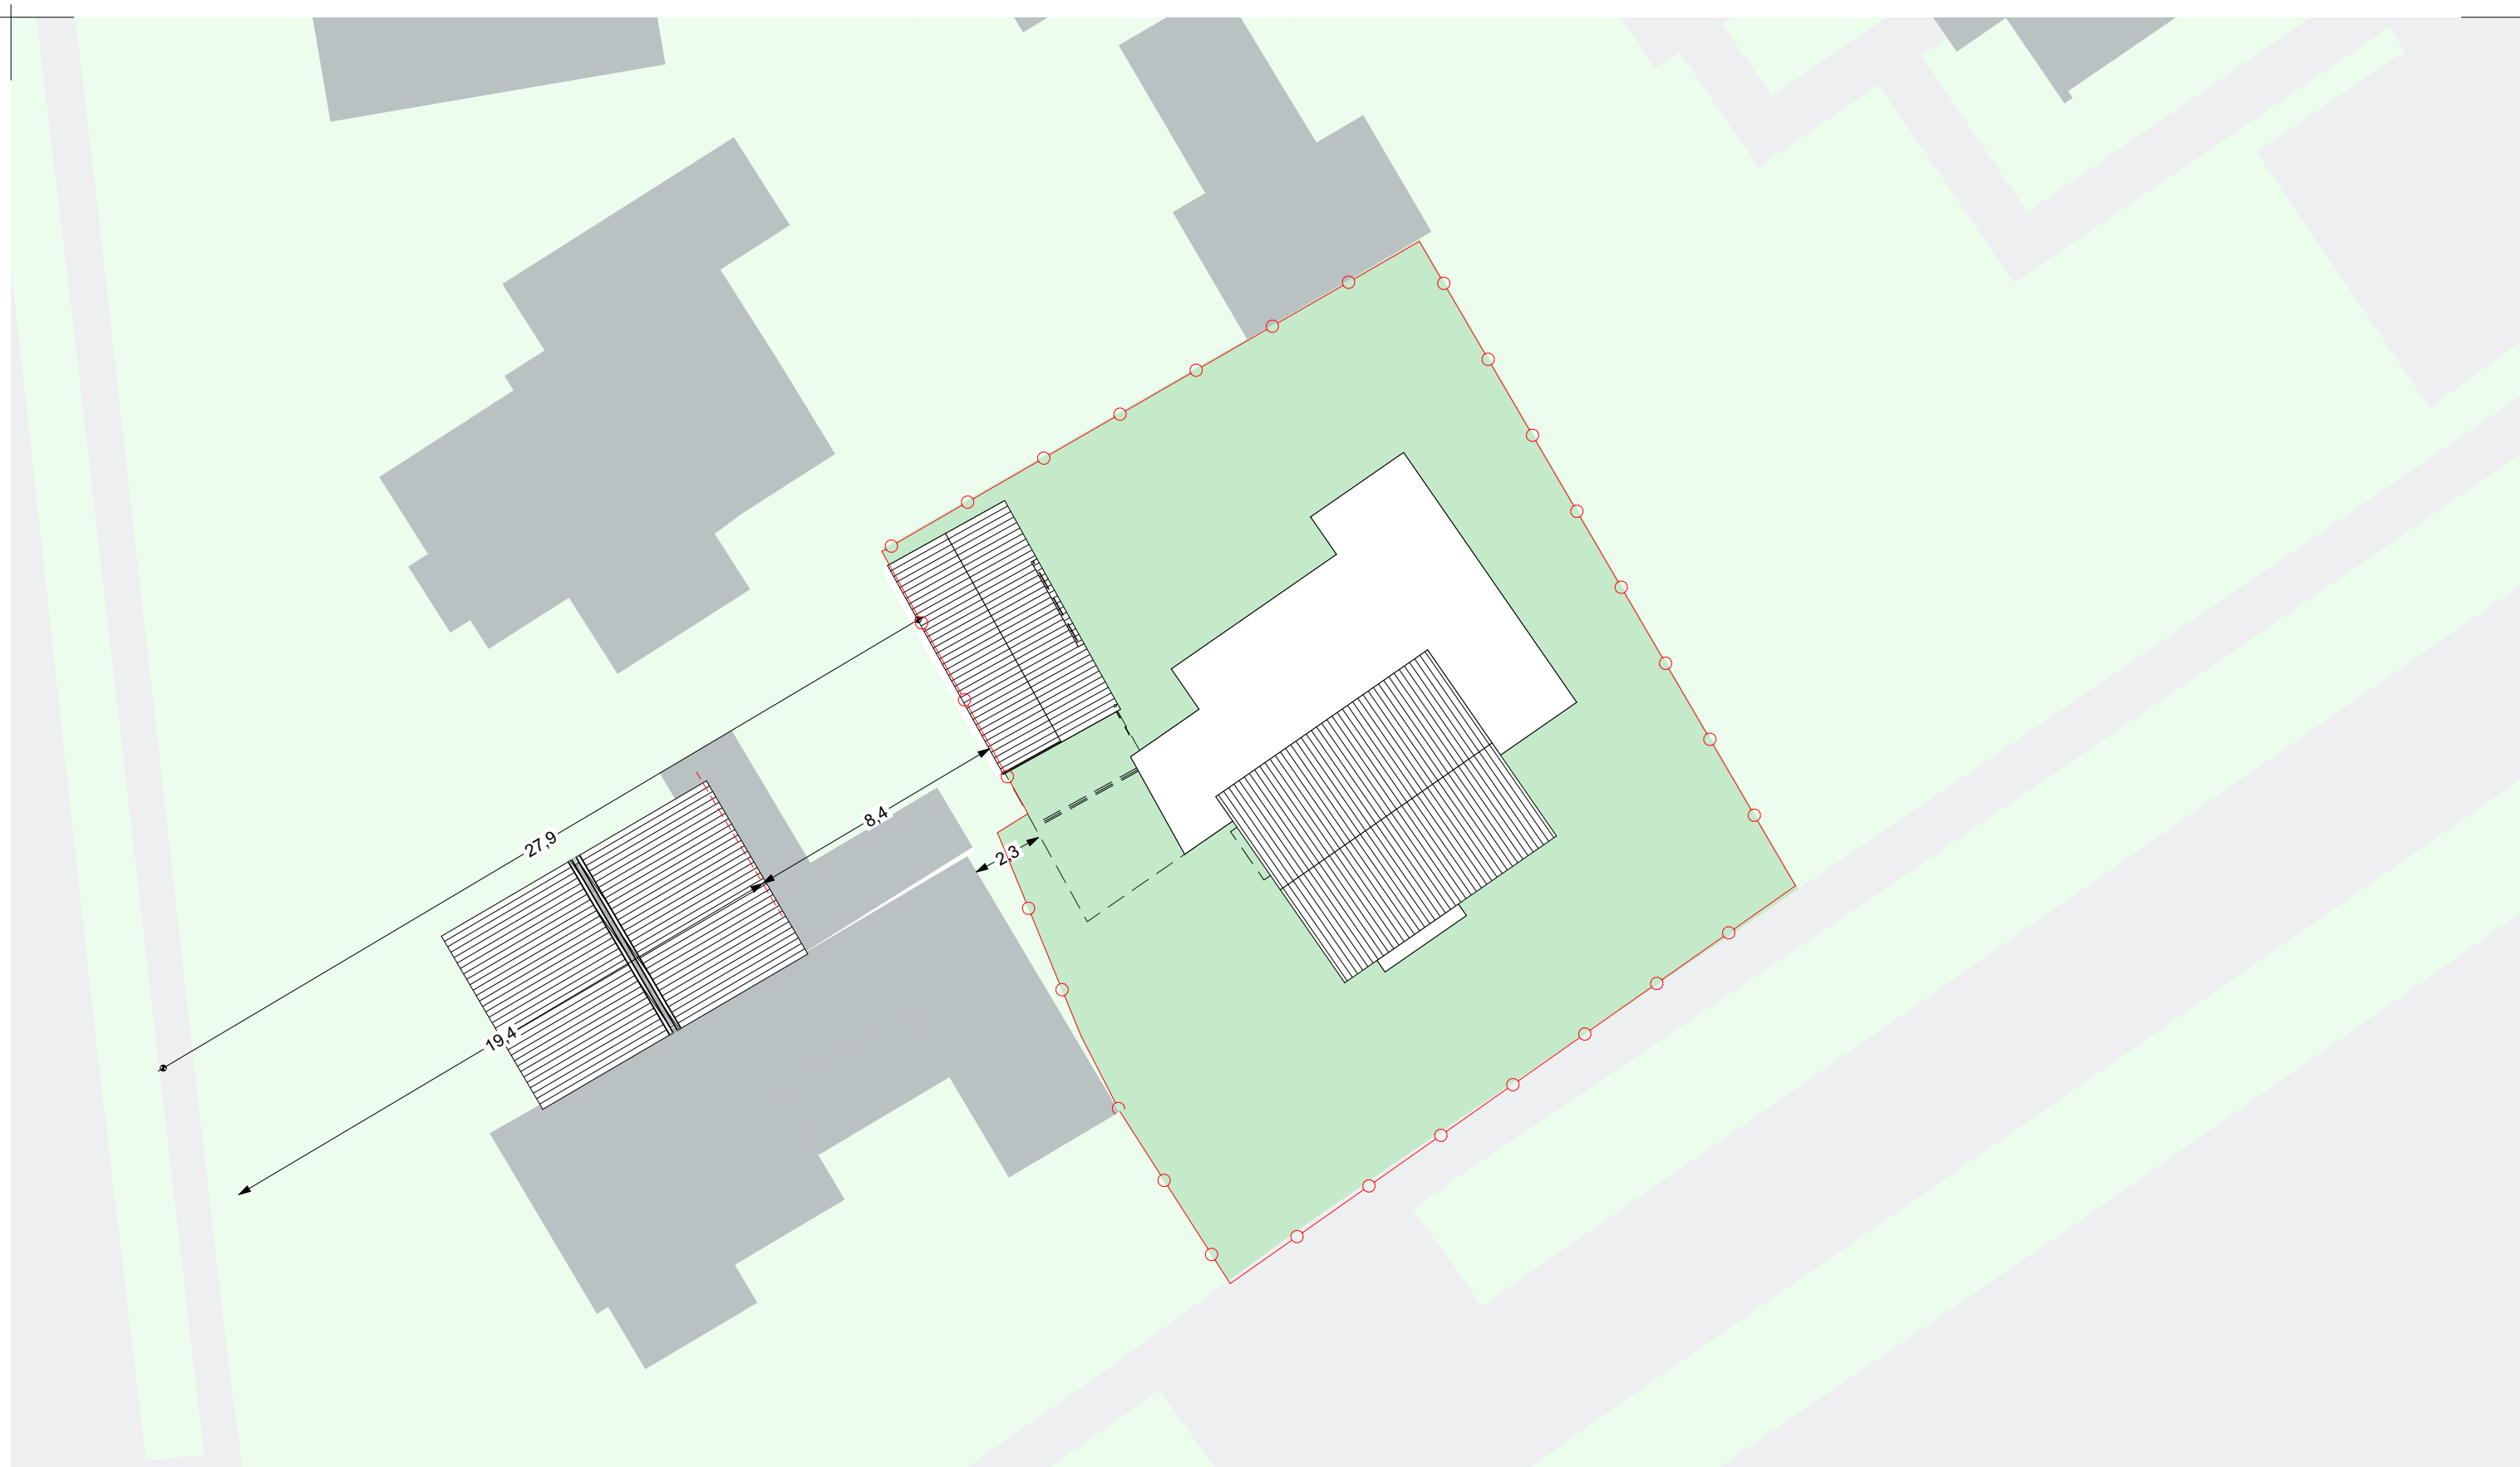


1323 DO 02.01 situatie bestaand versie 260519
schaal 1:200
Sint Willibrordusstraat 14
www.valkarchitecten.nl

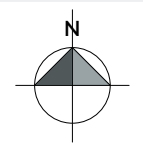

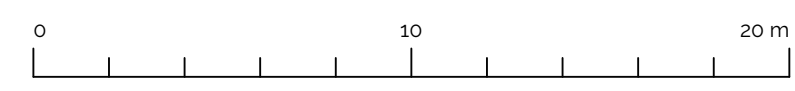

1323 DO 02.02 situatie nieuw versie 260519
schaal 1:200
Sint Willibrordusstraat 14
www.valkarchitecten.nl


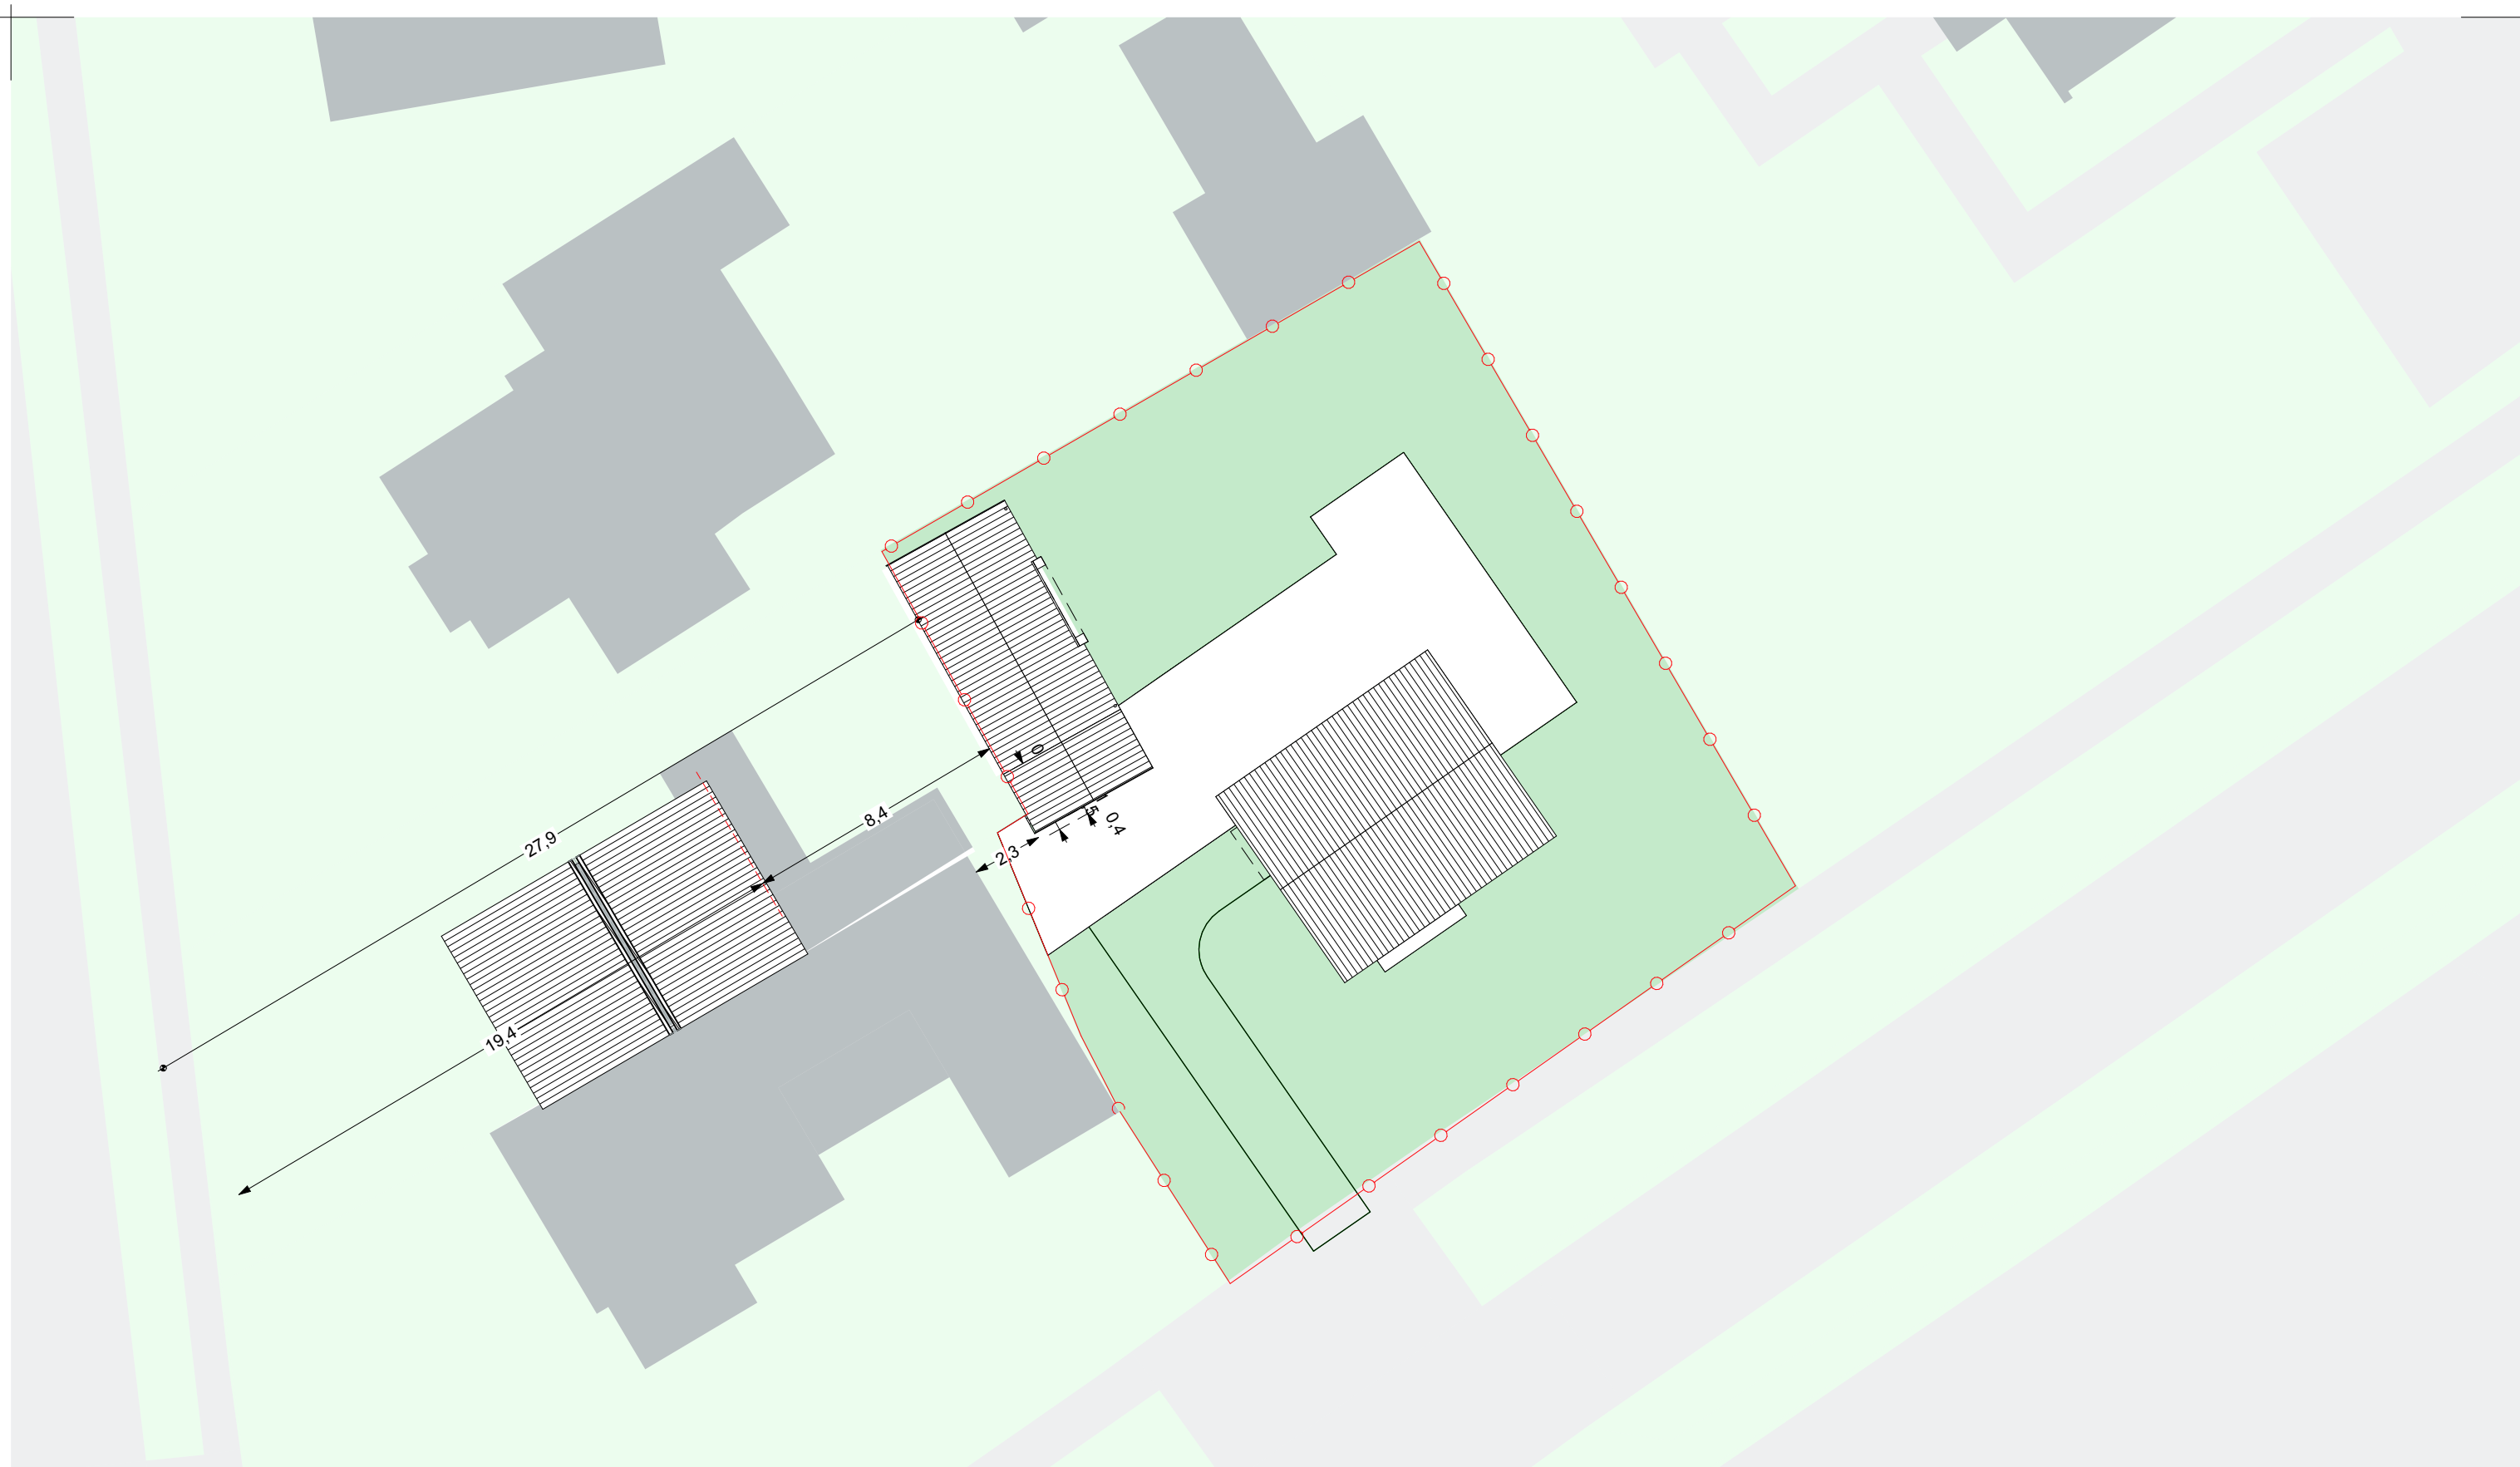




B ▼

▲ A


▼ B

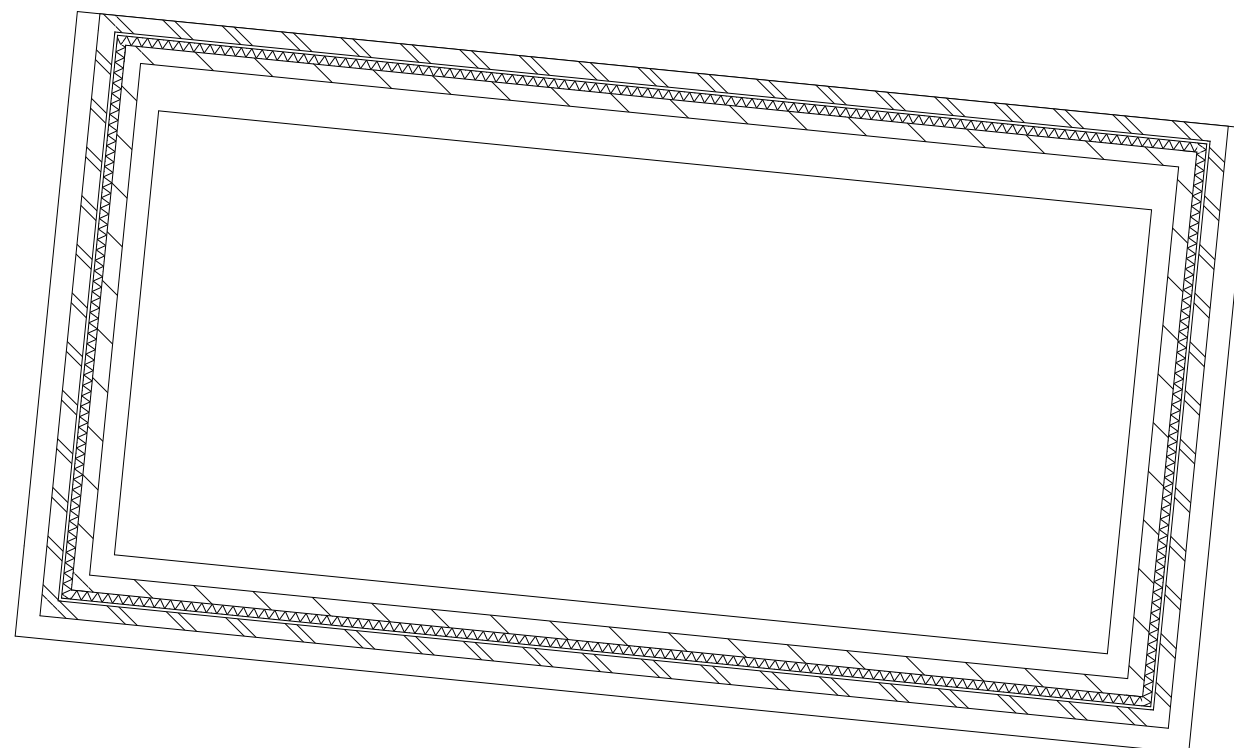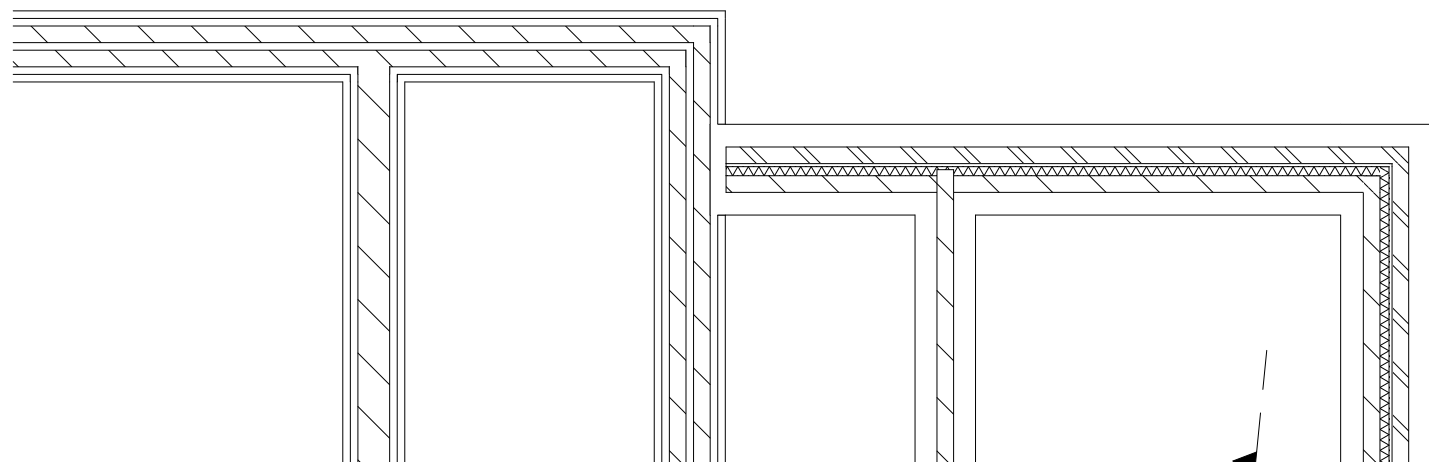

Alle maatvoering in het werk controleren

1323 DO 03.01 fundering bestaand versie 260519
schaal 1:50
Sint Willibrordusstraat 14
www.valkarchitecten.nl



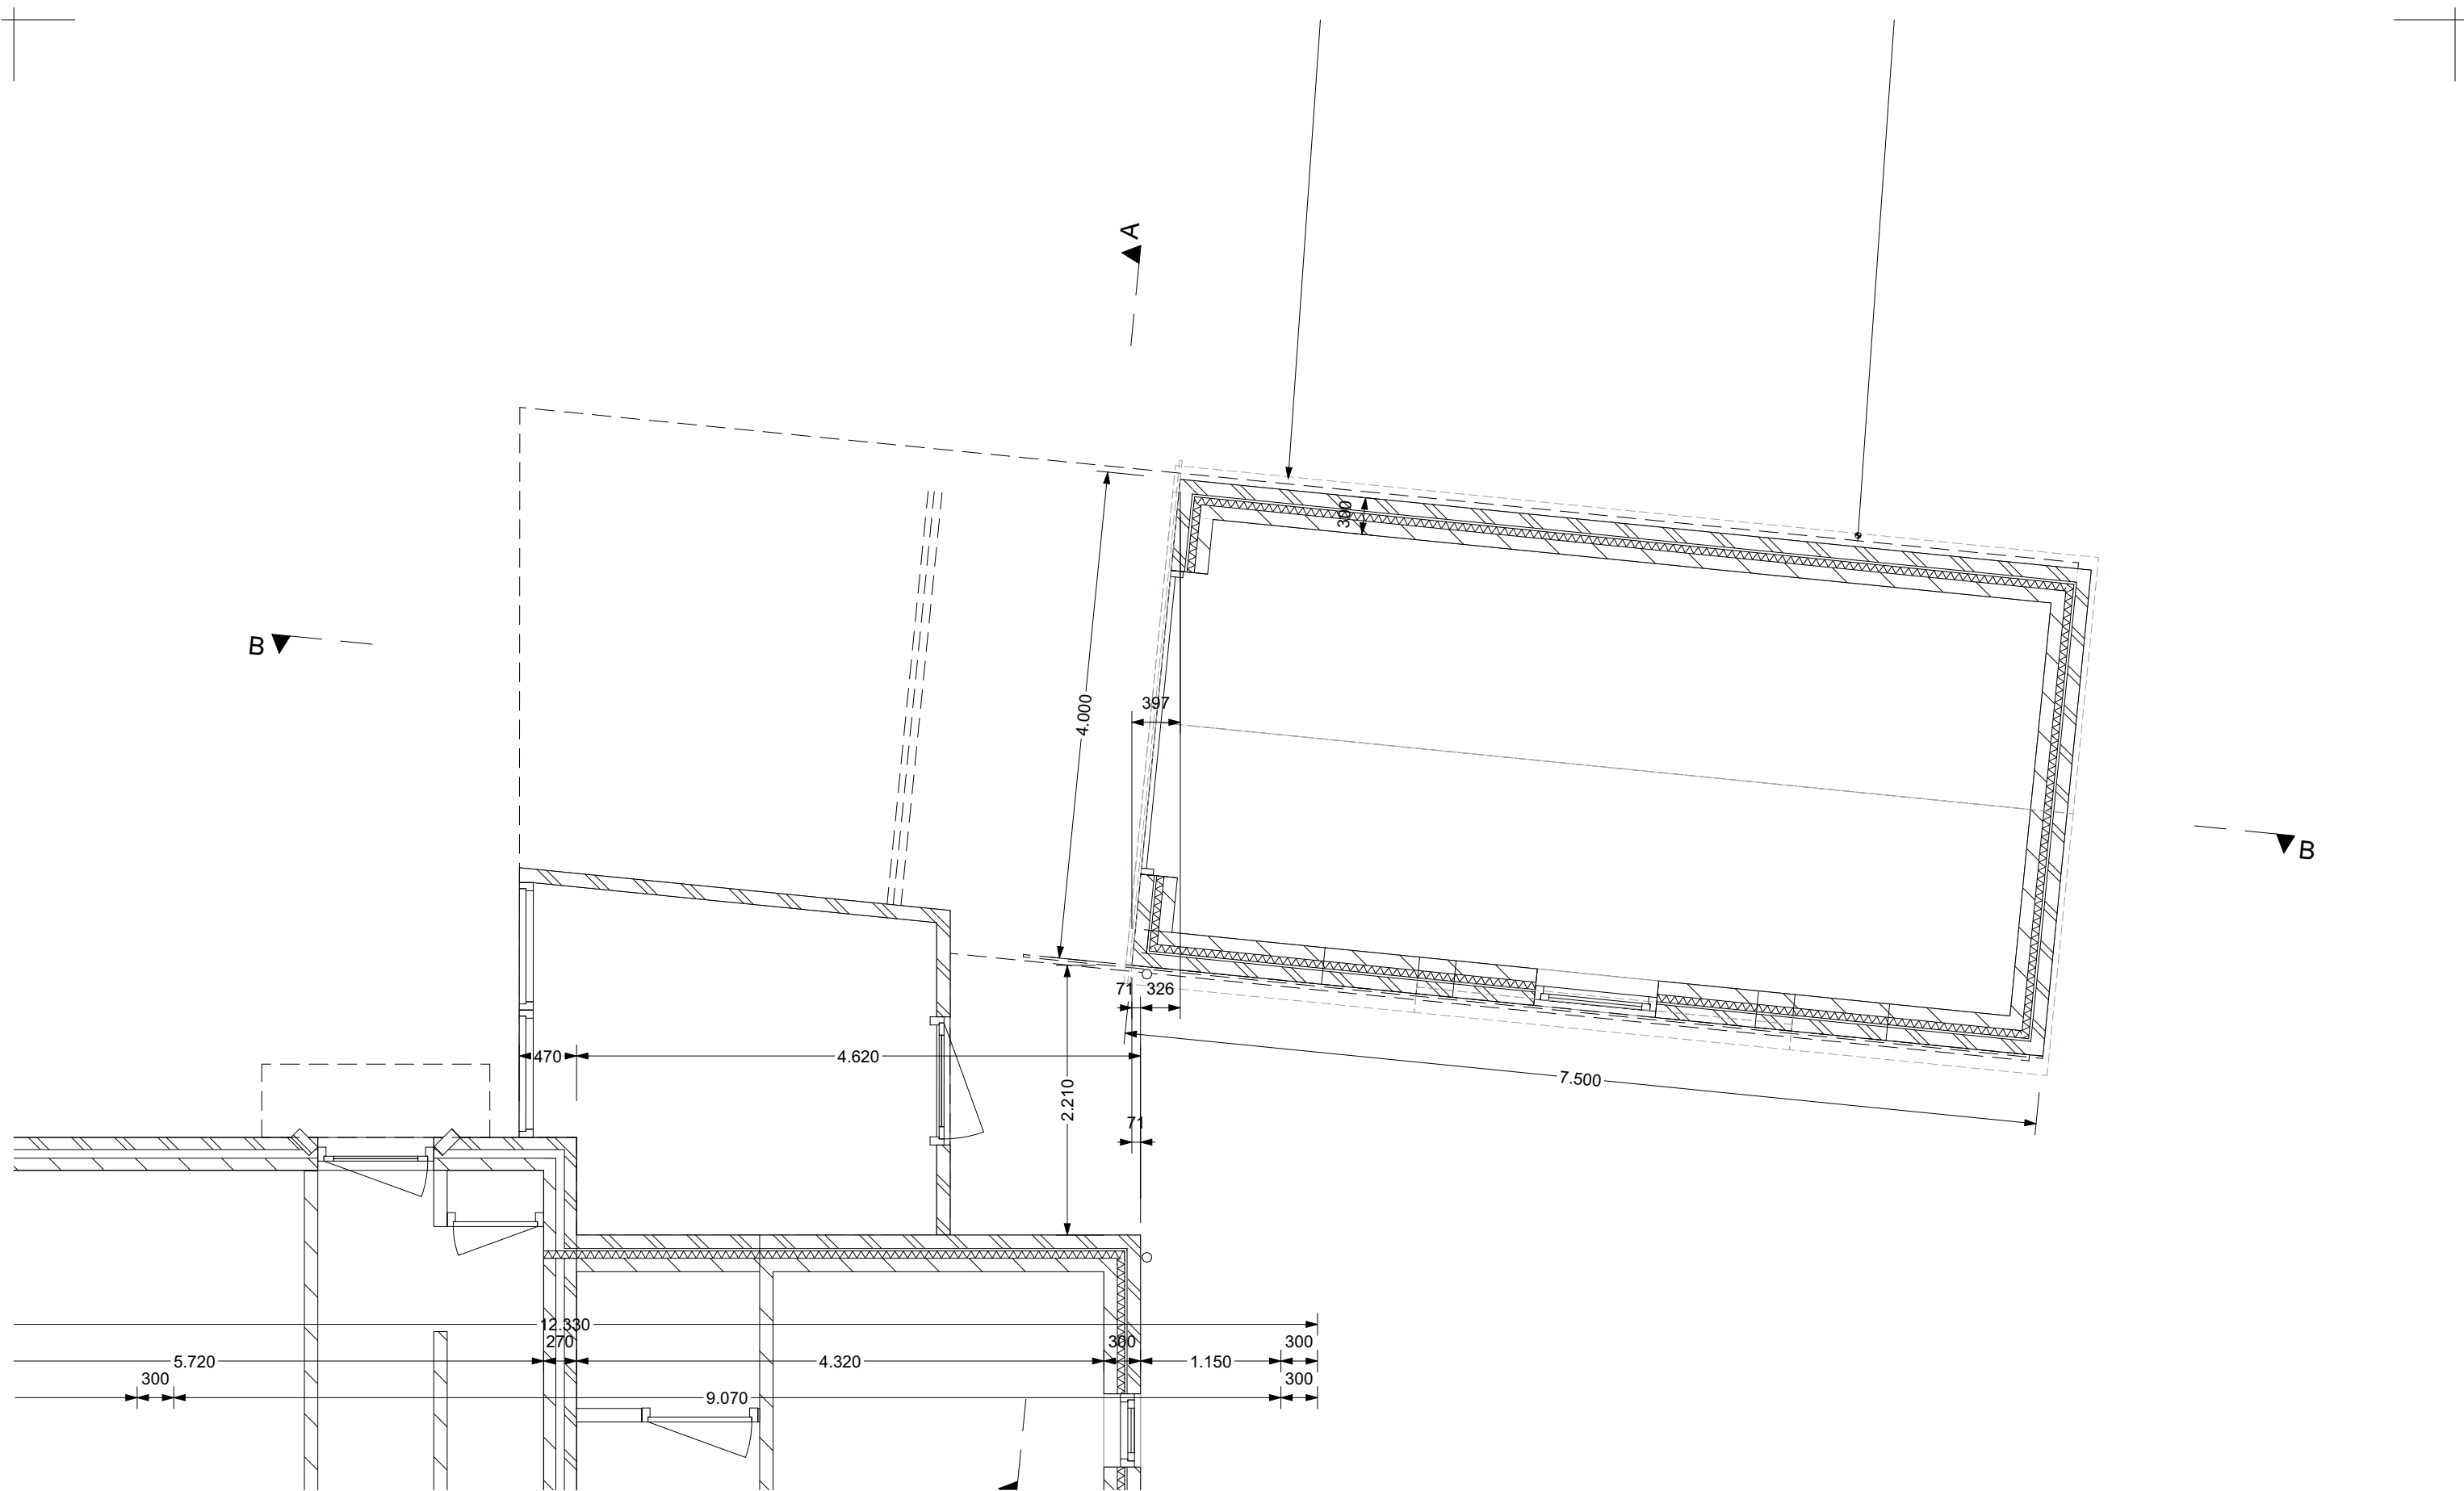

Alle maatvoering in het werk controleren


1323 DO 03.02 begane grond bestaand versie 260519
 schaal 1:50
 Sint Willibrordusstraat 14
 www.valkarchitecten.nl





B ▼


▲ A

▼ B

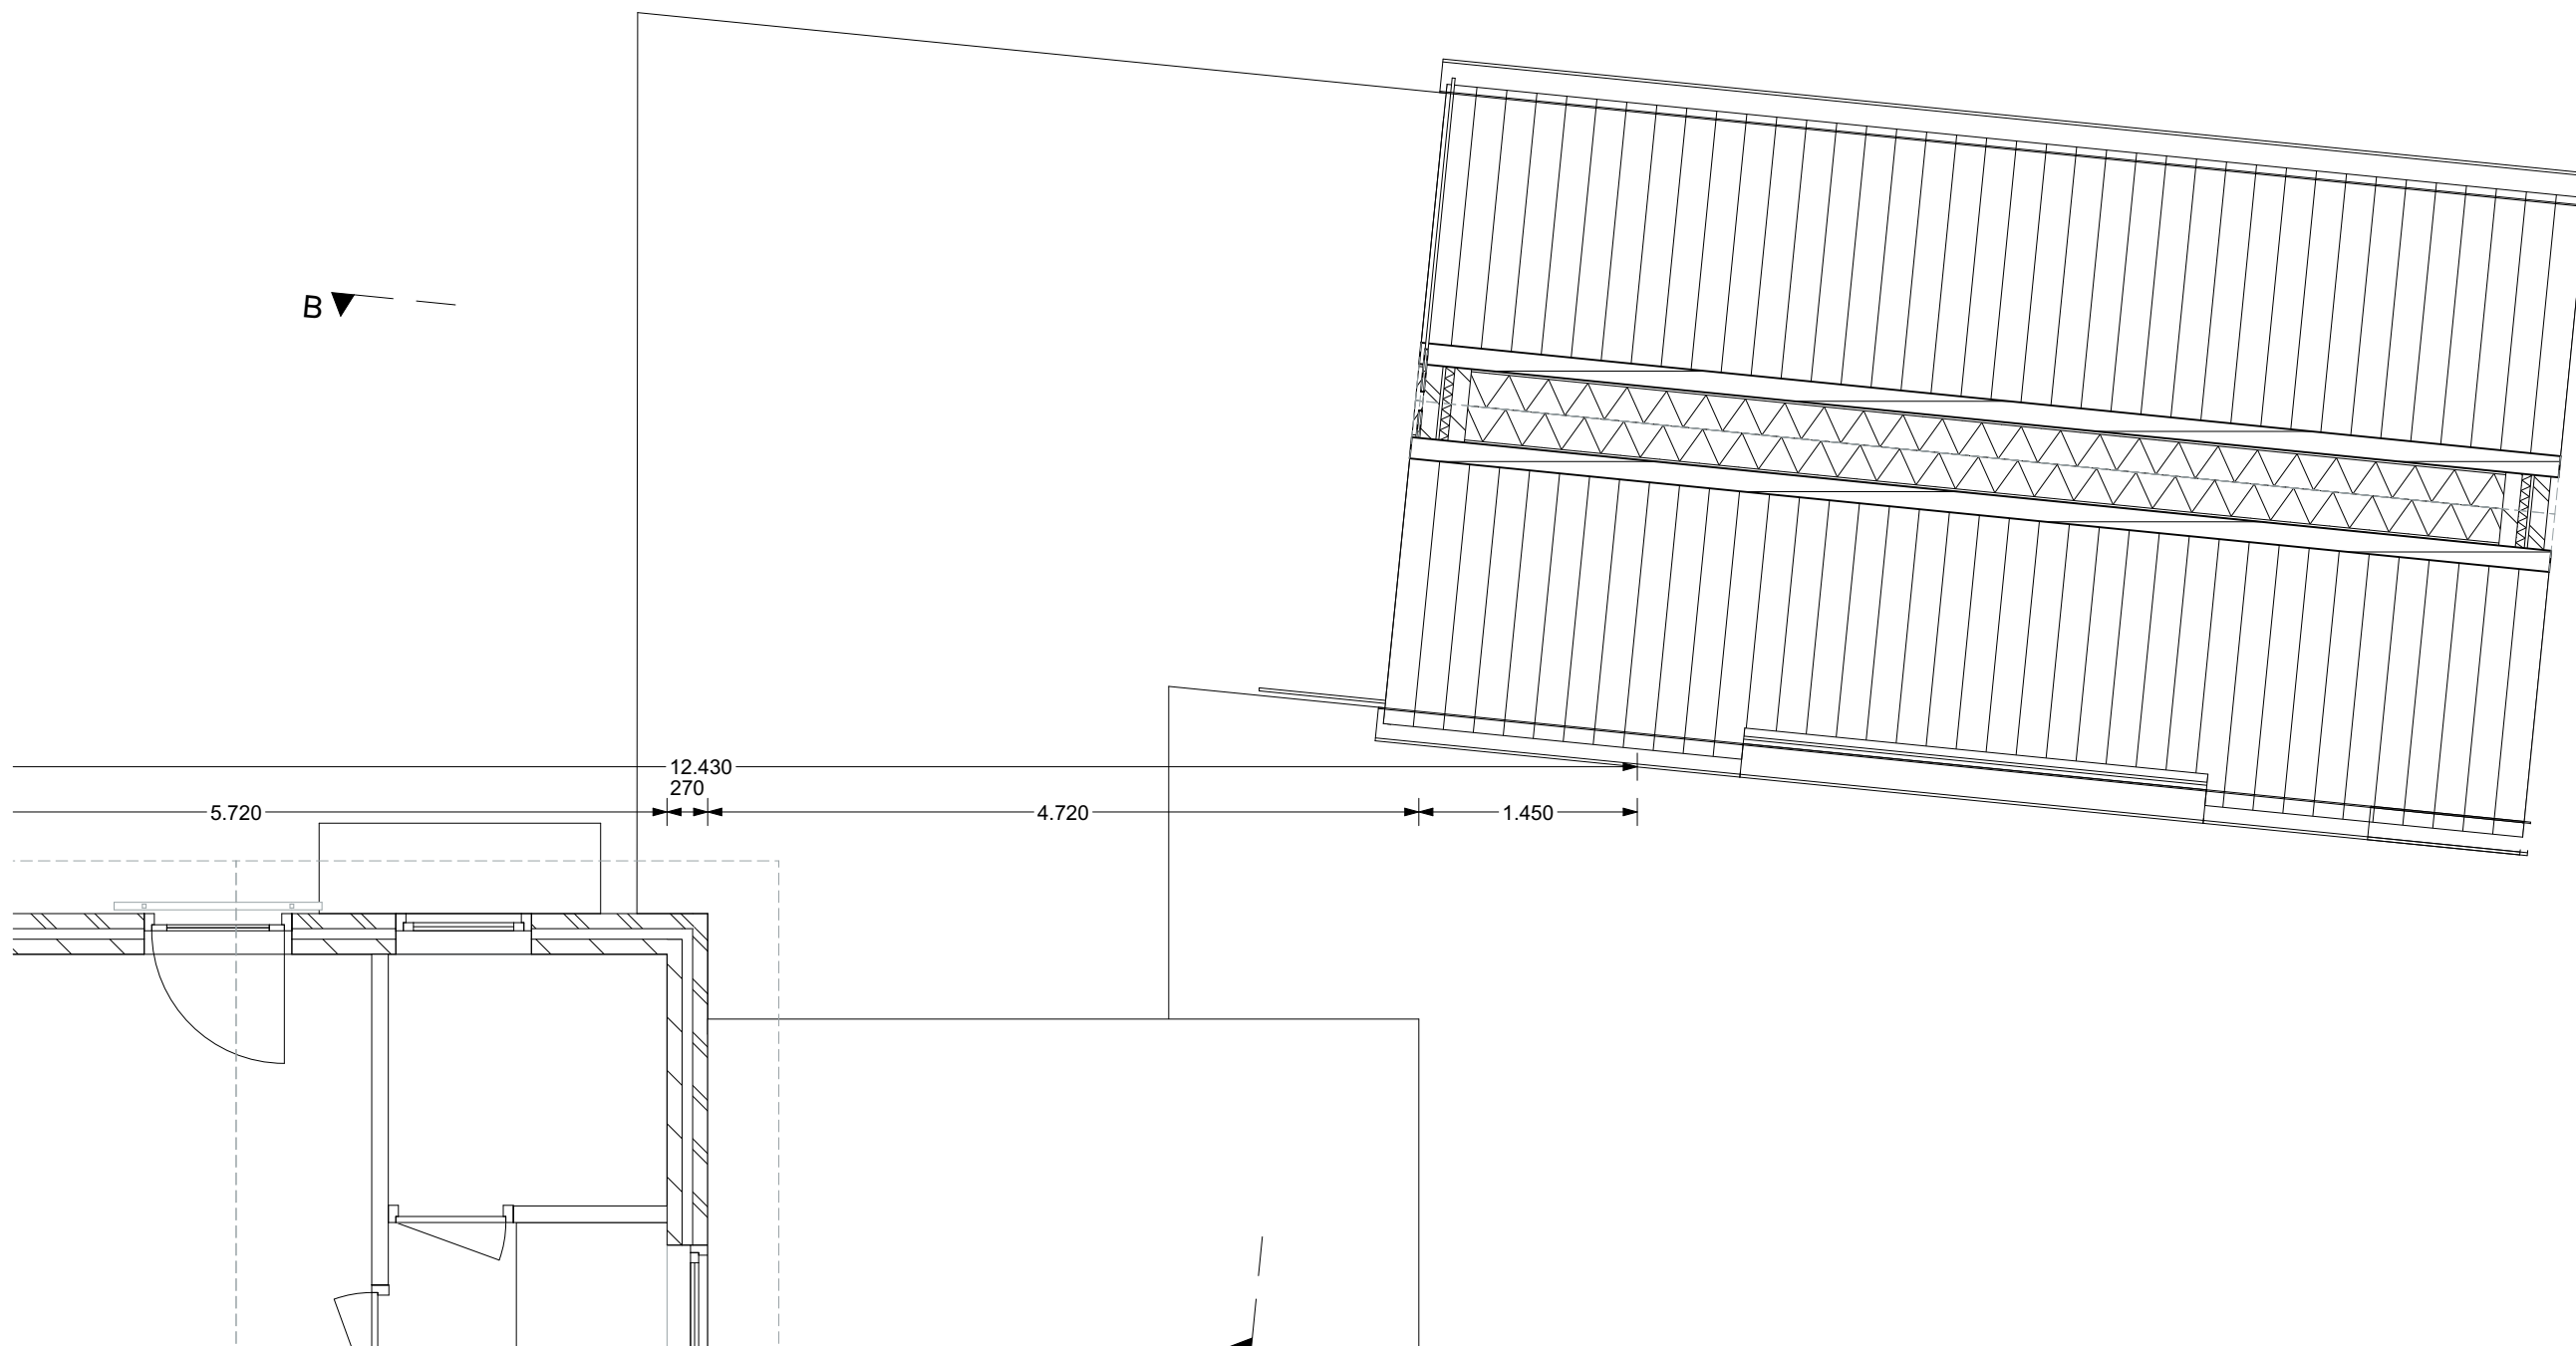

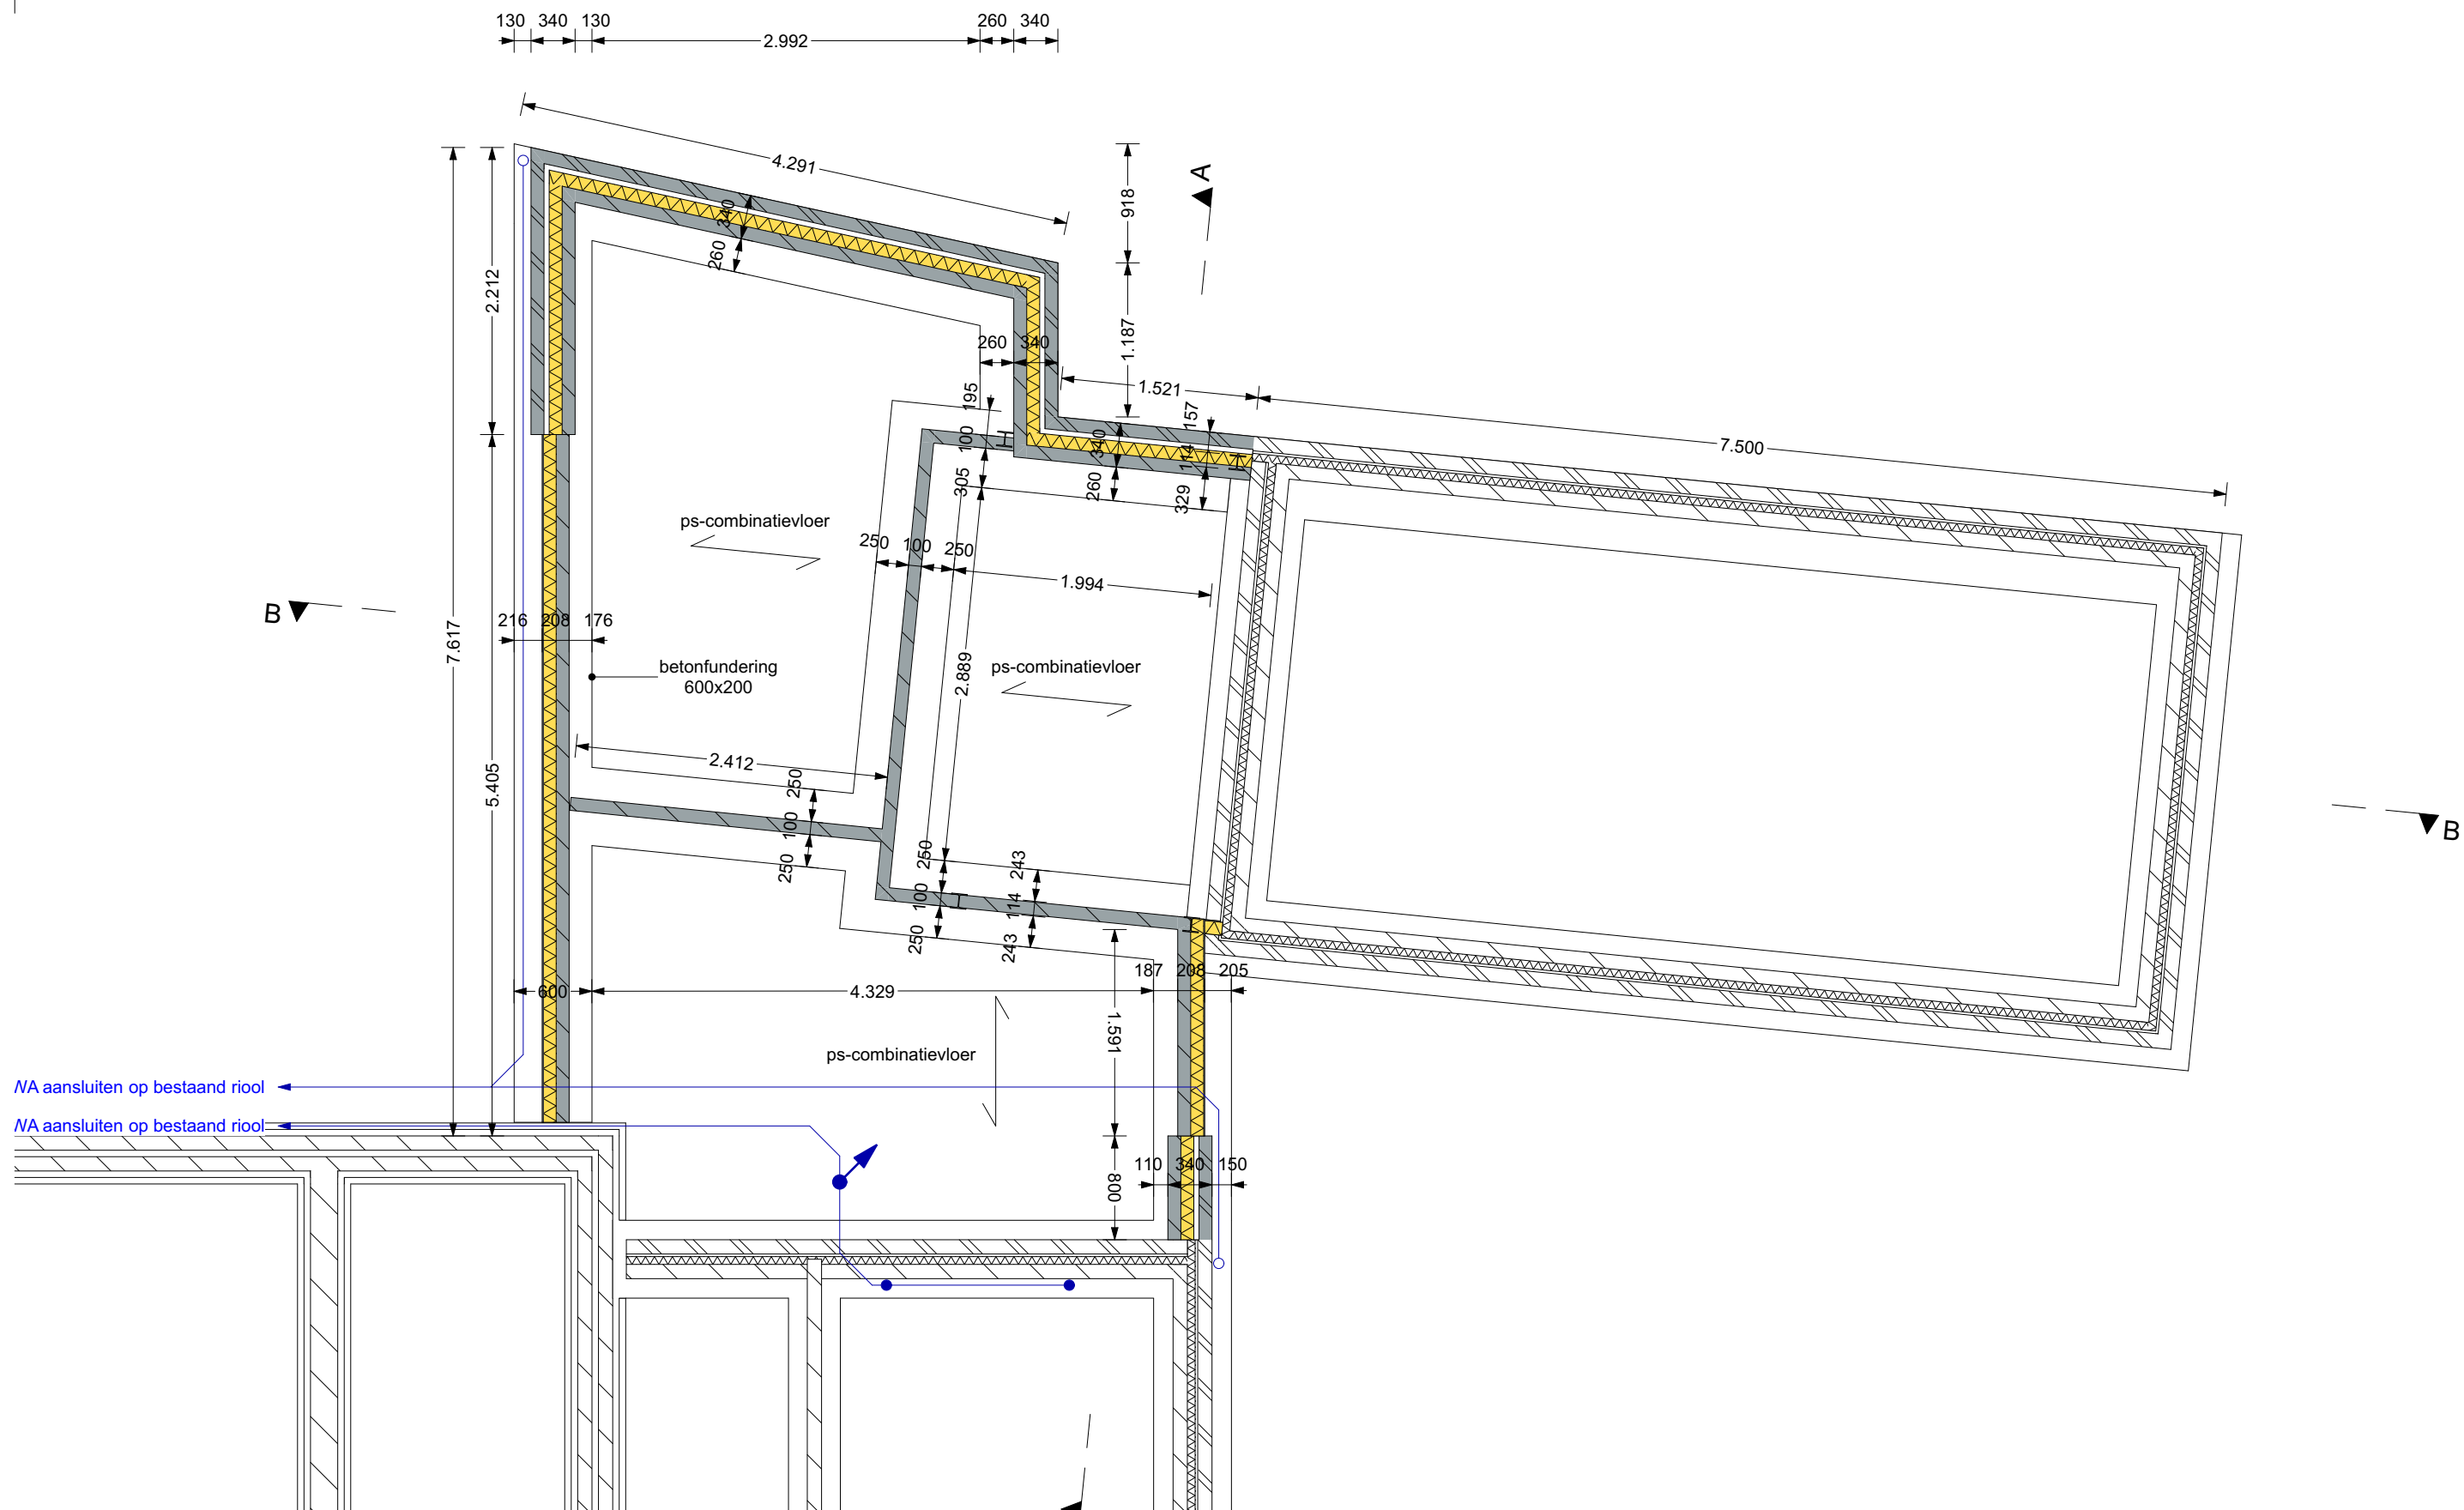

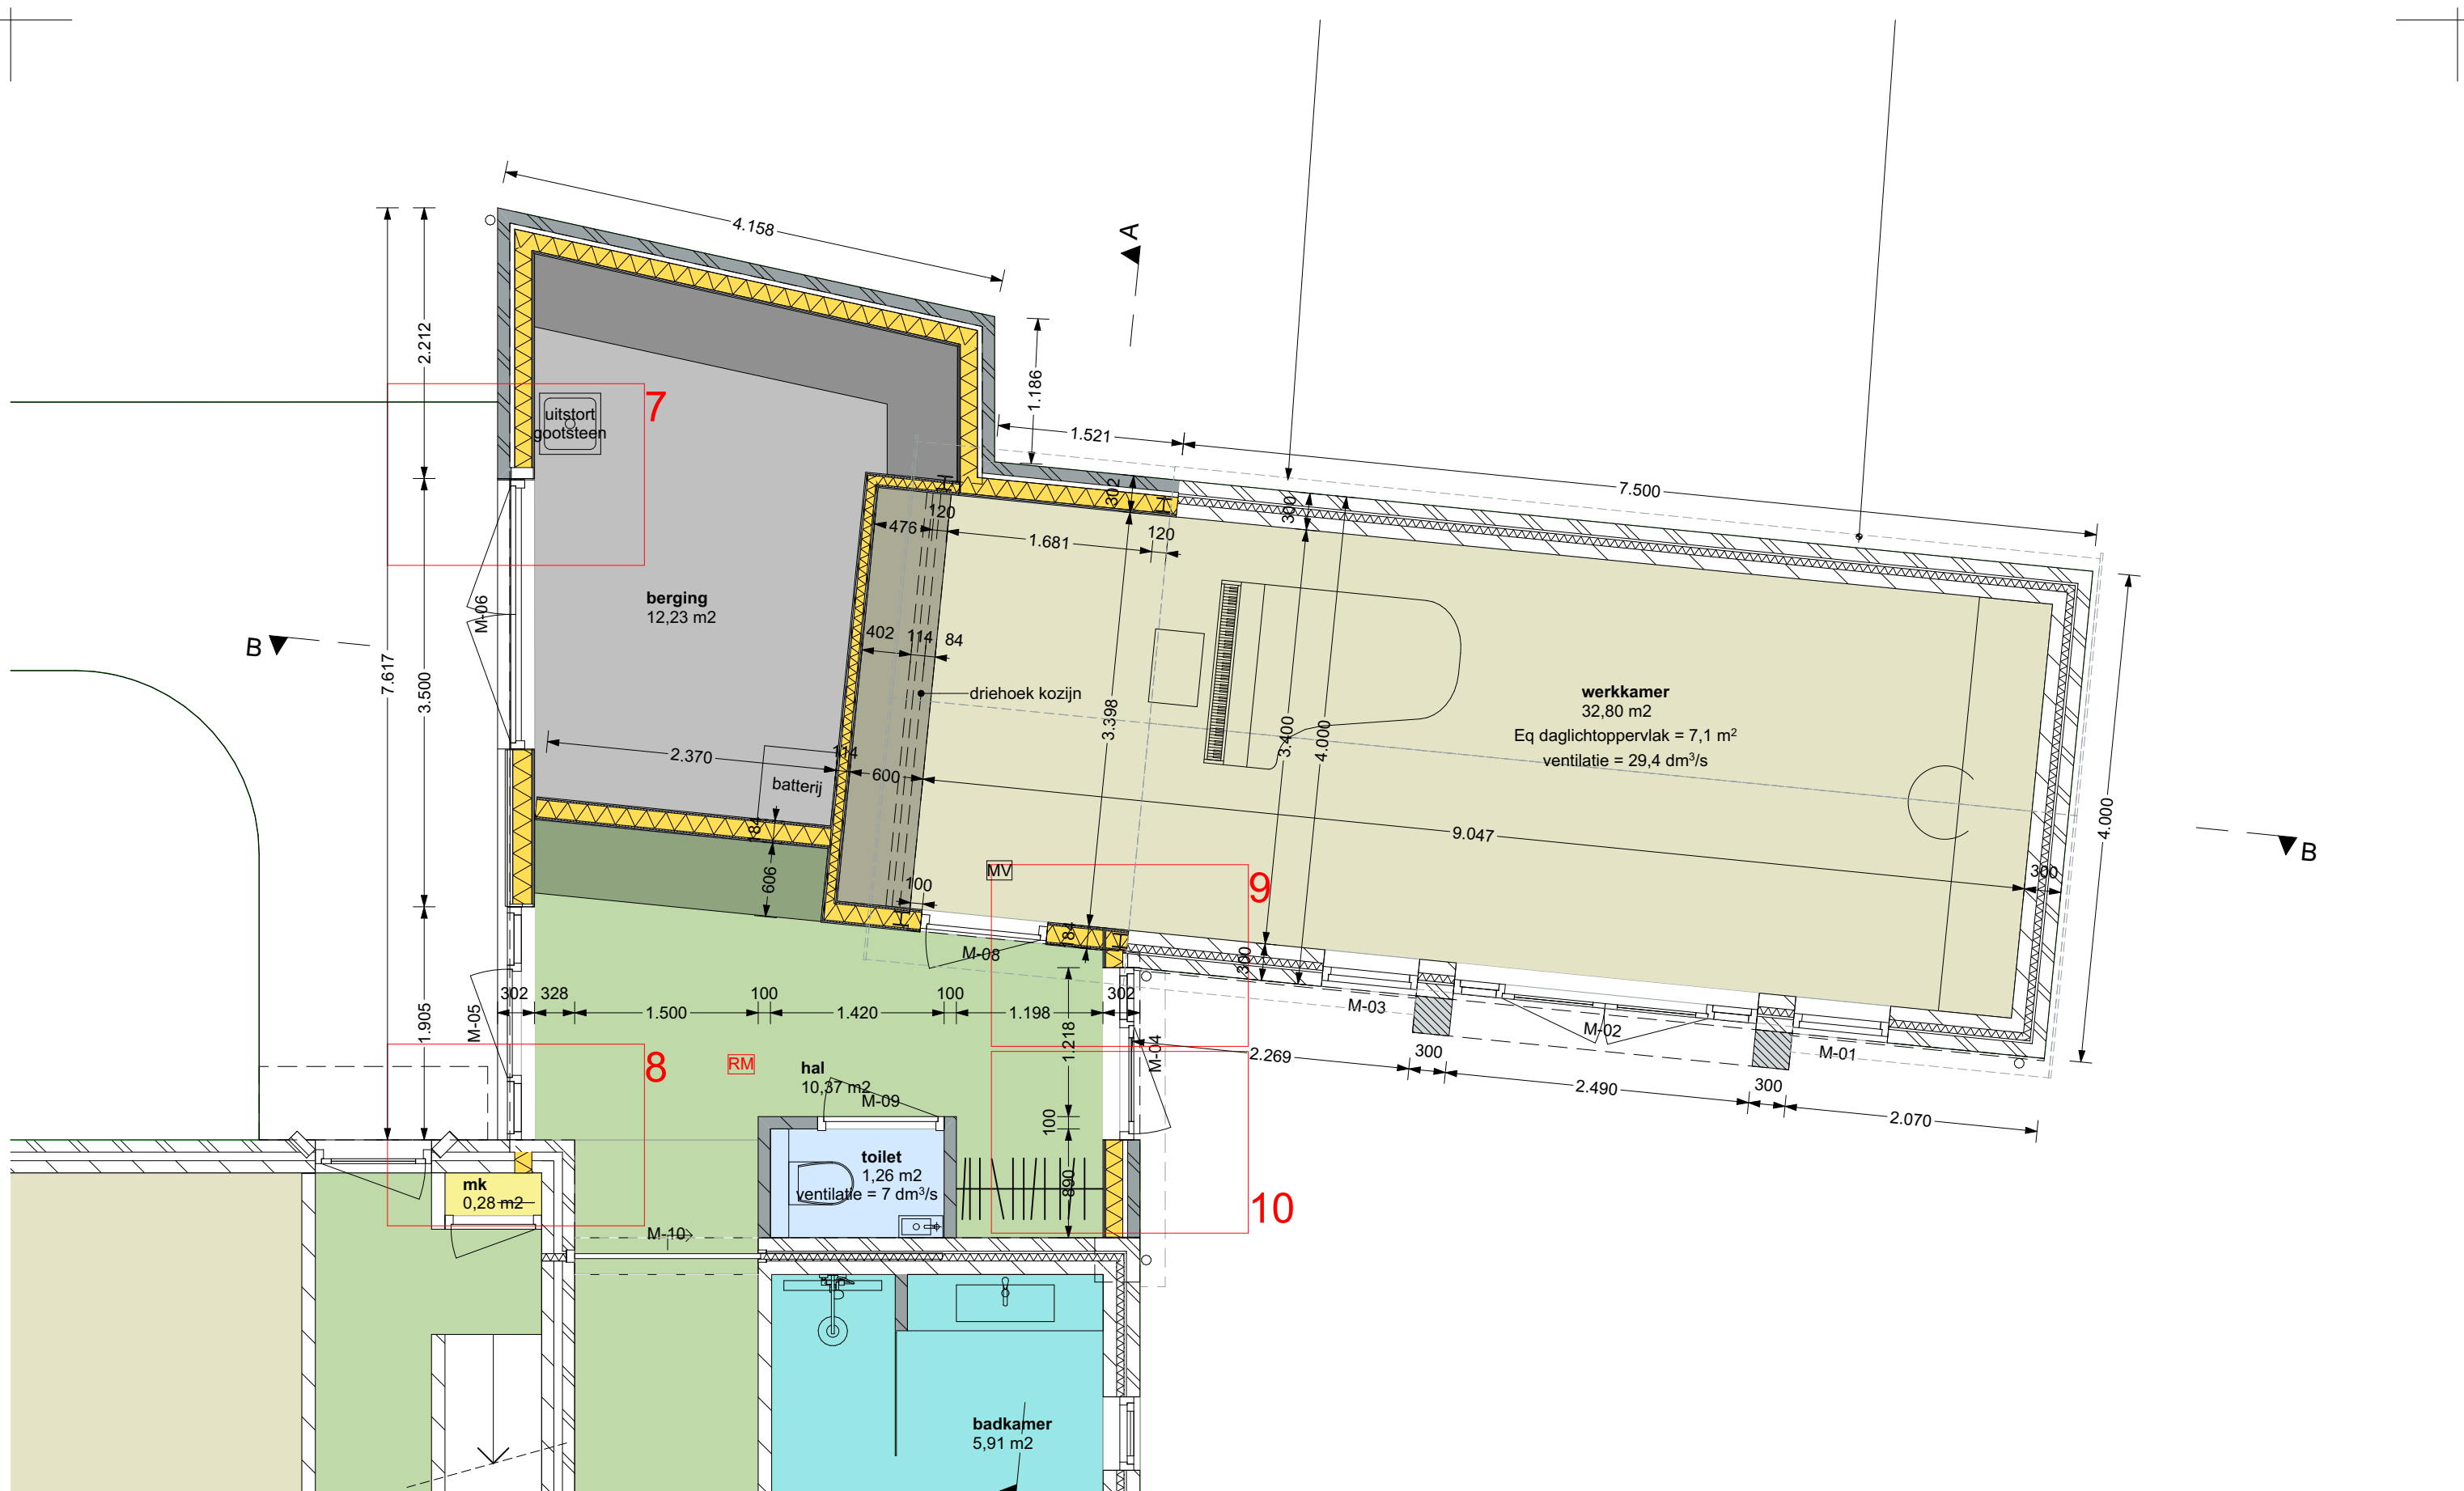


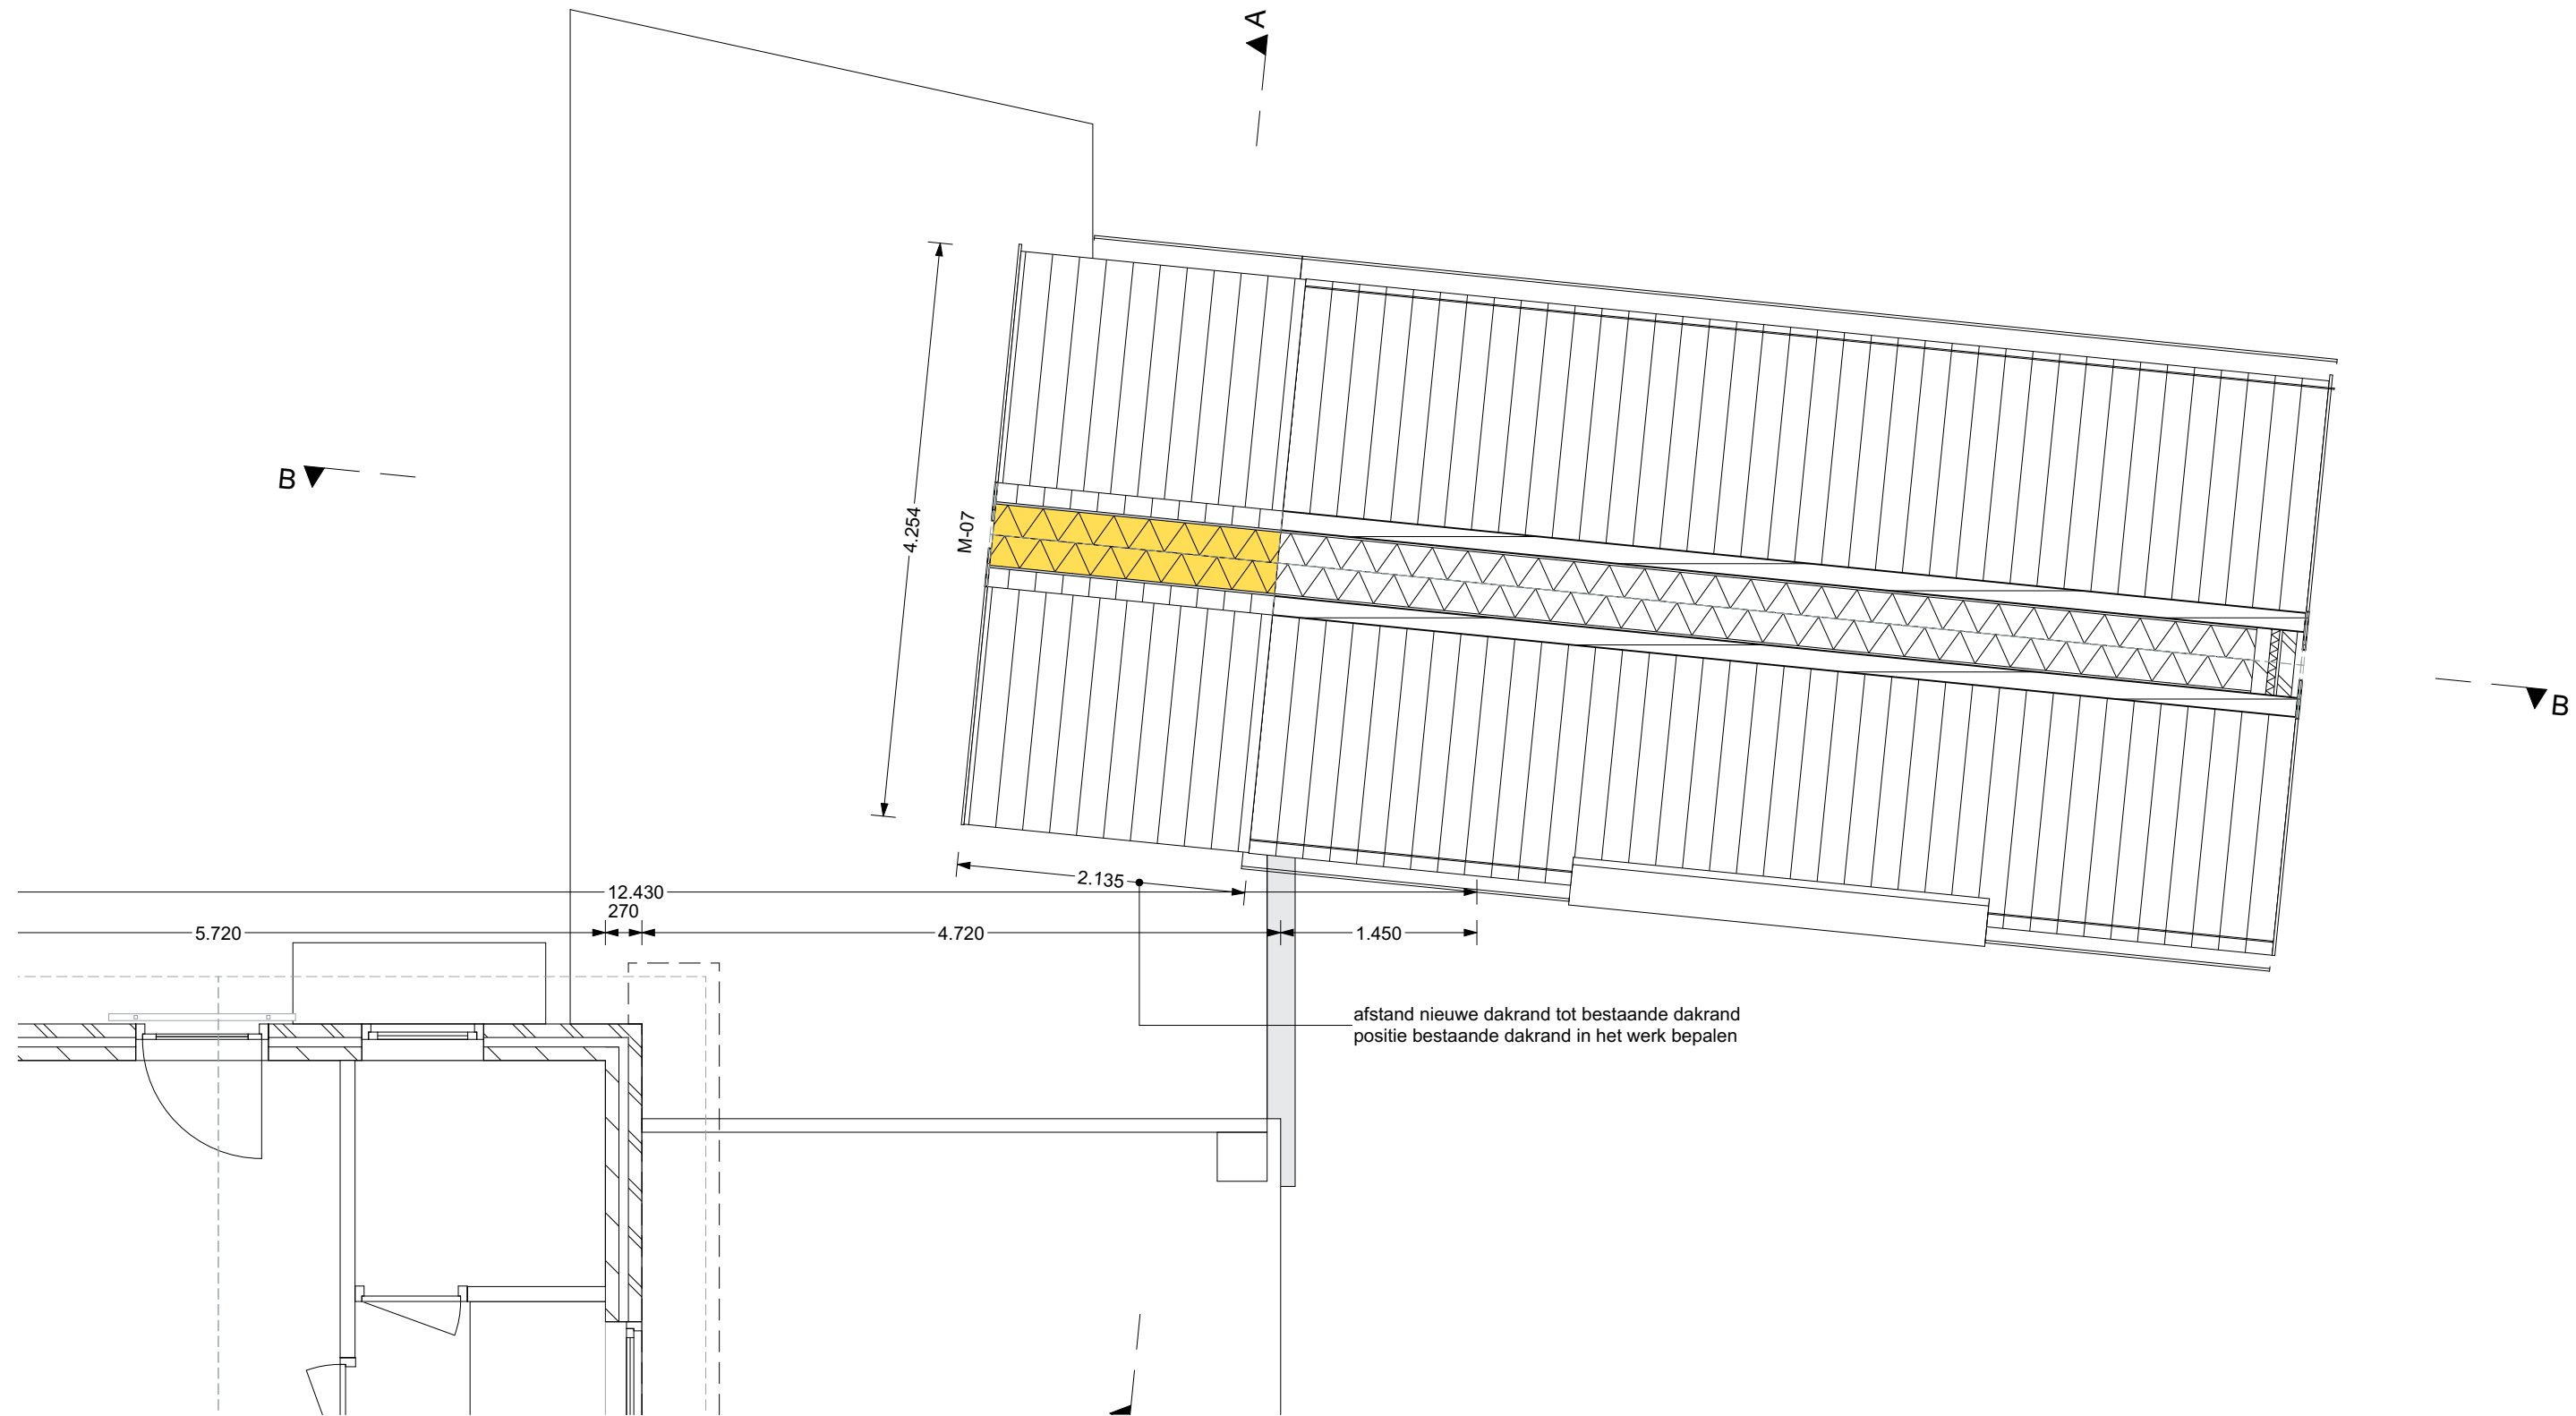

Alle maatvoering in het werk controleren

1323 DO 03.08 verdieping nieuw versie 260519
schaal 1:50
Sint Willibrordusstraat 14
www.valkarchitecten.nl



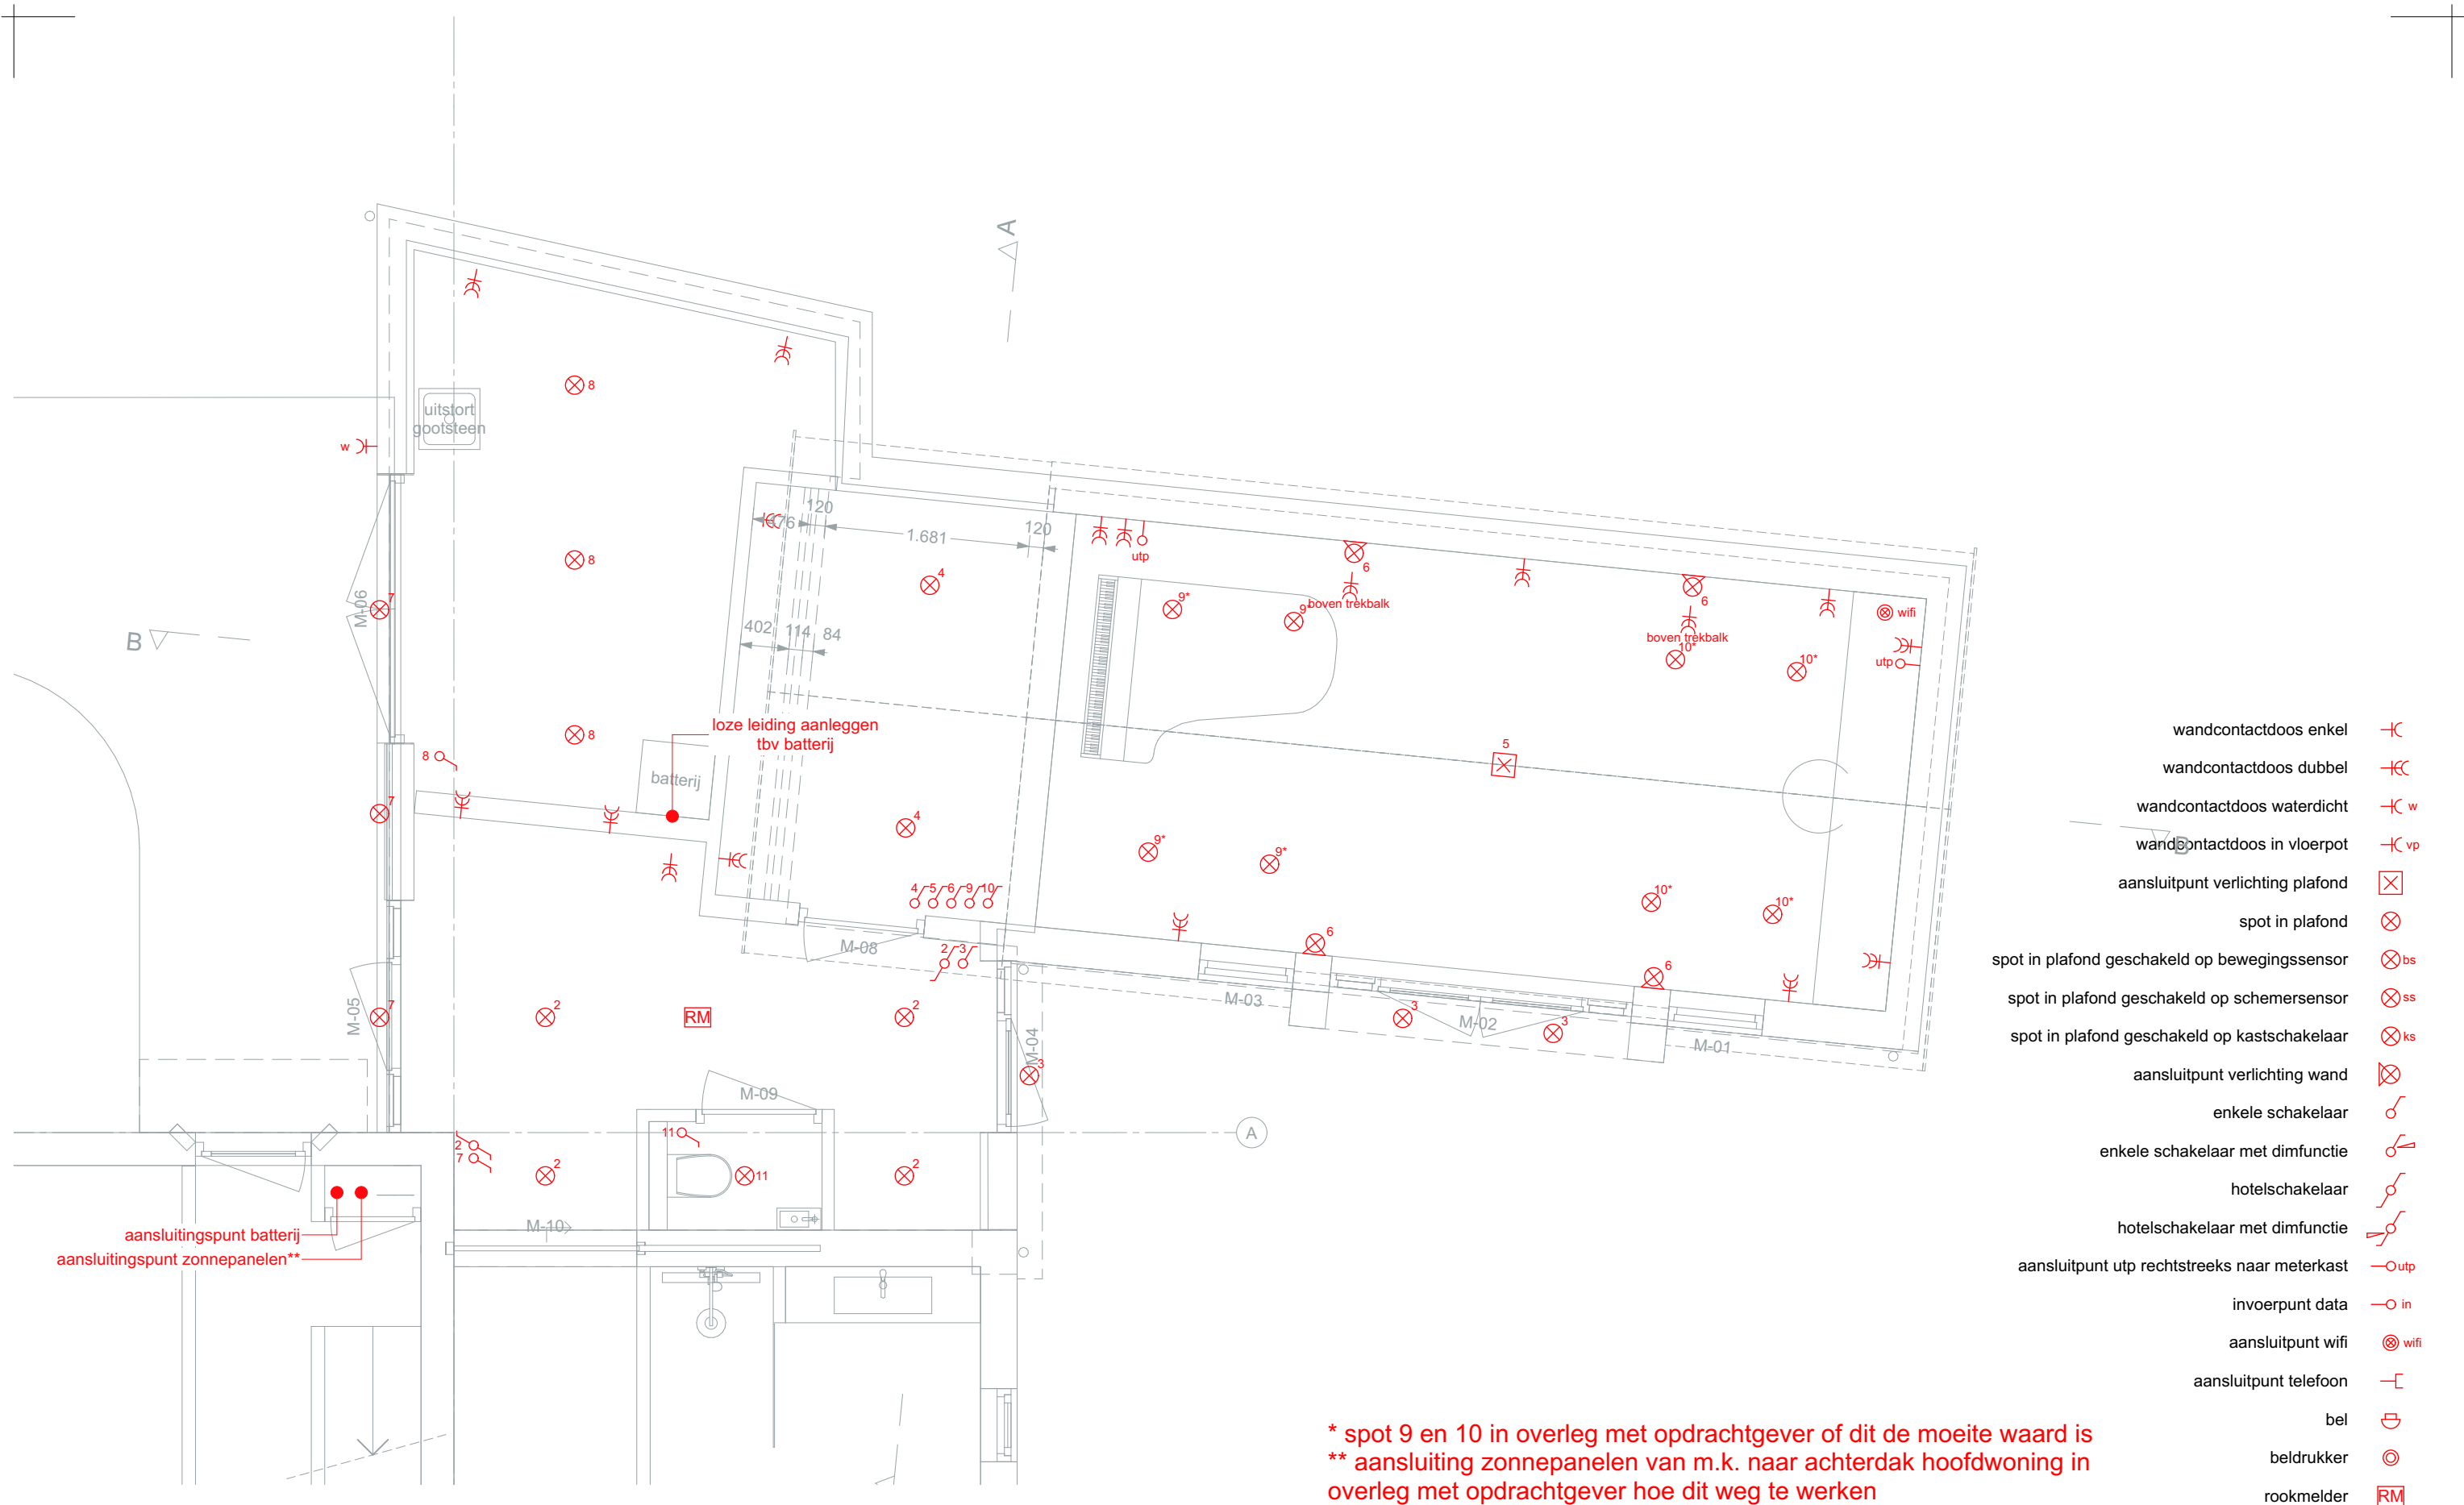

▽ +7.461


▽ +4.986

▽ +2.800


△ +2.500

▽ ±0


voorgevel

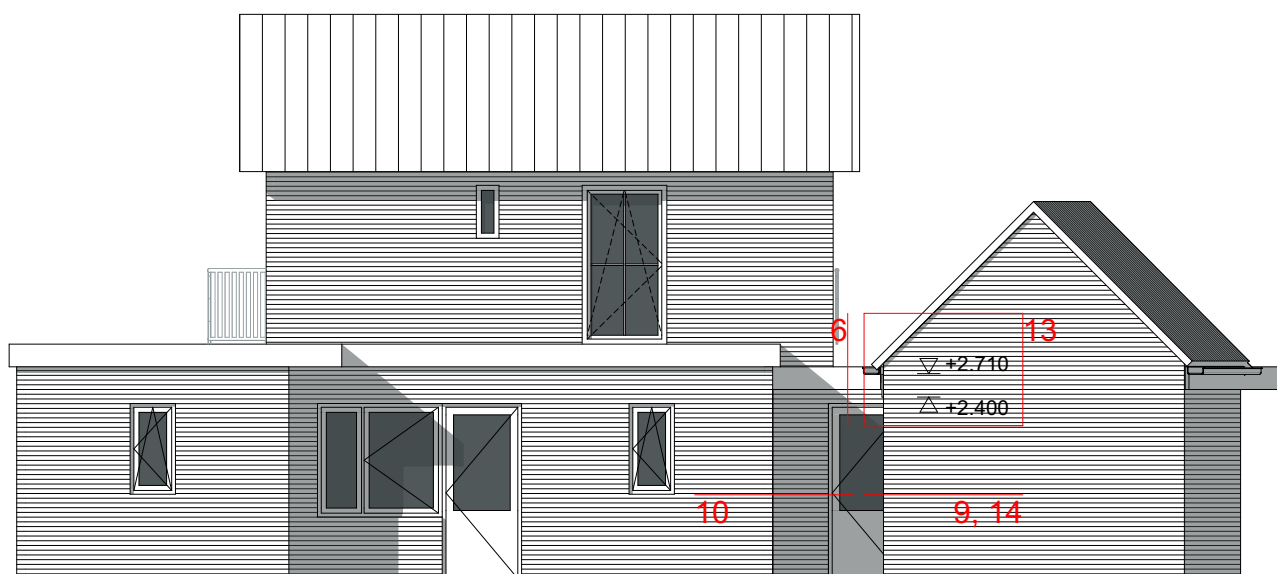


achtergevel

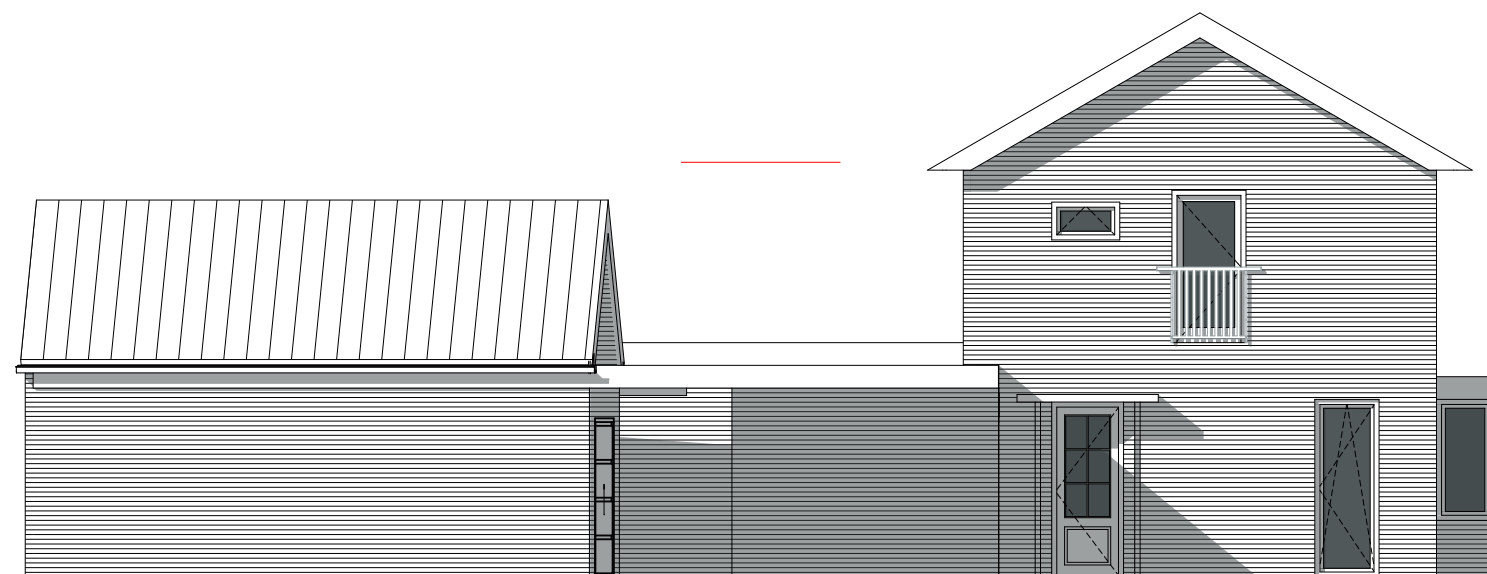


rechter zijgevel

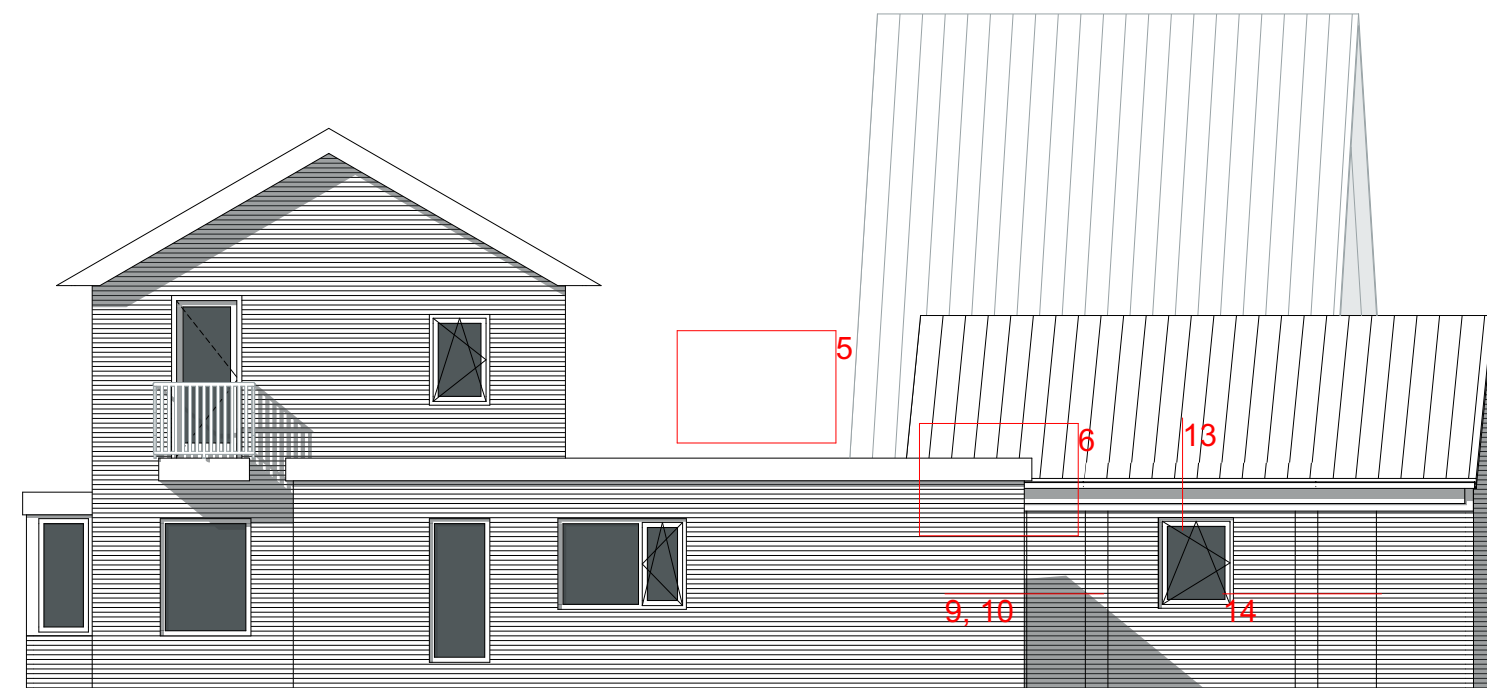


linker zijgevel

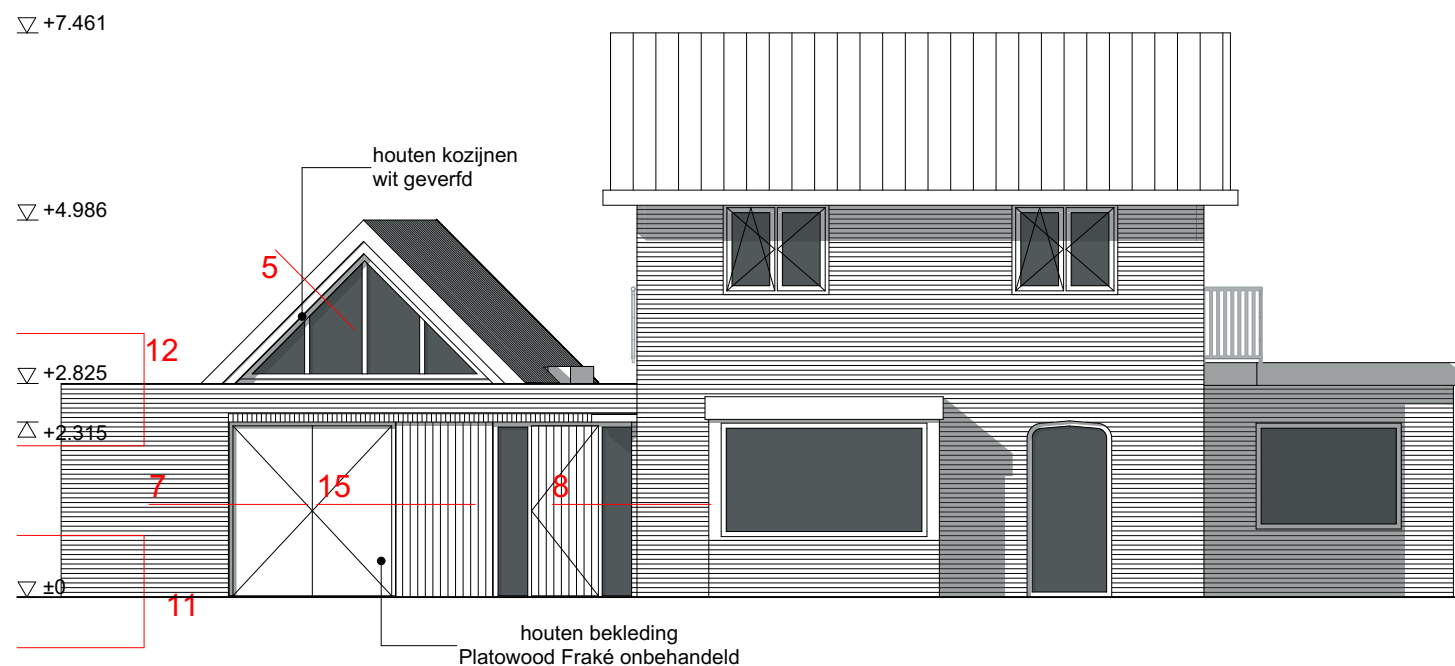


voorgevel

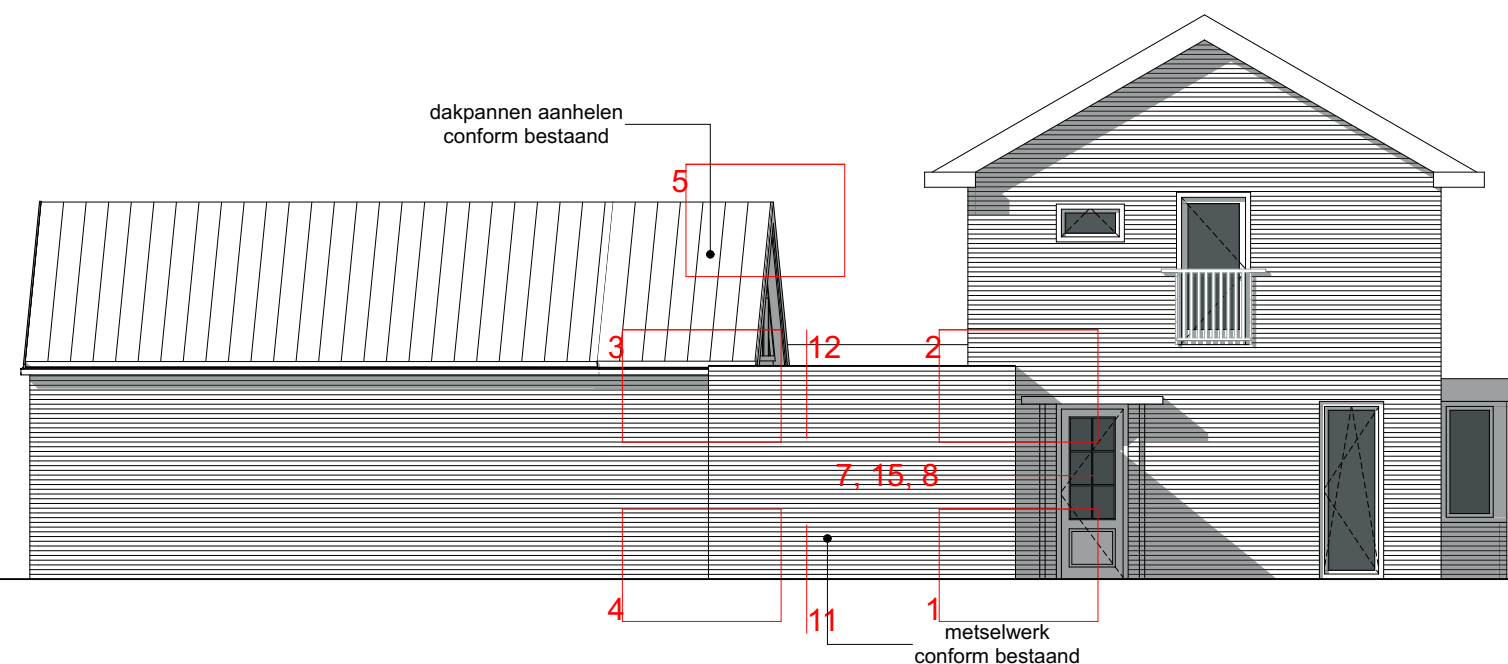



rechter zijgevel

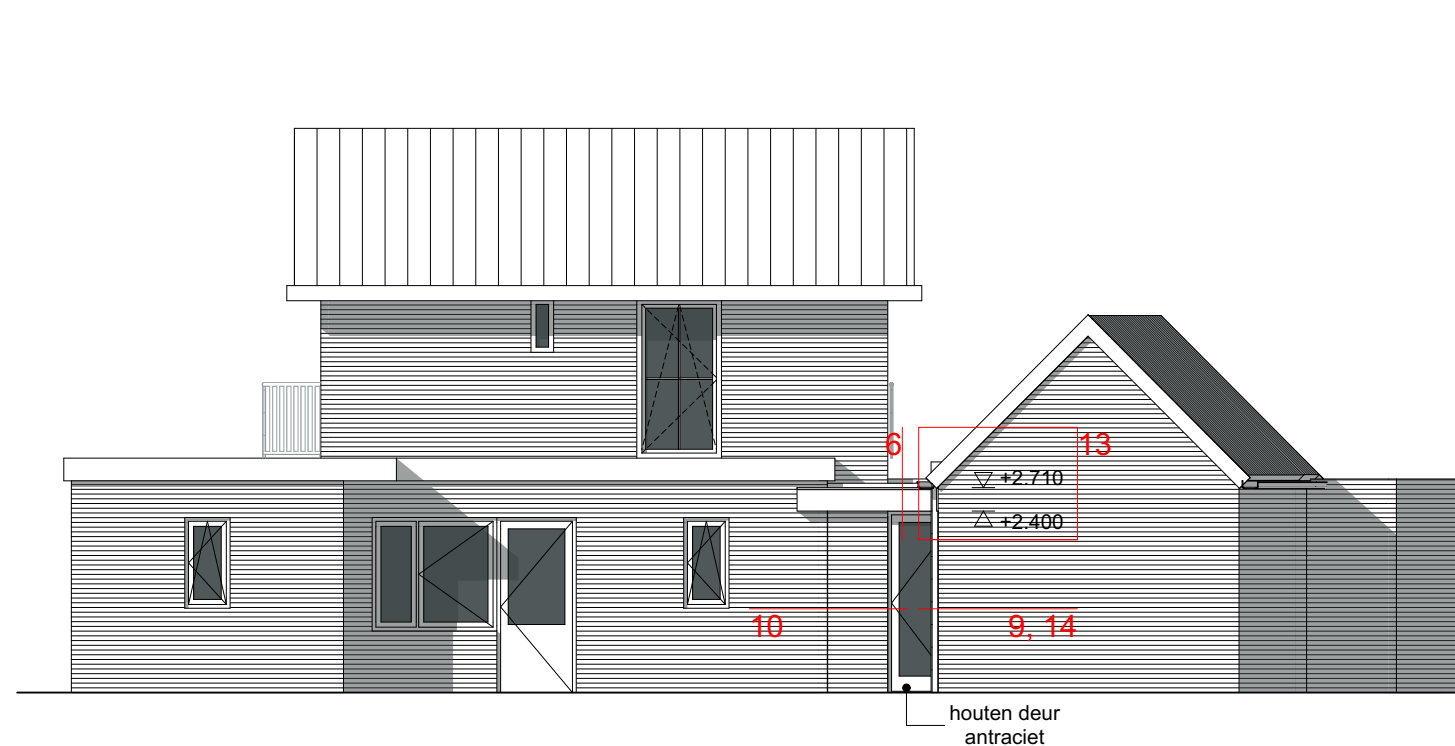


achtergevel

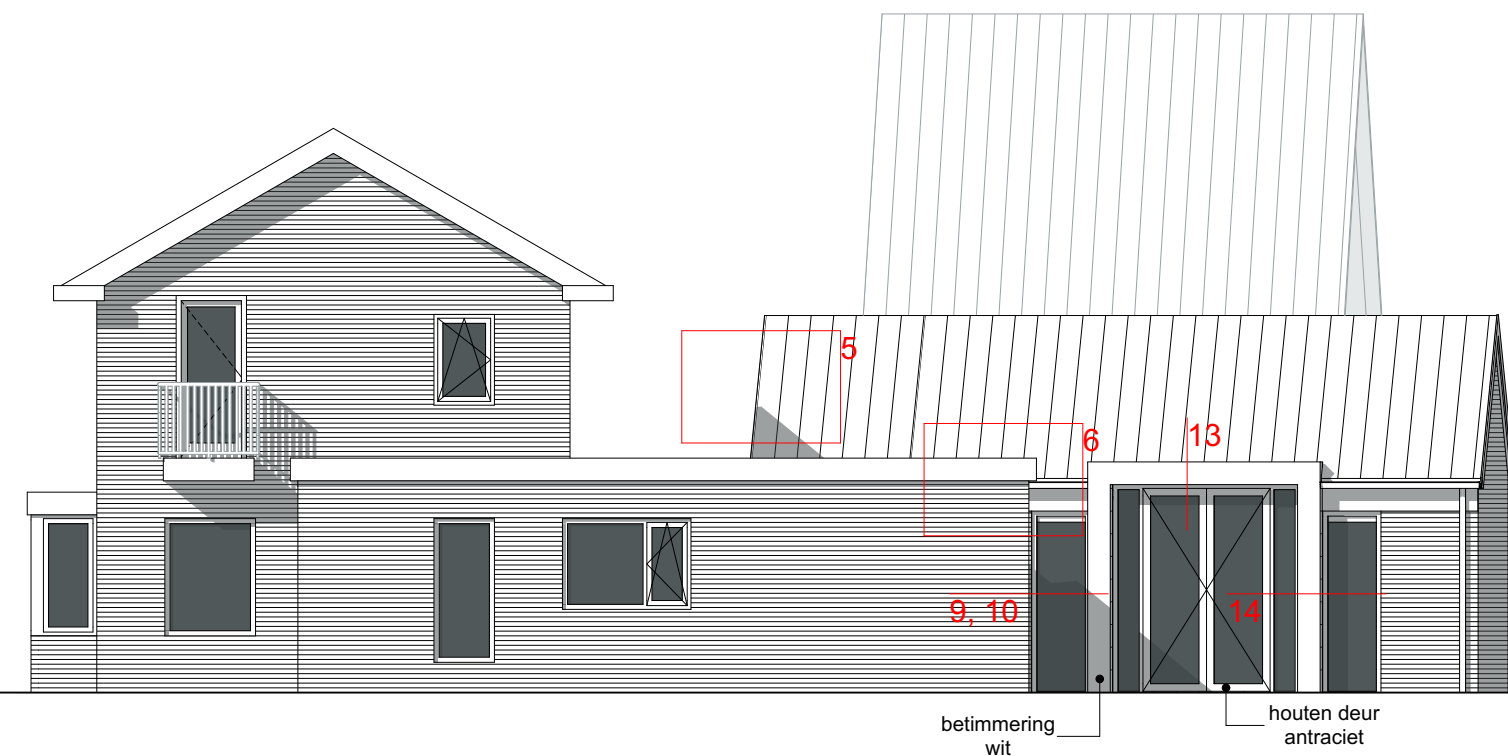

linker zijgevel

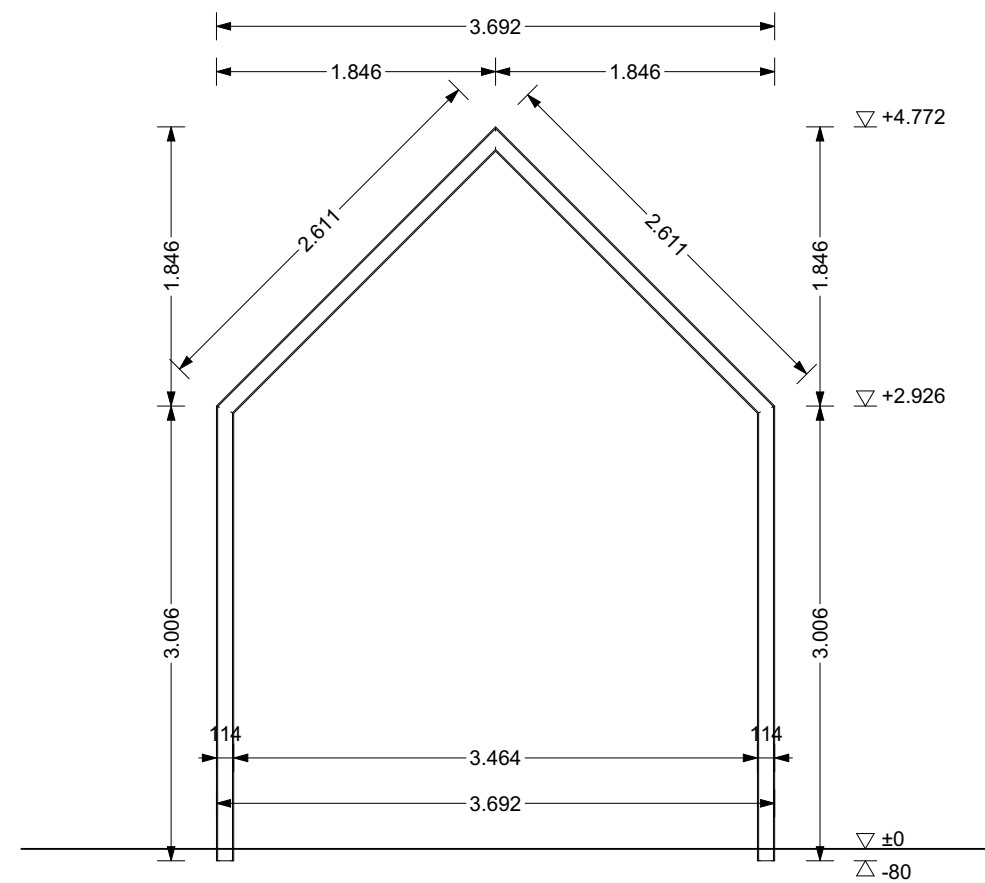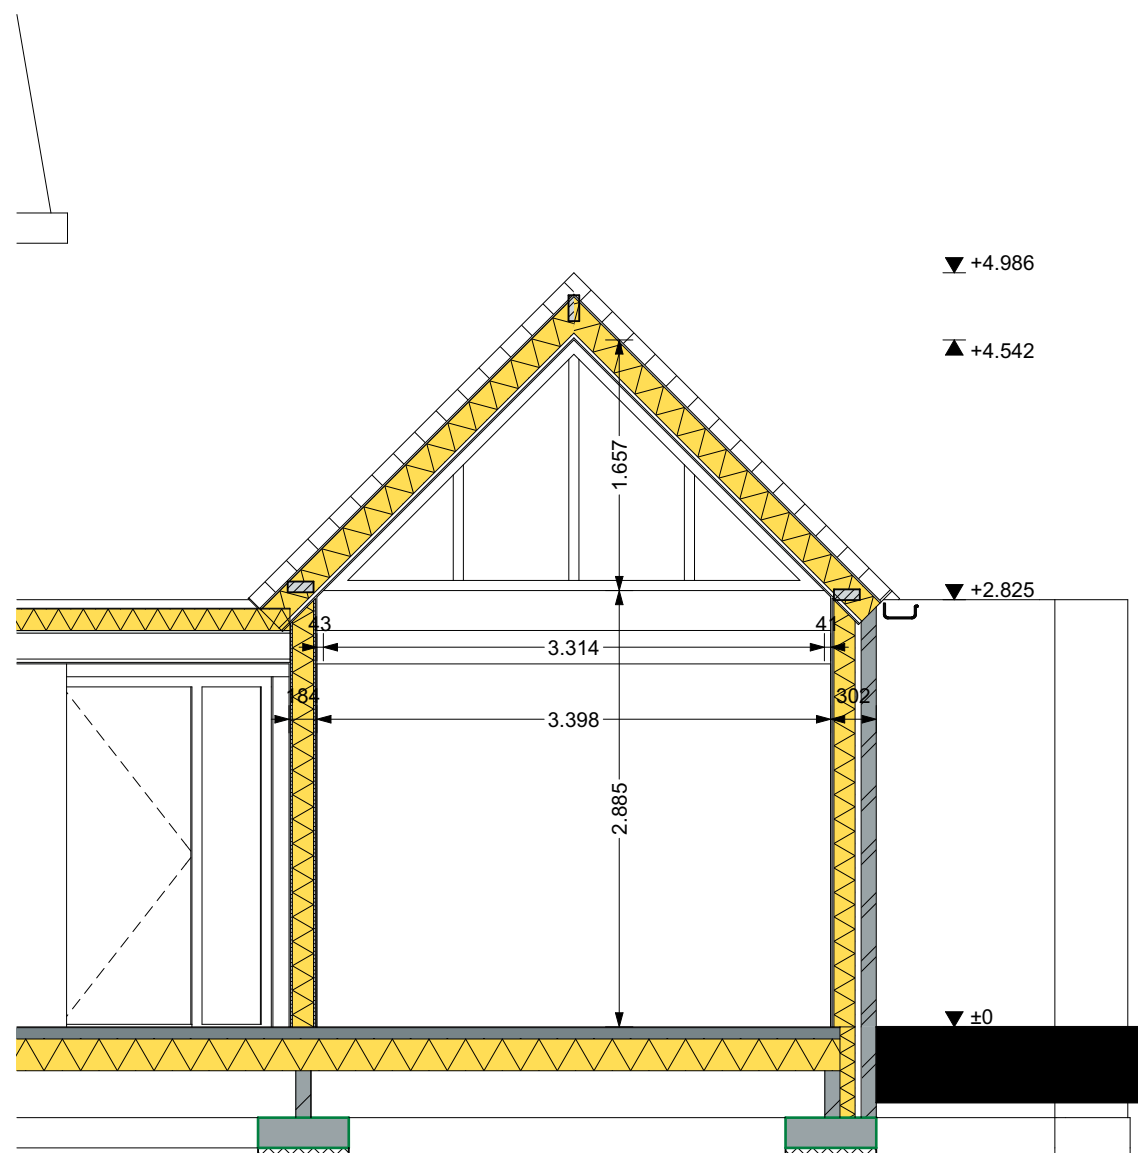


stalen spantconstructie

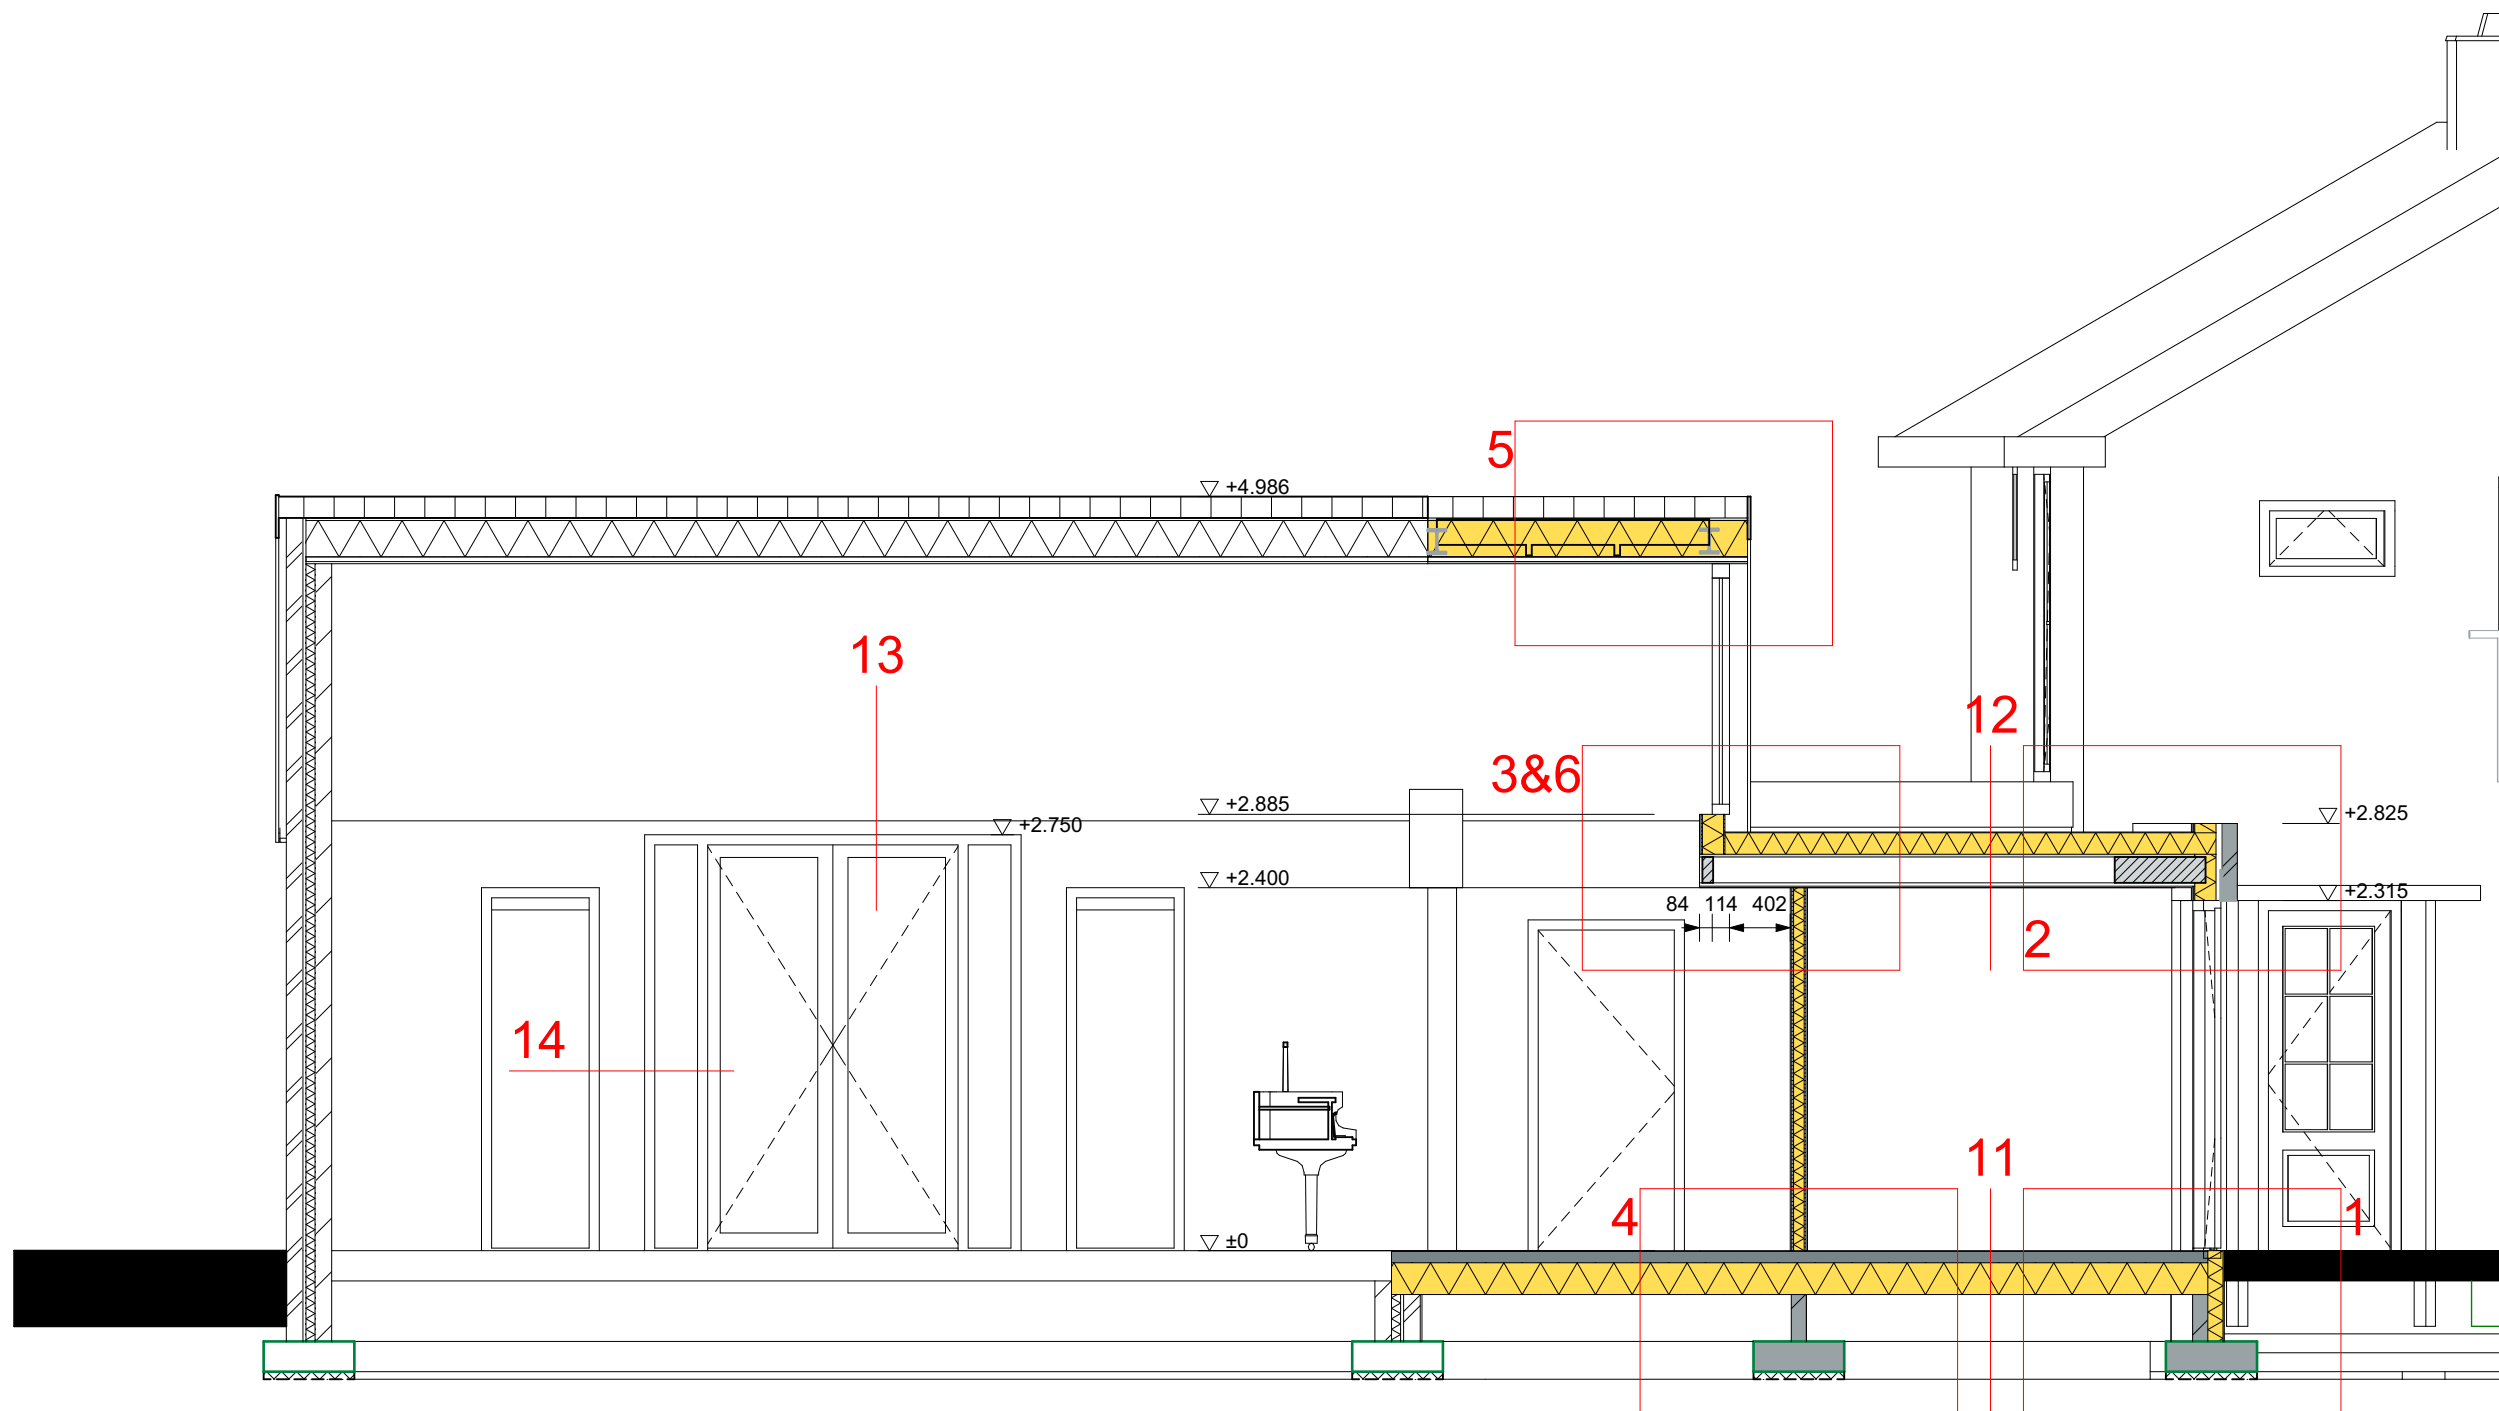



1323 DO 05.04 doorsnede B-B nieuw versie 260519
 schaal 1:50
 Sint Willibrordusstraat 14
 www.valkarchitecten.nl



Alle maatvoering in het werk controleren

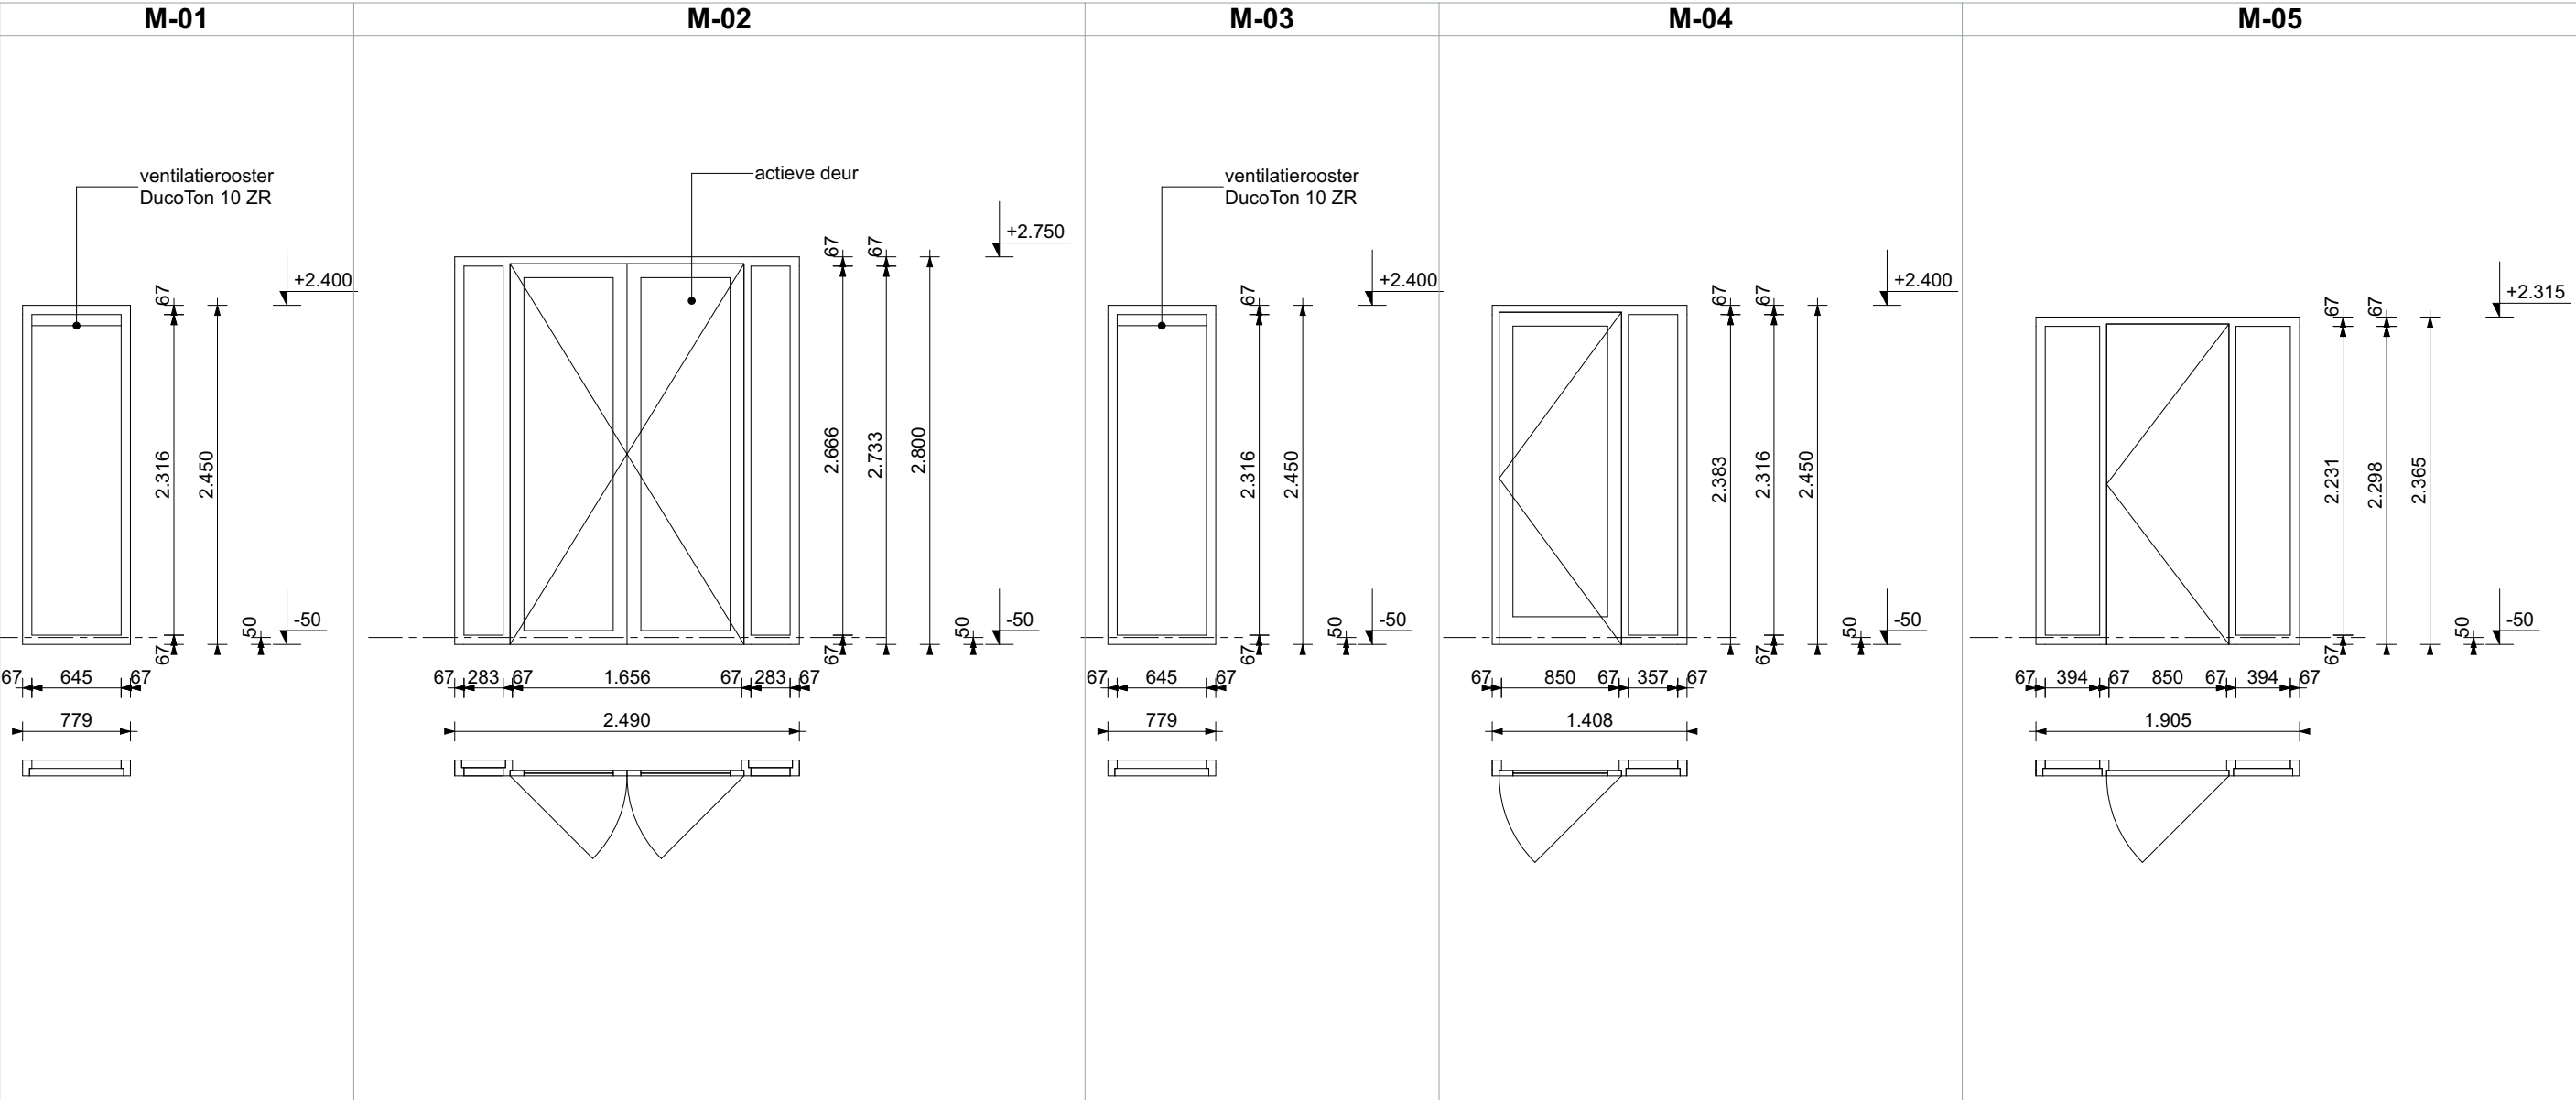


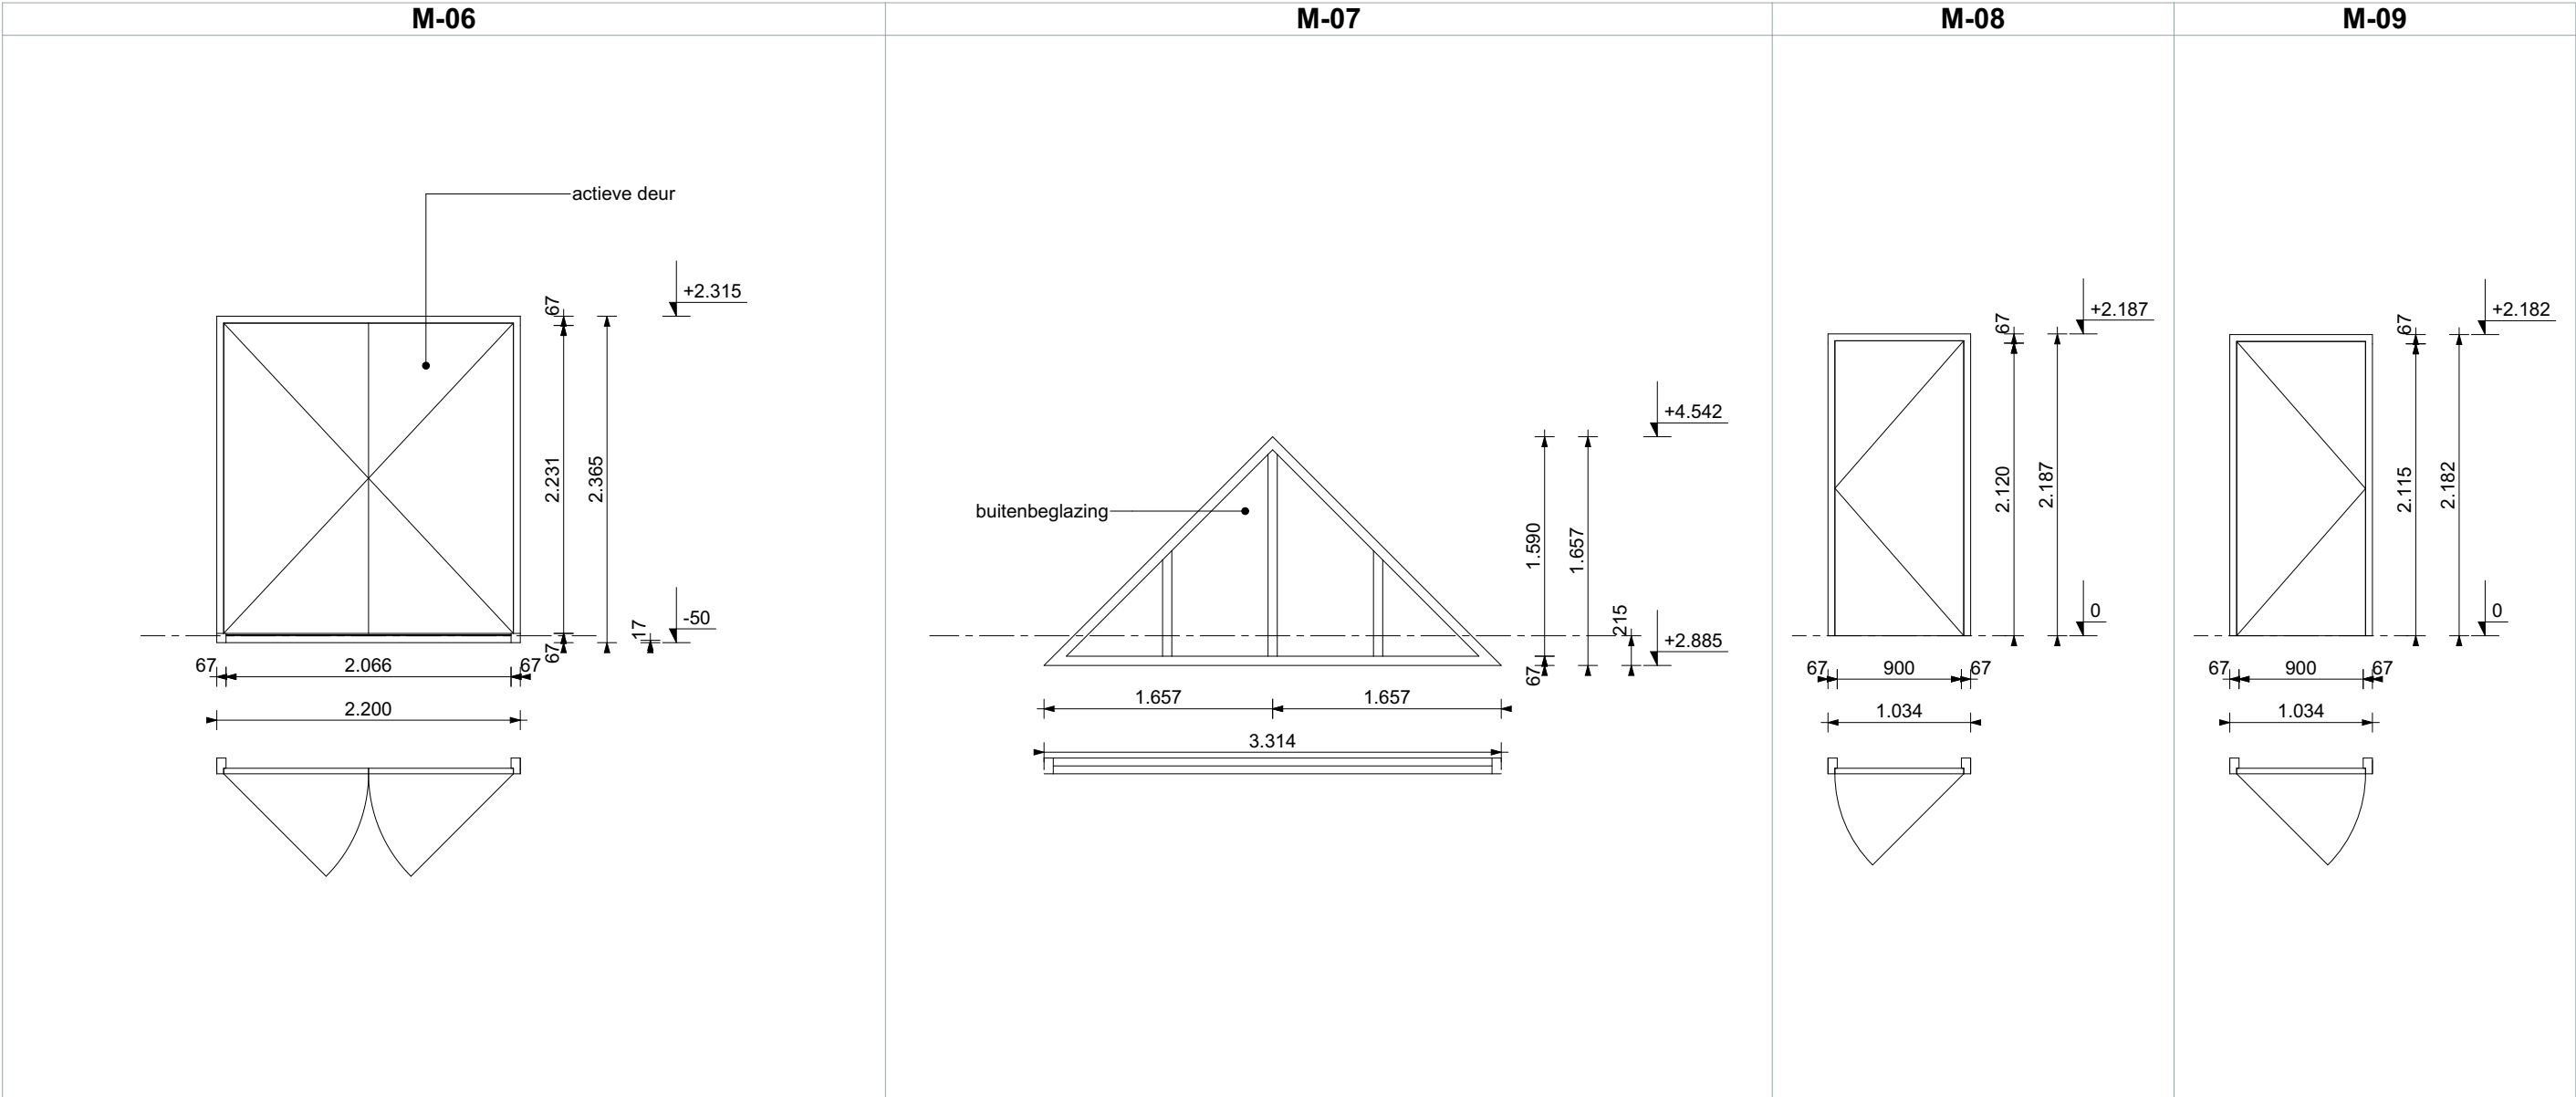


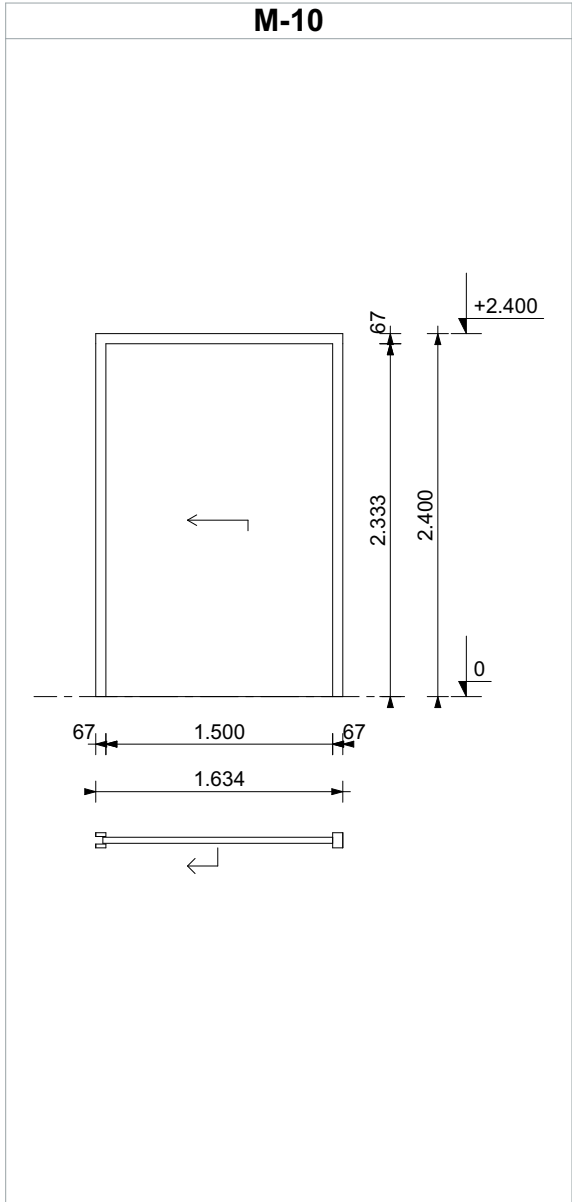



Alle maatvoering in het werk controleren




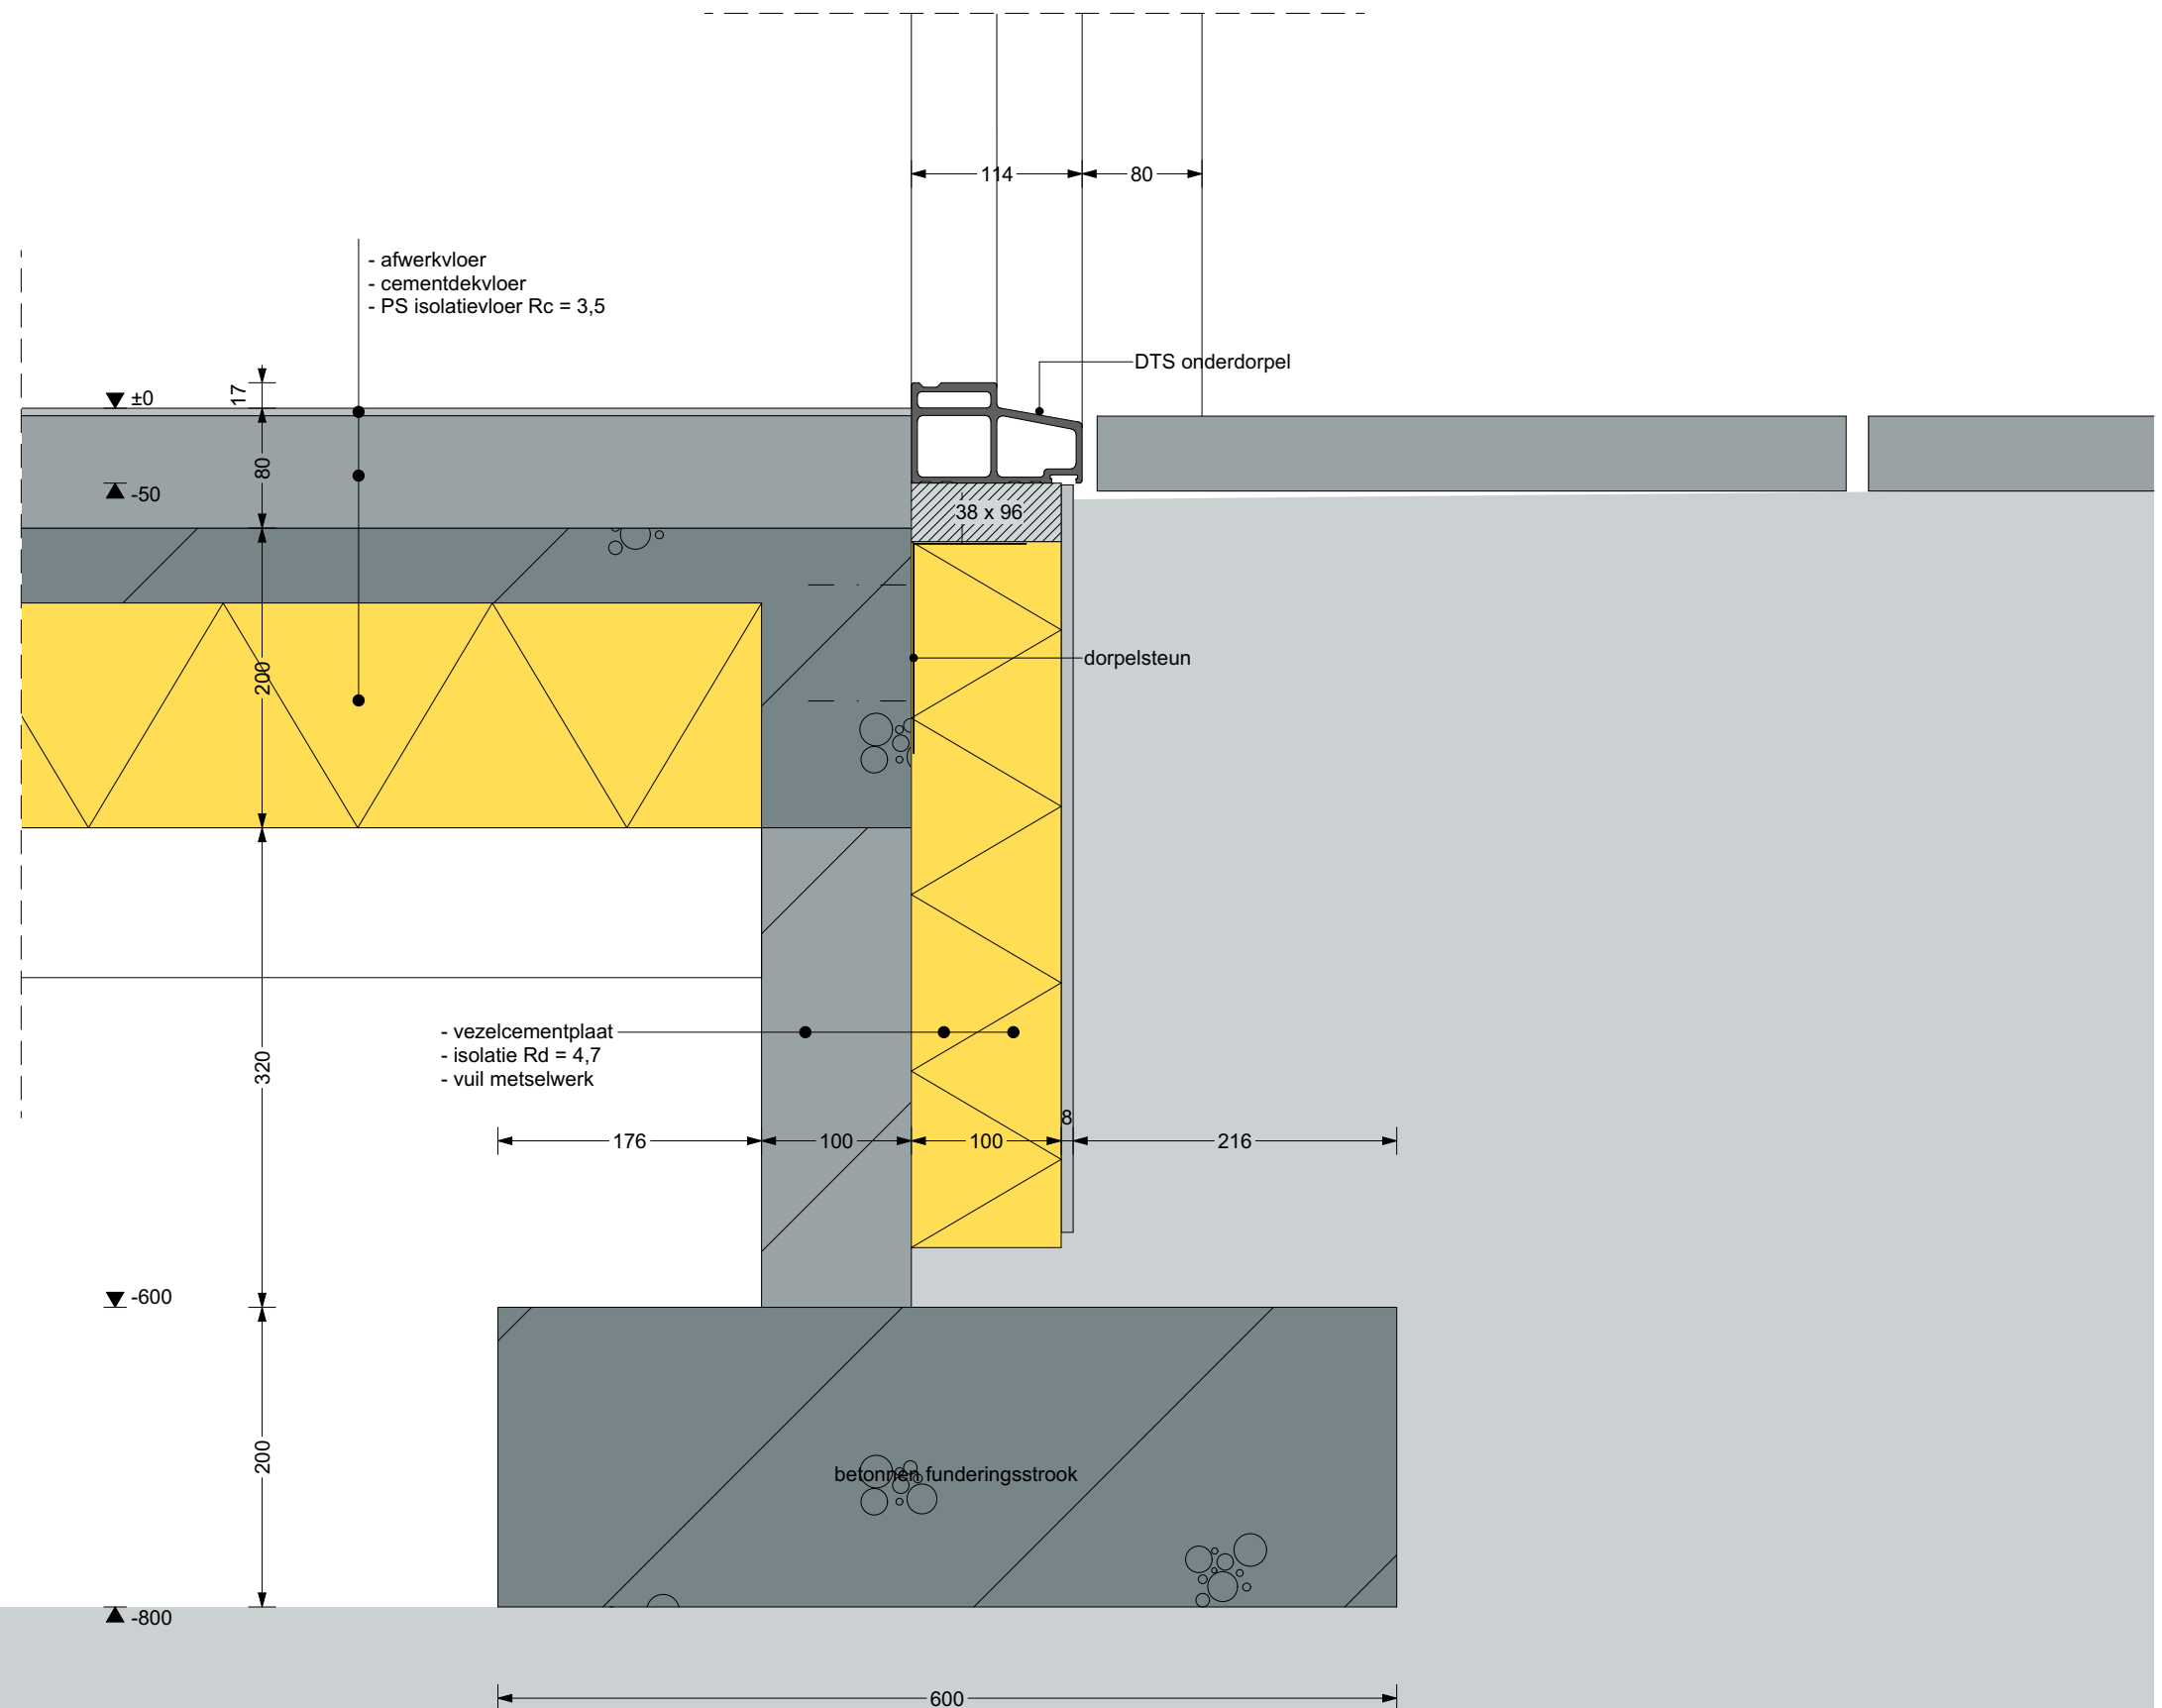


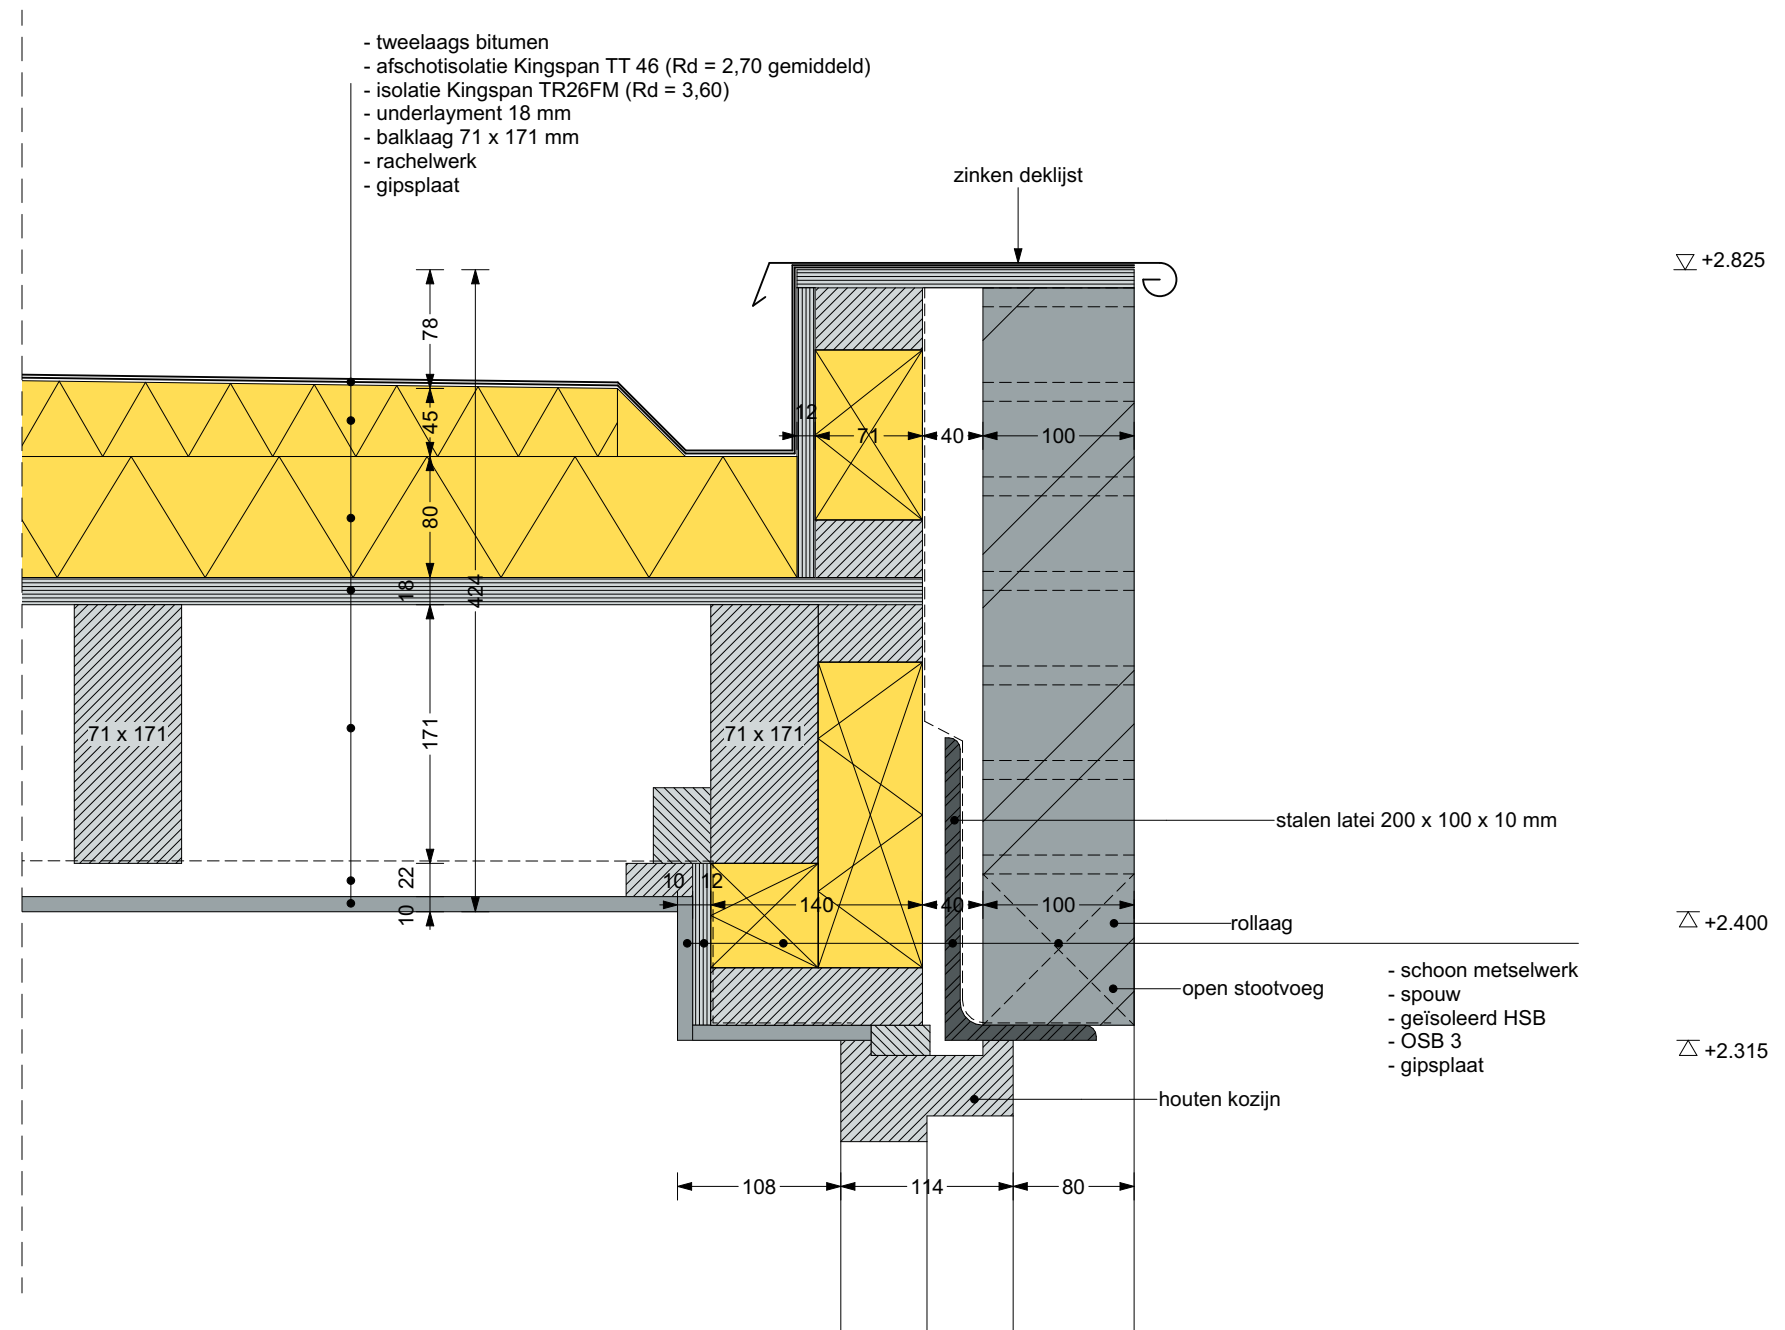


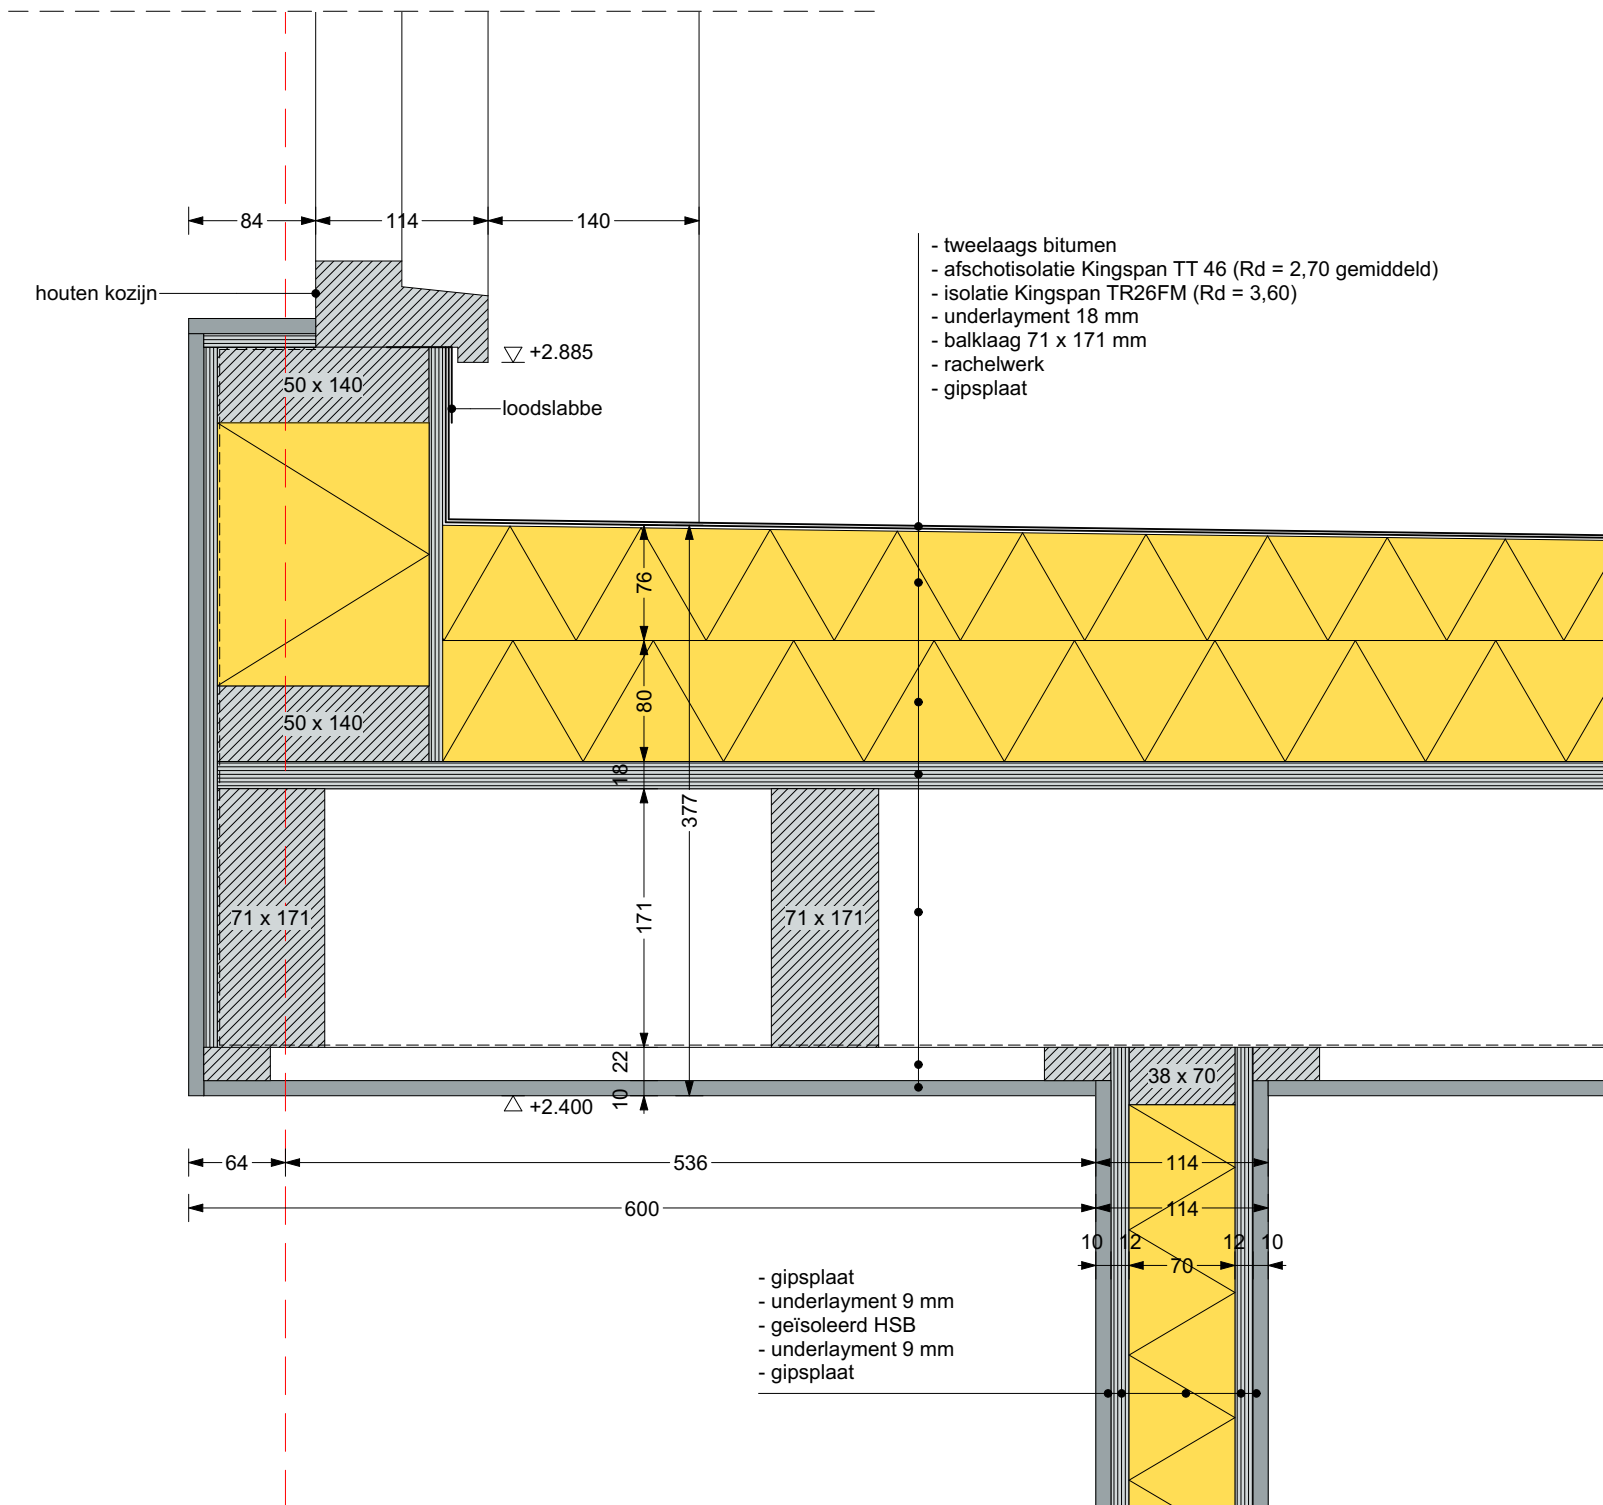


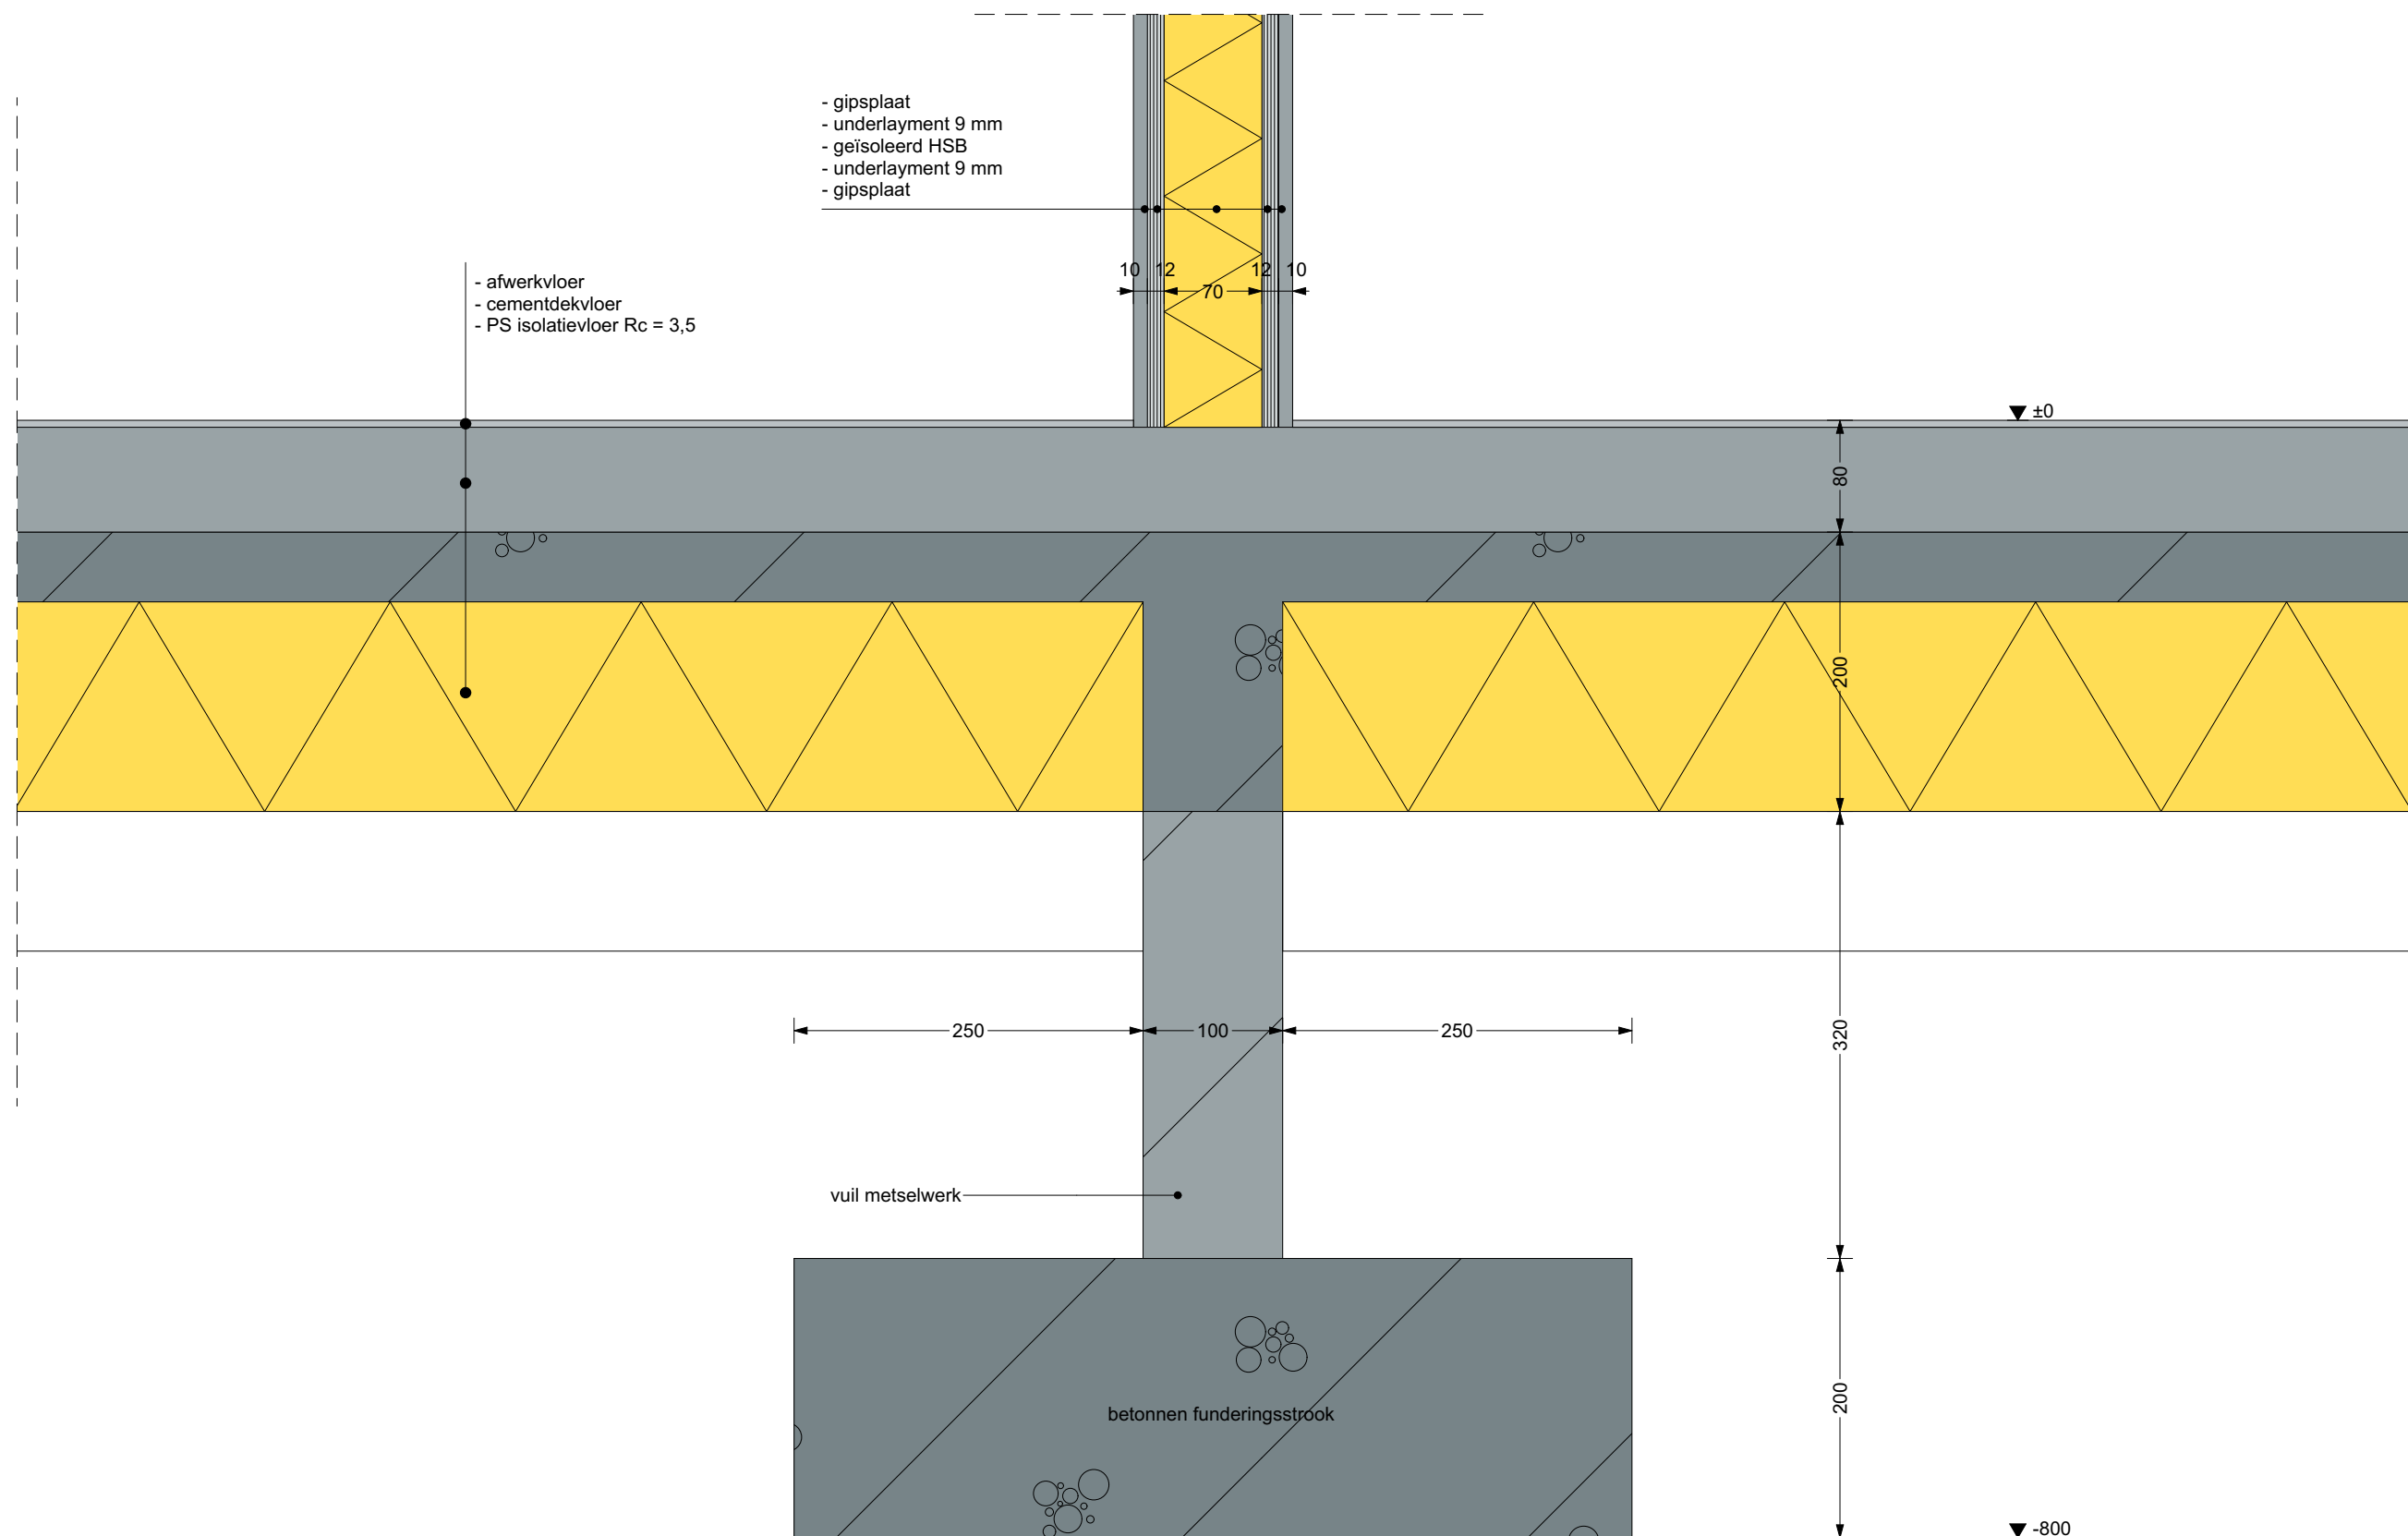


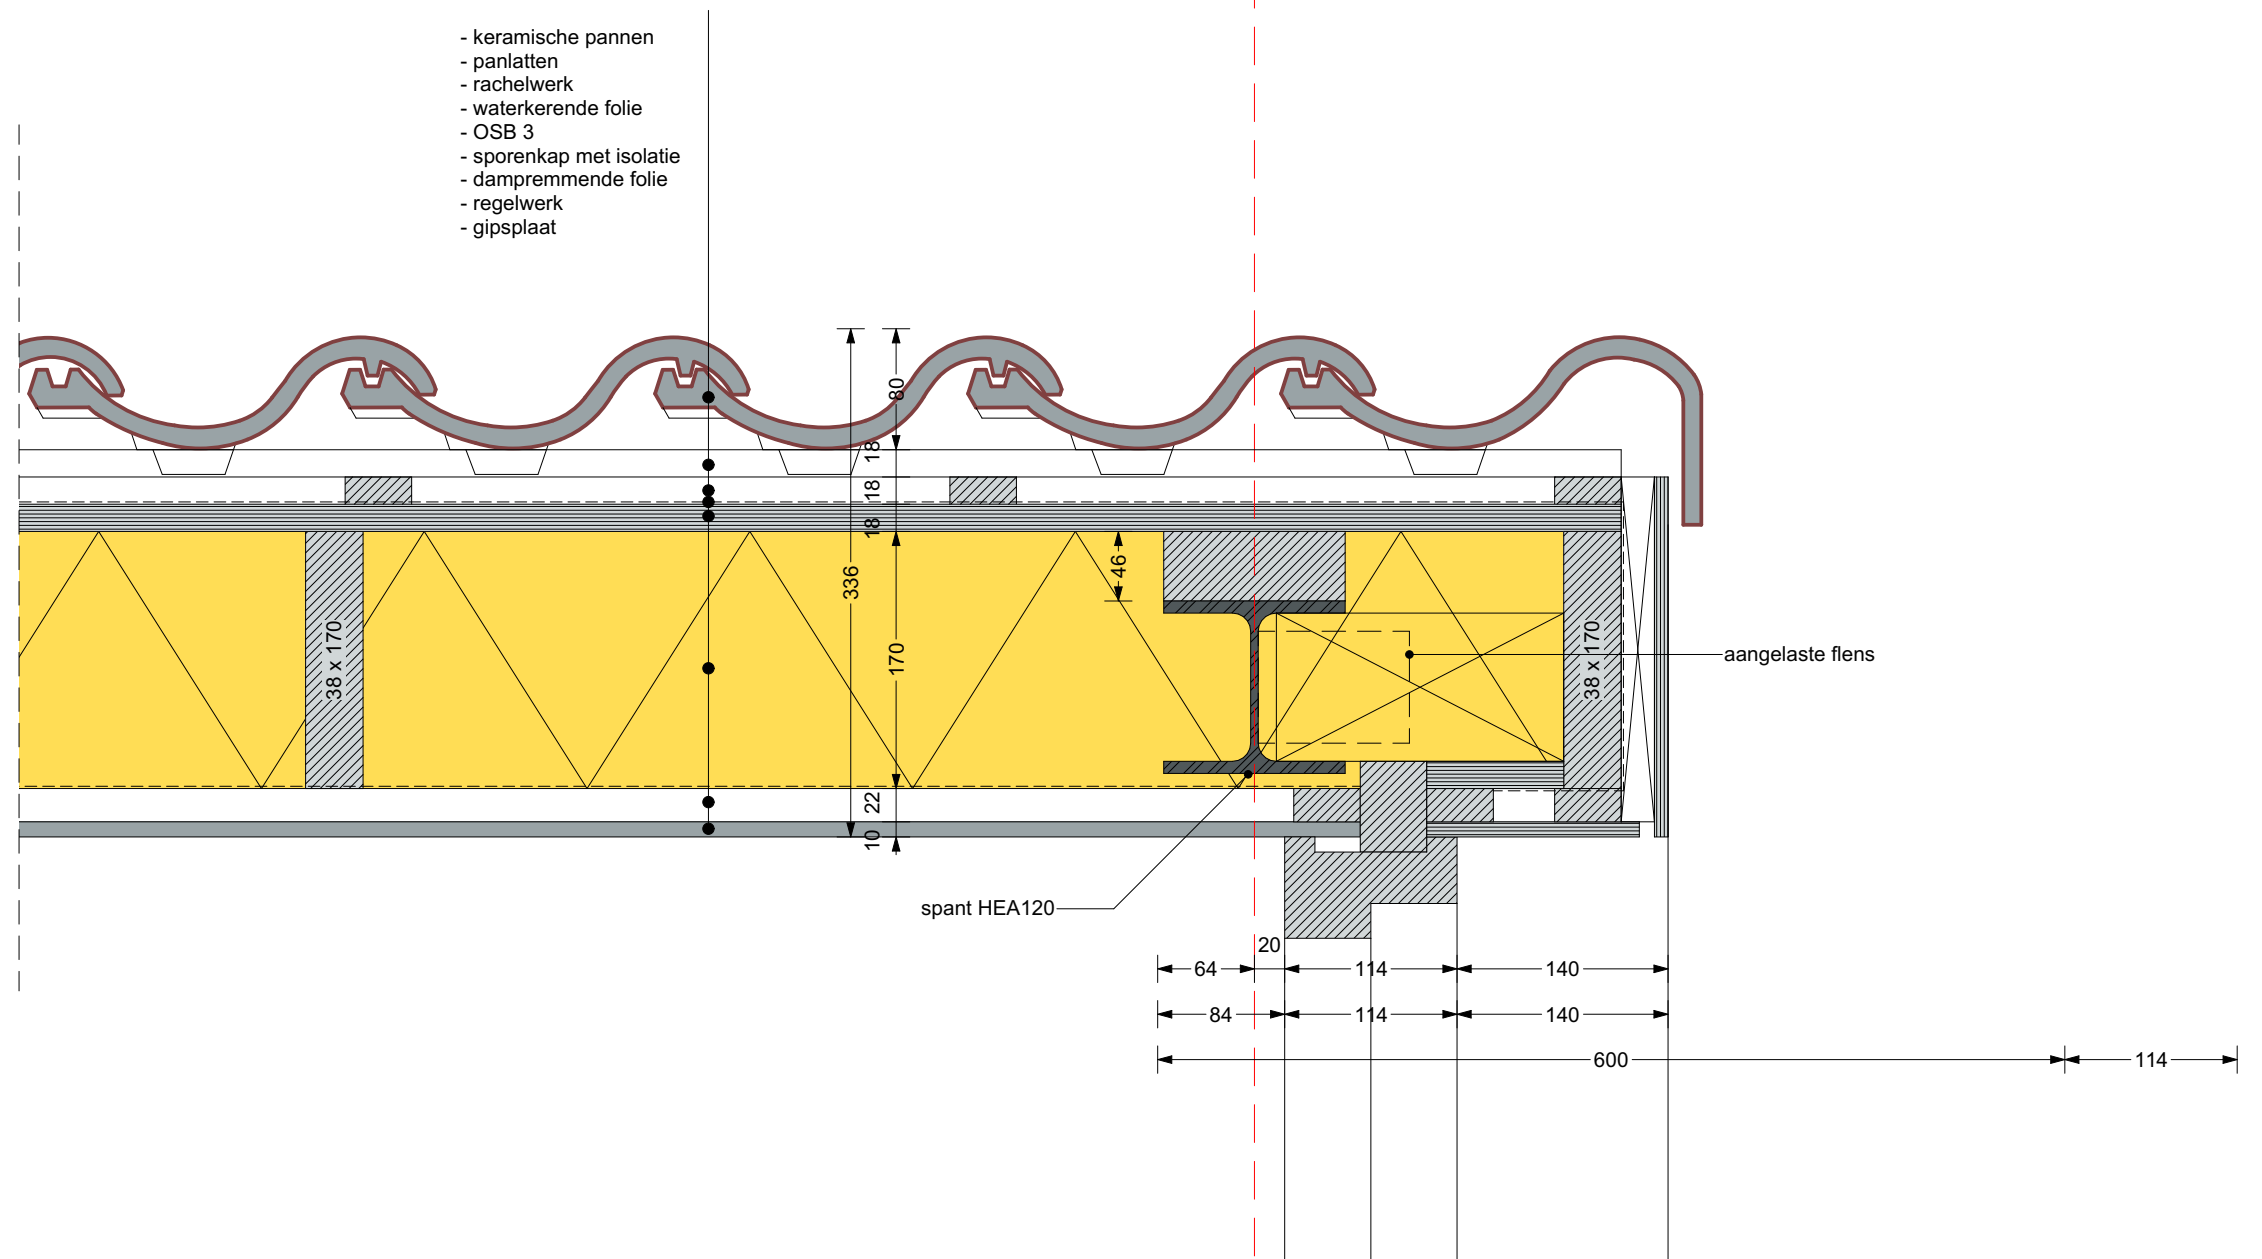


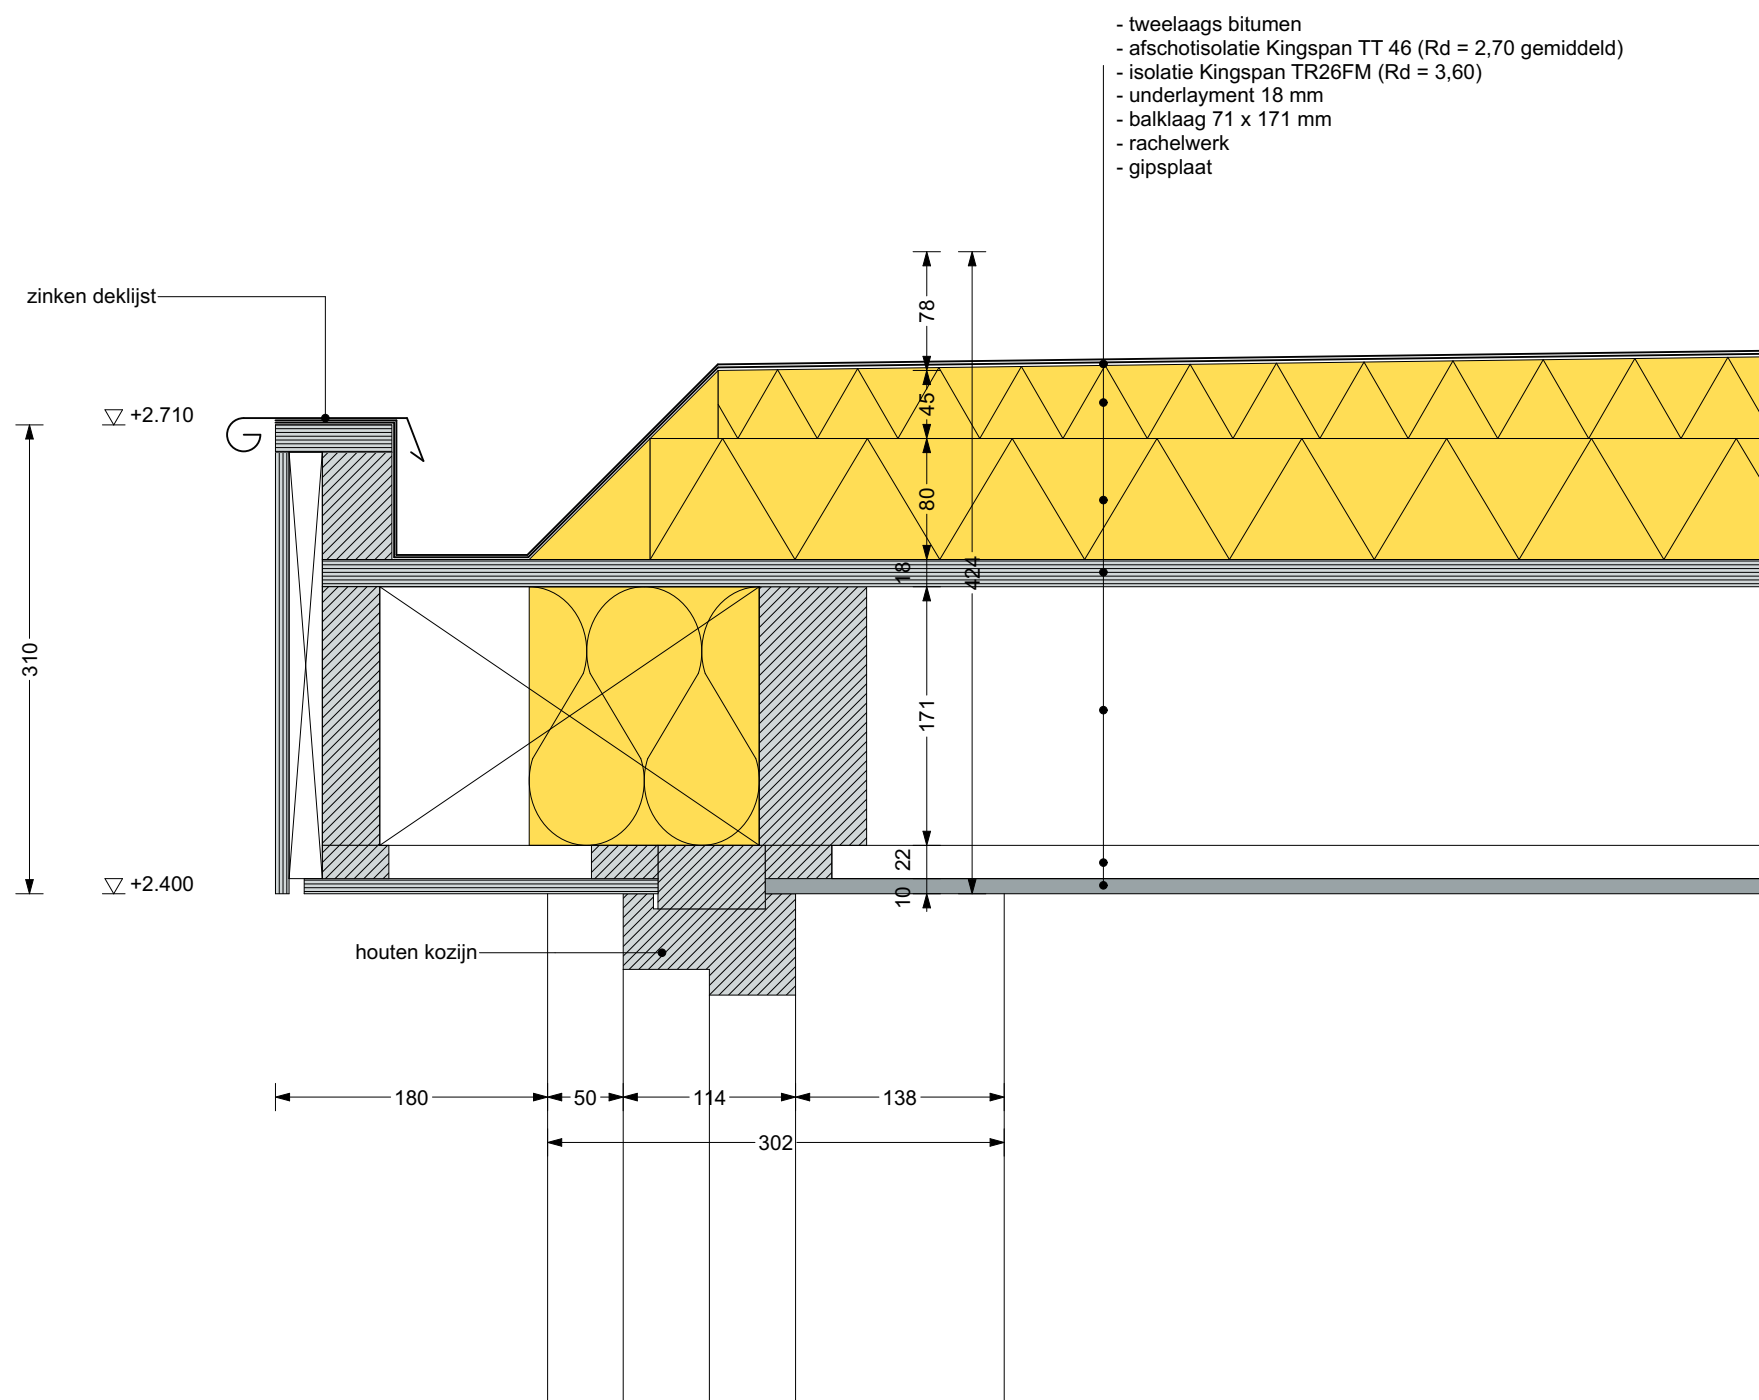


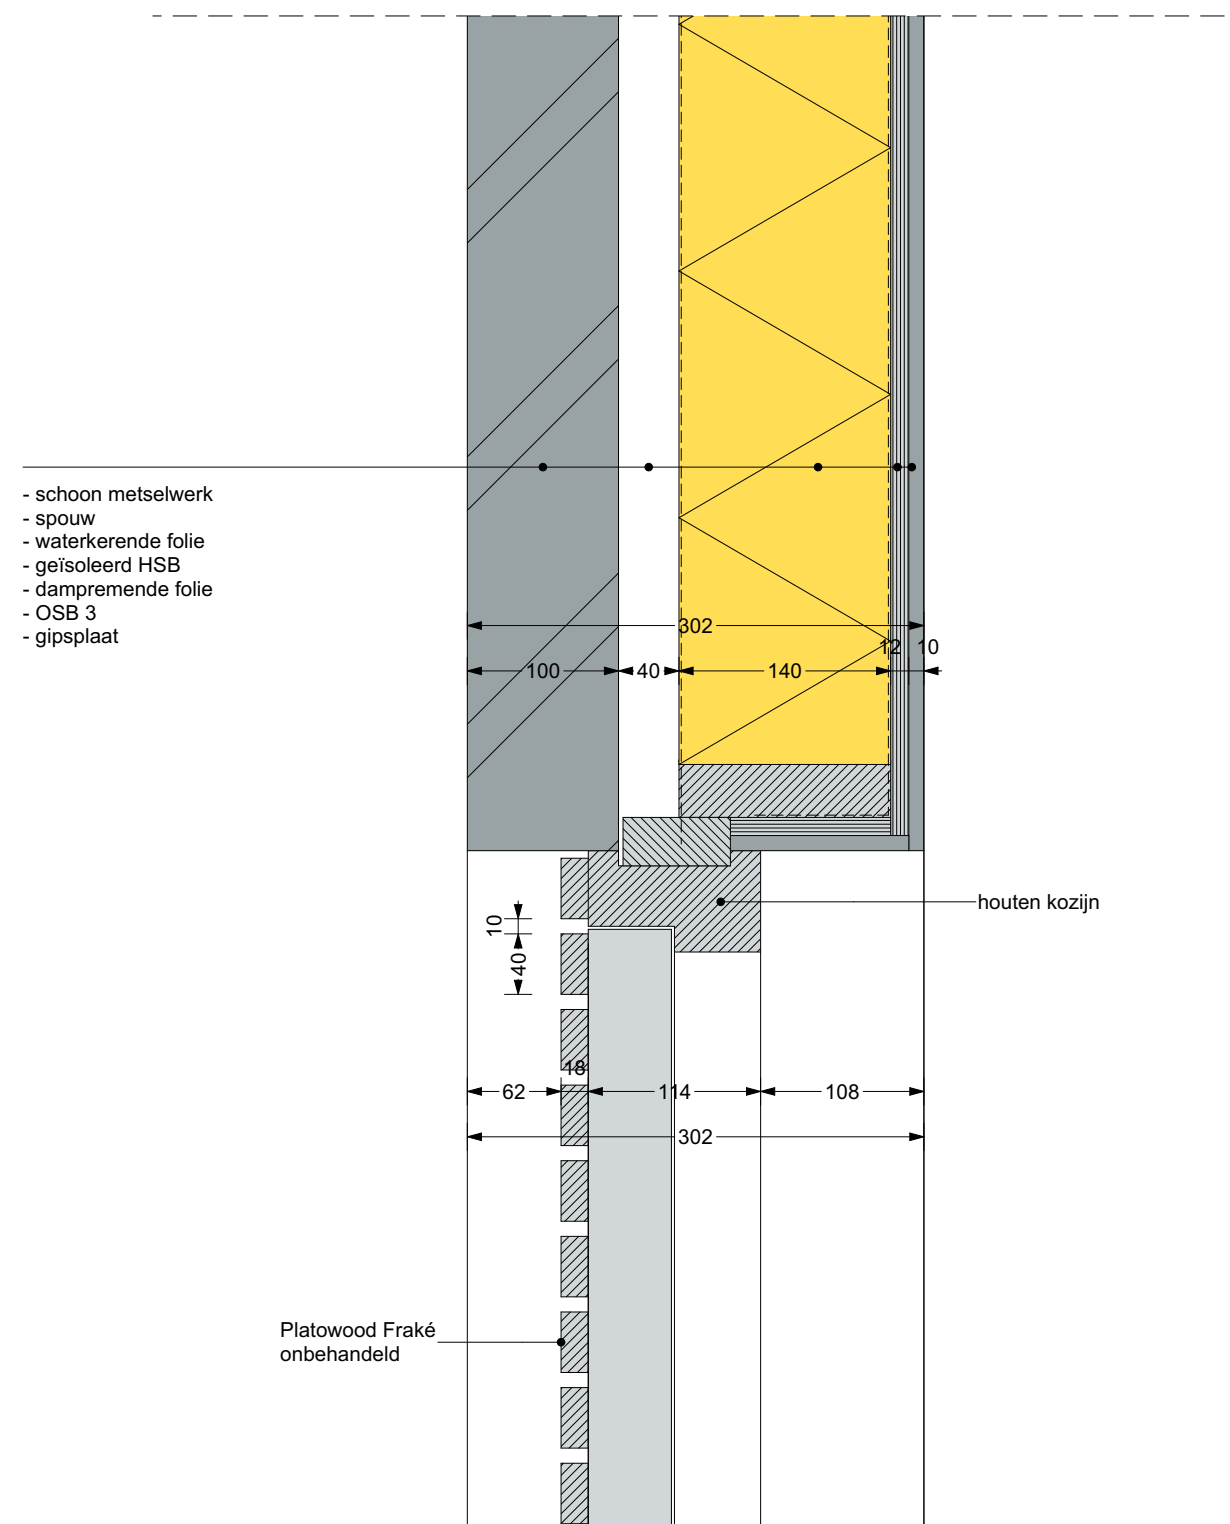


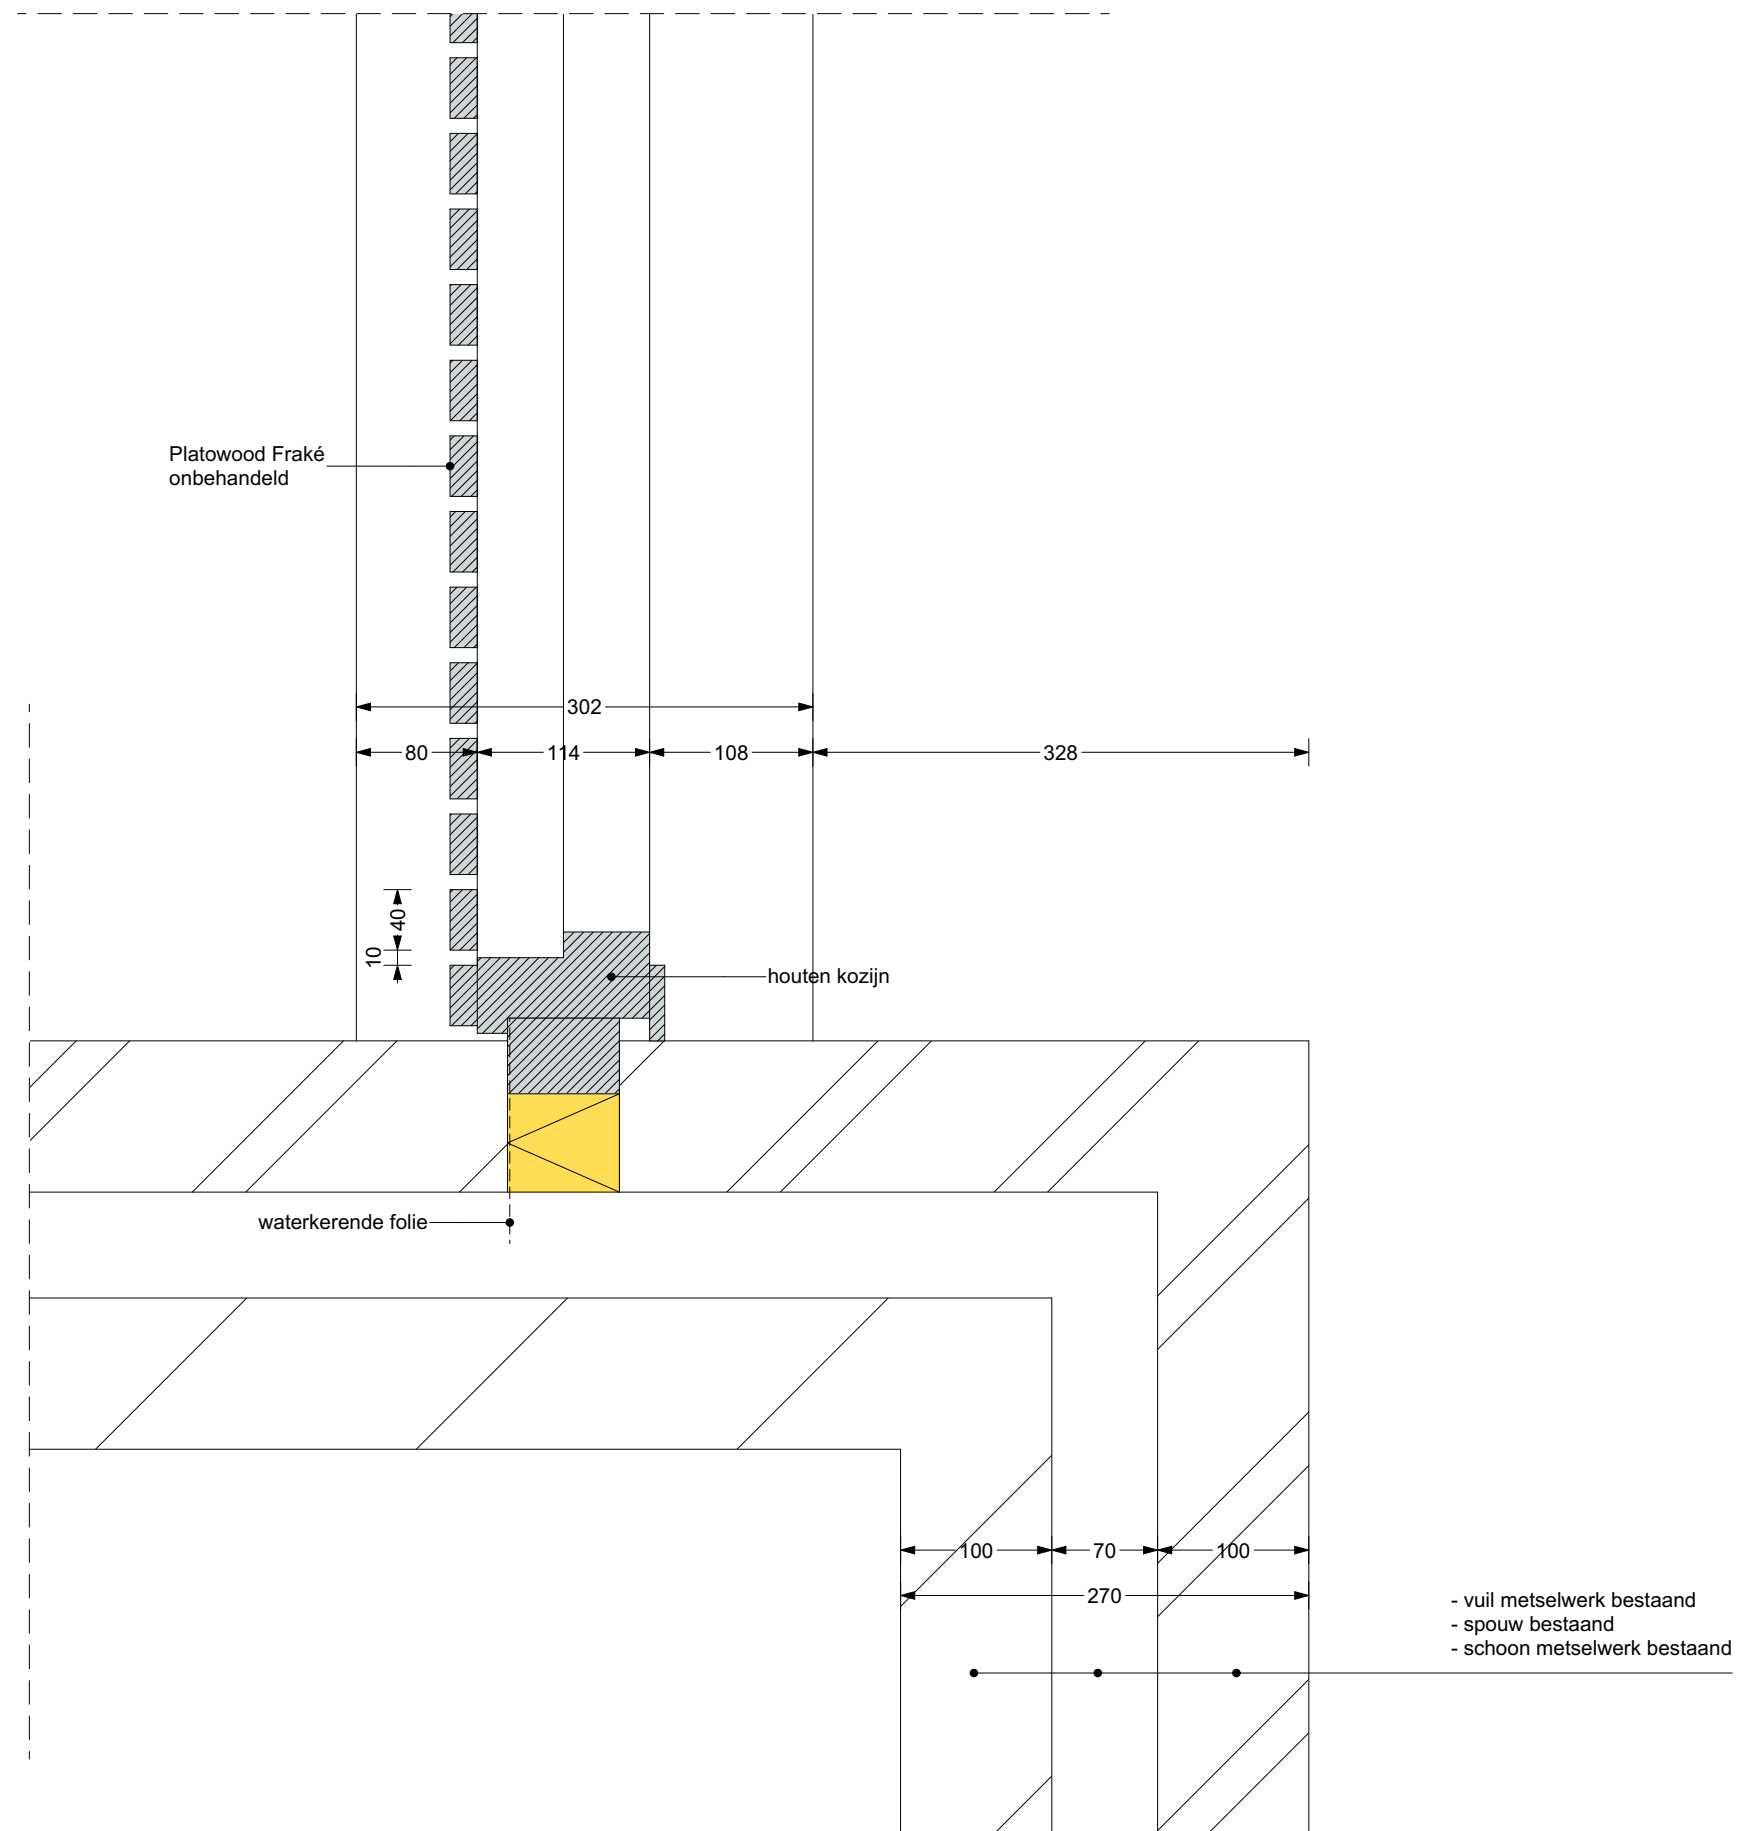


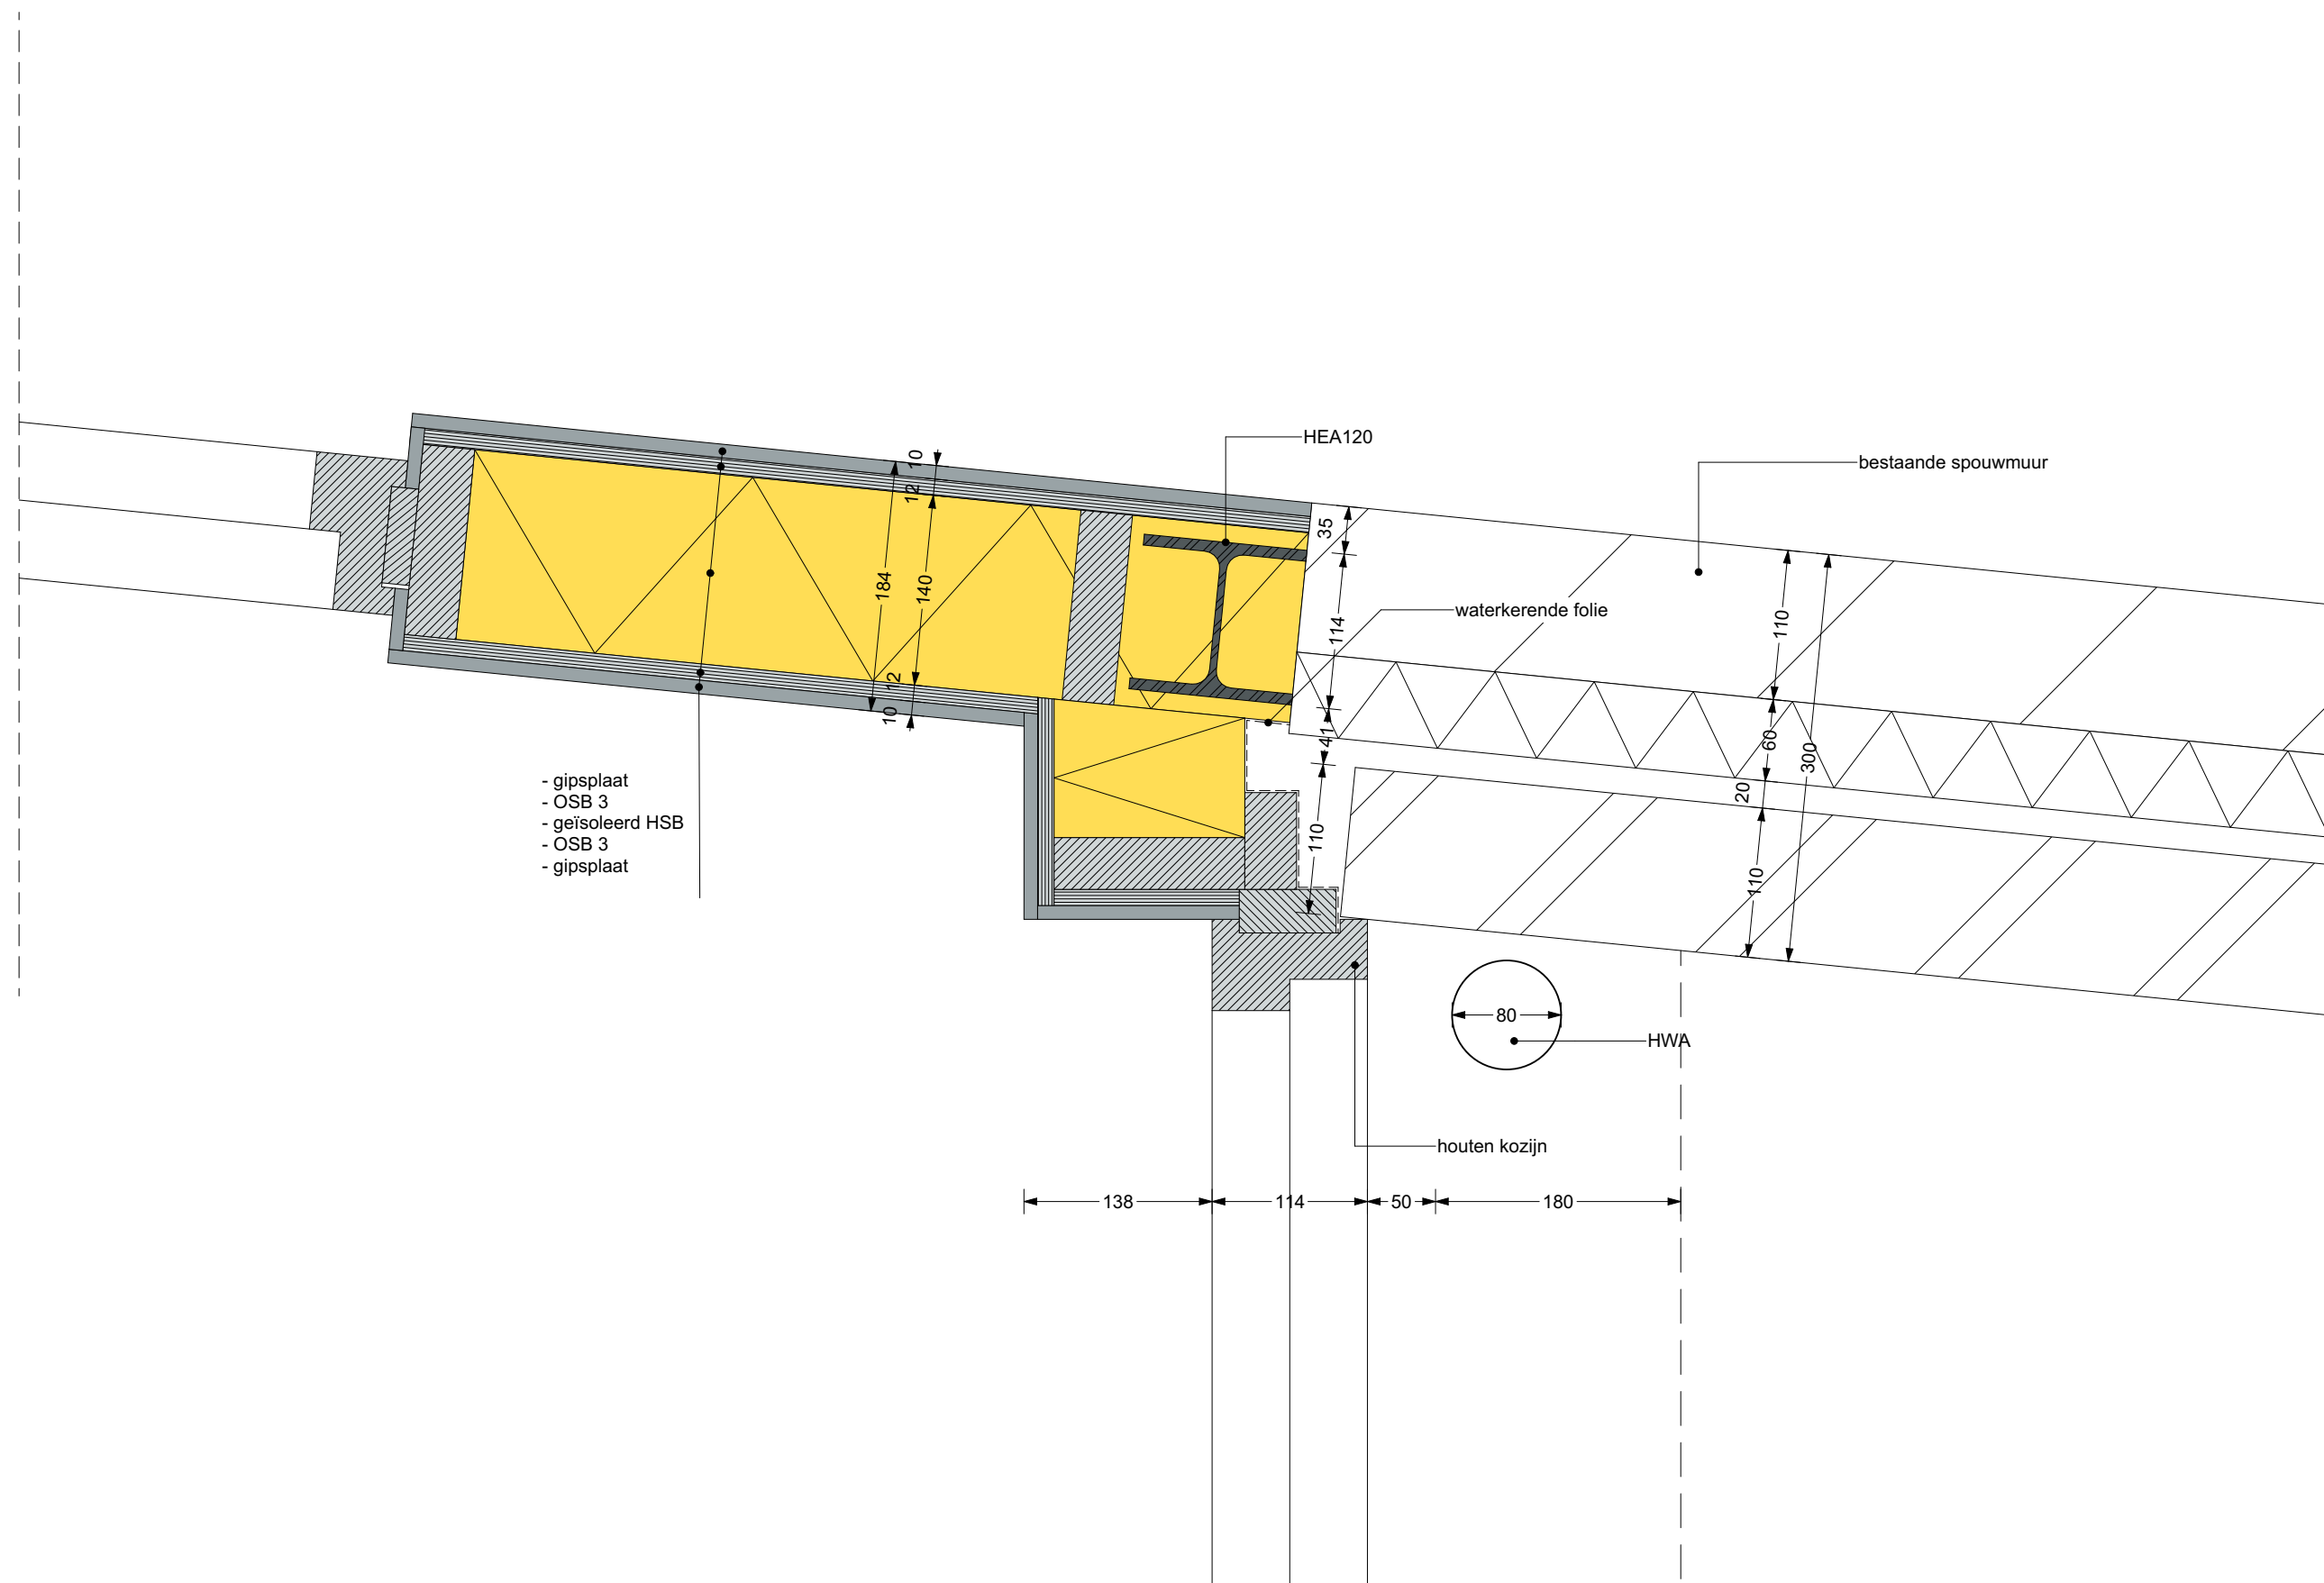

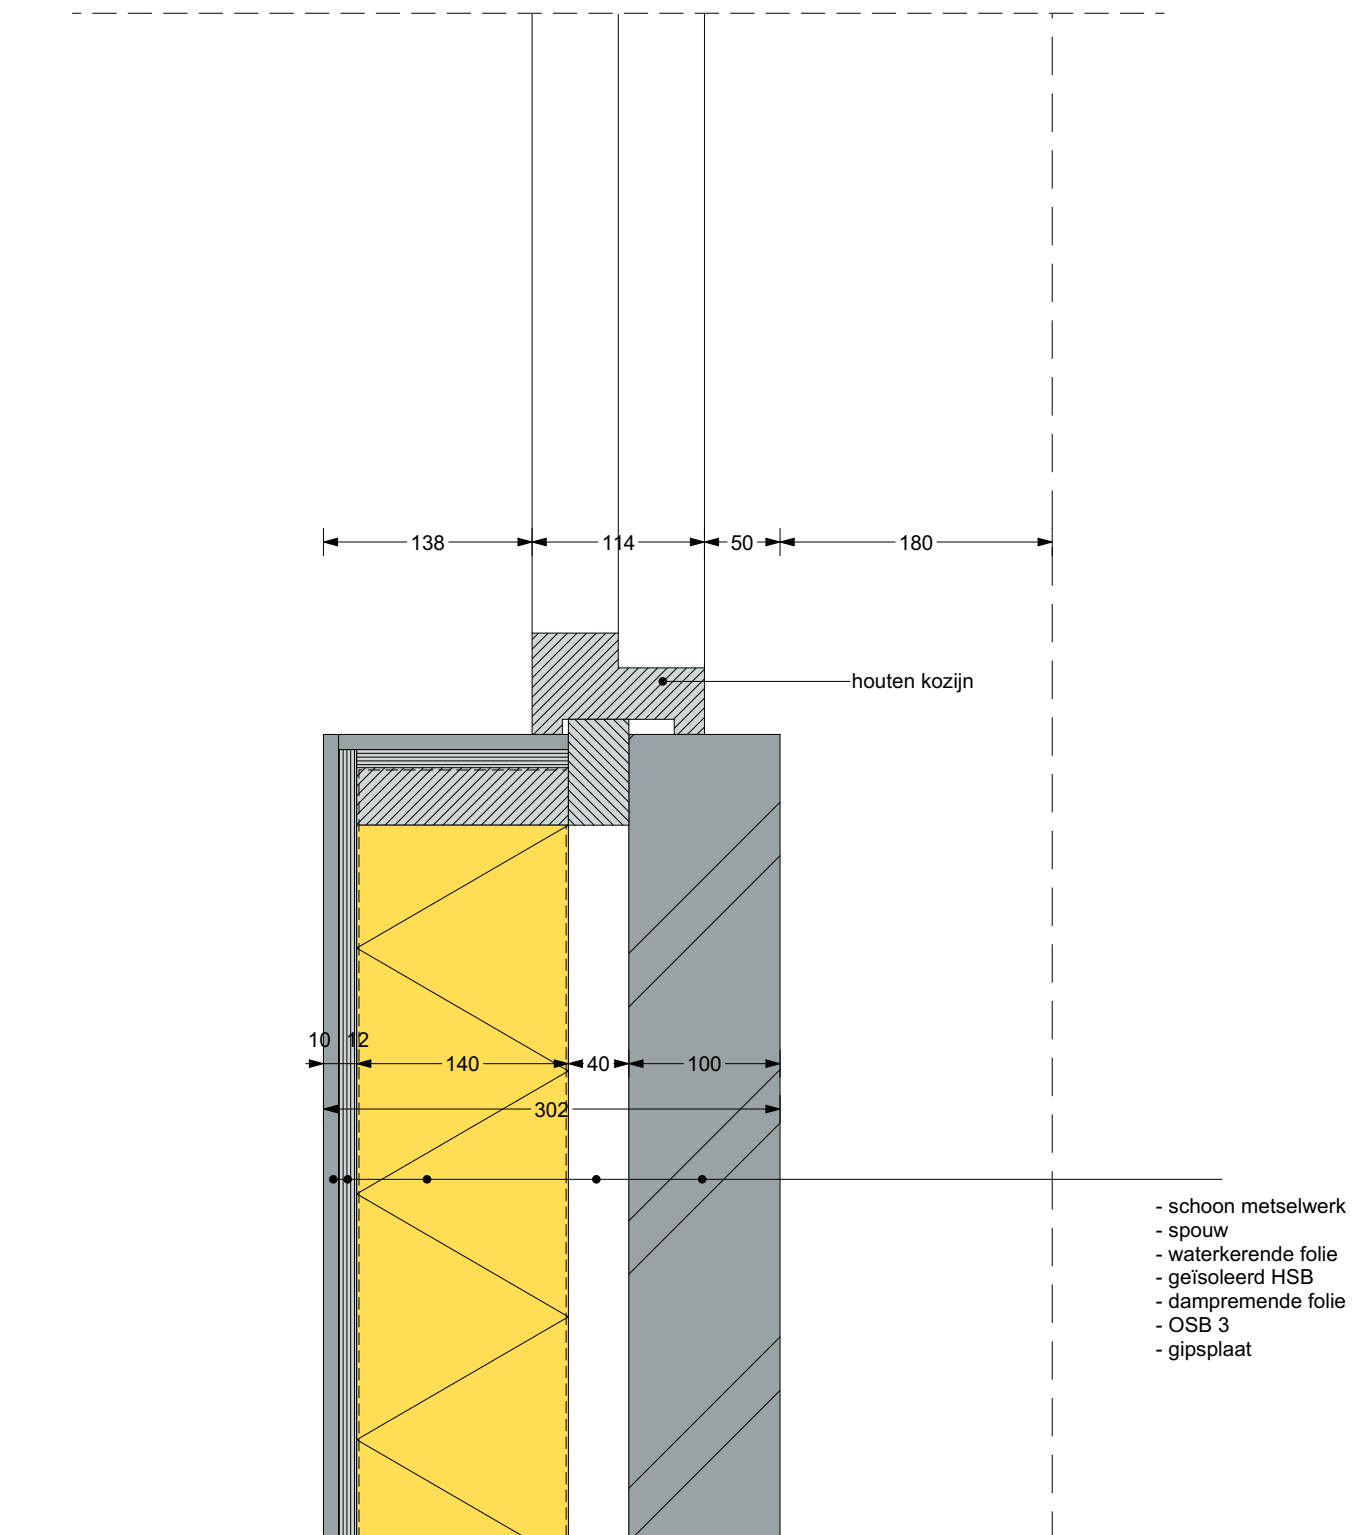

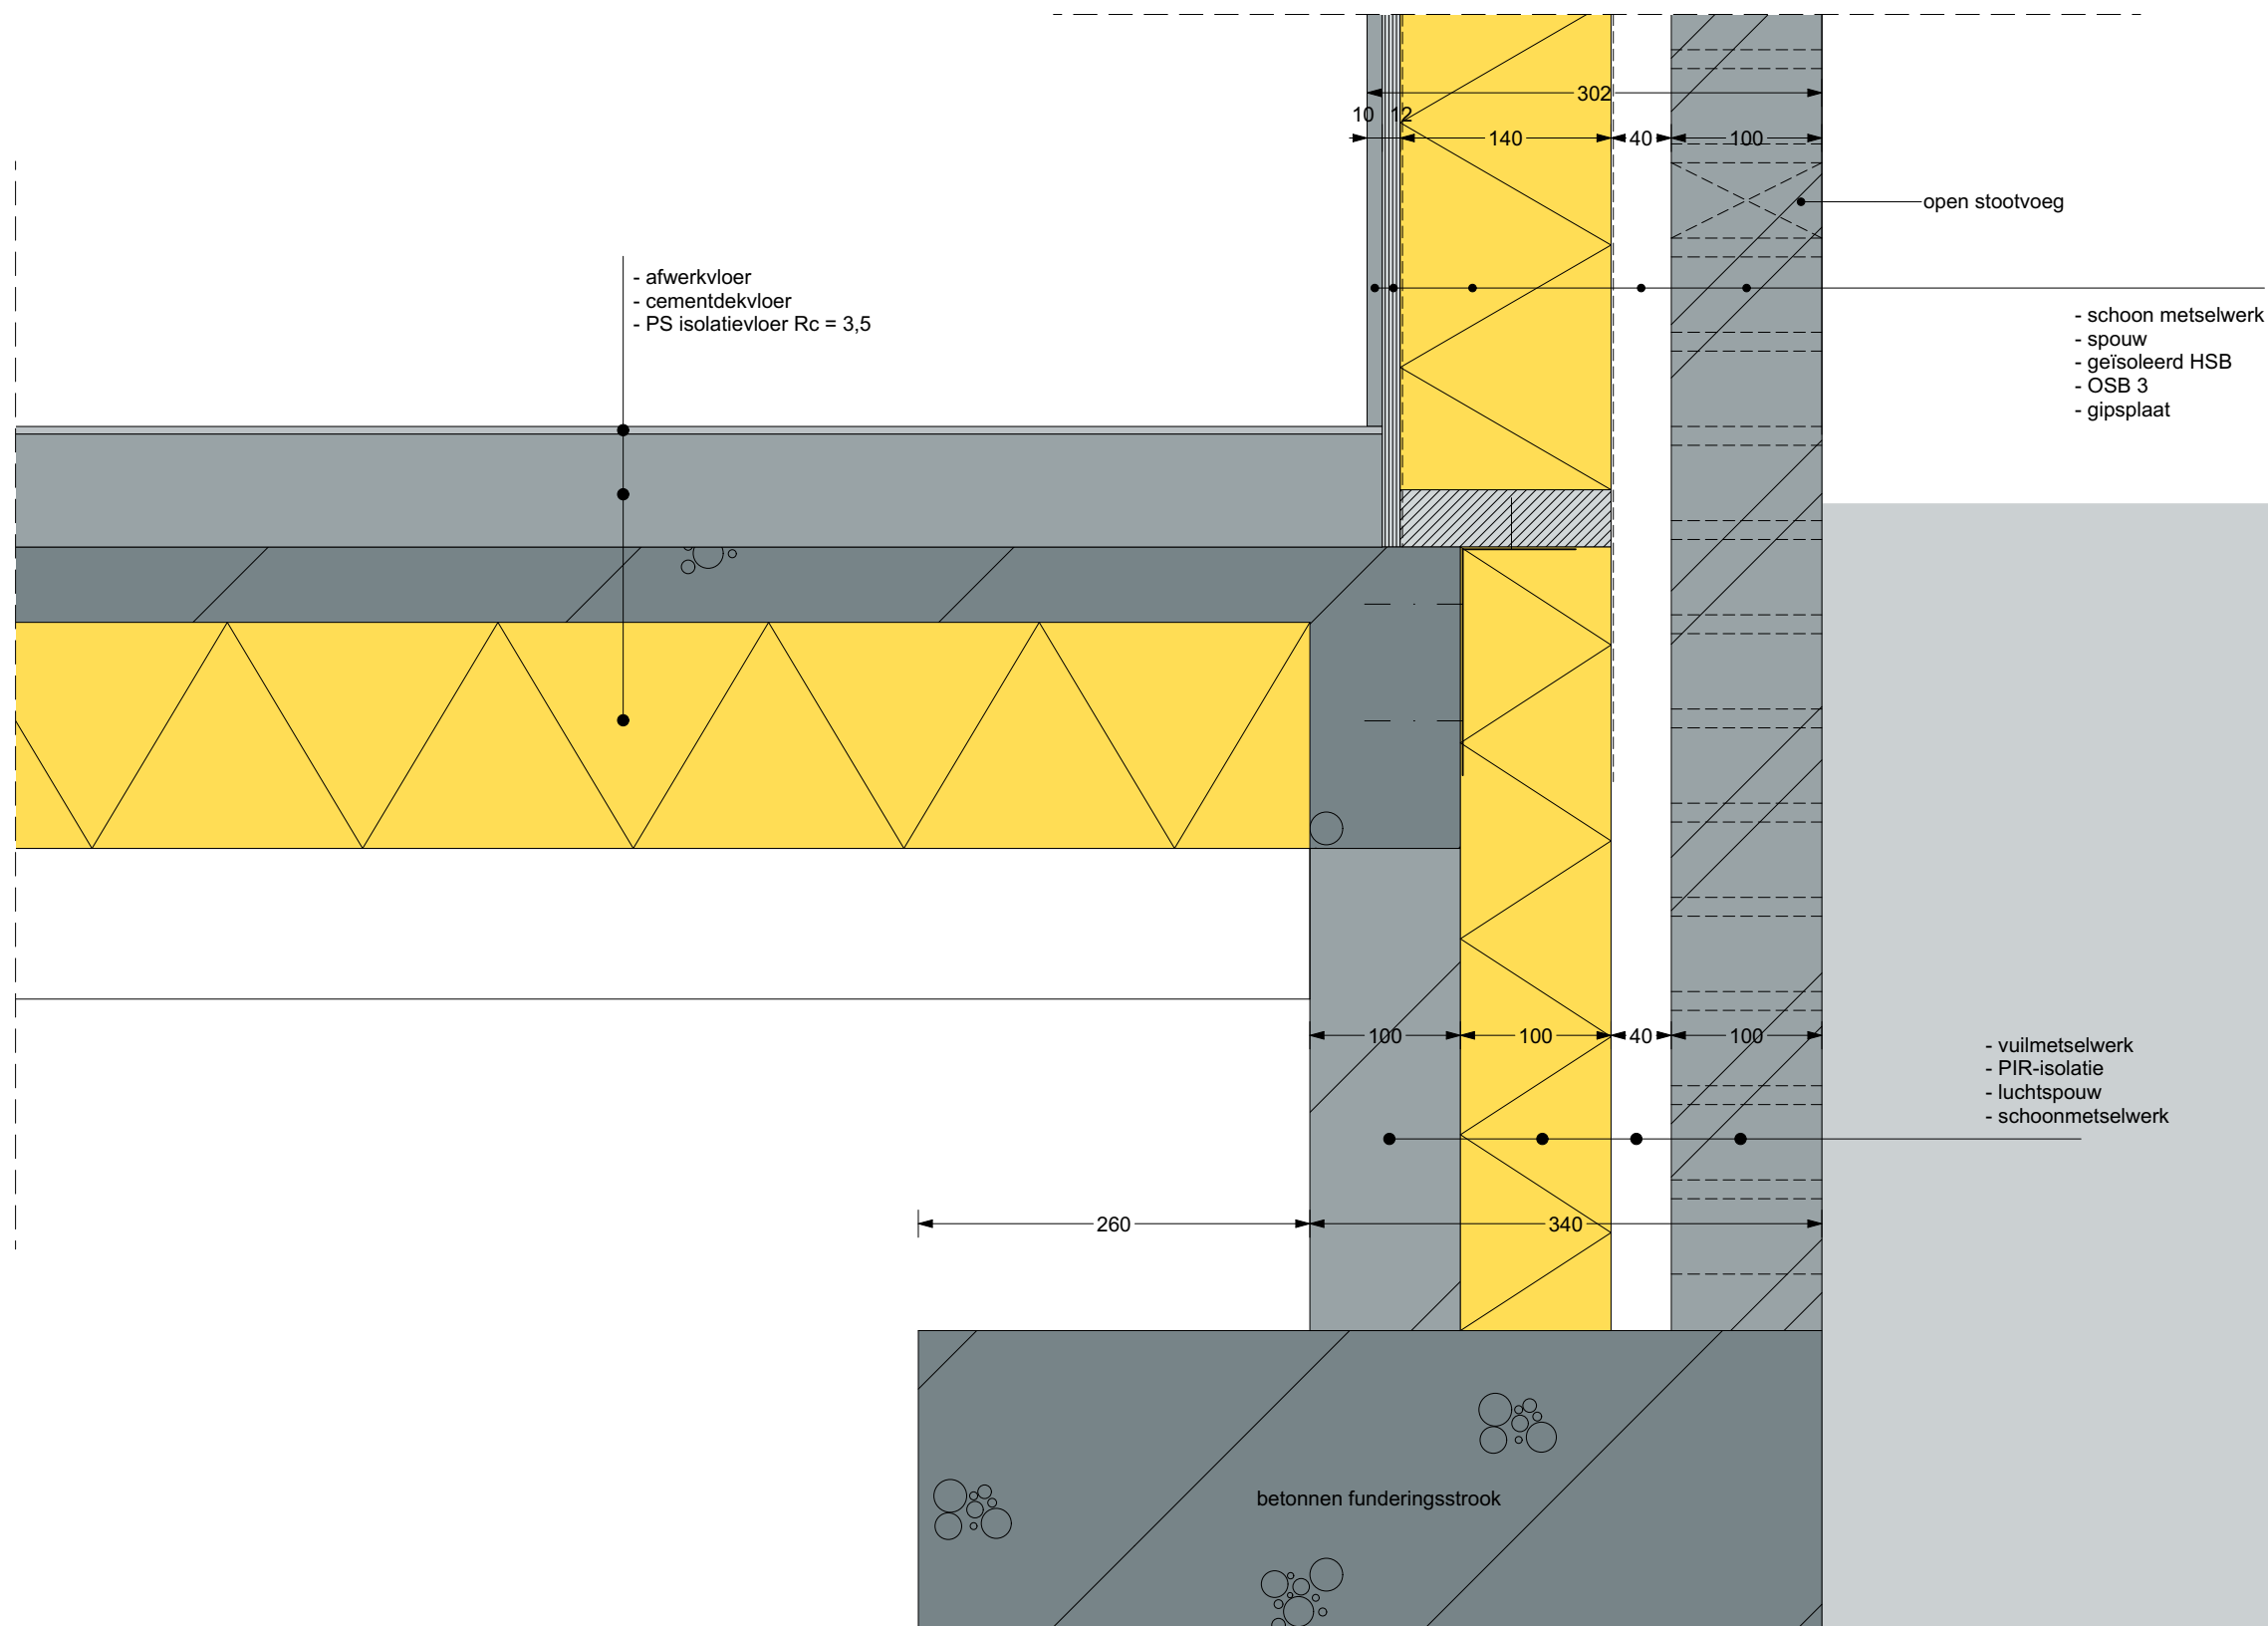

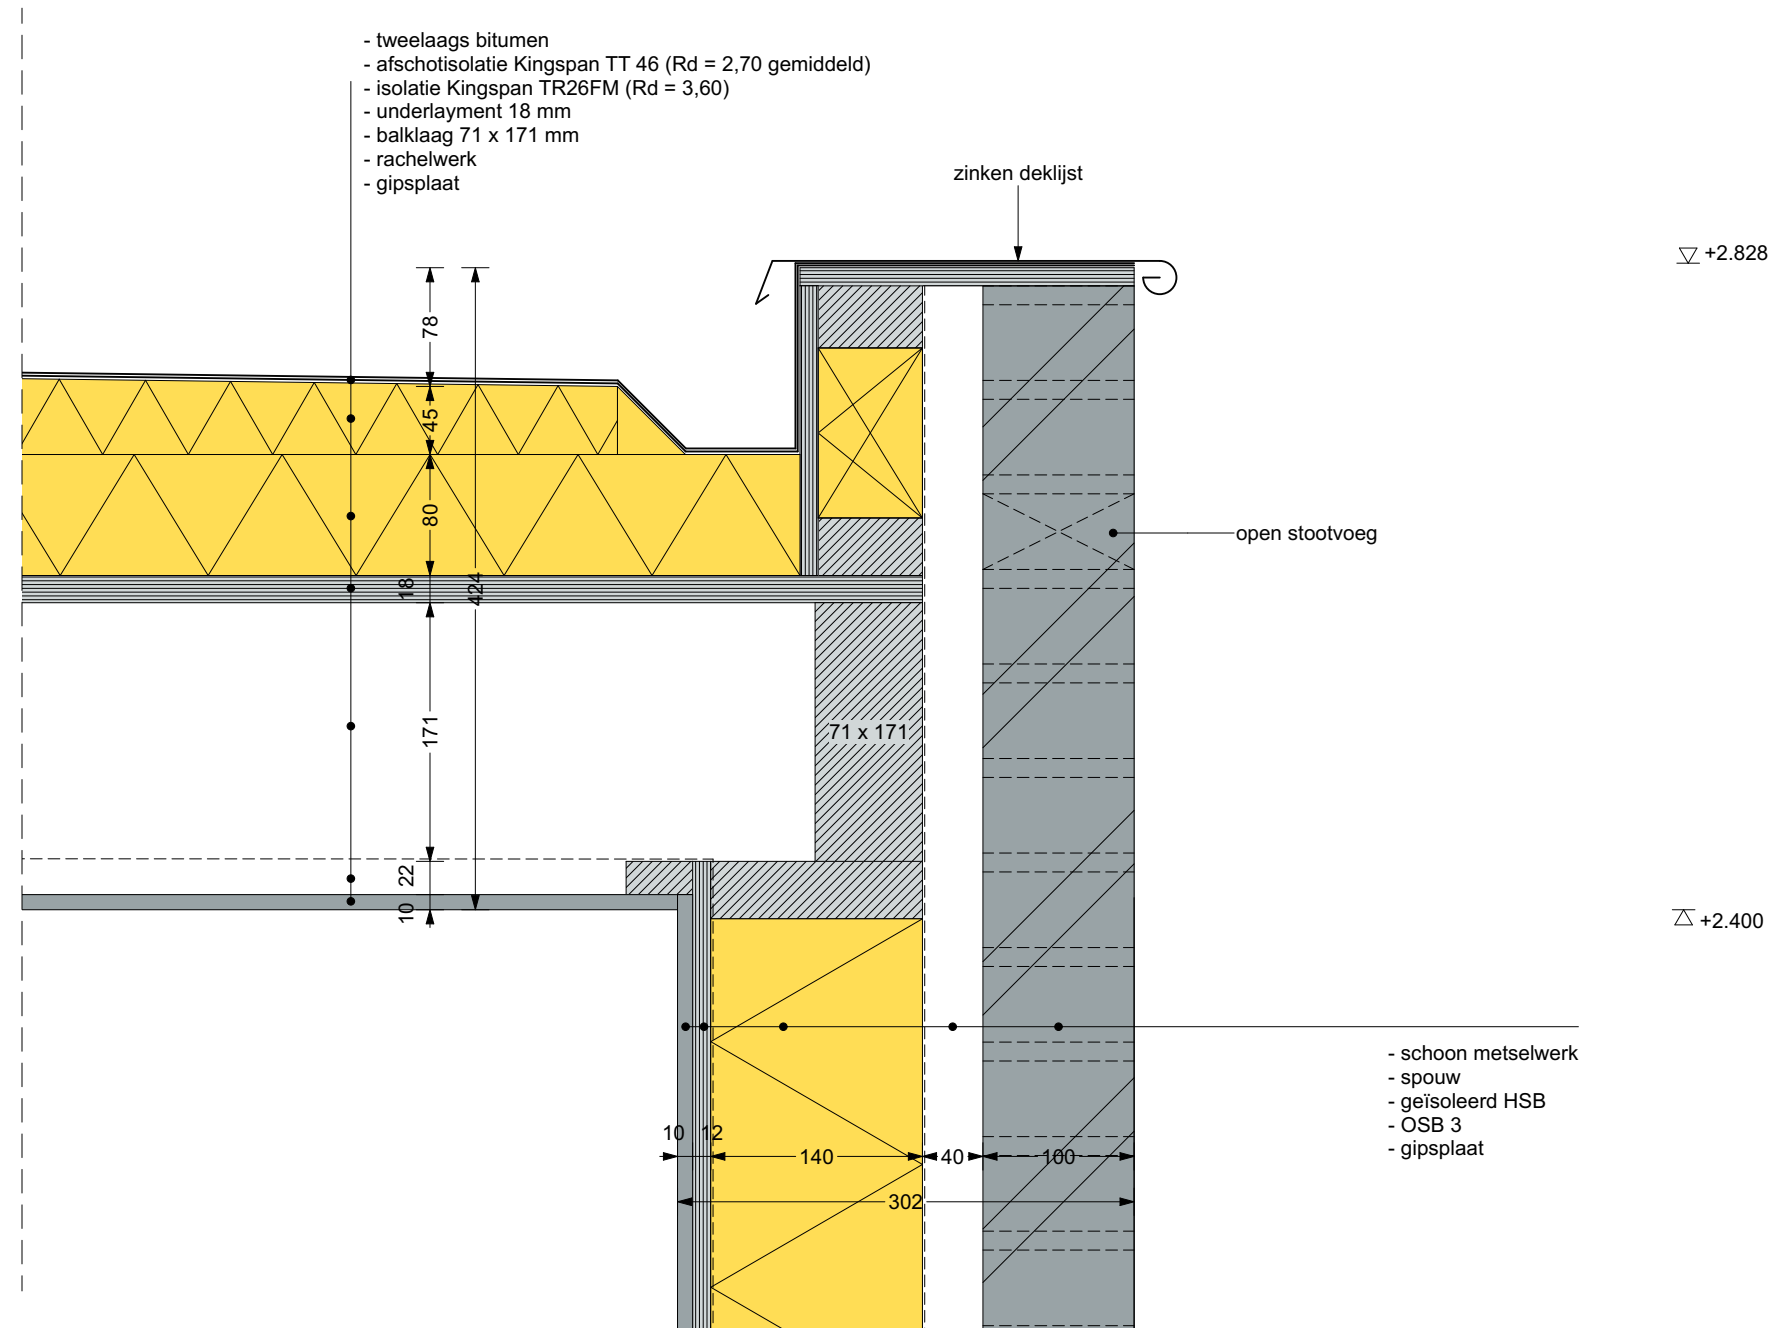

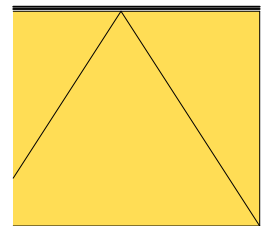

▽ +3.050

▽ +2.750

300

zinken dekljst

tweelaags bitumen

houten kozijn

bestaande dakopbouw
in het werk controleren

71 x 171

71 x 171

350

114

136

100

314

170

22

10



