

Onderwerp	Nieuwbouw woning met aangrenzend bijgebouw aan de Zevenmorgen 26 te Ingen
Opdrachtgever	Familie van Toorn
Bouwlocatie	Zevenmorgen 26 te Ingen

Werk nr	W 20.1850
Formaat	A 3
Tek nr	1850-03

Blad	Principe details
Status	AANVRAAG OMGEVINGSVERGUNNING
Datum	24-2-2022

Schaal	1 : 10
Getekend	AvdB
Gewijzigd	



BVB
BURO VAN BLIJDERVEEN

Rijnstraat 7


4031 KJ INGEN

T 0344-606686

F 0344-600811

I info@burovanblijderveen.nl

W www.burovanblijderveen.nl

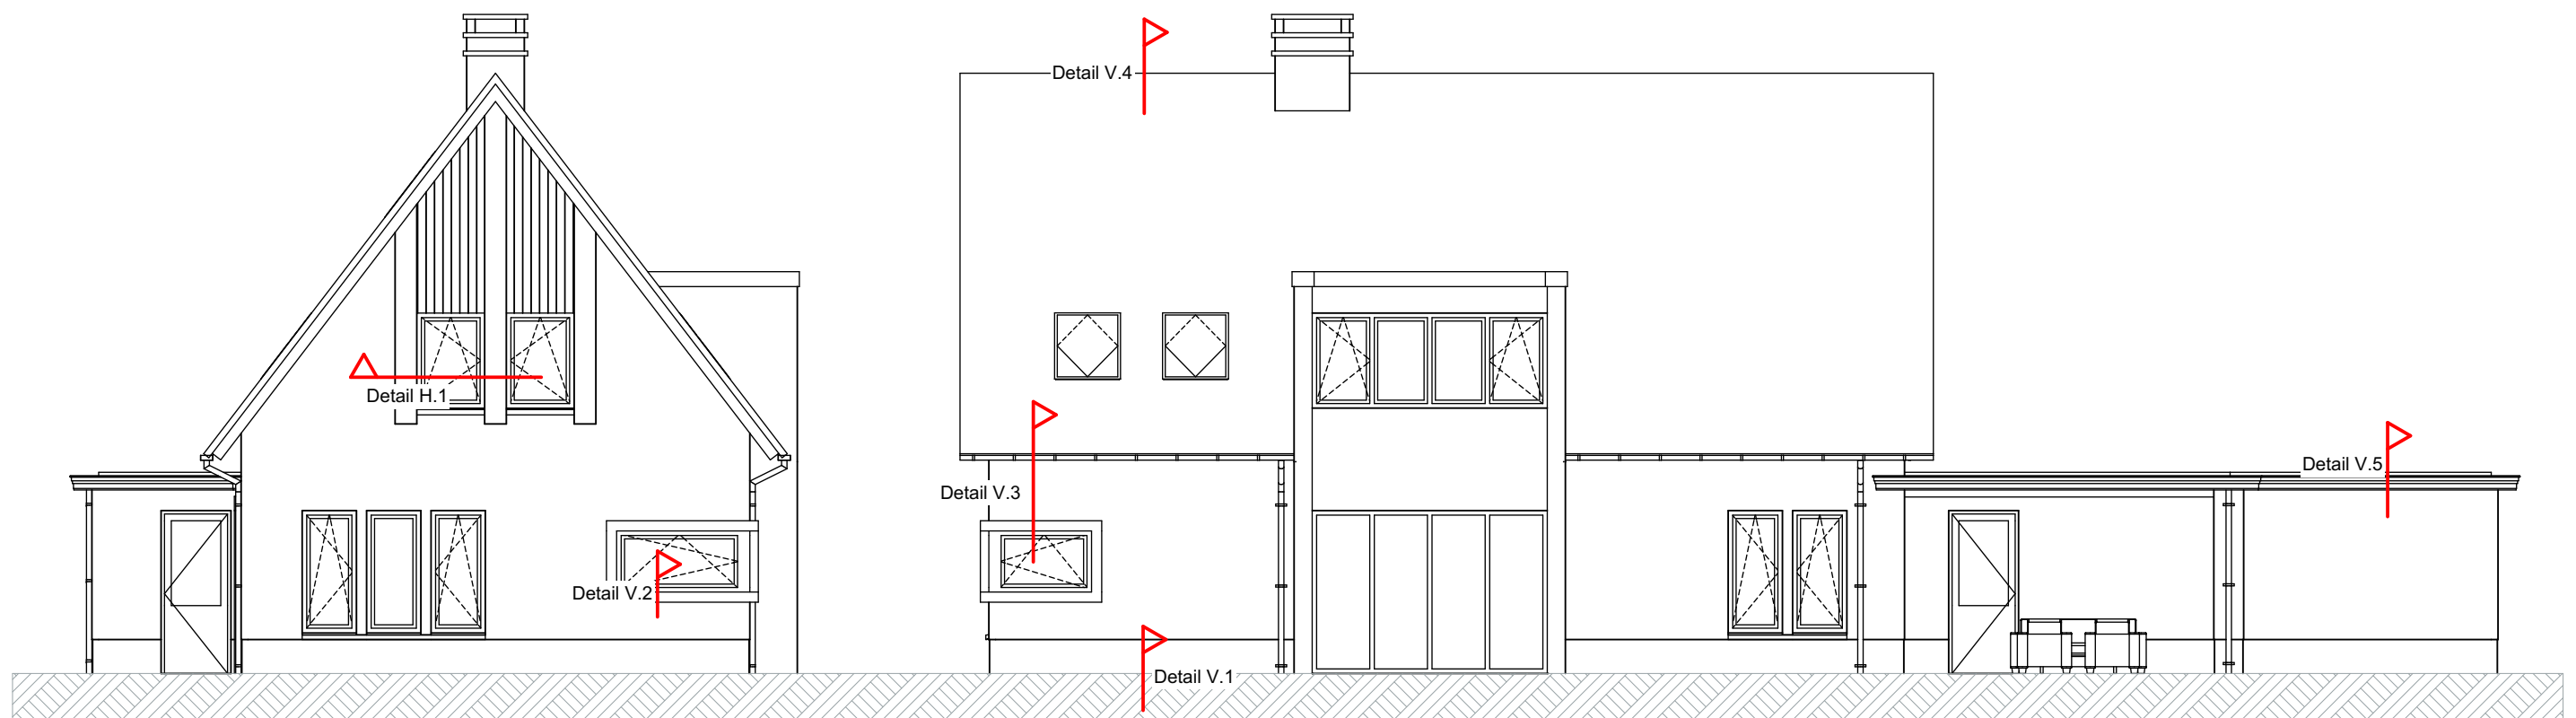

Voorgevel

Rechtergevel

Project
Nieuwbouw woning met aangrenzend bijgebouw aan de Zevenmorgen 26 te Ingen


Werk nr
W 20.1850

Datum
01-07-2021


Gewijzigd
21-07-2021



Rijnstraat 7
4031 KJ INGEN
T 0344-606686
F 0344-600811
I info@burovanblijderveen.nl
W www.burovanblijderveen.nl

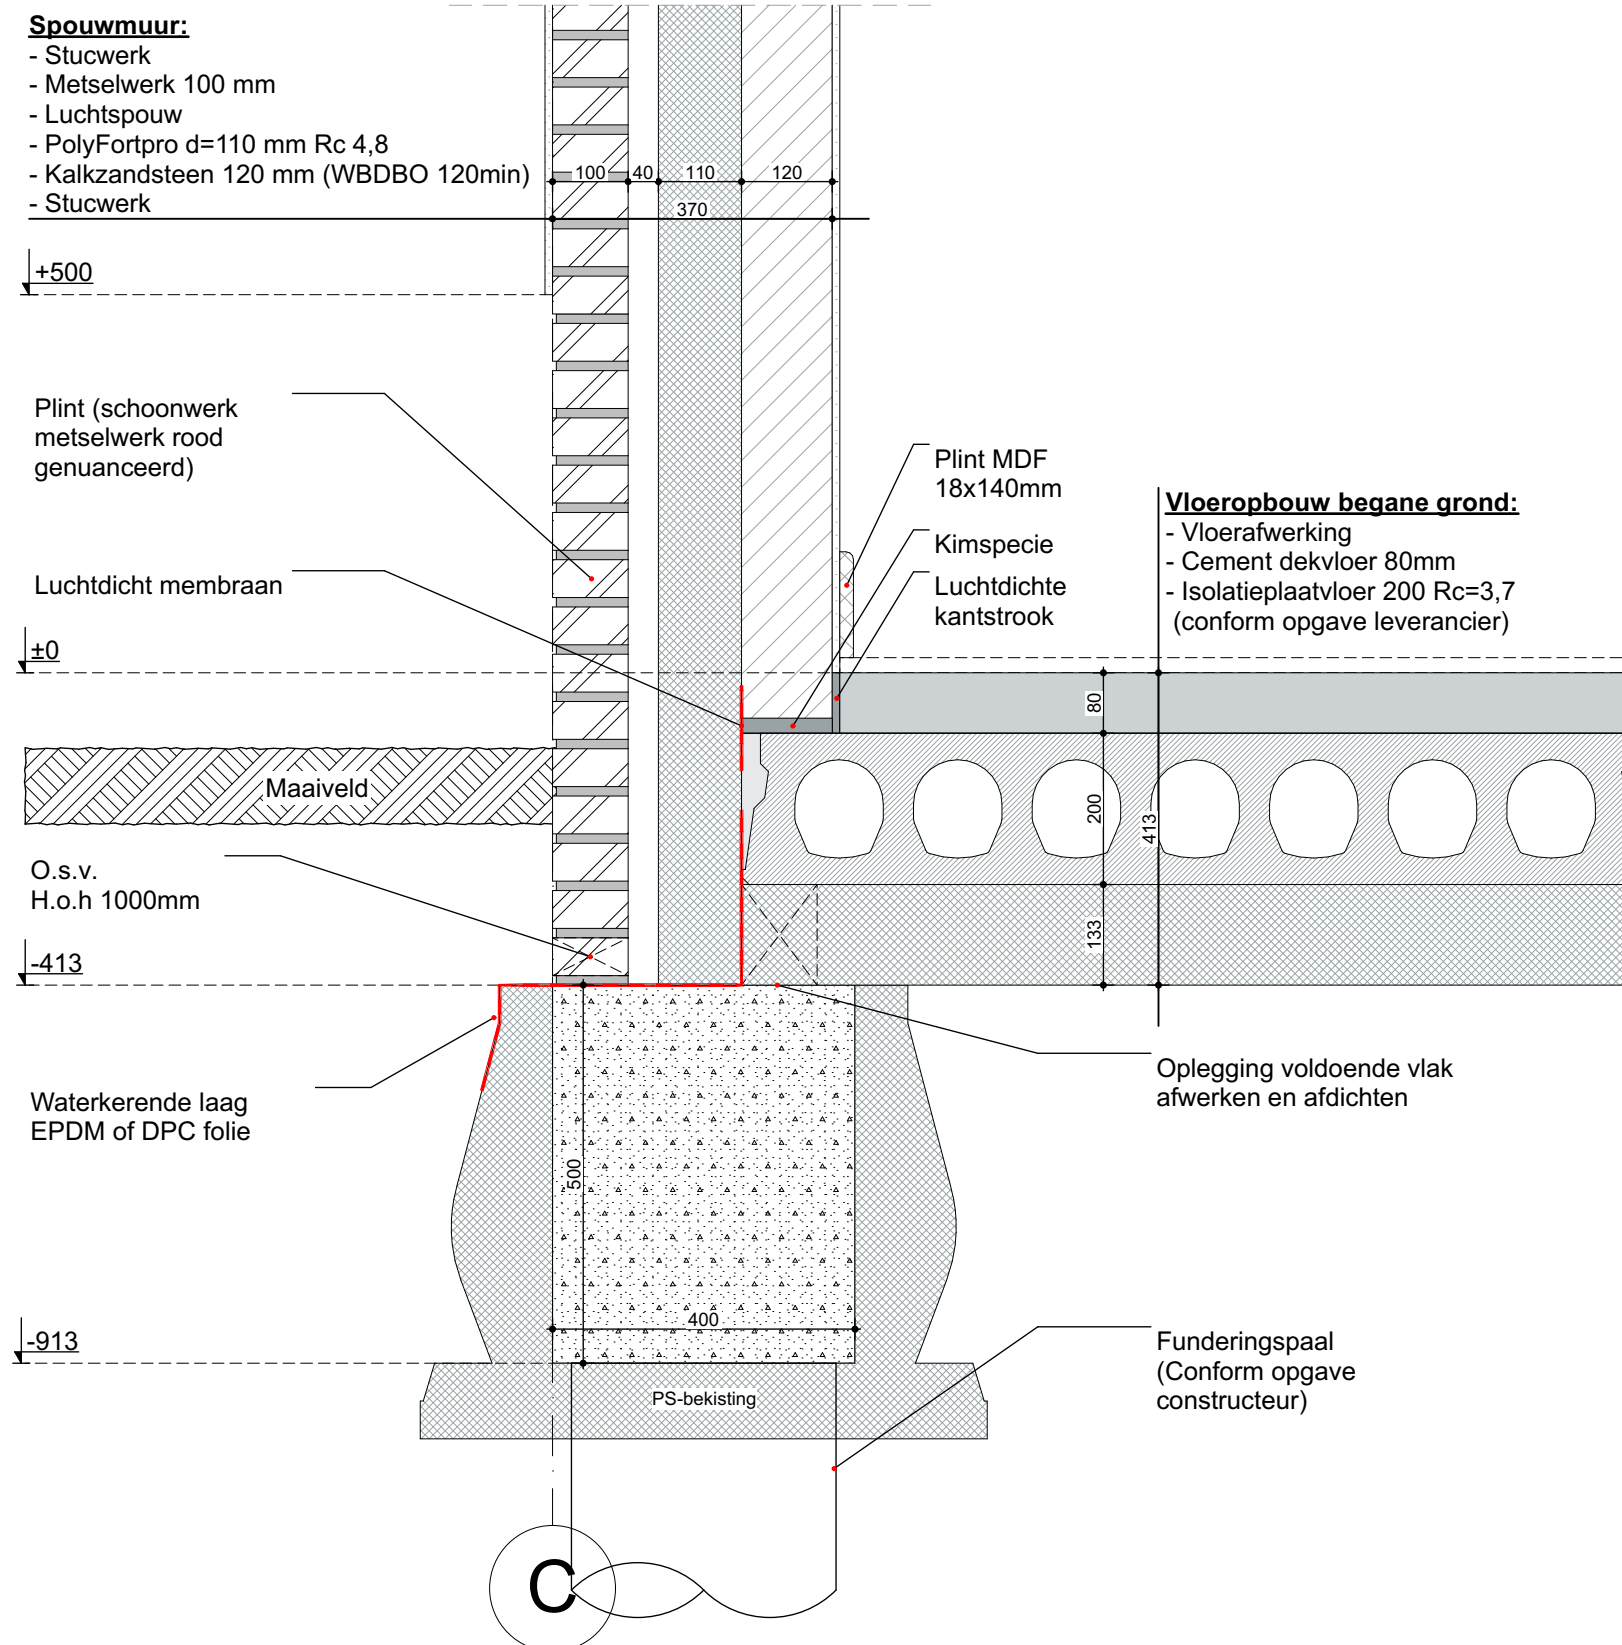

Detail V.1

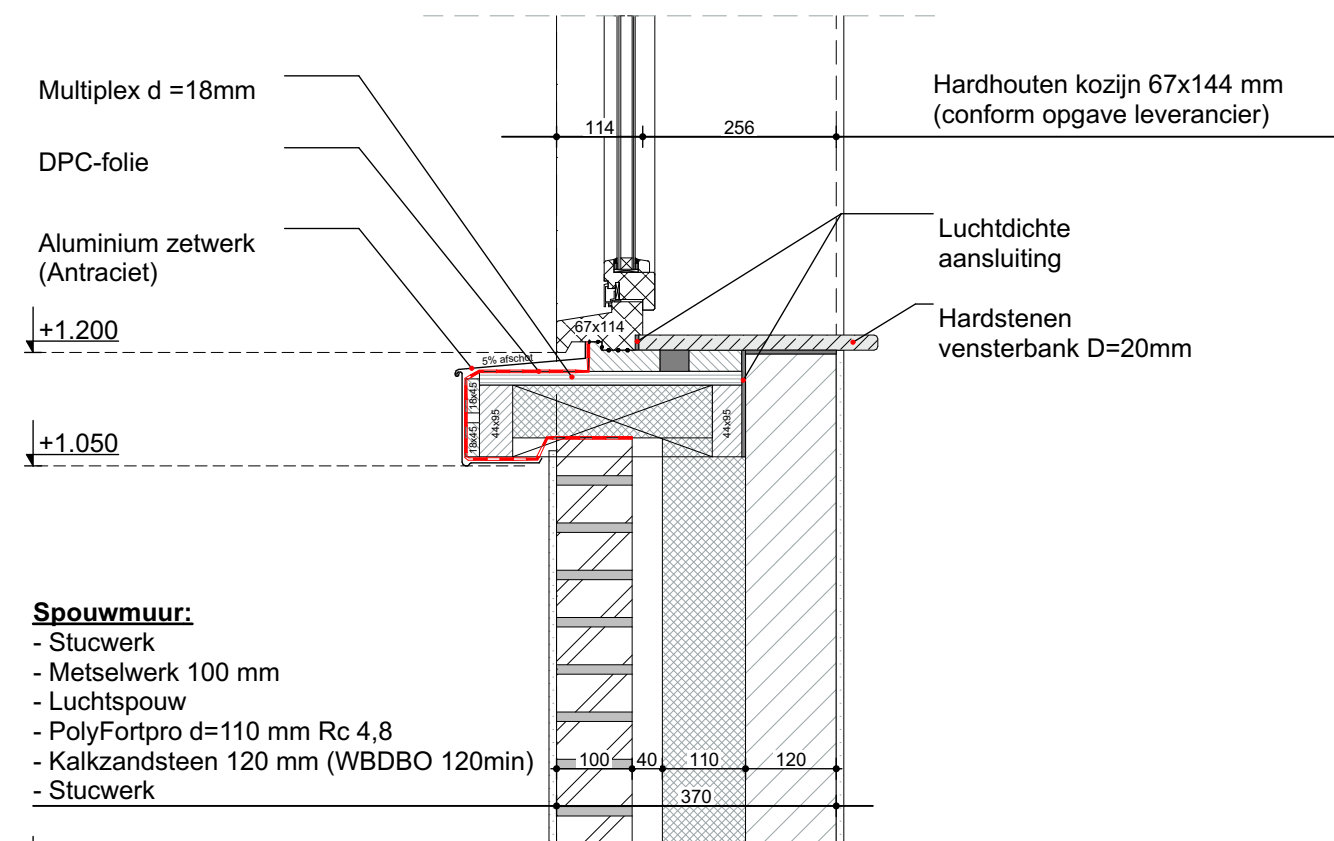

Detail V.2

Project
Nieuwbouw woning met aangrenzend bijgebouw aan de Zevenmorgen 26 te Ingen

Werk nr
W 20.1850

Datum
01-07-2021

Gewijzigd
21-07-2021



Rijnstraat 7
4031 KJ INGEN
T 0344-606686
F 0344-600811
I info@burovanblijderveen.nl
W www.burovanblijderveen.nl

Dakopbouw prefabkap:

- Leipannen
- Panlatten 22x50 h.o.h.300-600mm
- Tengels 38x38 h.o.h. 600mm
- Dampdoorlatende folie
- Prefab kap met isolatie Rc 6,3
(Conform opgave leverancier)
- Dampremmende folielaag
- Watervaste binnenbeplating 11mm

DPC-folie
(overlap tot in de goot)

Vogelschroot

+3.487

Mastgoot M44
(zink)

Redcedar
boeideel
(antraciet)

WBP 12mm
(antraciet)

+2.910

DPC-Folie

+2.600

Geveldrager

O.s.v.
H.o.h 1000mm

+2.100

Draagconstructie
prefabkap
(conform opgave
leverancier)

Plint MDF
18x140mm

Vloeropbouw begane grond:

- Vloerafwerking
- Cement dekvloer 70mm
- Breedplaatvloer 240mm
(conform opgave leverancier)

Luchtdichte aansluiting

Project

Nieuwbouw woning met aangrenzend bijgebouw aan de Zevenmorgen 26 te Ingen

Werk nr

W 20.1850

Datum

01-07-2021


Gewijzigd

21-07-2021

Detail V.3



Rijnstraat 7
4031 KJ INGEN
T 0344-606686
F 0344-600811
I info@burovanblijderveen.nl
W www.burovanblijderveen.nl

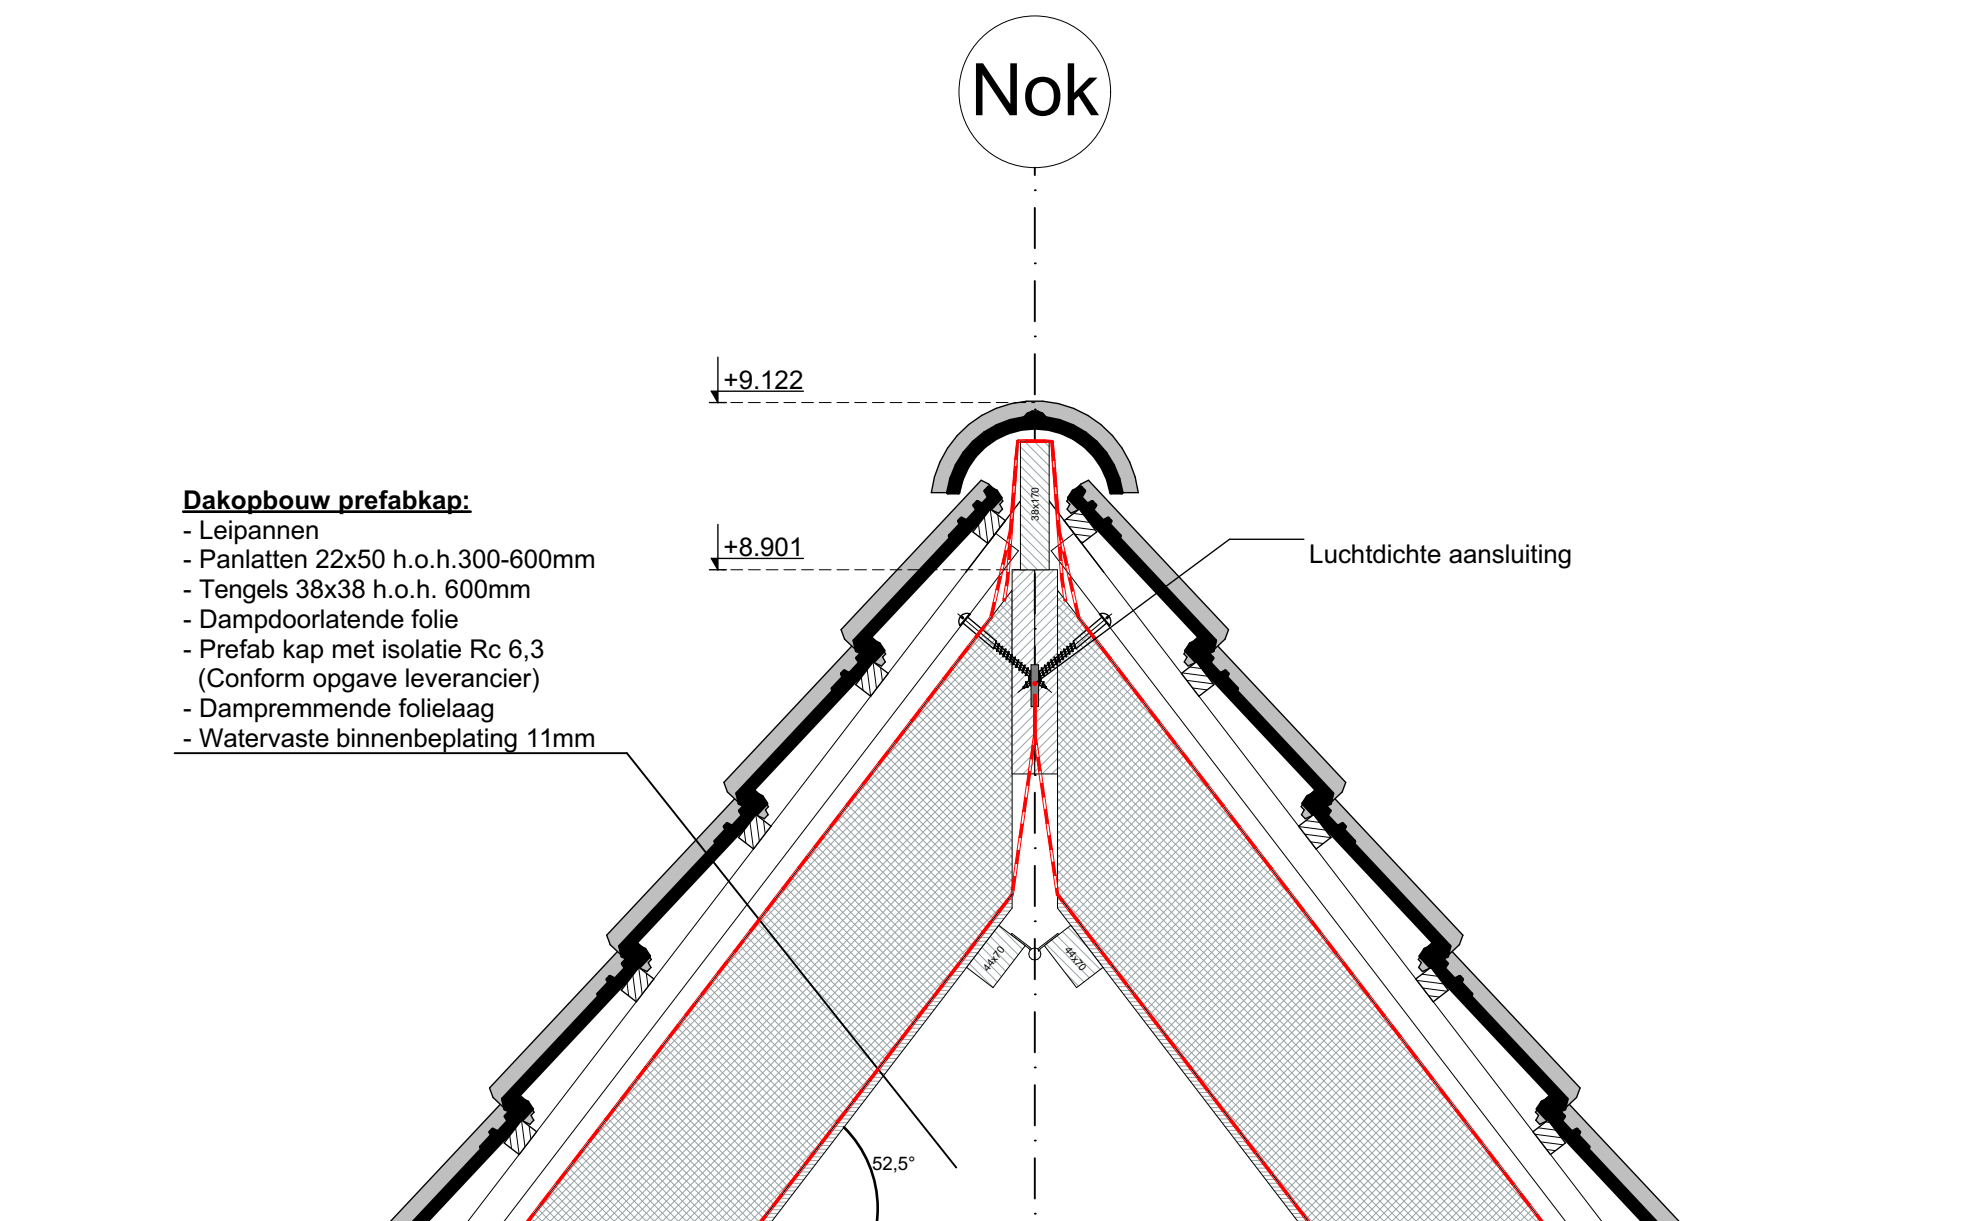

Dakopbouw prefabkap:

- Leipannen
- Panlatten 22x50 h.o.h. 300-600mm
- Tengels 38x38 h.o.h. 600mm
- Dampdoorlatende folie
- Prefab kap met isolatie Rc 6,3
(Conform opgave leverancier)
- Dampremmende folielaag
- Watervaste binnenbeplating 11mm

Detail V.4

Project
Nieuwbouw woning met aangrenzend bijgebouw aan de Zevenmorgen 26 te Ingen


Werk nr
W 20.1850

Datum
01-07-2021

Gewijzigd
21-07-2021



Rijnstraat 7
4031 KJ INGEN
T 0344-606686
F 0344-600811
I info@burovanblijderveen.nl
W www.burovanblijderveen.nl

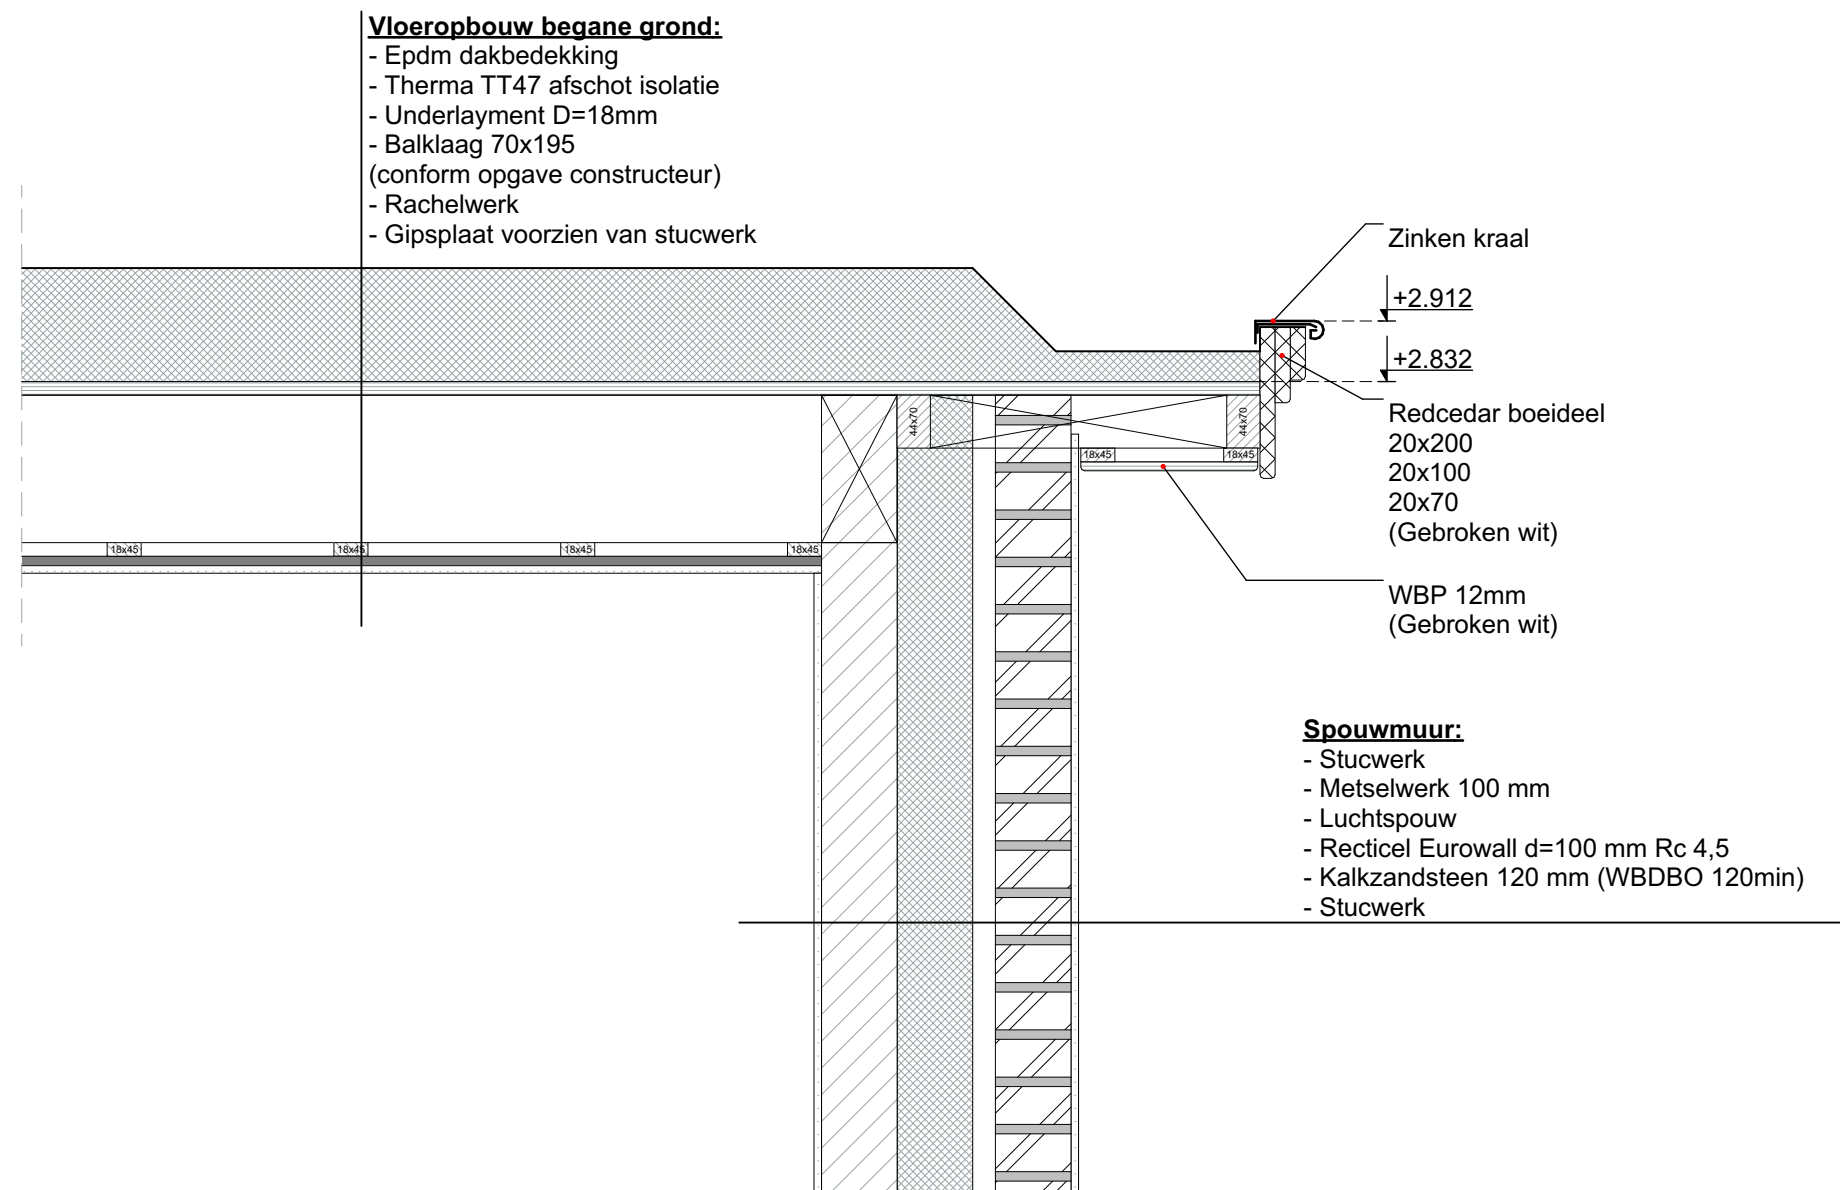

Detail V.5

Project
Nieuwbouw woning met aangrenzend bijgebouw aan de Zevenmorgen 26 te Ingen


Werk nr
W 20.1850

Datum
01-07-2021

Gewijzigd
21-07-2021



Rijnstraat 7
4031 KJ INGEN
T 0344-606686
F 0344-600811
I info@burovanblijderveen.nl
W www.burovanblijderveen.nl

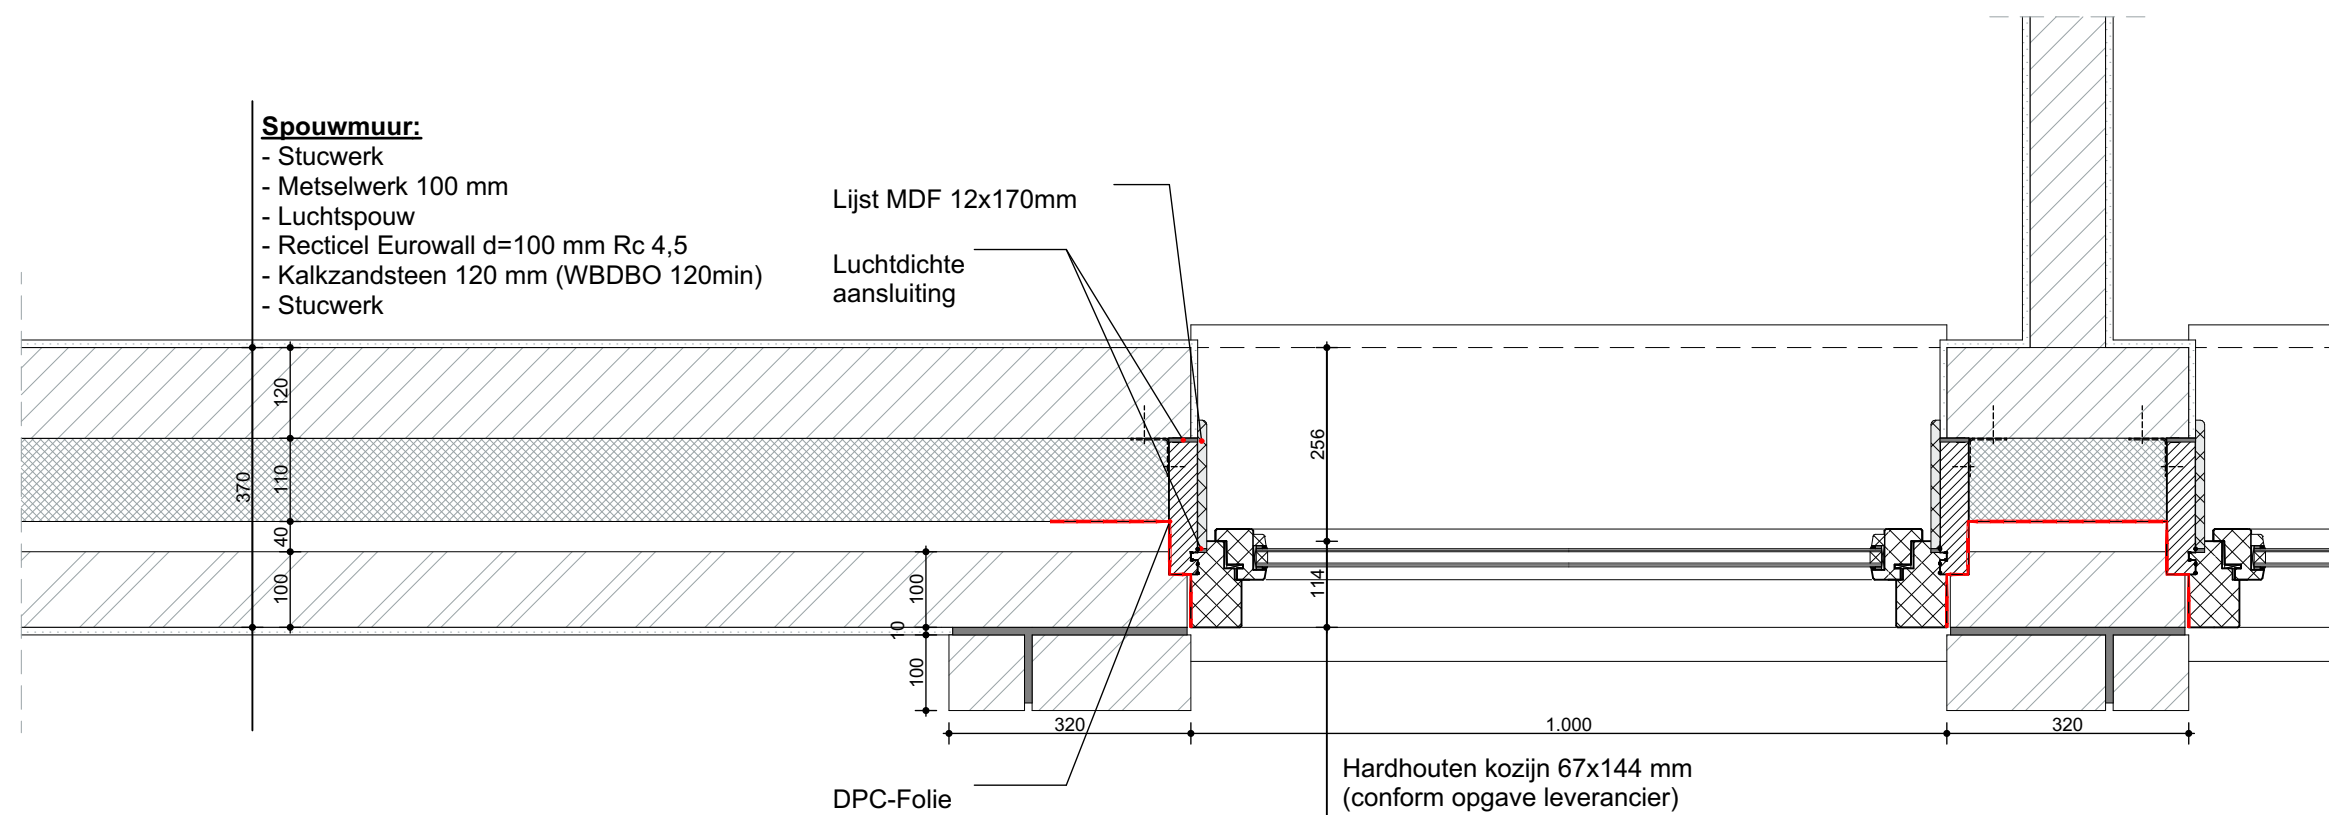

Detail H.1

Project
Nieuwbouw woning met aangrenzend bijgebouw aan de Zevenmorgen 26 te Ingen

Werk nr
W 20.1850

Datum
01-07-2021

Gewijzigd
21-07-2021



Rijnstraat 7
4031 KJ INGEN
T 0344-606686
F 0344-600811
I info@burovanblijderveen.nl
W www.burovanblijderveen.nl