


VOORGEVEL


RECHTER ZIJGEVEL

ACHTERGEVEL


LINKER ZIJGEVEL

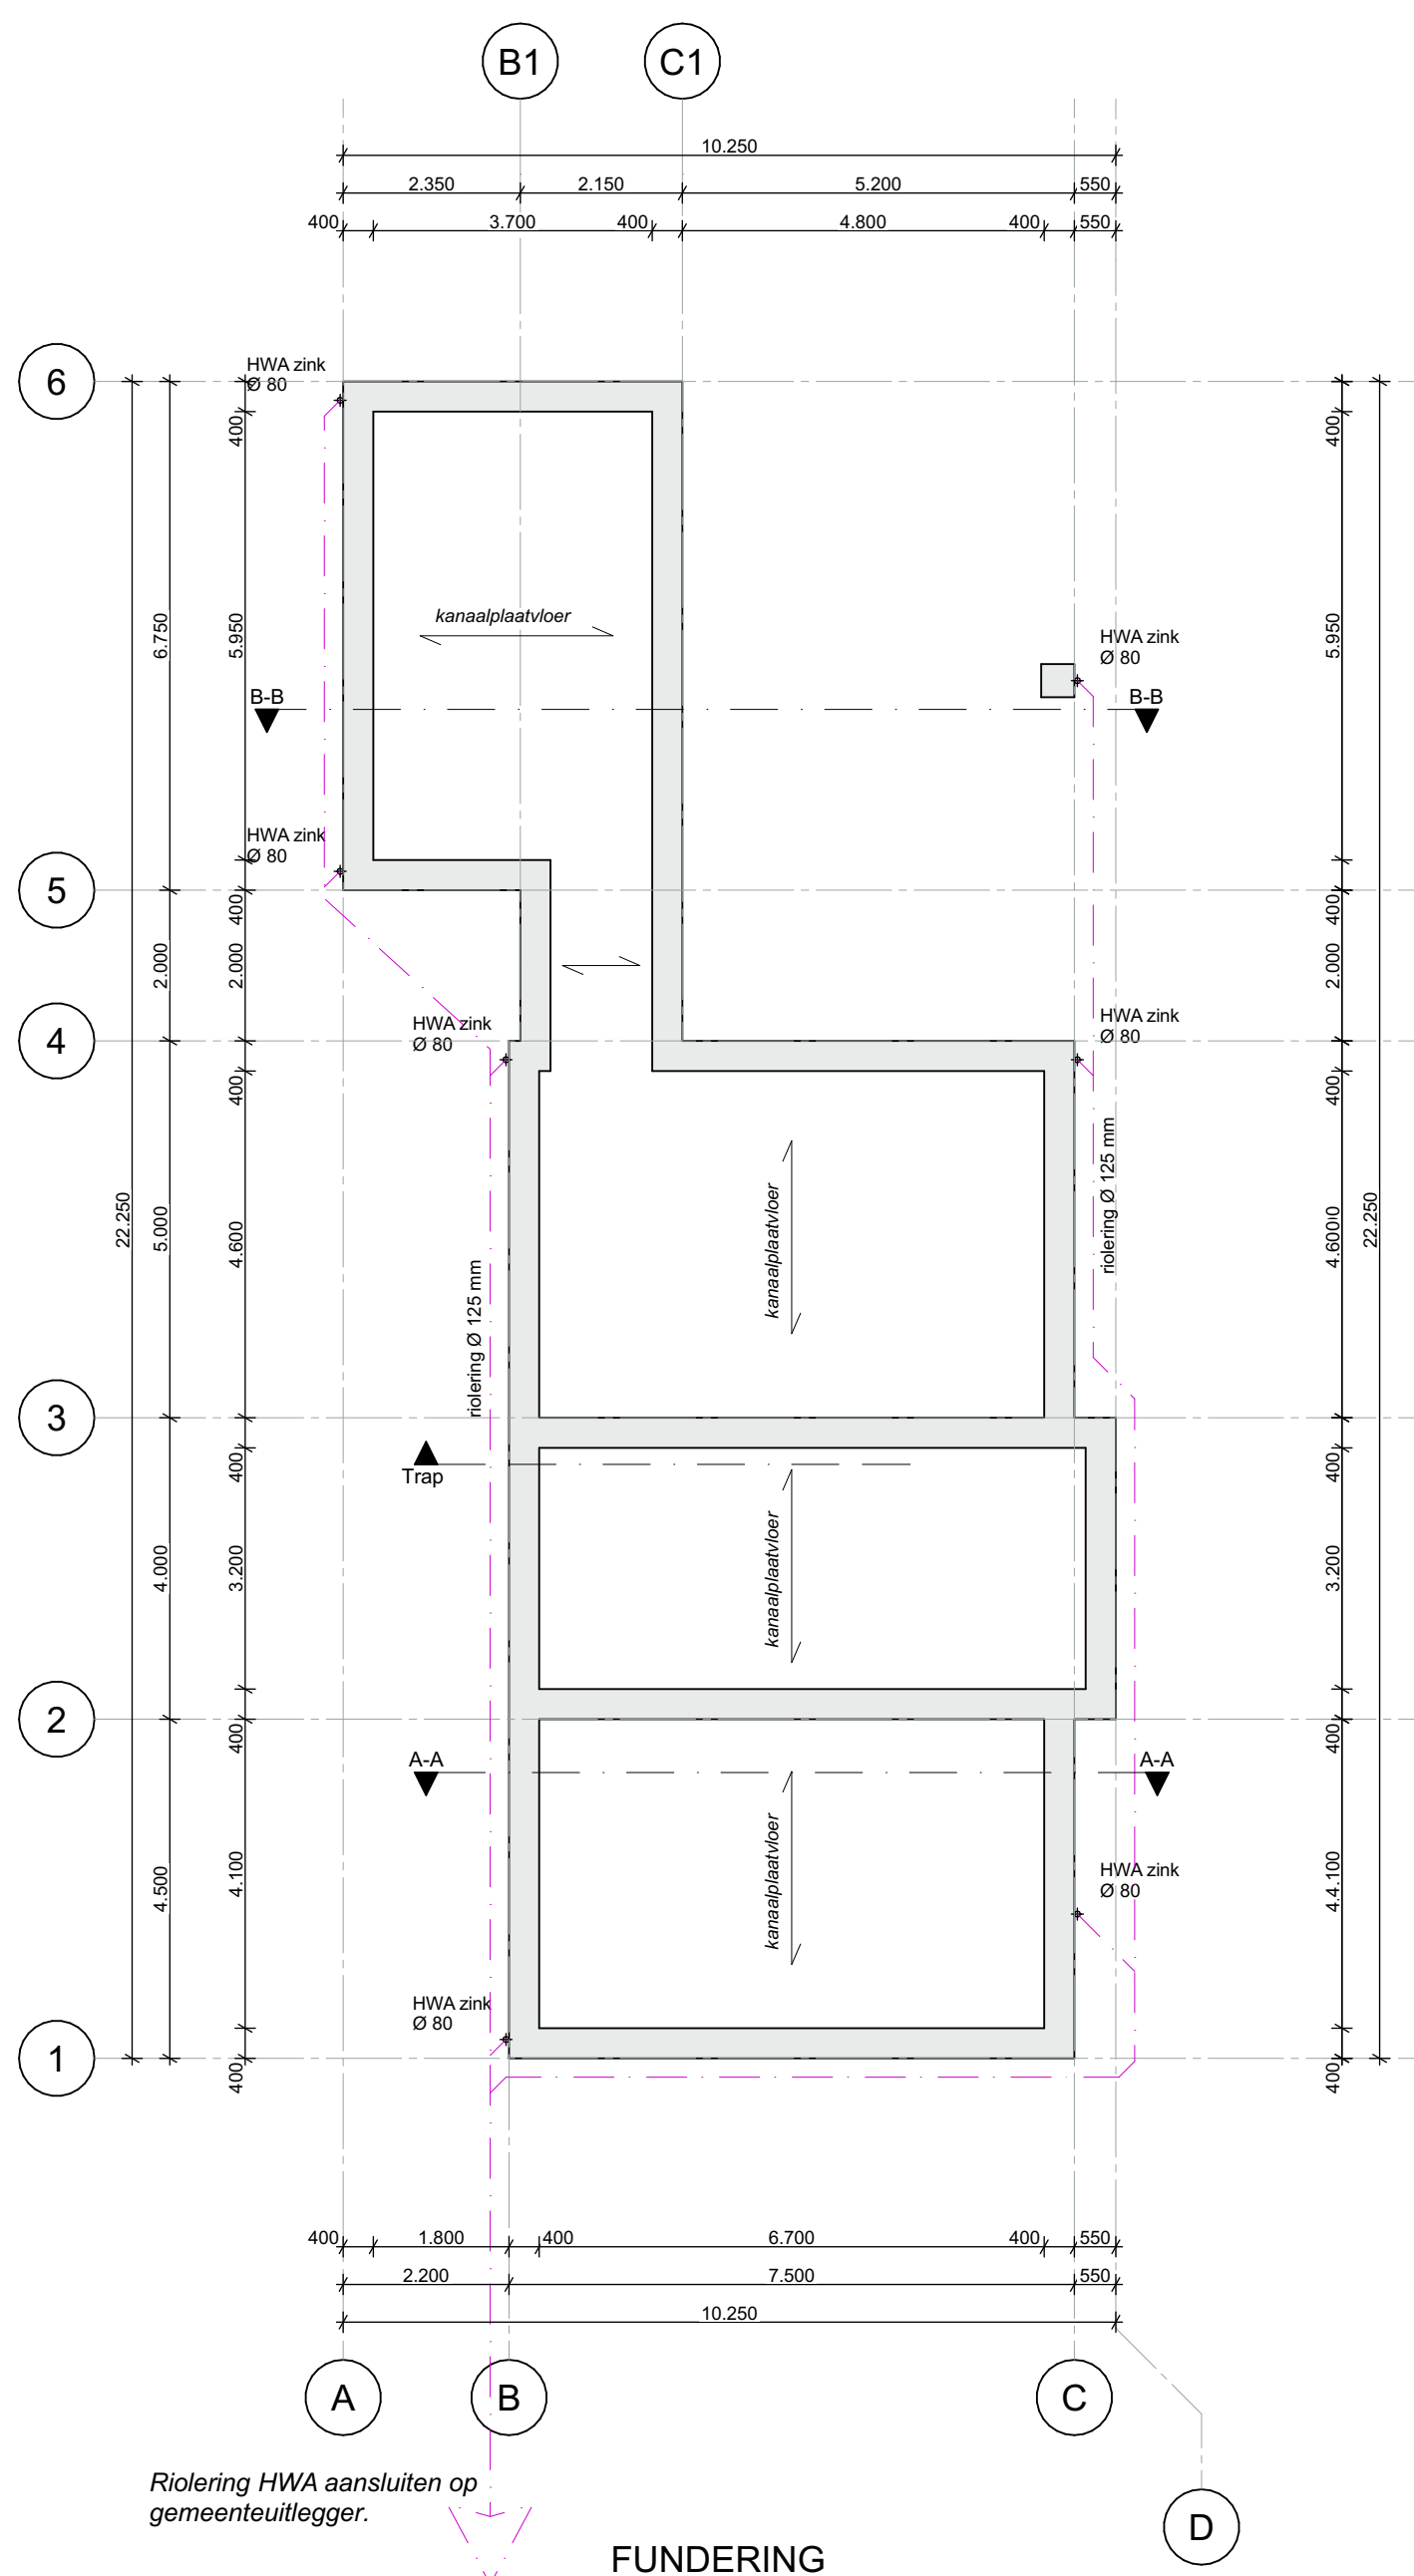


FUNDERING

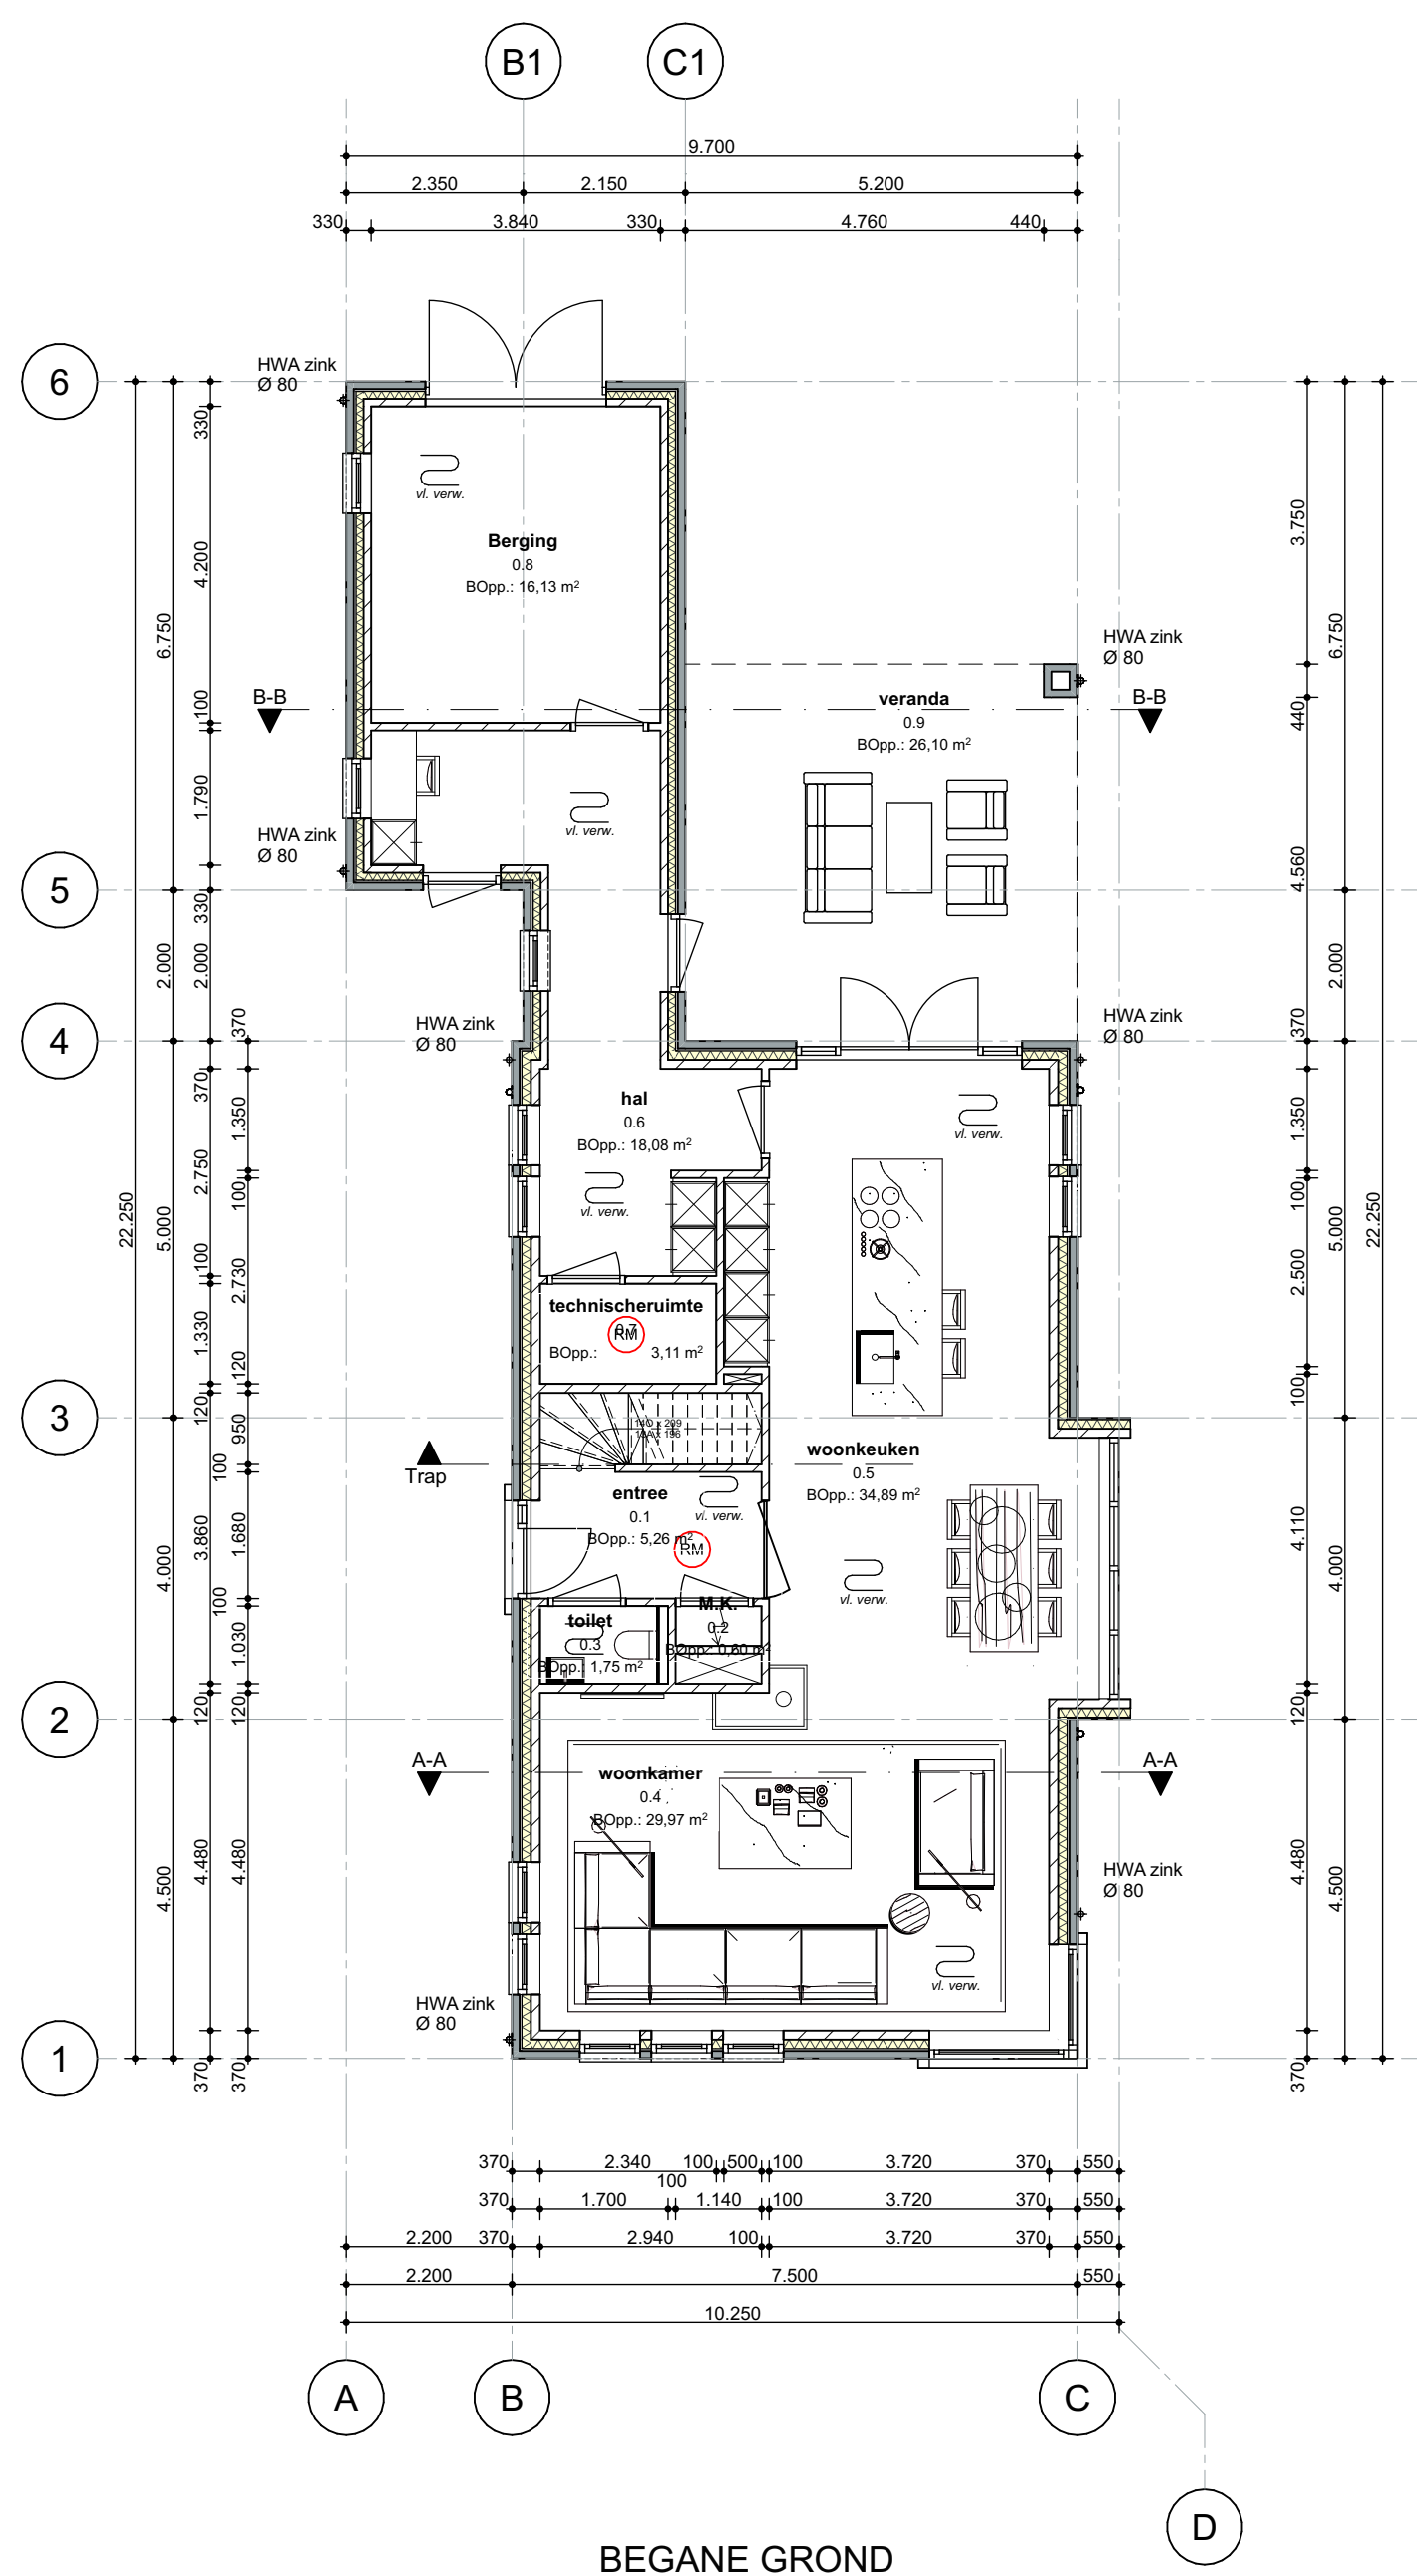


BEGANE GROND

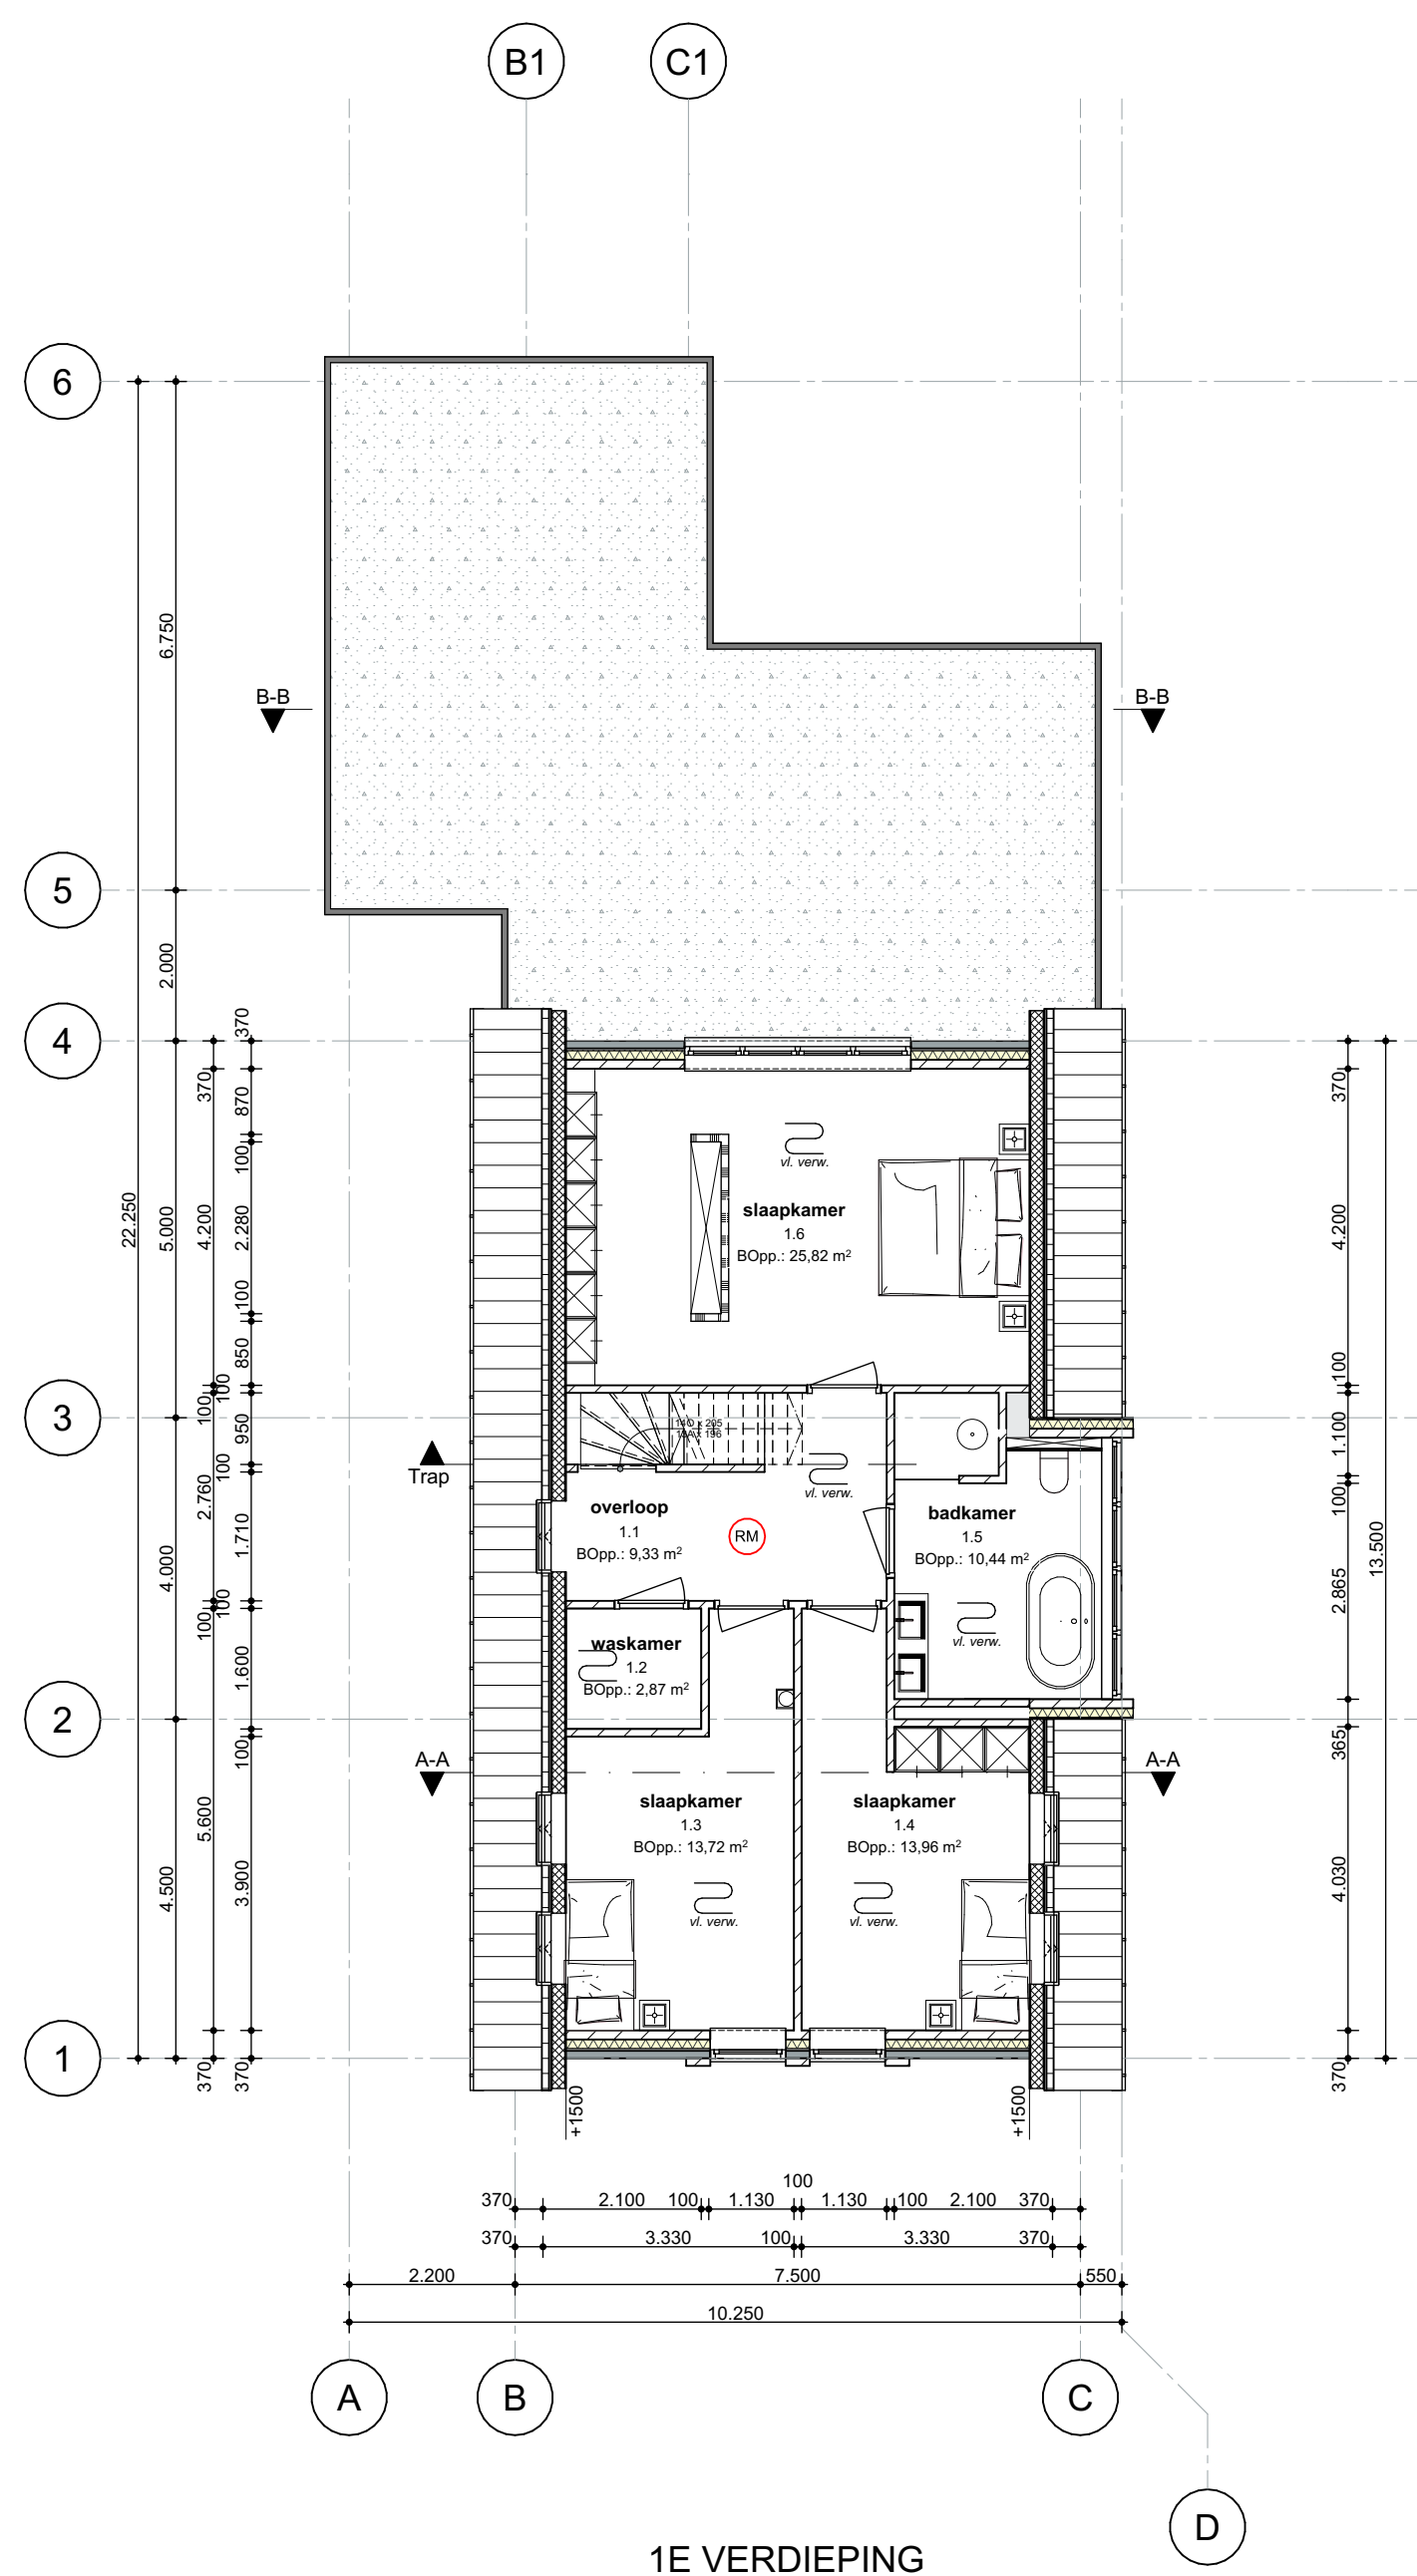


1E VERDIEPING

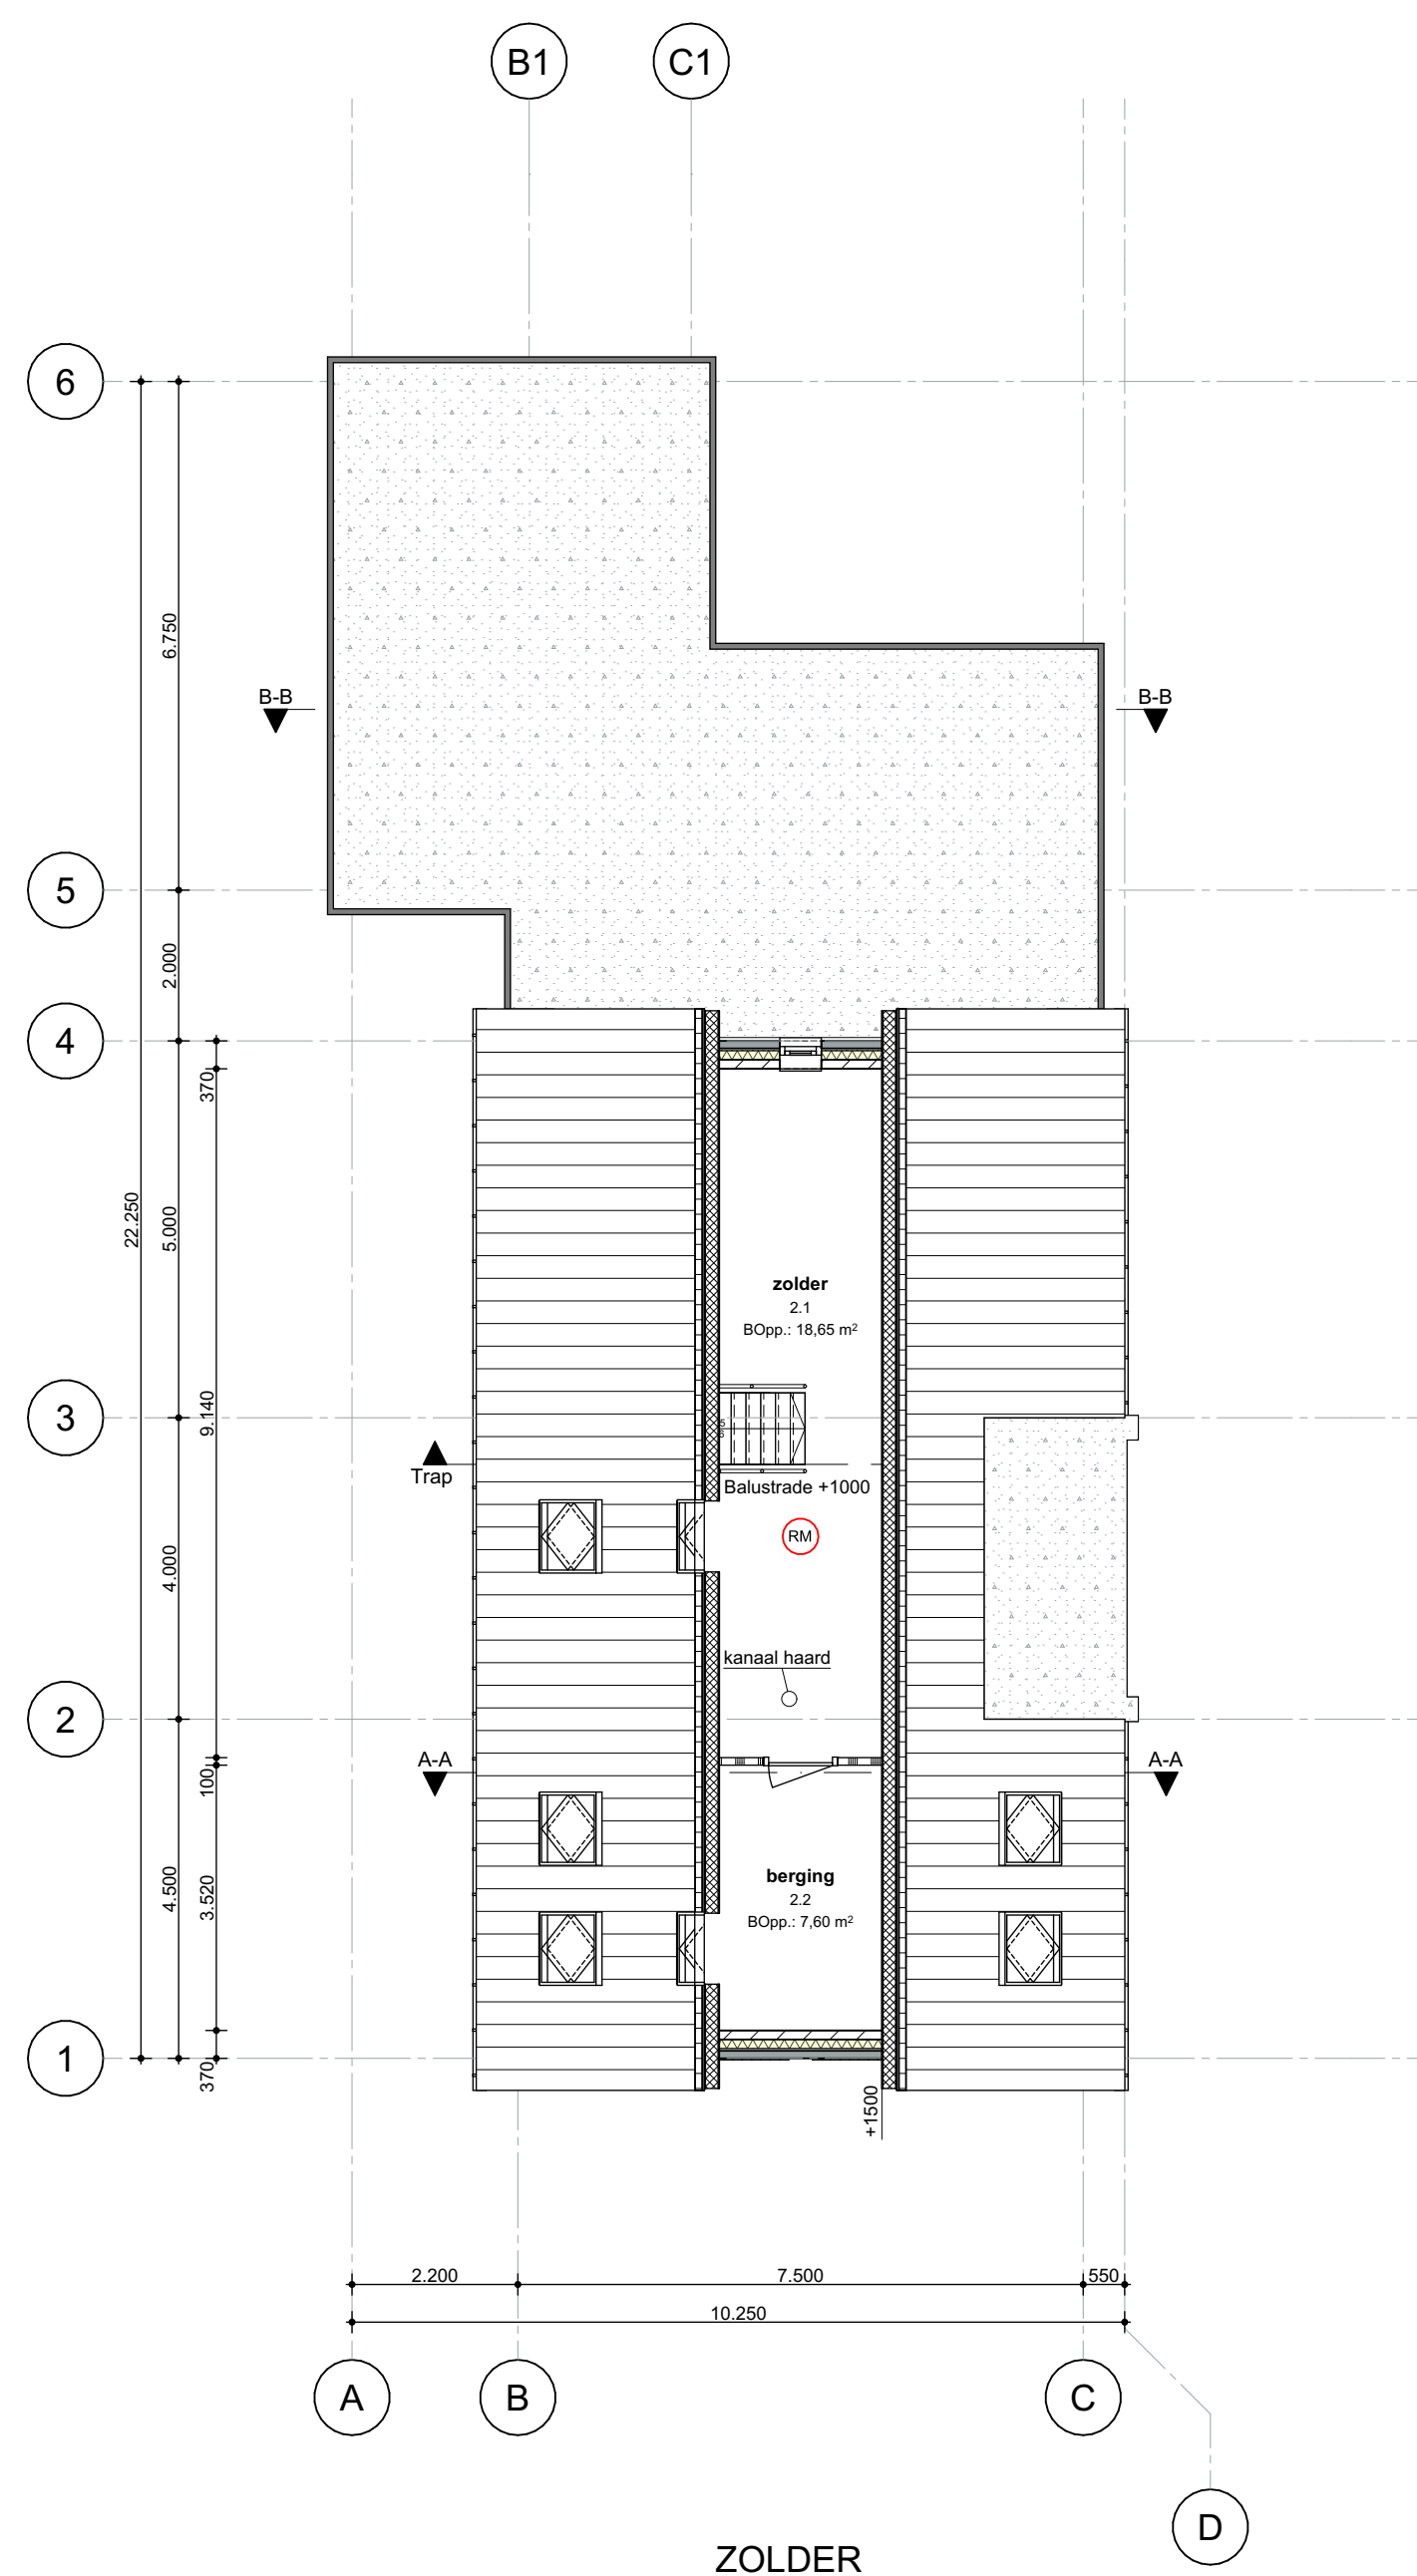


ZOLDER

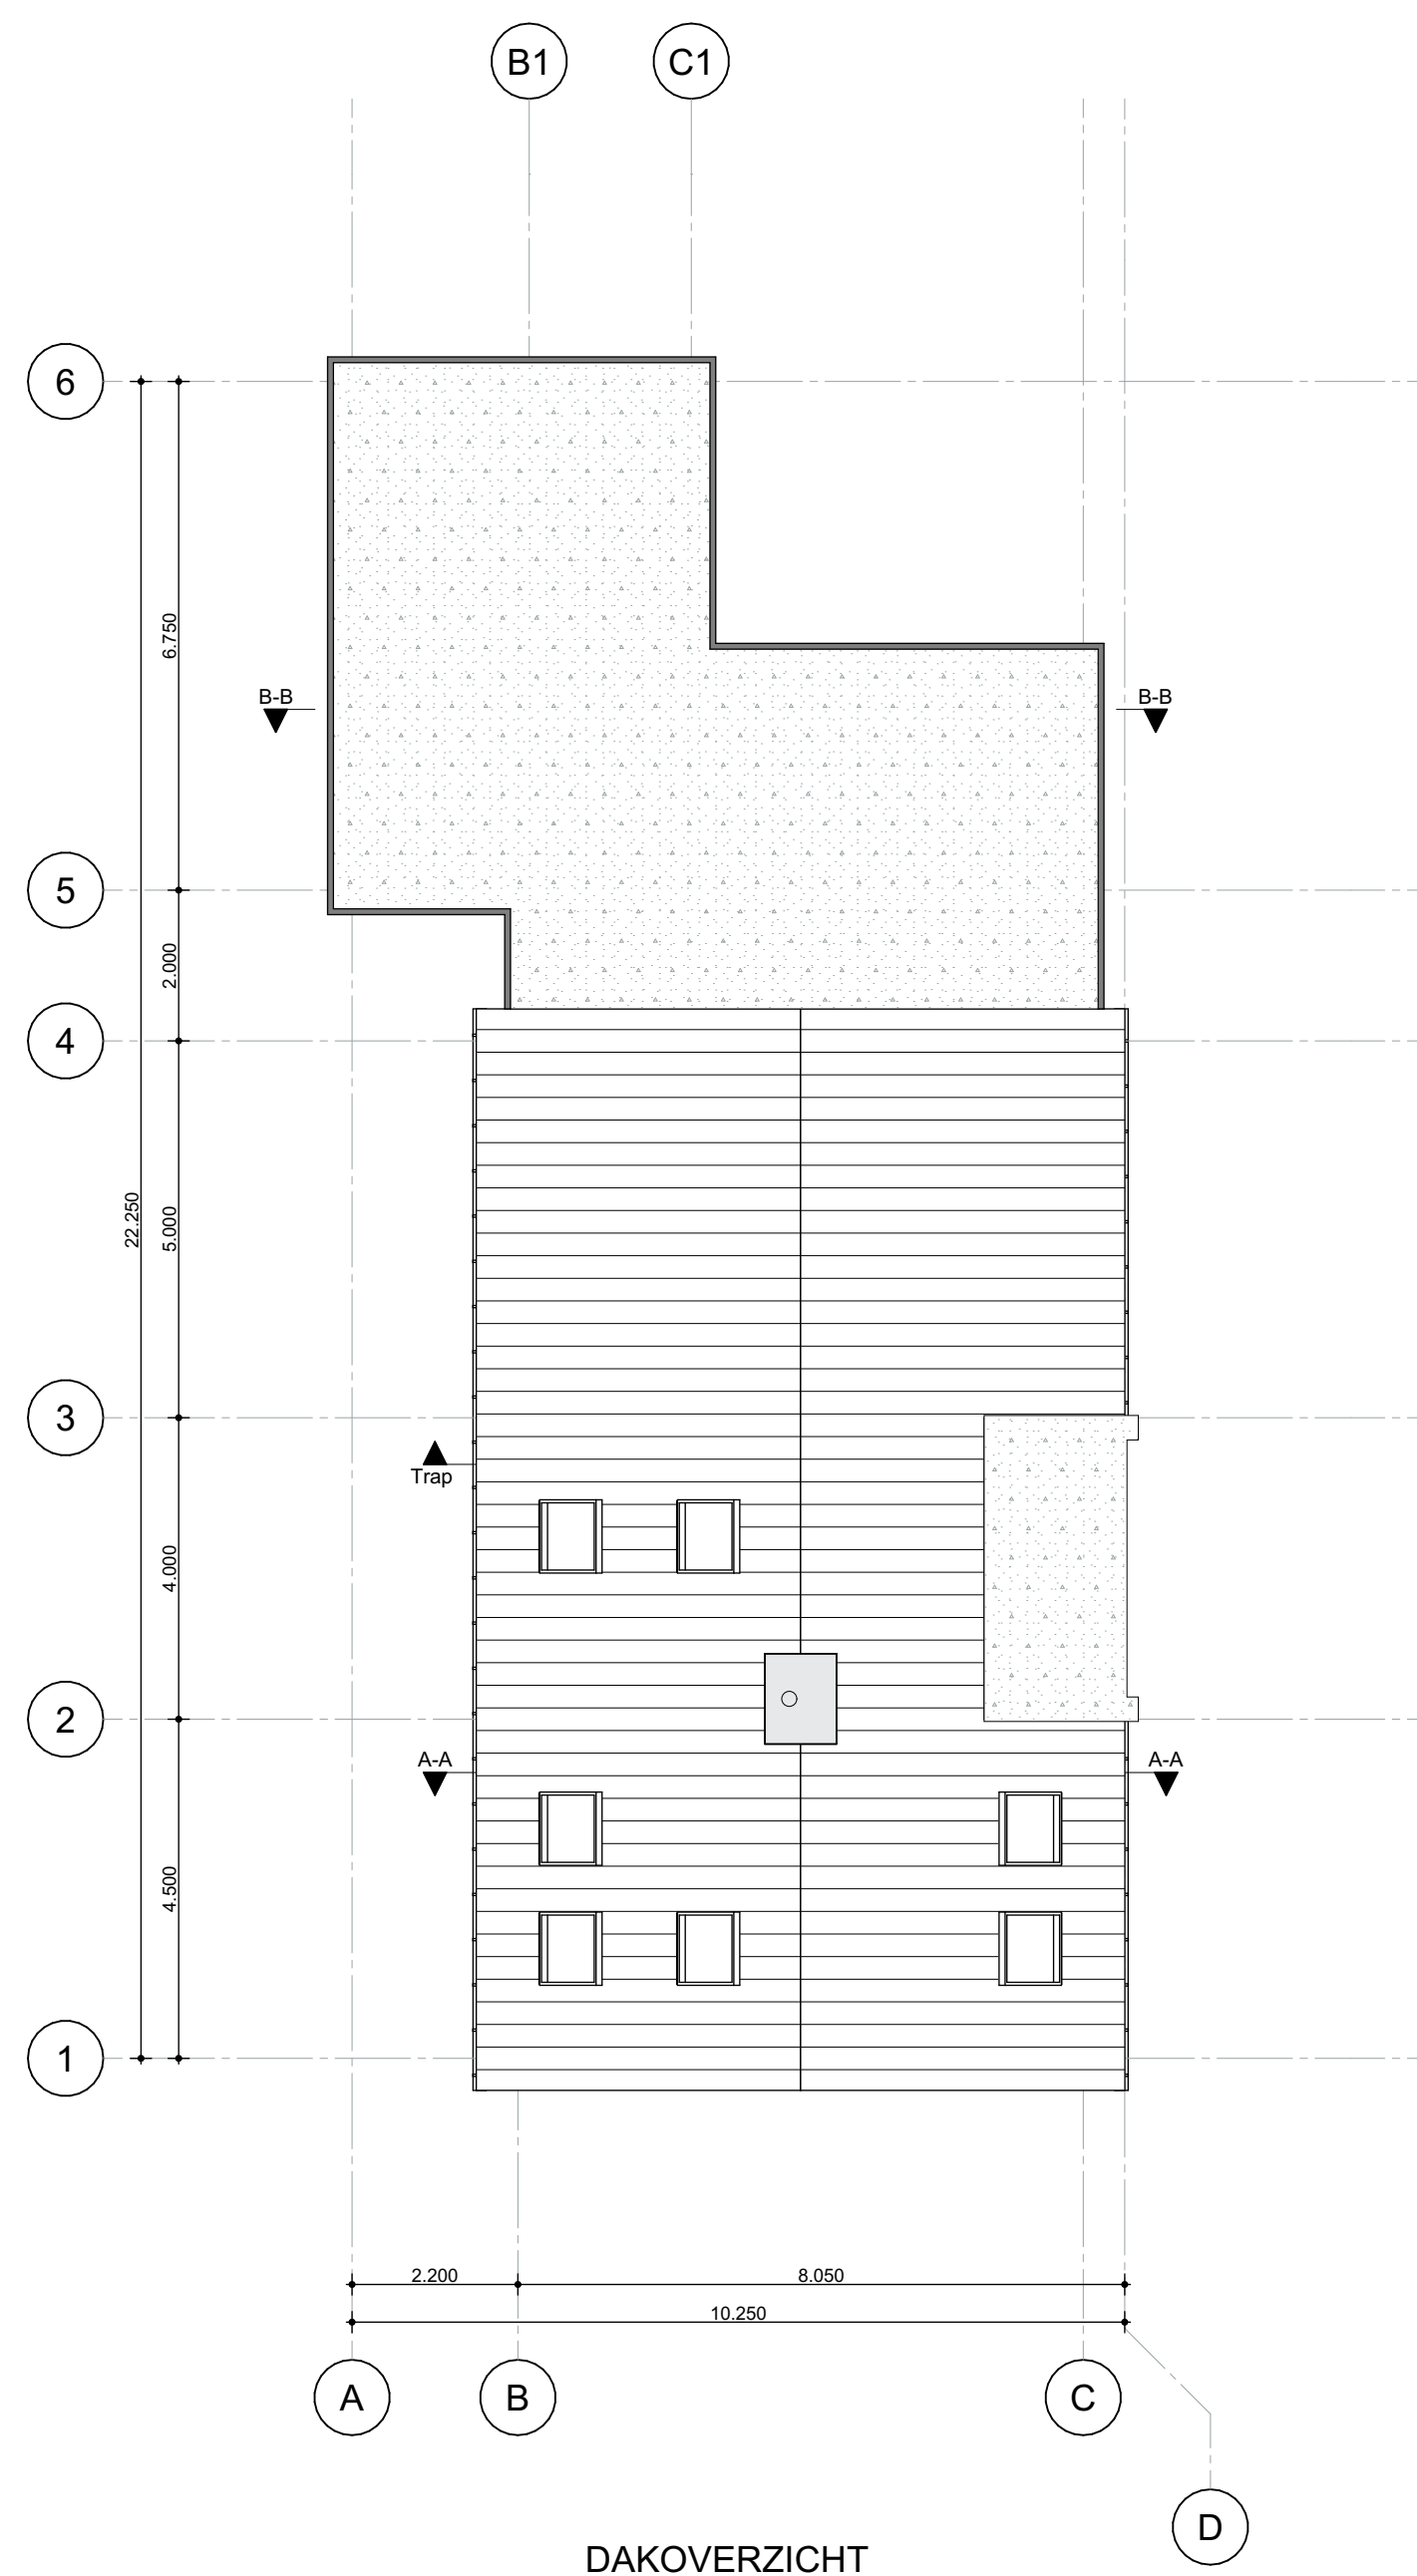


DAKOVERZICHT

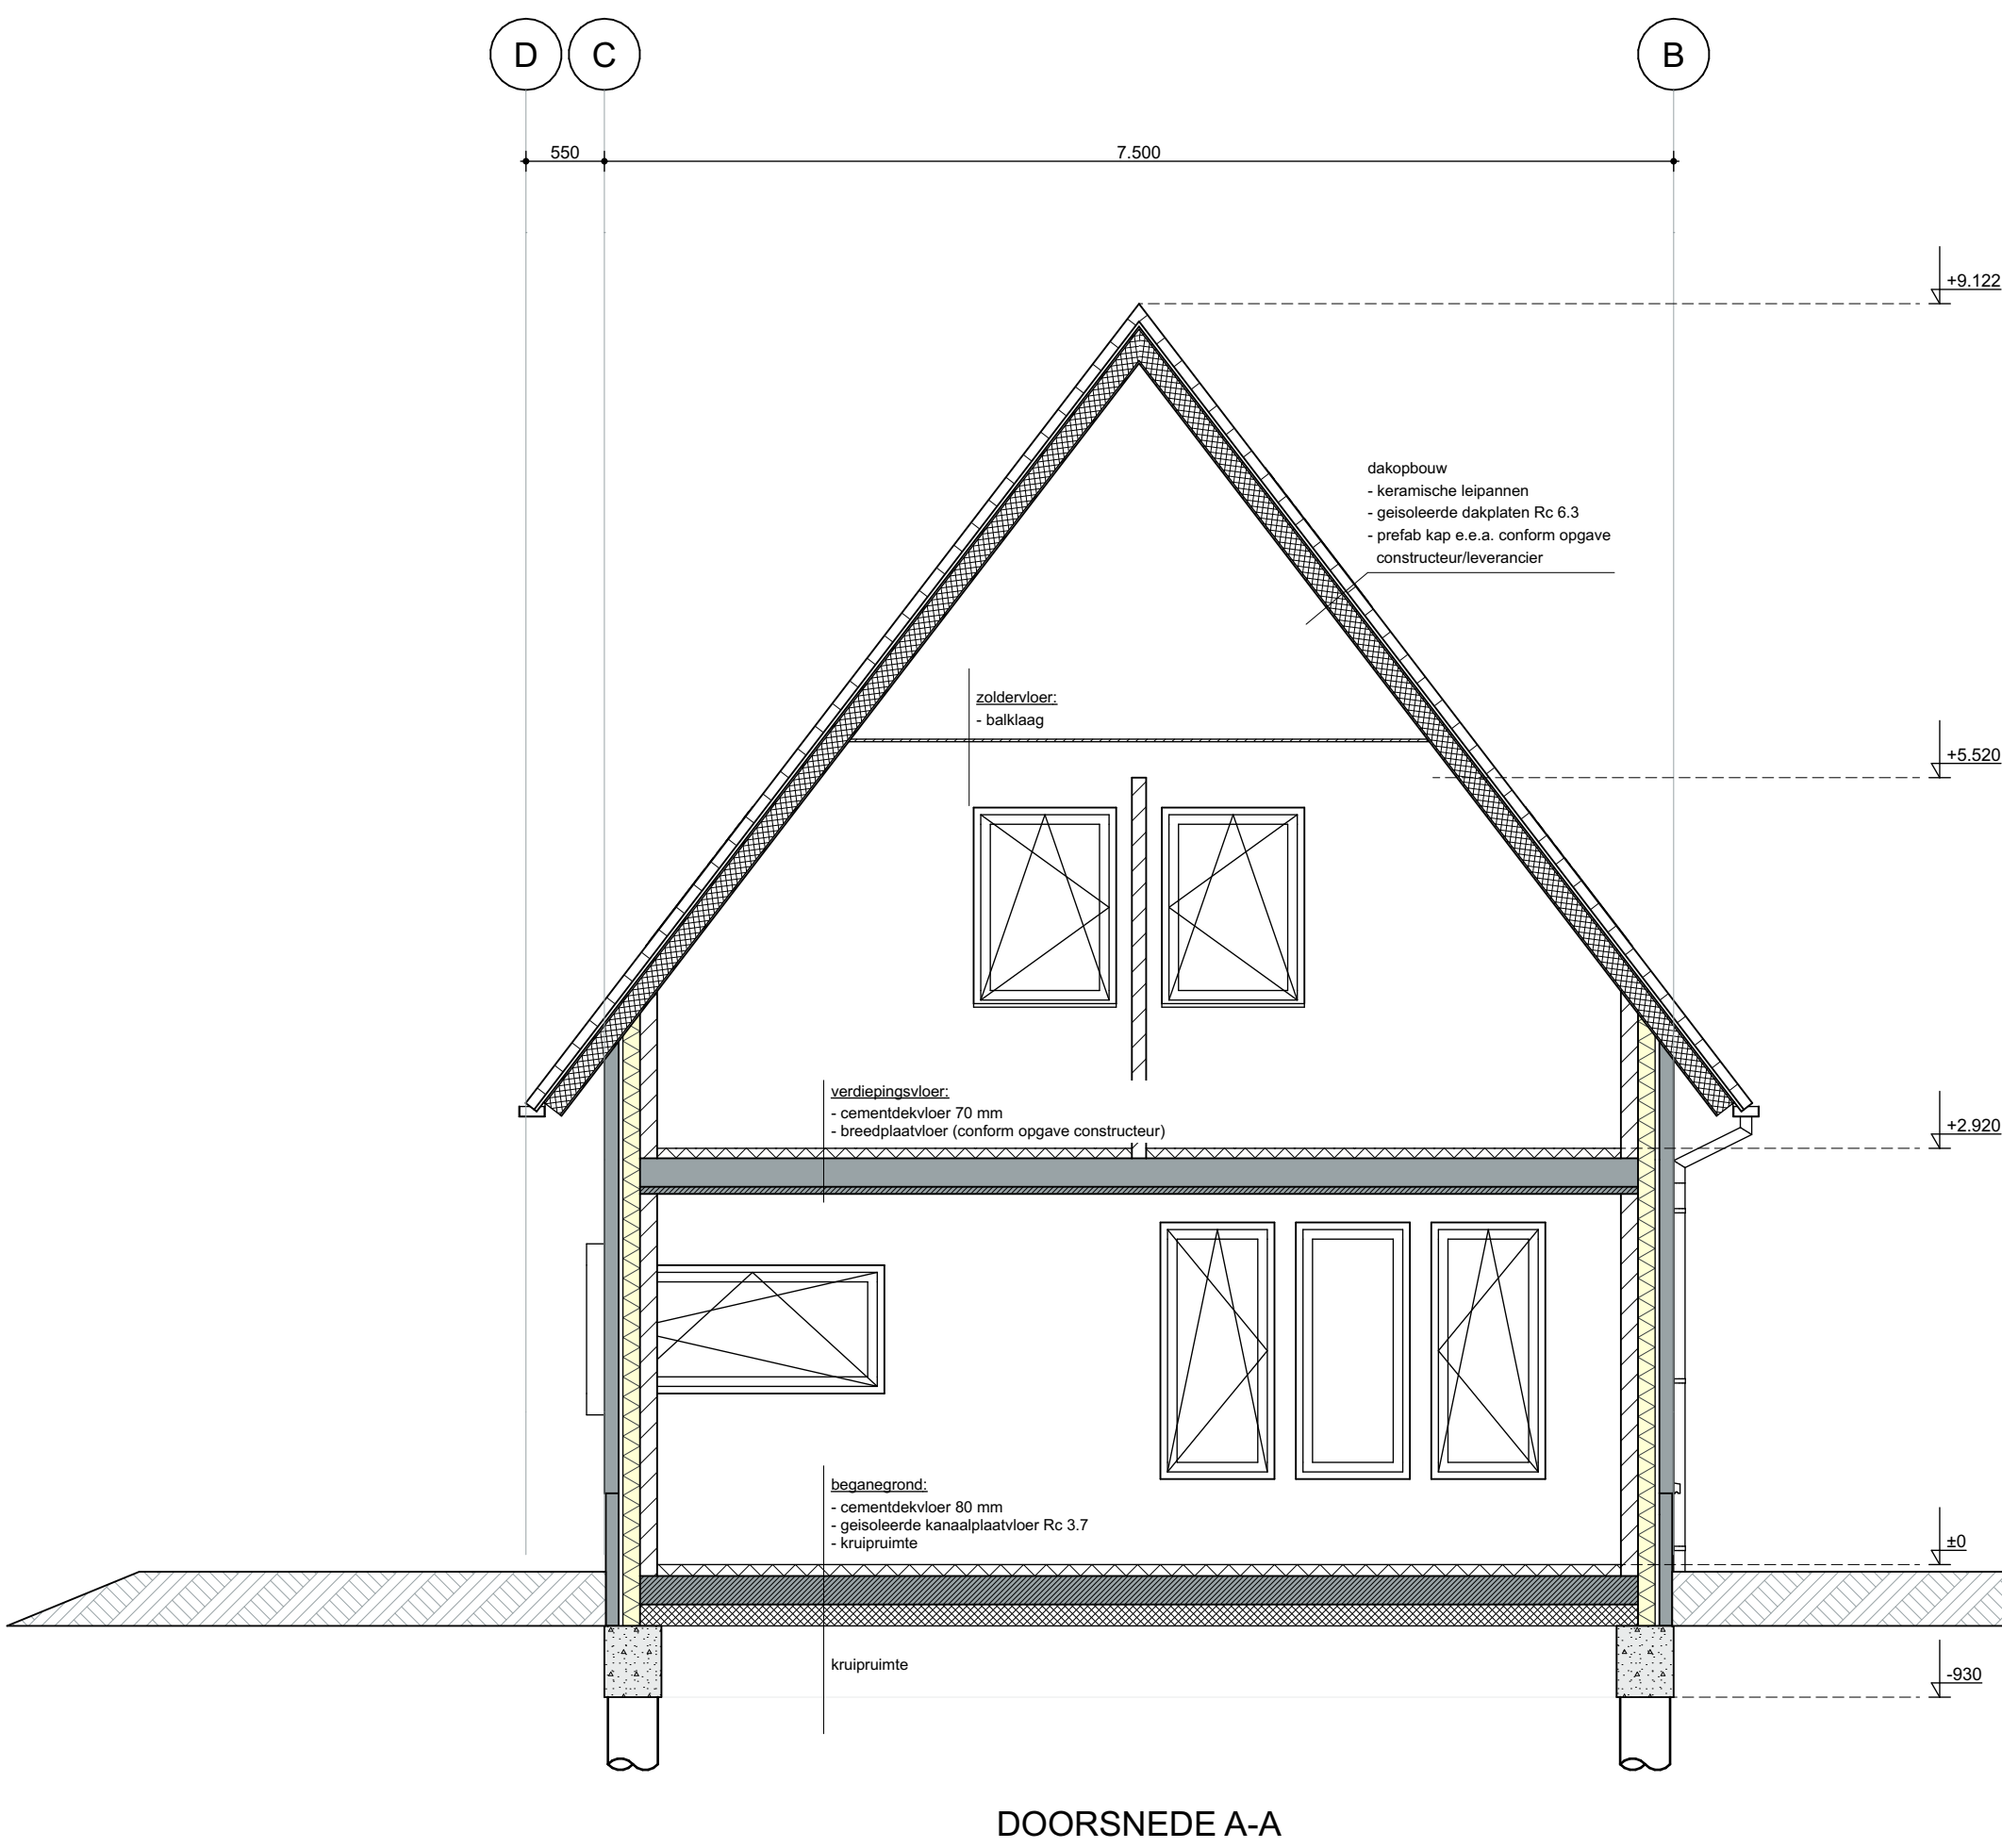

DOORSNEDE A-A

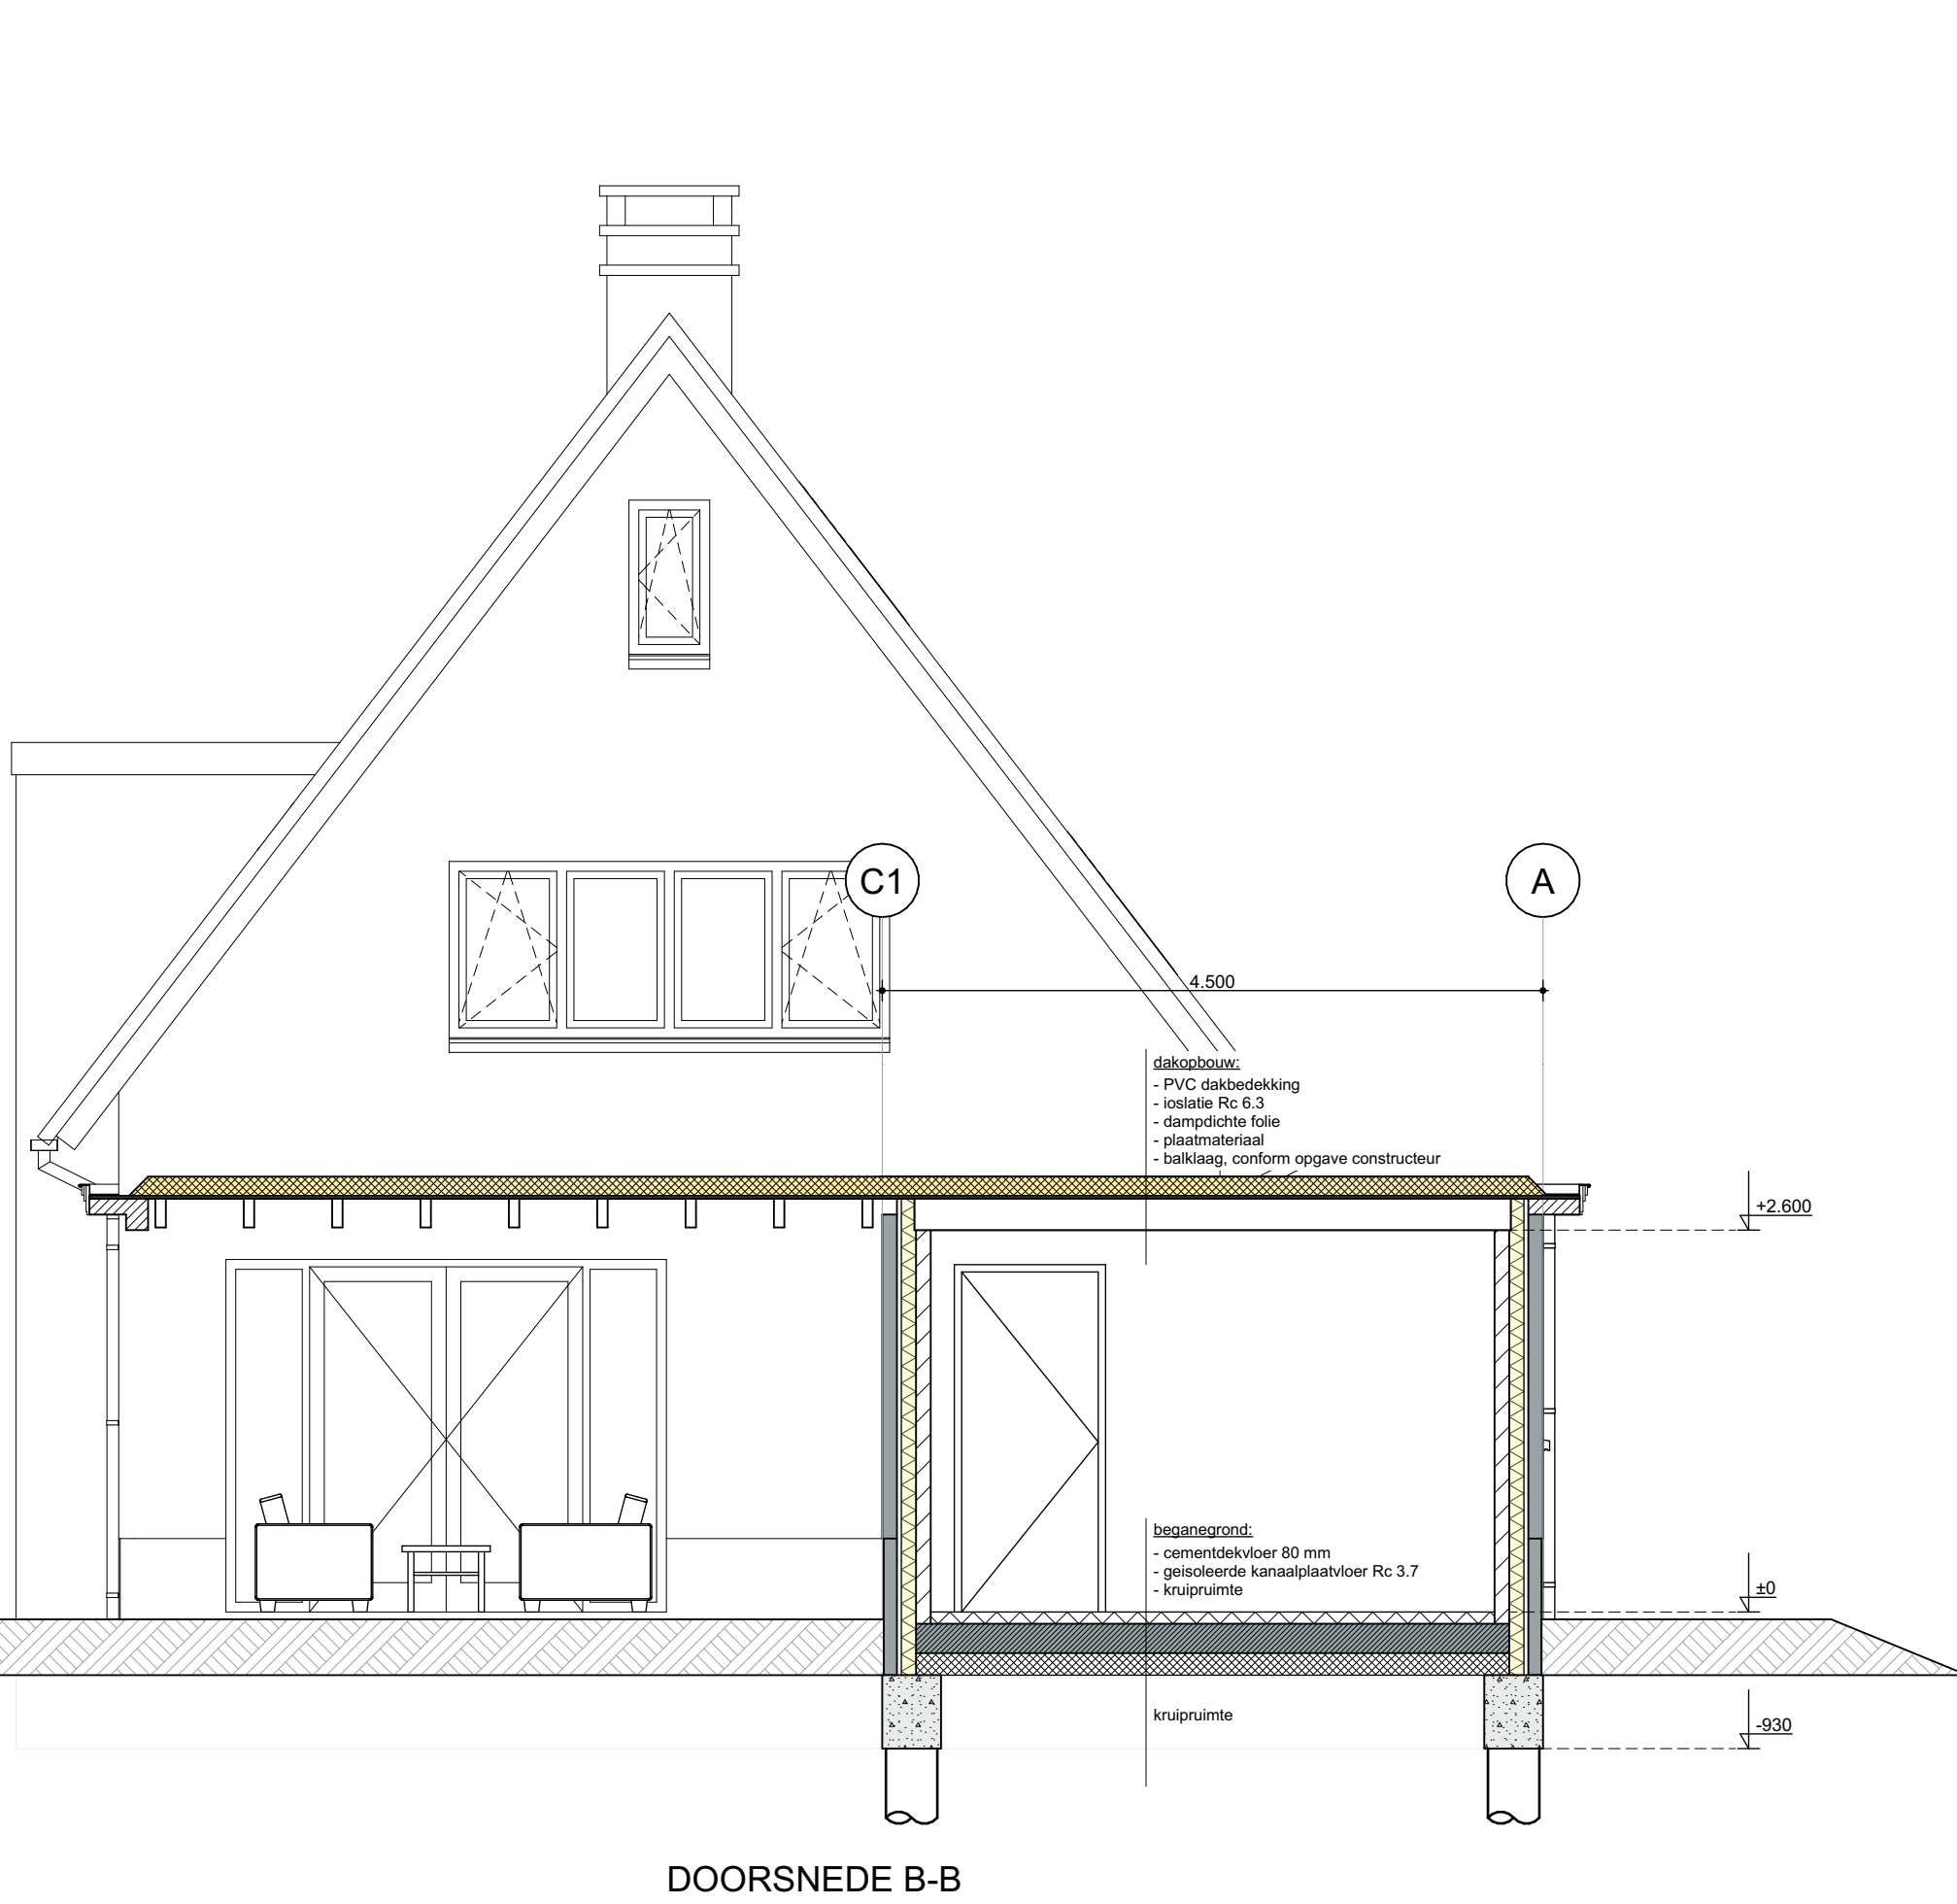

DOORSNEDE B-B

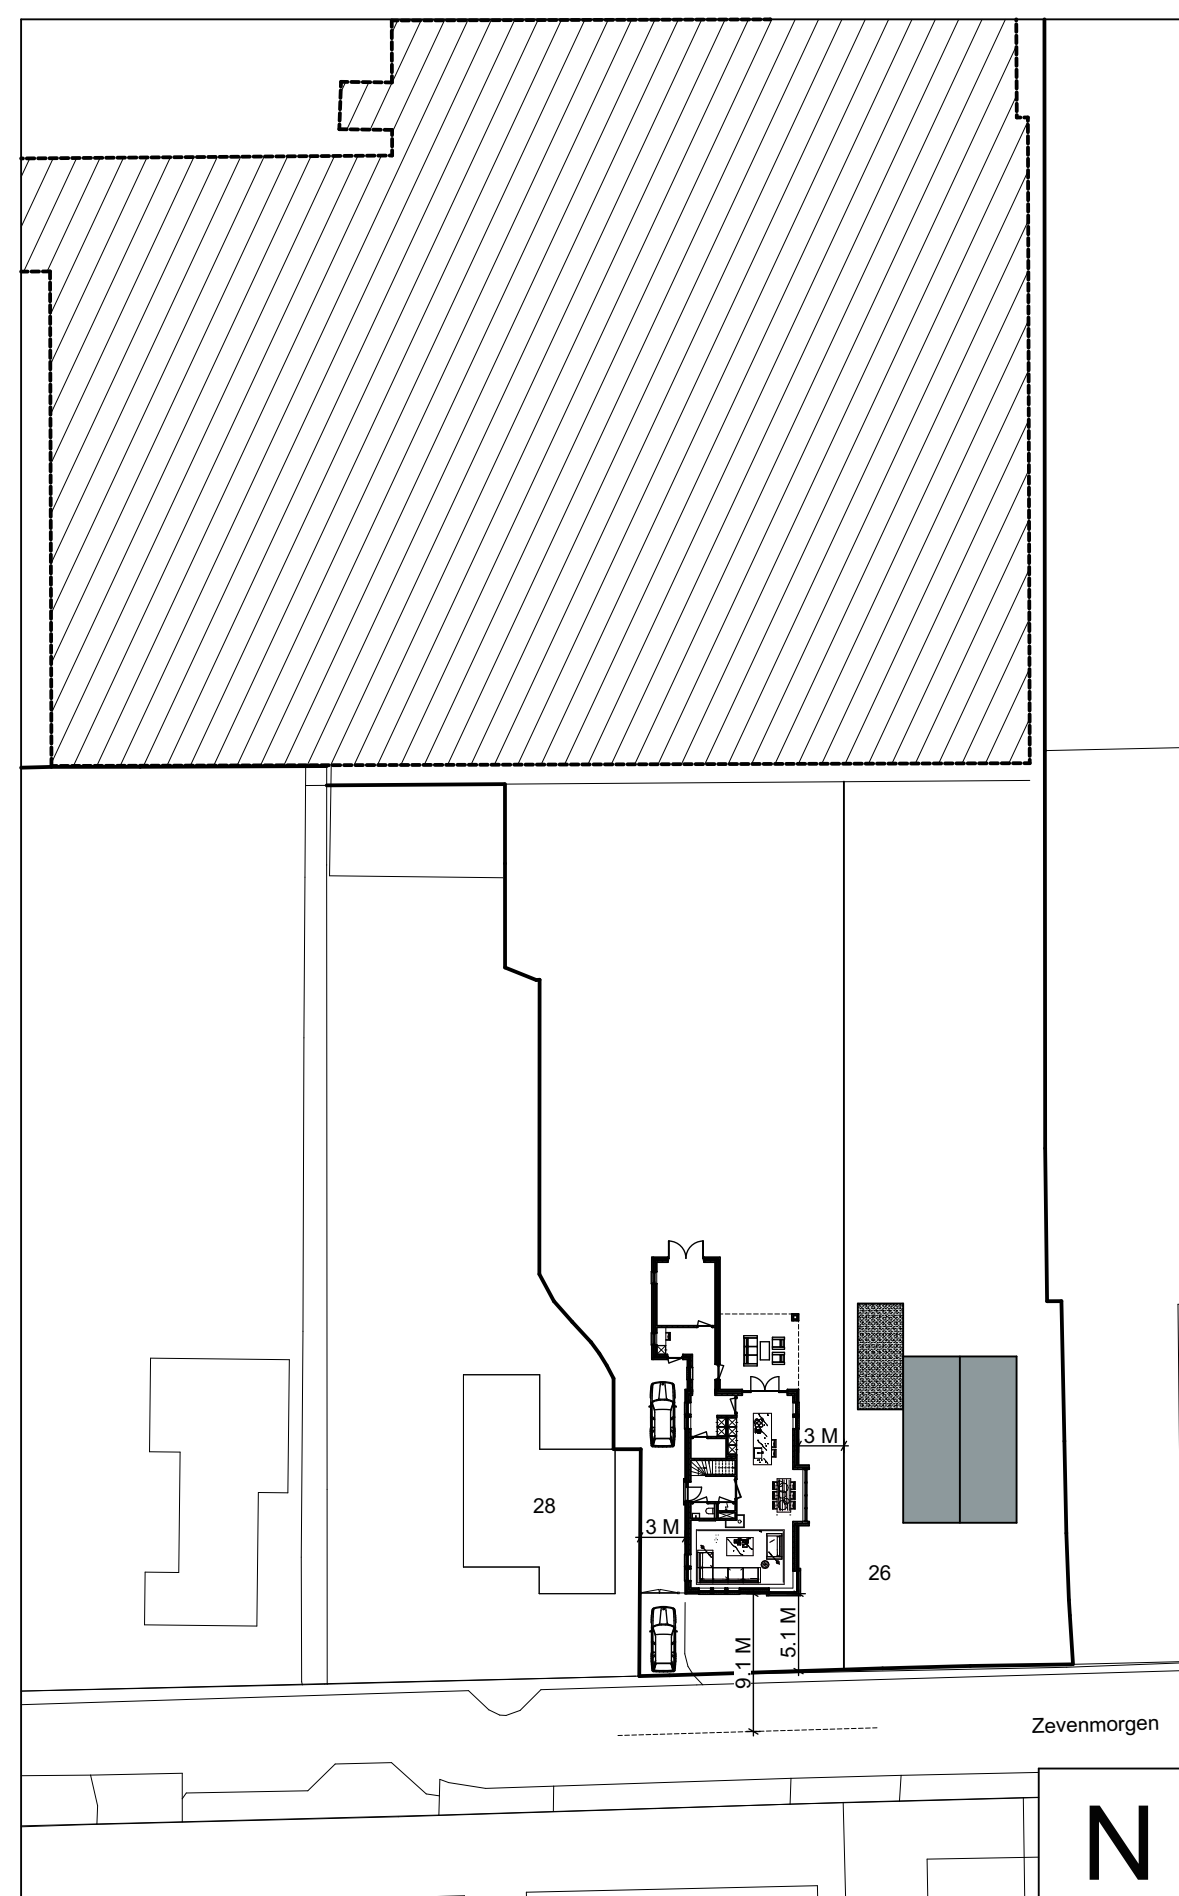

Situatie aan de Zevenmorgen 26 te Ingen

Gem : Lienden
Sectie : 1491
Nr : 1491
Schaal : 1 : 500

renvool:	beschrijving
	gevelstenen
	isolatie
	baksteen binnenmuren vops constr
	binnendeuren 930 x 2315
	vloerwarming + isolatie
	raamkelder op 230 valt / onderling gekoppeld
	H.W.A. afvoer Ø 80 mm (zink)

Onderdeel:	Rc waarde (m²·K)/W
Beganegrondvloer	3,70
Builengevel	4,70
Hellend dak	6,30

Onderdeel:	U waarde W/(m²·K)
Glas (begane grond)	0,4 W/m²·K HR++ triple glas
Glas	1,10 algemeen verkrijgbaar
Kozijn	2,40 hardhout
Raam	1,64 gecombineerde waarde kozijn + glas
Deur	1,65 maximale U-waarde conform bouwbesluit
Dakram	1,30 vetux dakraam

CONSTRUCTIE

- Alle beton-staal-en houtconstructie's volgens tek + berekening constructeur.
- Alle latten volgens berekening constructeur.
- Technische wijzigingen voortbouwen.

Materialen Renvool:		
Bouwdeel	Materiaal	Kleur
Gevels	Stucwerk	Gebroken wit
Gevels (voorgevel)	Hout (verticaal)	Antraciet
Gevels binnendeuren	Metselwerk	Rood gezuurdeerd
Vloerwerk	-	Licht grijs
Waterslagen	Belgisch hardsteen	Natuur
Buitenkozijnen	Hardhout	Antraciet
Ramen deuren	Hardhout	Antraciet
Voordeur	Hardhout	Antraciet
Dakoverstekken	Hardhout	Antraciet
Beglazing	Isolatieglas Hr++	Natuur
H.W.A.	Zink	Natuur
Dakbedekking	Keramische leipannen	Antraciet

PEIL = N.T.B.

B.K. AANGEWERTE BEGANE GRONDVLOER
E.E.A. CONFORM NAAST GELEGEN WONINGEN

Onderwerp : Nieuwbouw woning met aangrenzend bijgebouw aan de Zevenmorgen 26 te Ingen
Oudarchitect : Familie van Toon
Bouwlocatie : Zevenmorgen 26 te Ingen

Werk nr : W 20.1850
Formaat : A0
Tek nr : 1850-01

Blad : Overzichtstekening
Status : AANVRAAG OMGEVINGSVERGUNNING
Datum : 01-07-2021

Schaal : 1 : 100
Getekend : JBL
Gewijzigd : 21-07-2021

Rijnstraat 7
4031 KJ INGEN
T 0344-606686
F 0344-600611
I info@burovanbijldeveen.nl
W www.burovanbijldeveen.nl

