

|               |                                                                           |
|---------------|---------------------------------------------------------------------------|
| Onderwerp     | Nieuwbouw woning met aangrenzend bijgebouw aan de Zevenmorgen 26 te Ingen |
| Opdrachtgever | Familie van Toorn                                                         |
| Bouwlocatie   | Zevenmorgen 26 te Ingen                                                   |

|         |           |
|---------|-----------|
| Werk nr | W 20.1850 |
| Formaat | A 3       |
| Tek nr  | 1850-04   |


|        |                                                  |
|--------|--------------------------------------------------|
| Blad   | Trap beganegrond -> 1e ver. en 1e ver. -> zolder |
| Status | AANVRAAG OMGEVINGSVERGUNNING                     |
| Datum  | 24-2-2022                                        |

|           |        |
|-----------|--------|
| Schaal    | 1 : 50 |
| Getekend  | AvdB   |
| Gewijzigd |        |



**BVB**  
BURO VAN BLIJDERVEEN

Rijnstraat 7  
  
4031 KJ INGEN  
  
T 0344-606686  
  
F 0344-600811  
  
I [info@burovanblijderveen.nl](mailto:info@burovanblijderveen.nl)  
  
W [www.burovanblijderveen.nl](http://www.burovanblijderveen.nl)

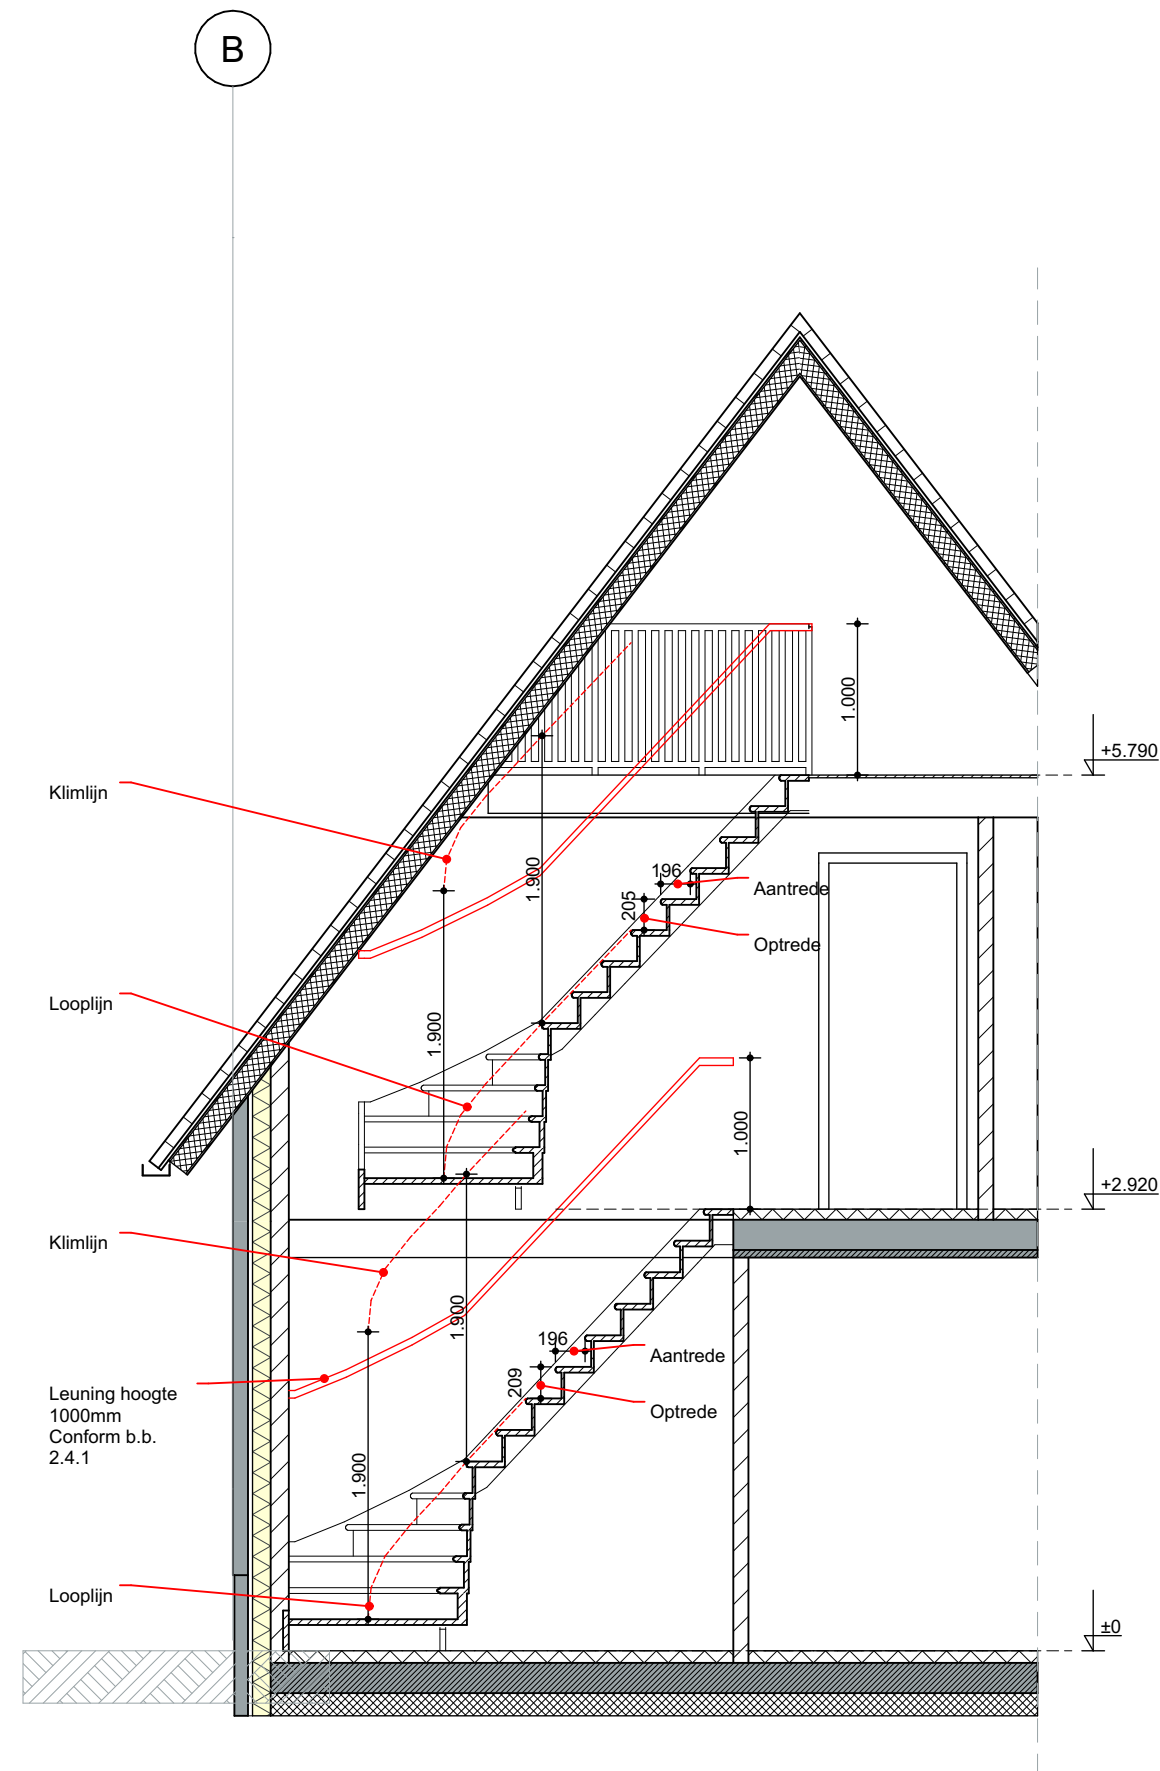

Exacte uitvoering/materiaal trap n.t.b.

Uitvoering trappen volgens NEN 3509 'Trappen in woningen en woongebouwen'

Trap conform bb 2012 afdeling 2.5 artikel 2.5.2 Bestaande bouw  
(conform regelgeving particuliere overdrachtschap Art. 1.12a)

|                                            |        |
|--------------------------------------------|--------|
| Min. breedte trap                          | 0,70 m |
| Min. vrije hoogte                          | 1,90 m |
| Min. aantrede t.p.v. klimlijn              | 0,13 m |
| Max. hoogte optrede                        | 0,22 m |
| Min. afstand van klimlijn tot zijkant trap | 0,20m  |

**Project**  
Nieuwbouw woning met aangrenzend bijgebouw aan de Zevenmorgen 26 te Ingen

**Werk nr**  
W 20.1850

**Datum**  
01-07-2021

**Gewijzigd**  
21-07-2021



Rijnstraat 7  
4031 KJ INGEN  
T 0344-606686  
F 0344-600811  
I [info@burovanblijderveen.nl](mailto:info@burovanblijderveen.nl)  
W [www.burovanblijderveen.nl](http://www.burovanblijderveen.nl)