
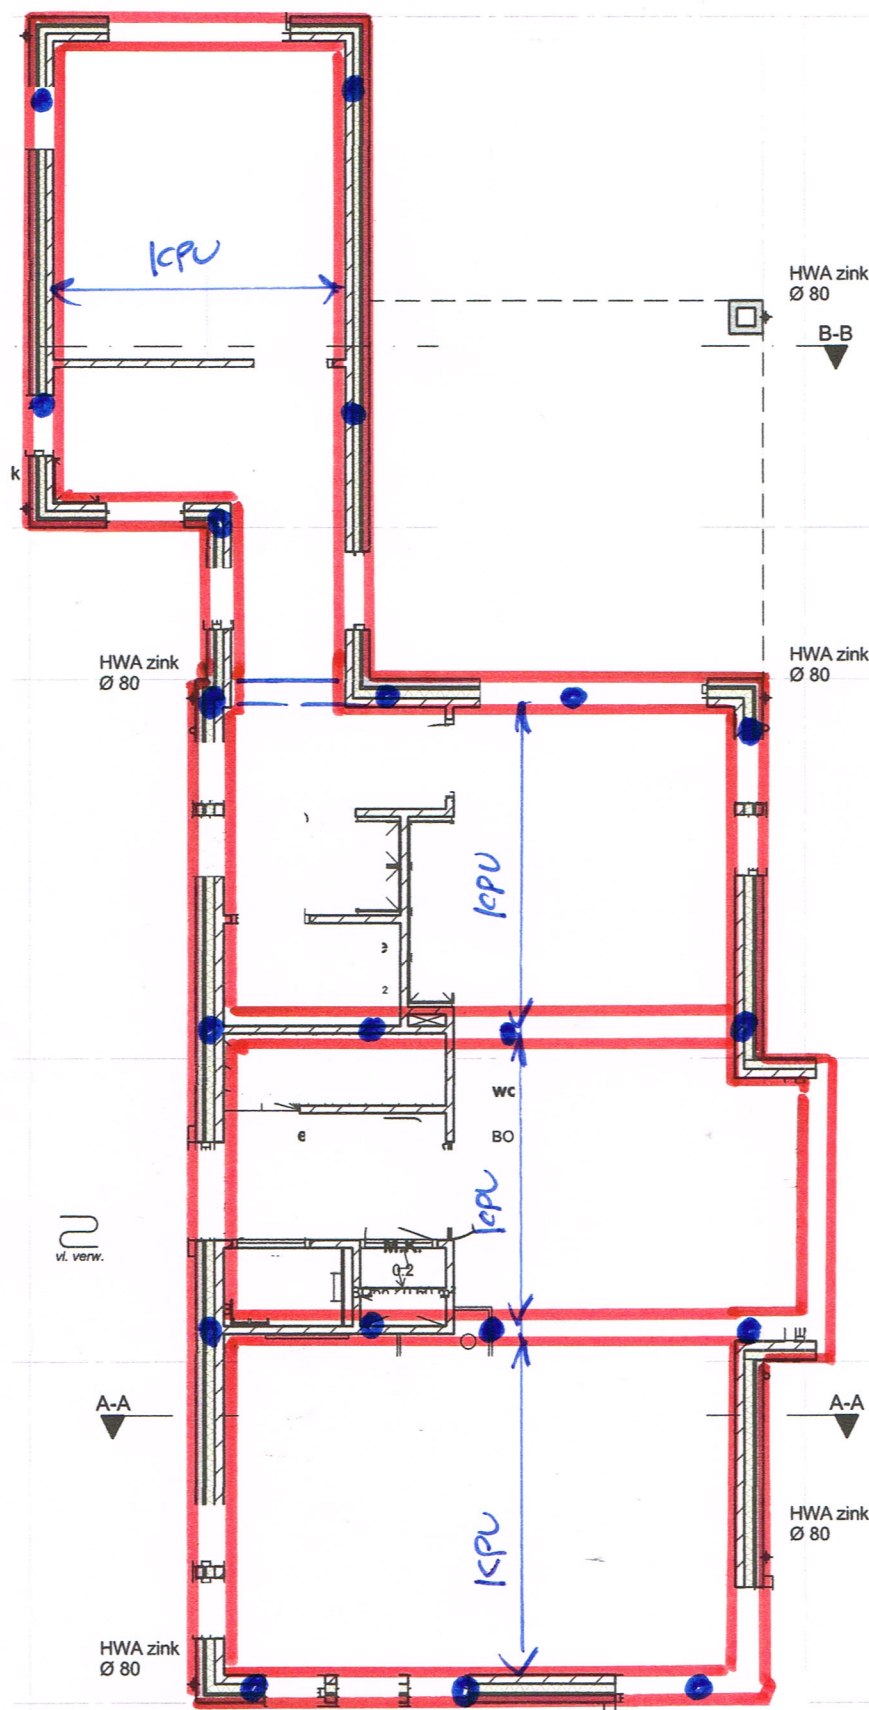


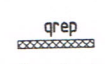

Fundering / Begane grondvloer

 Systeenvloer type *kanalplaatvloer*
 vlg berekening / tekening fabrikant
 Lijntlast op de vloer in kN/m'
 Funderingsbalken : *400 x 500*
 Hart paal = hart balk (tenzij anders aangegeven)

 *mortelschroefpaal vlg nader grondonderzoek*

Materialen



Beton C20/25 milieuklasse XC2
 Betonstaal B500B
 Dekking : Balken/stroken/voeren 35mm b/o
 vloer boven 15mm onder 30mm
 Constructiestaal S235 las min. 4mm
 Bouten min 8.8
 Houtkwaliteit min C18
 Metselwerk : druksterkte min. 12 N/mm²
 mortelsterkte min. 5 N/mm²

MD Bouwconstructie BV
 4153 XR 27 Beesd
 06 30553257

18 FEB 2022

VOORLOPIG

211214-001

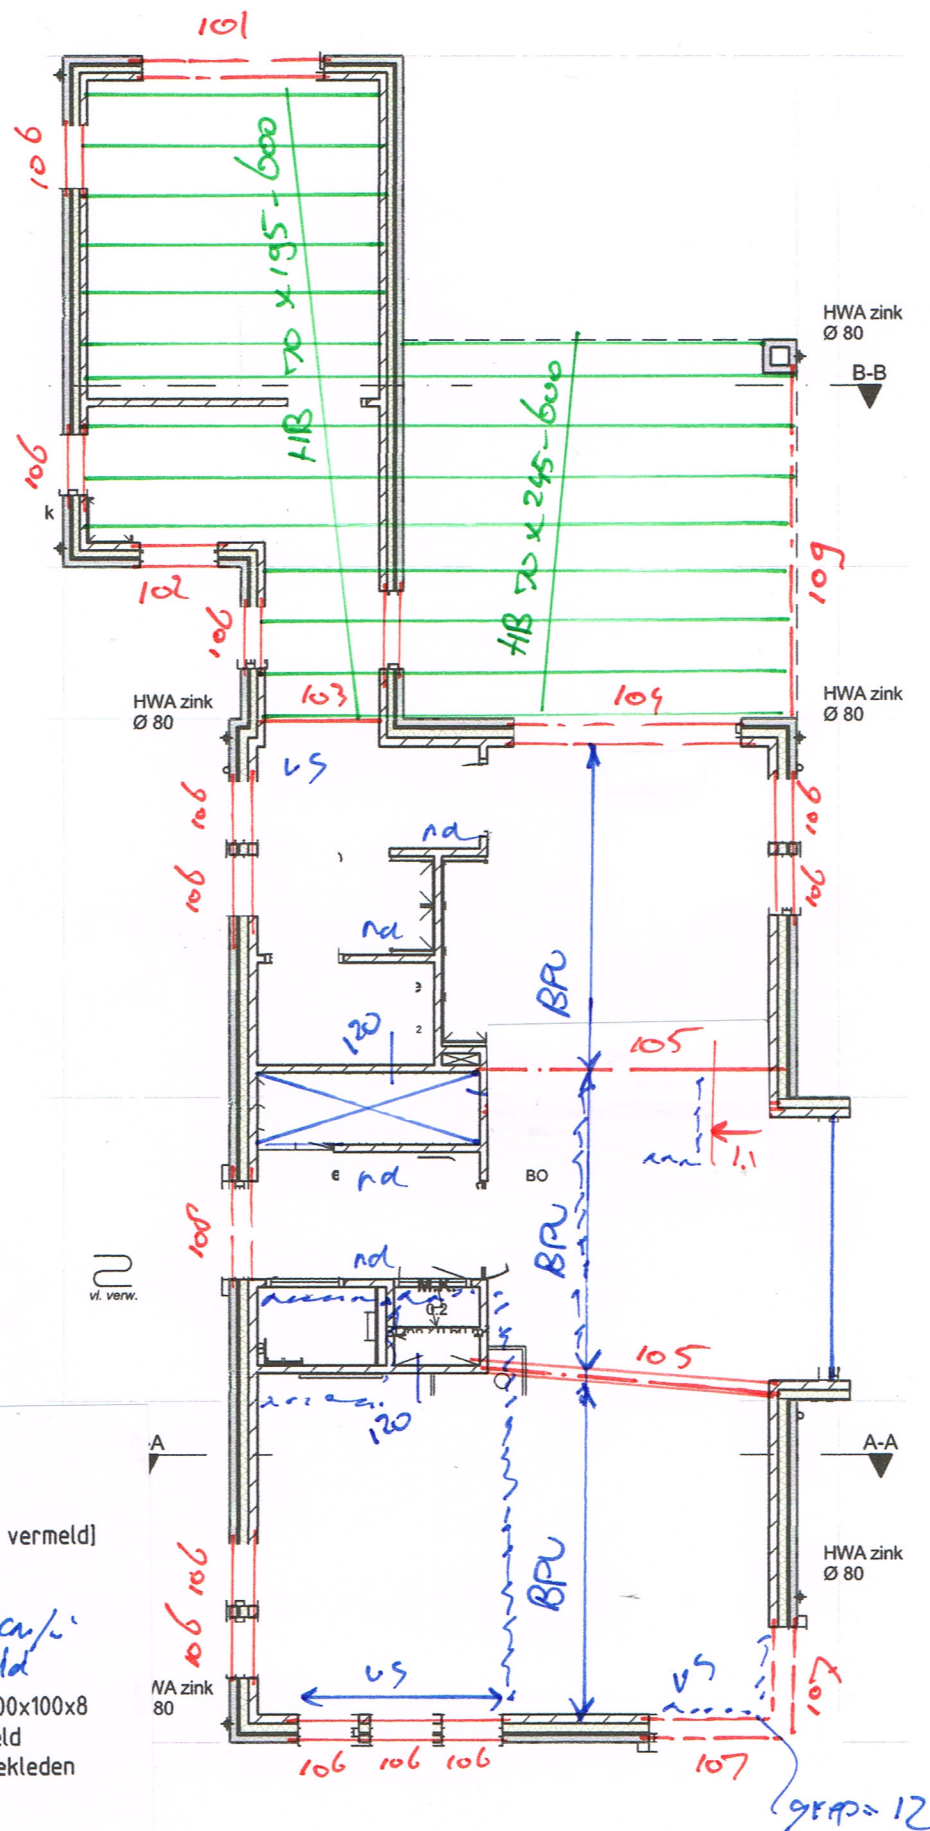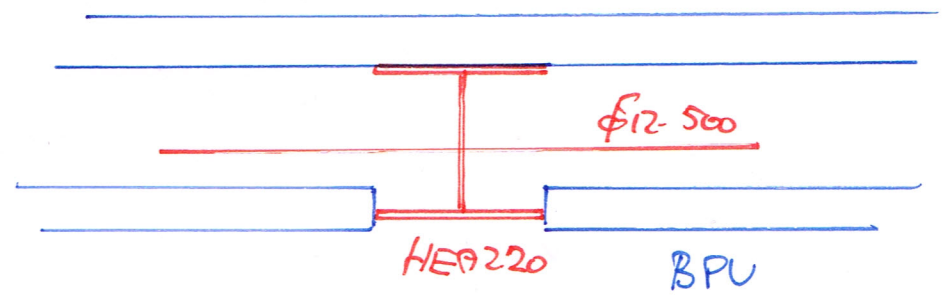

Verdiepingsvloer

- BPV Breedplaatvloer dik 240 mm (tenzij anders vermeld) vlg berekening / tekening fabrikant
- VS Versterkte strook in de vloer
- qrep Lijnlast op de vloer in kN/m' *qrep = 6 kN/m' tenzij anders vermeld*

Boven overige muuropeningen VEBO of stalton of L100x100x8
 Dragend metselwerk dik 120 mm, tenzij anders vermeld
 Constructies in overleg met gemeente brandwerend bekleden
 Dilataties in metselwerk vlg opgave steenfabrikant


- 101= bi/bui $\angle 150 \times 100 \times 10$ opleg 150 mm
- 102= bi staltonlatei bui staltonlatei
- 103= staltonlatei
- 104= bi vnp240 opleg 200 mm bui $\angle 200 \times 100 \times 10$ opleg 150 mm
- 105= HEA220 opleg links 250 mm rechts 120 mm
- 106= bi/bui staltonlatei
- 107= geveldroger aan vloer bi uitklimmen
- 108= bi/bui staltonlatei
- nd= niet dragende wand

VOORLOPIG

MD Bouwconstructie BV
 4153 XR 27 Beesd
 06 30553257

18 FEB 2022

211214-002

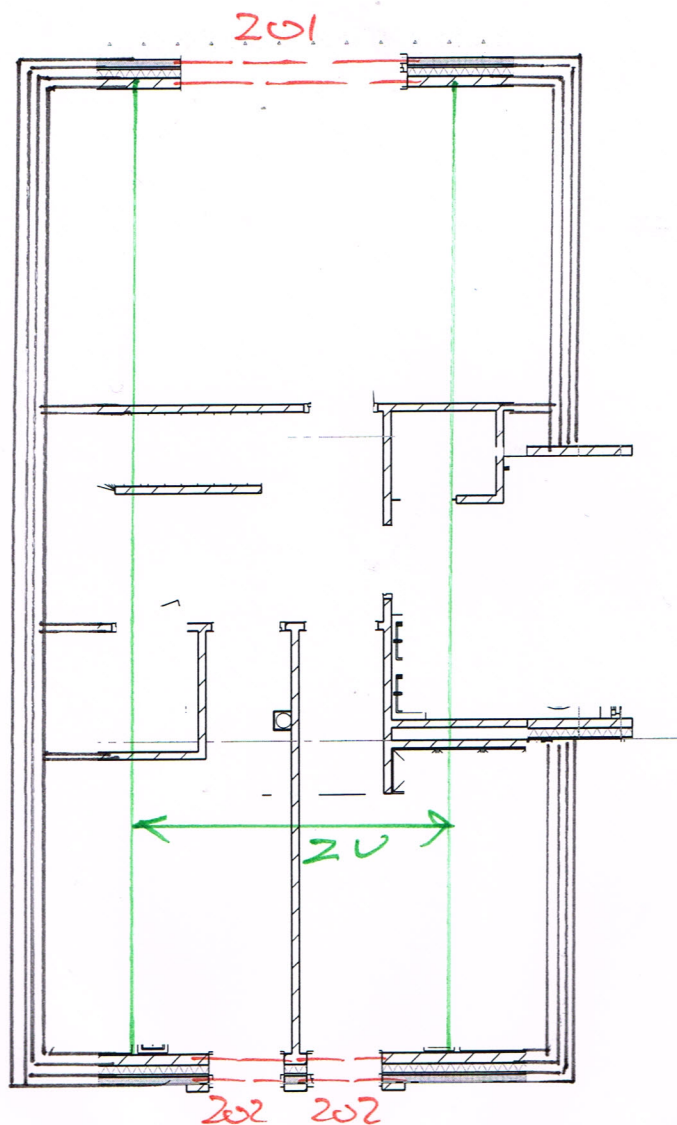

Zoldervloer

← ZV → Zoldervloer is een onderdeel van de kapconstructie
 berekening en tekening volgens leverancier prefab kapconstructie

Constructies in overleg met gemeente brandwerend bekleden
 Dilataties in metselwerk vlg opgave steenfabrikant
 Alle constructies onderling goed verbinden


MD Bouwconstructie BV
 4153 XR 27 Beesd
 06 30553257

201: bi/bui L150 x 100 x 10 opleg 150mm
 202: bi/bui slat kanloten

18 FEB 2022

211214-003

VOORLOPIG

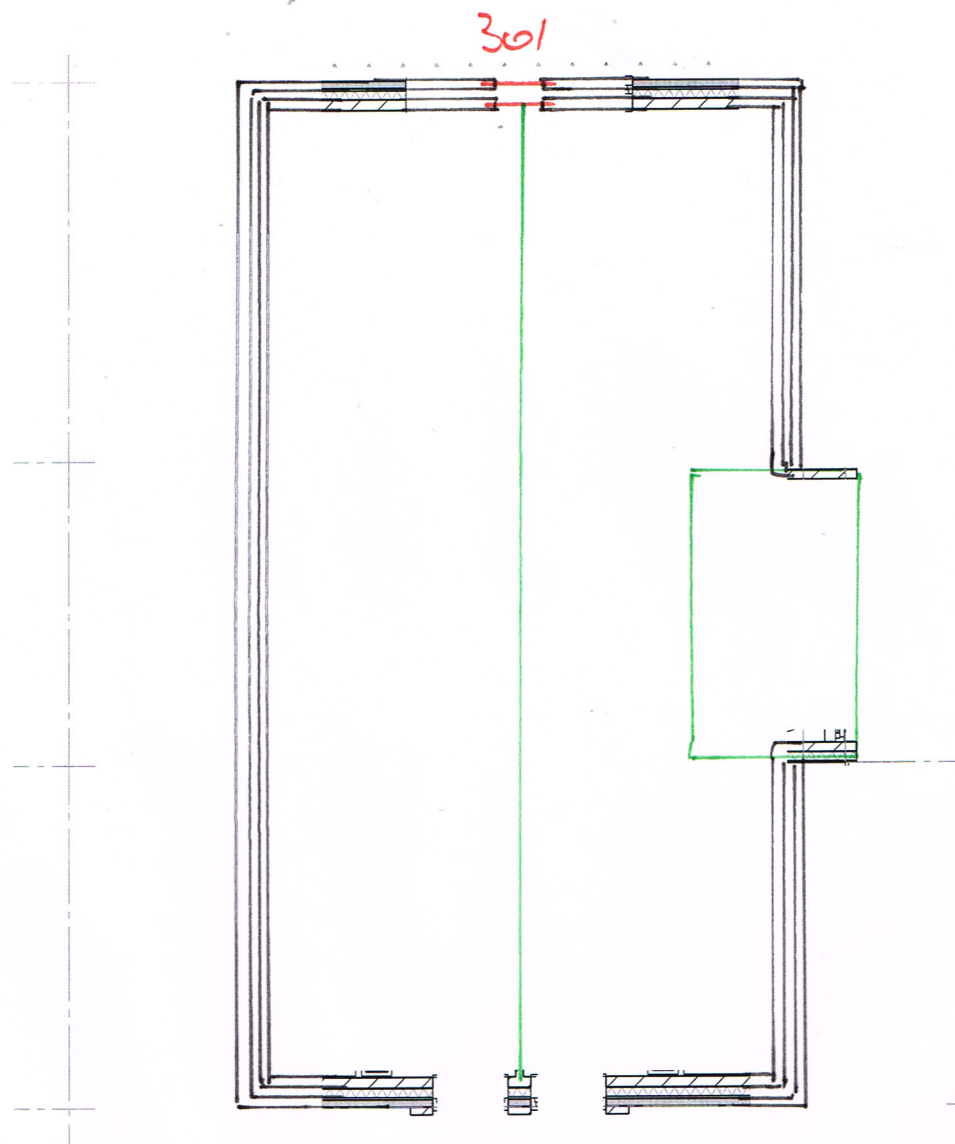

Dakconstructie

Scharnierkap volgens berekening en tekening leverancier

Kapconstructie aan systeemvloer bevestigen volgens opgave leverancier kapconstructie

MP = Muurplaat vlg opgave leverancier dakconstructie

Alle constructies onderling goed verbinden

Kopgevel verankeren aan kapconstructie

VOORLOPIG

18 FEB 2022

MD Bouwconstructie BV
4153 XR 27 Beesd
06 30553257

301: bij staktonlotei bui staktonlotei

211214-004